


OPTION A — TRIANGLE, SAME ANGLE: void edge 2.20 + 1.26 = 3.46

TALL HOUSE WALL (exist., AC units)

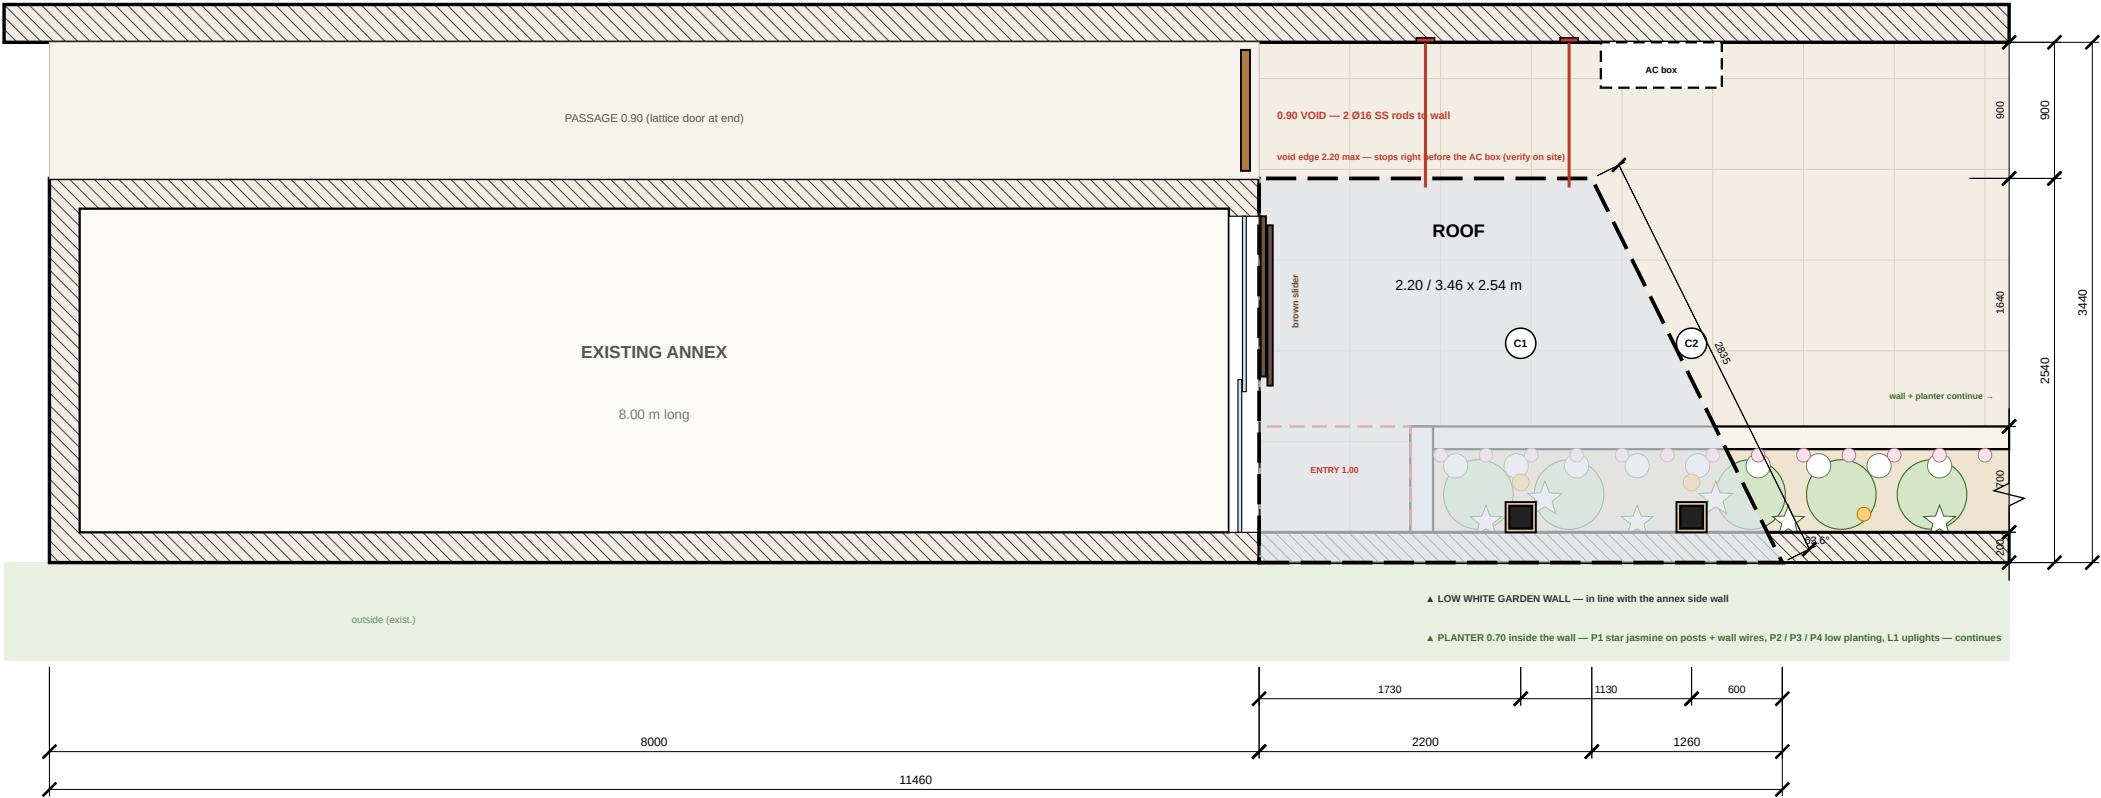


1
V2T-01

TOP VIEW — ANNEX, GARDEN & ROOF

1:50 @ A3 — annex + garden wall in one line; planter 0.70 continues; entry 1.00 at the door

2/V2T-01 ROOF FRAMING PLAN — 1:30

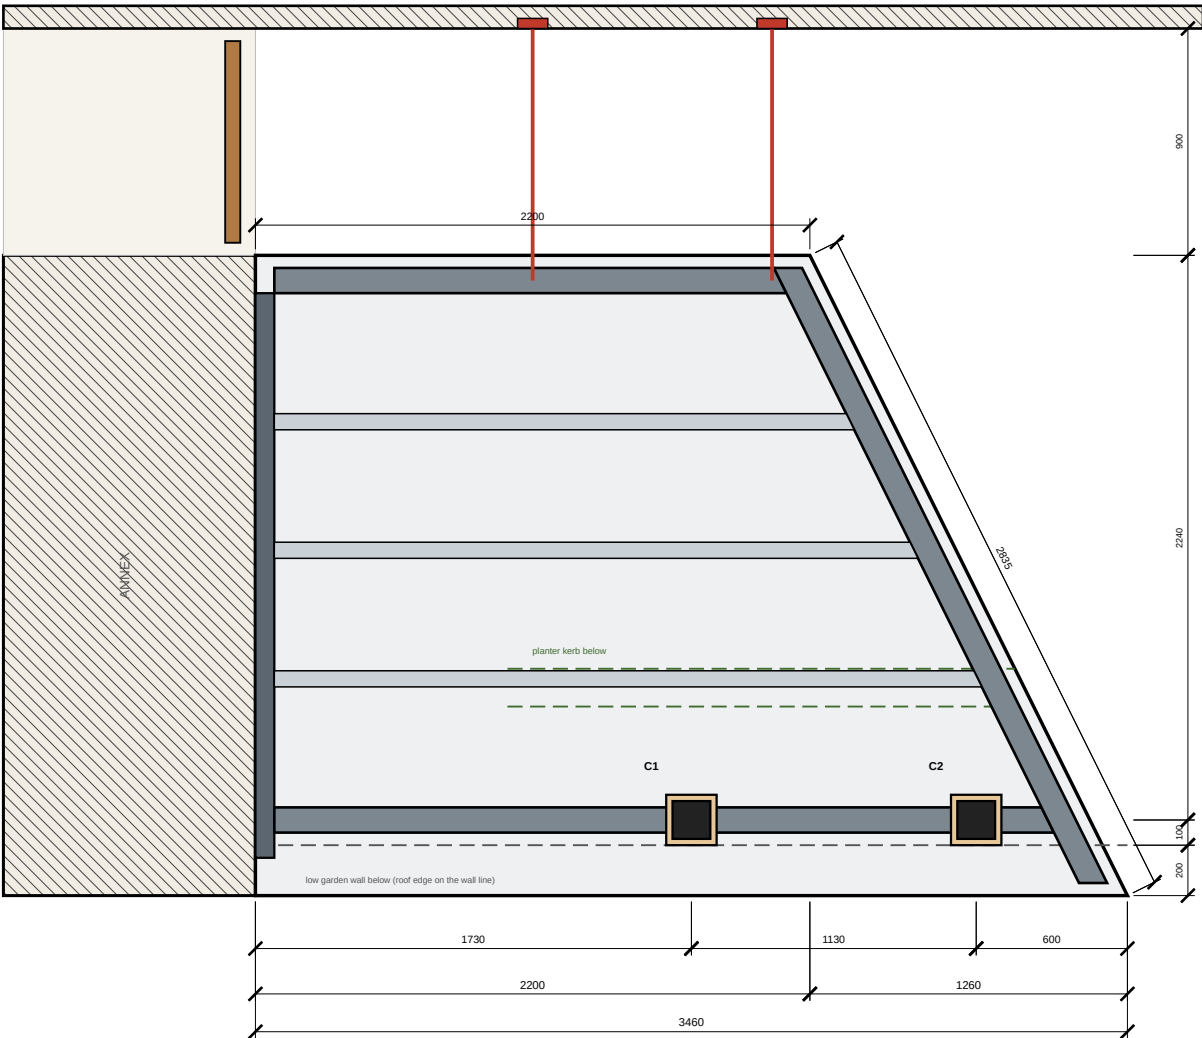

THIS VERSION

triangular roof, same angle: plants edge 2.20 + 1.26 = 3.46, void edge 2.20 (max, stops before the AC box), raked edge 2.84; 0.90 m void open, 2 slim Ø16 stainless hangers to the tall wall; 2 columns against the garden wall.

Roof fixed to the annex end façade (ledger). The 0.90 m passage to the lattice door stays open.

Void edge hung from the tall house wall on 2 Ø16 stainless rods (tumbuckles, wall plates) — slim, almost invisible.

Triangle (same angle as before): plants edge 2.20 + 1.26 = 3.46 m; raked edge 2.84 m at 63.6° to the plants edge.

C1 in the middle of the 3.46 edge (1.73 from the façade); C2 0.60 m in from the tip (the tip cantilevers 0.60).

Joists run from the annex ledger to the raked edge beam (max. span = 4.2 m).

COMMON

Annex side wall and low white garden wall are ONE line; the roof's plants edge (fascia) is on it.


Planter 0.70 inside the wall (soil + white kerb), continues along the wall; paved entry space 1.00 between the façade and the planter (walk in to the left glass door).

Entrance opening runs to the side wall (no pier).


C1 / C2: SHS 150 clad 200x200 thermo-ash, against the garden wall, 2 SS brackets each into the wall; edge beam on the column line, roof cantilevers 0.30 to the fascia over the wall.

Underside +2.36, fascia 0.43 (top +2.79); columns 0.13 above roof. Falls 1:70 to the box gutter on the raked edge; rainwater down C2.

3/V2T-01 3D — BIRD'S EYE (from outside, over the low garden wall)

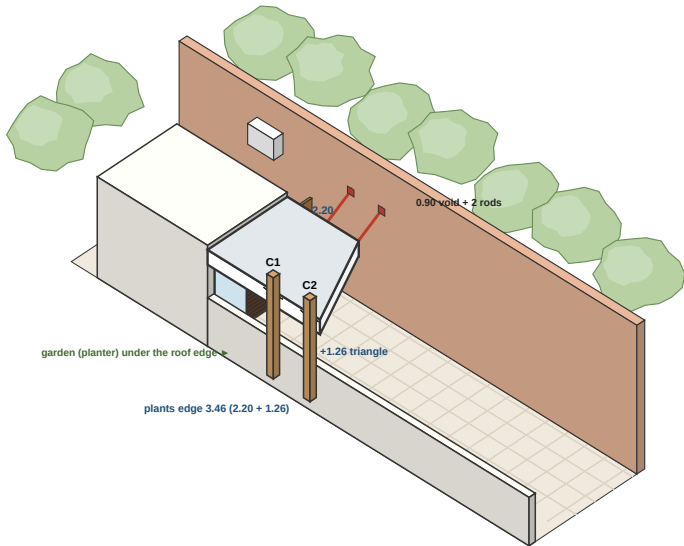

SCALE BAR 1:50 (top view)

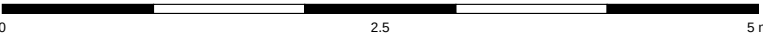

COURTYARD ROOF — V2T

OPTION A — TRIANGLE, SAME ANGLE: void edge 2.20 + 1.26 = 3.46;

triangular roof, same angle: plants edge 2.20 + 1.26 = 3.46, void

edge 2.20 (max, stops before the AC box), raked edge 2.84; 0.90 m

void open, 2 slim Ø16 stainless hangers to the tall wall; 2 columns

against the garden wall

Client: Owner / Client

Design & drawings: Claude Code

DRAWING NOTES

- Do not scale from this drawing. Use figured dimensions only.
- All dimensions in millimetres; levels in metres relative to internal FFL ±0.000 (datum to be tied to site survey).
- Contractor to verify all dimensions, levels & existing structure on site before fabrication or ordering.
- Read with all other architectural, structural & services drawings and the specification notes (A-001).
- Structural members are preliminary: final design, connections & calculations by a licensed structural engineer to local code before construction.
- Report any discrepancy to the designer before proceeding.

REVISIONS

Rev	Date	Description
C15	08.10.2026	Void edge max 2.20 (before the AC box): A triangle same angle / B rectangle 2.20
C14	07.10.2026	Planting per client reference: jasmine, low shrubs, uprights
C13	07.10.2026	Planter 0.70 (-30 %), soil only, no bushes; garden wall continues

FOR CLIENT CHECK — roof void edge max 2.20 m: OPTION A (triangle, same angle) / OPTION B (rectangle 2.20)

DRAWING TITLE

OPTION A — TRIANGLE
top view & roof framing

SCALE @ A3

1:50 / 1:30

DRAWN / CHECKED

CC / —

DATE

08.10.2026

SERIES

ARCHITECTURAL

DRAWING No.


REV

C15-A

C15


OPTION B — RECTANGLE, MAX LENGTH 2.20 (2.20 x 2.54)

TALL HOUSE WALL (exist., AC units)

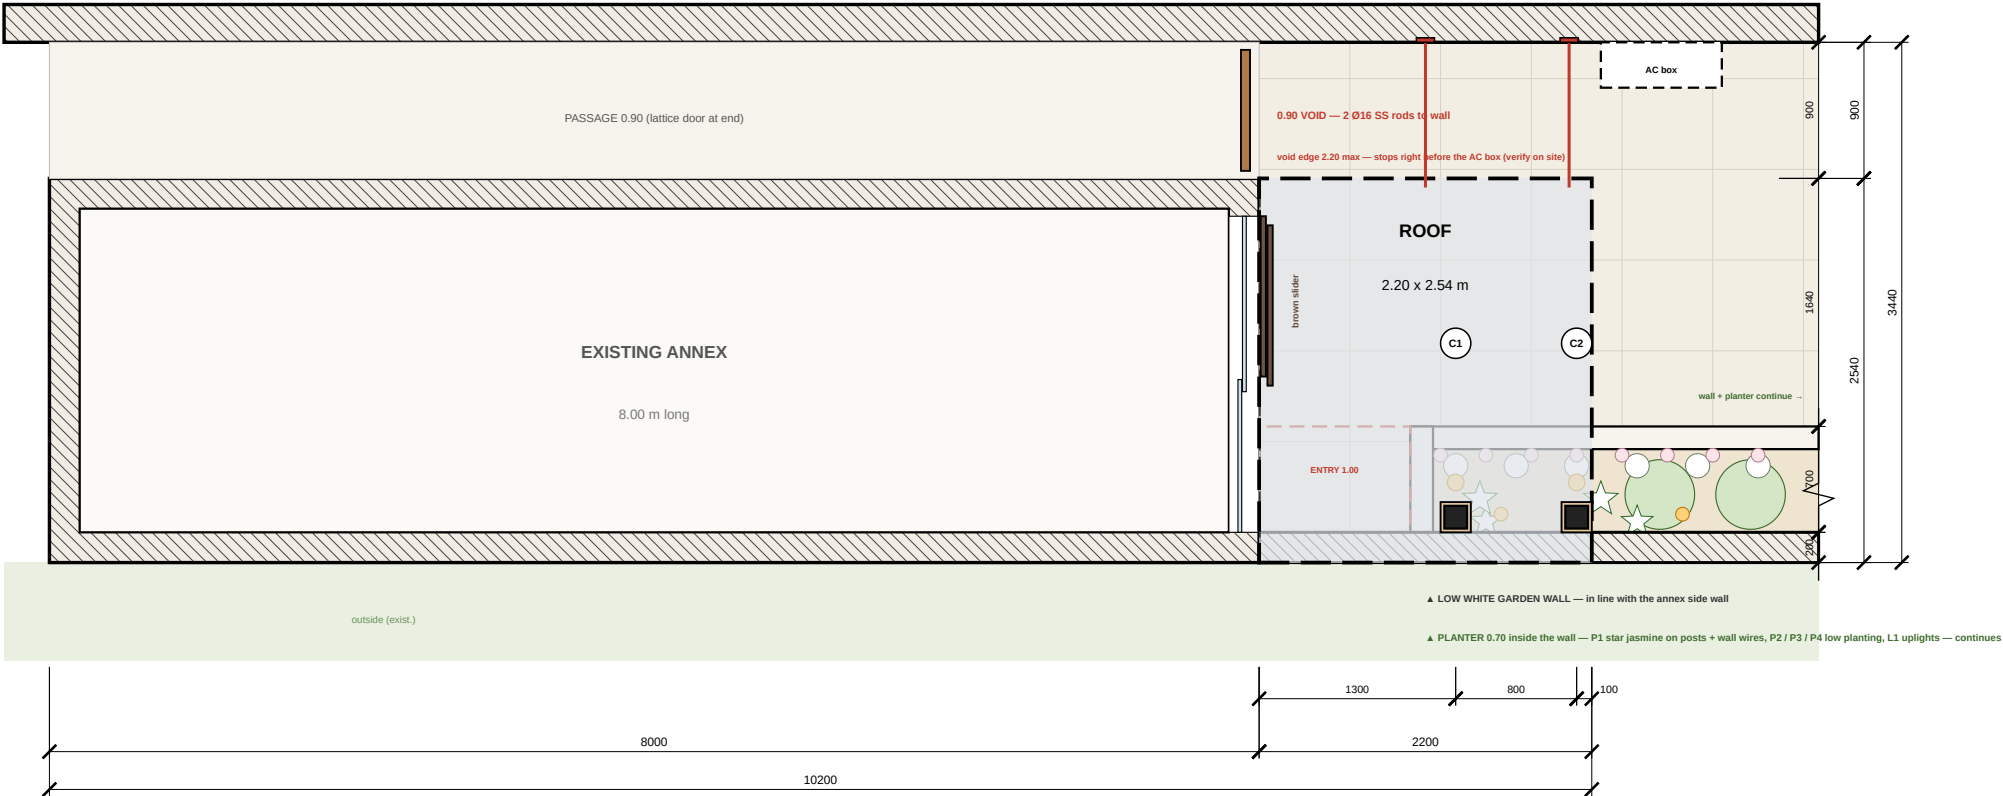


1 TOP VIEW — ANNEX, GARDEN & ROOF

2/V2-01 ROOF FRAMING PLAN — 1:30

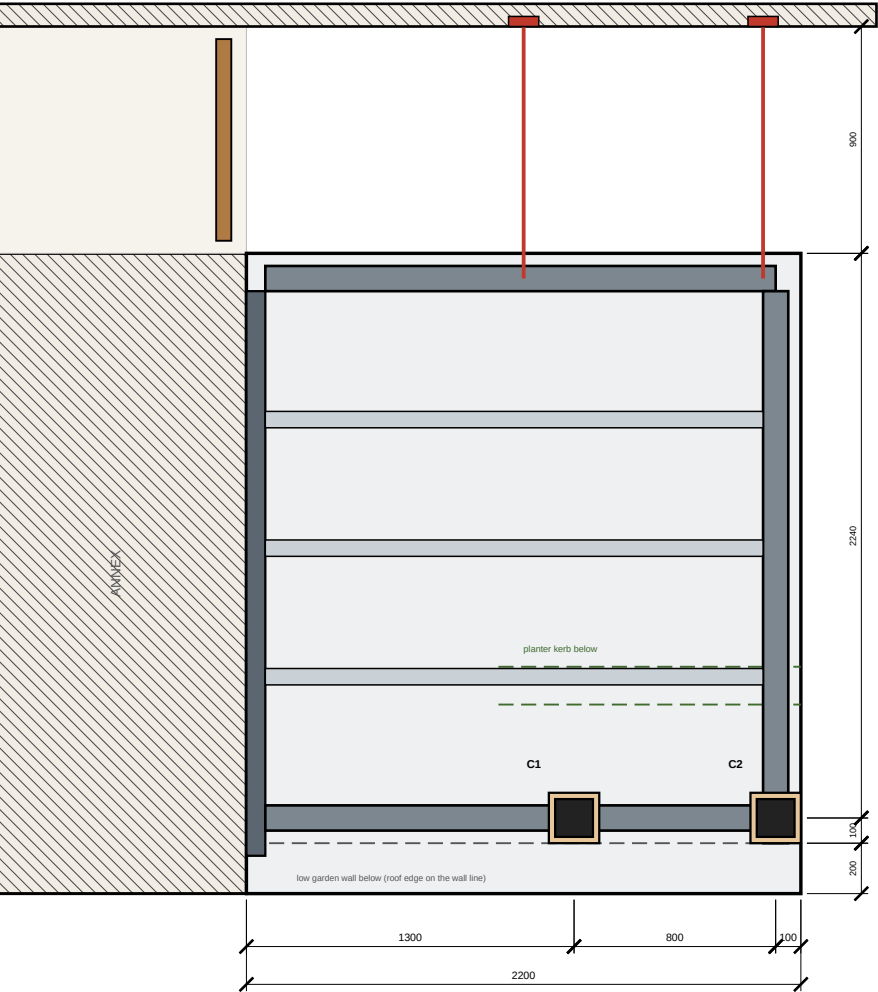

THIS VERSION
rectangular roof 2.20 x 2.54 (max length 2.20, stops before the AC box); 0.90 m void left open; void edge tied to the tall wall with 2 slim Ø16 stainless rods (rising = 30°); 2 columns on the plants side.
Roof fixed to the annex end façade (ledger). The 0.90 m passage to the lattice door stays open.
Void edge hung from the tall house wall on 2 Ø16 stainless rods (tumbuckles, wall plates) — slim, almost invisible.
C1 just inside the planter (clear of the near-end kerb), C2 at the corner; void edge 2.20 max — stops right before the AC box.
COMMON
Annex side wall and low white garden wall are ONE line; the roof's plants edge (fascia) is on it.
Planter 0.70 inside the wall (soil + white kerb), continues along the wall; paved entry space 1.00 between the façade and the planter (walk in to the left glass door).
Entrance opening runs to the side wall (no pier).
C1 / C2: SHS 150 clad 200x200 thermo-ash, against the garden wall, 2 SS brackets each into the wall; edge beam on the column line, roof cantilevers 0.30 to the fascia over the wall.
Underside +2.36, fascia 0.43 (top +2.79); columns 0.13 above roof. Falls 1.70 to the box gutter on the raked edge; rainwater down C2.

3/V2-01 3D — BIRD'S EYE (from outside, over the low garden wall)

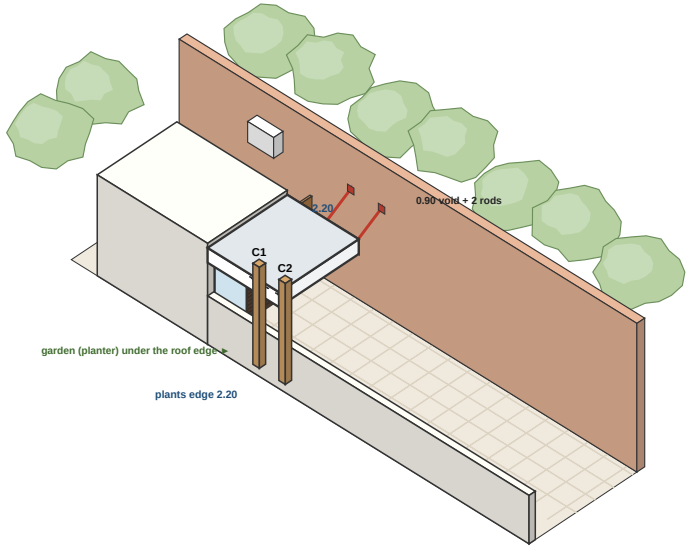

COURTYARD ROOF — V2

OPTION B — RECTANGLE, MAX LENGTH 2.20 (2.20 x 2.54): rectangular roof 2.20 x 2.54 (max length 2.20, stops before the AC box); 0.90 m void left open; void edge tied to the tall wall with 2 slim Ø16 stainless rods (rising = 30°); 2 columns on the plants side
Client: Owner / Client
Design & drawings: Claude Code

- DRAWING NOTES**
- Do not scale from this drawing. Use figured dimensions only.
 - All dimensions in millimetres; levels in metres relative to internal FFL ±0.000 (datum to be tied to site survey).
 - Contractor to verify all dimensions, levels & existing structure on site before fabrication or ordering.
 - Read with all other architectural, structural & services drawings and the specification notes (A-001).
 - Structural members are preliminary: final design, connections & calculations by a licensed structural engineer to local code before construction.
 - Report any discrepancy to the designer before proceeding.



REVISIONS		
Rev	Date	Description
C15	08.10.2026	Void edge max 2.20 (before the AC box): A triangle same angle / B rectangle 2.20
C14	07.10.2026	Planting per client reference: jasmine, low shrubs, uprights
C13	07.10.2026	Planter 0.70 (-30 %), soil only, no bushes; garden wall continues

FOR CLIENT CHECK — roof void edge max 2.20 m: OPTION A (triangle, same angle) / OPTION B (rectangle 2.20)

DRAWING TITLE	
OPTION B — RECTANGLE 2.20 top view & roof framing	
SCALE @ A3 1:50 / 1:30	DATE 08.10.2026
DRAWN / CHECKED CC / —	SERIES ARCHITECTURAL
DRAWING No.	REV

C15-B C15