


OPTION E — RECTANGLE 3.06 x 3.44 TO THE AC LINE


TALL HOUSE WALL (exist., AC units)

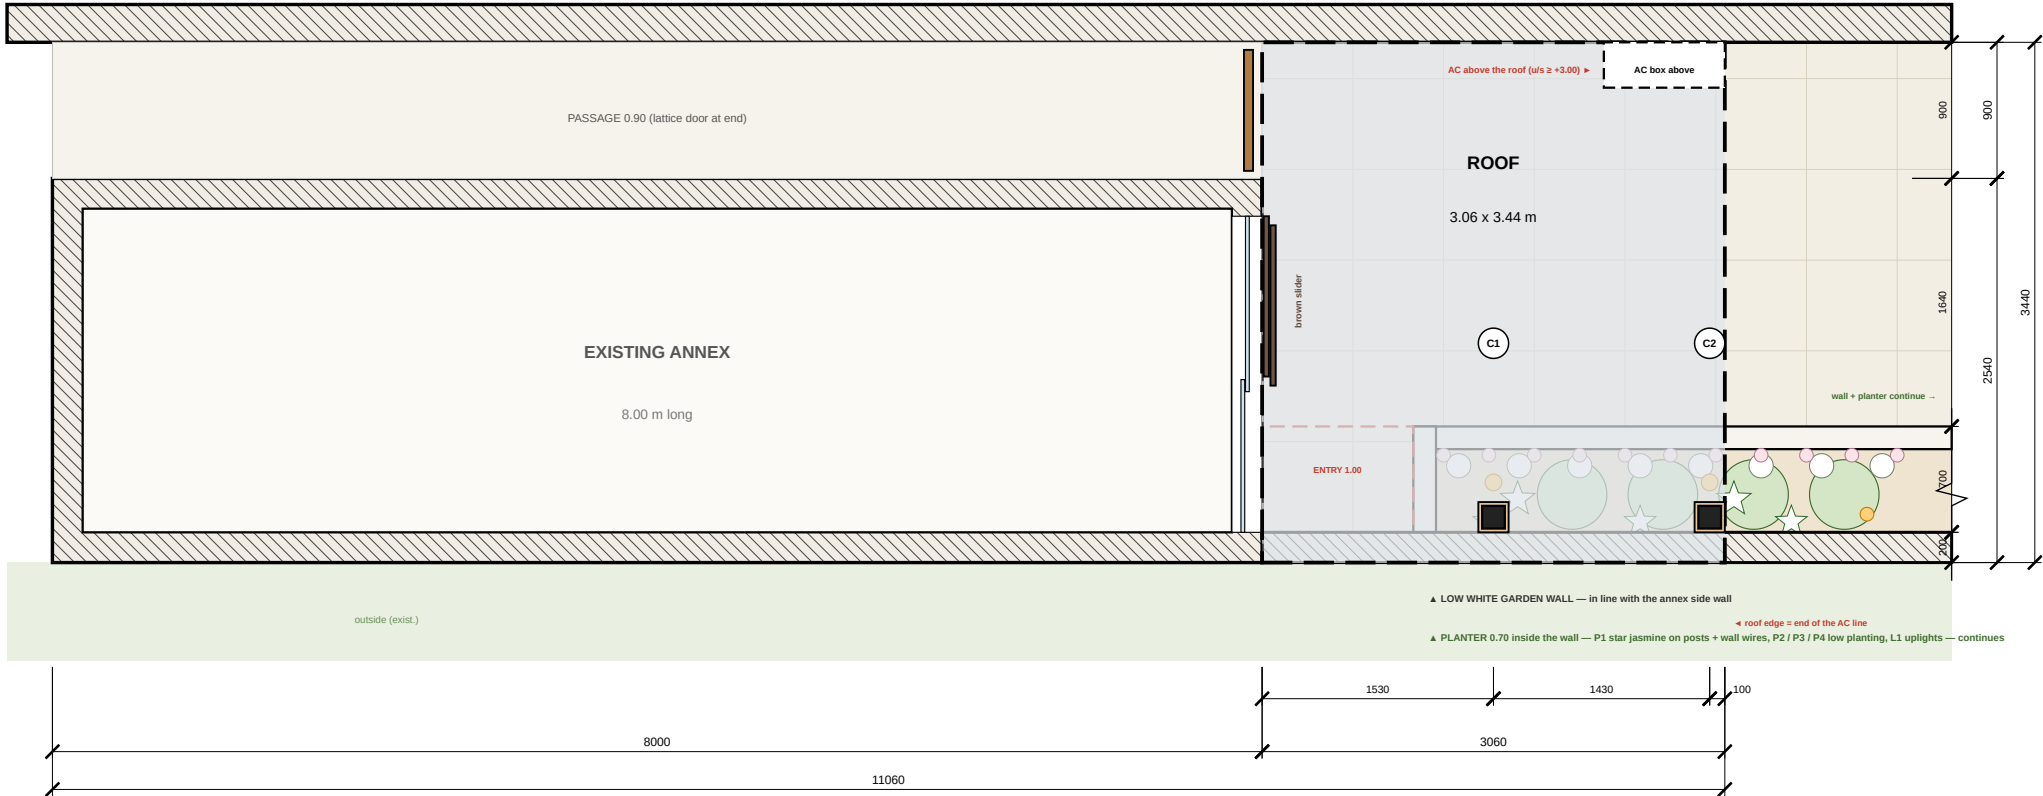

1 TOP VIEW — ANNEX, GARDEN & ROOF

V1-01 1:50 @ A3 — annex + garden wall in one line; planter 0.70 continues; entry 1.00 at the door

2/V1-01 ROOF FRAMING PLAN — 1:30

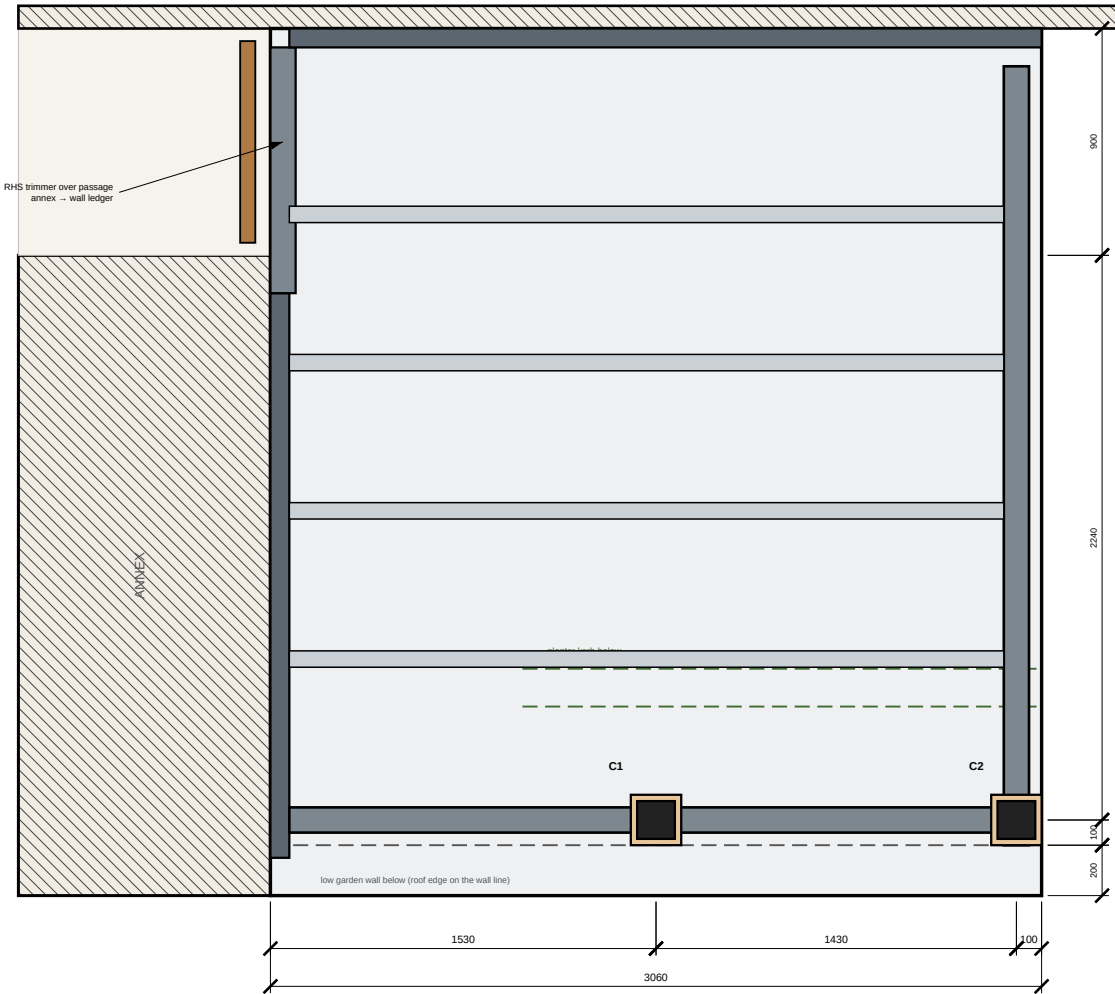

THIS VERSION

roof made longer: 3.06 x 3.44 to the tall wall, no void; right edge in line with the end of the AC box, the AC sits above the roof; bears on the annex ledger + a ledger on the tall wall; 2 columns against the garden wall.

Roof fixed to the annex end façade AND to the tall house wall (steel ledgers, resin anchors); covers the passage in front of the lattice door (RHS trimmer over the passage, annex ... wall ledger).

C1 in the middle of the plants edge, C2 at the corner; roof 3.06 long on both sides — right edge in line with the end of the AC box; the AC sits above the roof (u/s ≥ +3.00, verify / re-hang on brackets).

COMMON


Annex side wall and low white garden wall are ONE line; the roof's plants edge (fascia) is on it.

Planter 0.70 inside the wall (soil + white kerb), continues along the wall; paved entry space 1.00 between the façade and the planter (walk in to the left glass door). Entrance opening runs to the side wall (no pier).

C1 / C2: SHS 150 clad 200x200 thermo-ash, against the garden wall, 2 SS brackets each into the wall; edge beam on the column line, roof cantilevers 0.30 to the fascia over the wall.

Underside +2.36, fascia 0.43 (top +2.79); columns 0.13 above roof. Falls 1.70 to the box gutter on the raked edge; rainwater down C2.

3/V1-01 3D — BIRD'S EYE (from outside, over the low garden wall)

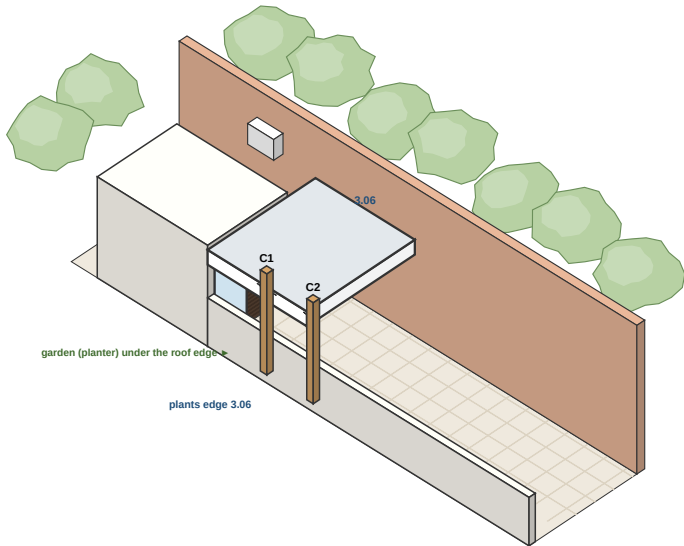

SCALE BAR 1:50 (top view)

0 2.5 5 m

COURTYARD ROOF — V1

OPTION E — RECTANGLE 3.06 x 3.44 TO THE AC LINE: roof made longer:

3.06 x 3.44 to the tall wall, no void; right edge in line with the end of the AC box, the AC sits above the roof; bears on the annex ledger + a ledger on the tall wall; 2 columns against the garden wall

Client: Owner / Client

Design & drawings: Claude Code

DRAWING NOTES

1. Do not scale from this drawing. Use figured dimensions only.
2. All dimensions in millimetres; levels in metres relative to internal FFL  $\pm 0.000$  (datum to be tied to site survey).
3. Contractor to verify all dimensions, levels & existing structure on site before fabrication or ordering.
4. Read with all other architectural, structural & services drawings and the specification notes (A-001).
5. Structural members are preliminary: final design, connections & calculations by a licensed structural engineer to local code before construction.
6. Report any discrepancy to the designer before proceeding.

REVISIONS

| Rev | Date       | Description                                                                  |
|-----|------------|------------------------------------------------------------------------------|
| C20 | 08.10.2026 | Option E: rectangle 3.06 x 3.44 to the end of the AC line; AC above the roof |
| C16 | 08.10.2026 | Roof supported by the tall wall, no void: C triangle / D rectangle 2.20      |

FOR CLIENT CHECK — option E: roof to the end of the AC line (3.06 x 3.44), AC above the roof

DRAWING TITLE

OPTION E — RECTANGLE 3.06  
top view & roof framing

SCALE @ A3

1:50 / 1:30

DRAWN / CHECKED

CC / —

DATE

08.10.2026

SERIES

ARCHITECTURAL

DRAWING No.

REV

C20-E

C20