

THE TWO ROOFS — TRIANGLE (C2) and SQUARE (D) — with their shadow on 21 JUNE

Same 3D model as the drawings (roof to the tall wall, no void); sun of 21 June, Athens; view from the garden side over the low wall. Month-by-month top views: next two sheets.

TRIANGLE C2

09:00



sun height 32°, from E

12:00



sun height 66°, from SE

15:00



sun height 65°, from SW

18:00



sun height 31°, from W

TRIANGLE — option C2 (tip at the AC line): plants edge 3.06, 1.75 at the tall wall

SQUARE D



sun height 32°, from E



sun height 66°, from SE



sun height 65°, from SW



sun height 31°, from W

SQUARE — option D (2.20 x 3.44): 2.20 along the planter, 2.20 at the tall wall

COURTYARD ROOF — SHADOW STUDY

Sun & shadow, 21 May - 21 August, Athens 37.98 N; TRIANGLE — option C2 (tip at the AC line); roof supported by the tall wall, no void
Client: Owner / Client
Design & drawings: Claude Code

DRAWING NOTES

- Do not scale from this drawing. Use figured dimensions only.
- All dimensions in millimetres; levels in metres relative to internal FFL ± 0.000 (datum to be tied to site survey).
- Contractor to verify all dimensions, levels & existing structure on site before fabrication or ordering.
- Read with all other architectural, structural & services drawings and the specification notes (A-001).
- Structural members are preliminary: final design, connections & calculations by a licensed structural engineer to local code before construction.
- Report any discrepancy to the designer before proceeding.

REVISIONS

Rev	Date	Description
C19	08.10.2026	Shadow study re-run: north towards the upper-left of the plan
C18	08.10.2026	Shadow study May-Aug: triangle C2 / square D
C17	08.10.2026	Option C2: tip at the AC line

SHADOW STUDY — orientation per client: NORTH towards the upper-left corner of the plan (tall wall faces NE)

DRAWING TITLE

SHADOW STUDY
both roofs in 3D (21 June)

SCALE @ A3 NTS	DATE 08.10.2026
DRAWN / CHECKED CC / —	SERIES SUN / SHADOW


DRAWING No. REV

SH-01

C19

WHERE THE SHADOW FALLS — TRIANGLE — option C2 (tip at the AC line)

Top views as the drawings — NORTH = upper-left (dial). ROOF = see-through white with red outline; dark = shade on the ground (roof + annex + walls); sun dial top-right of each view shows where the sun is.

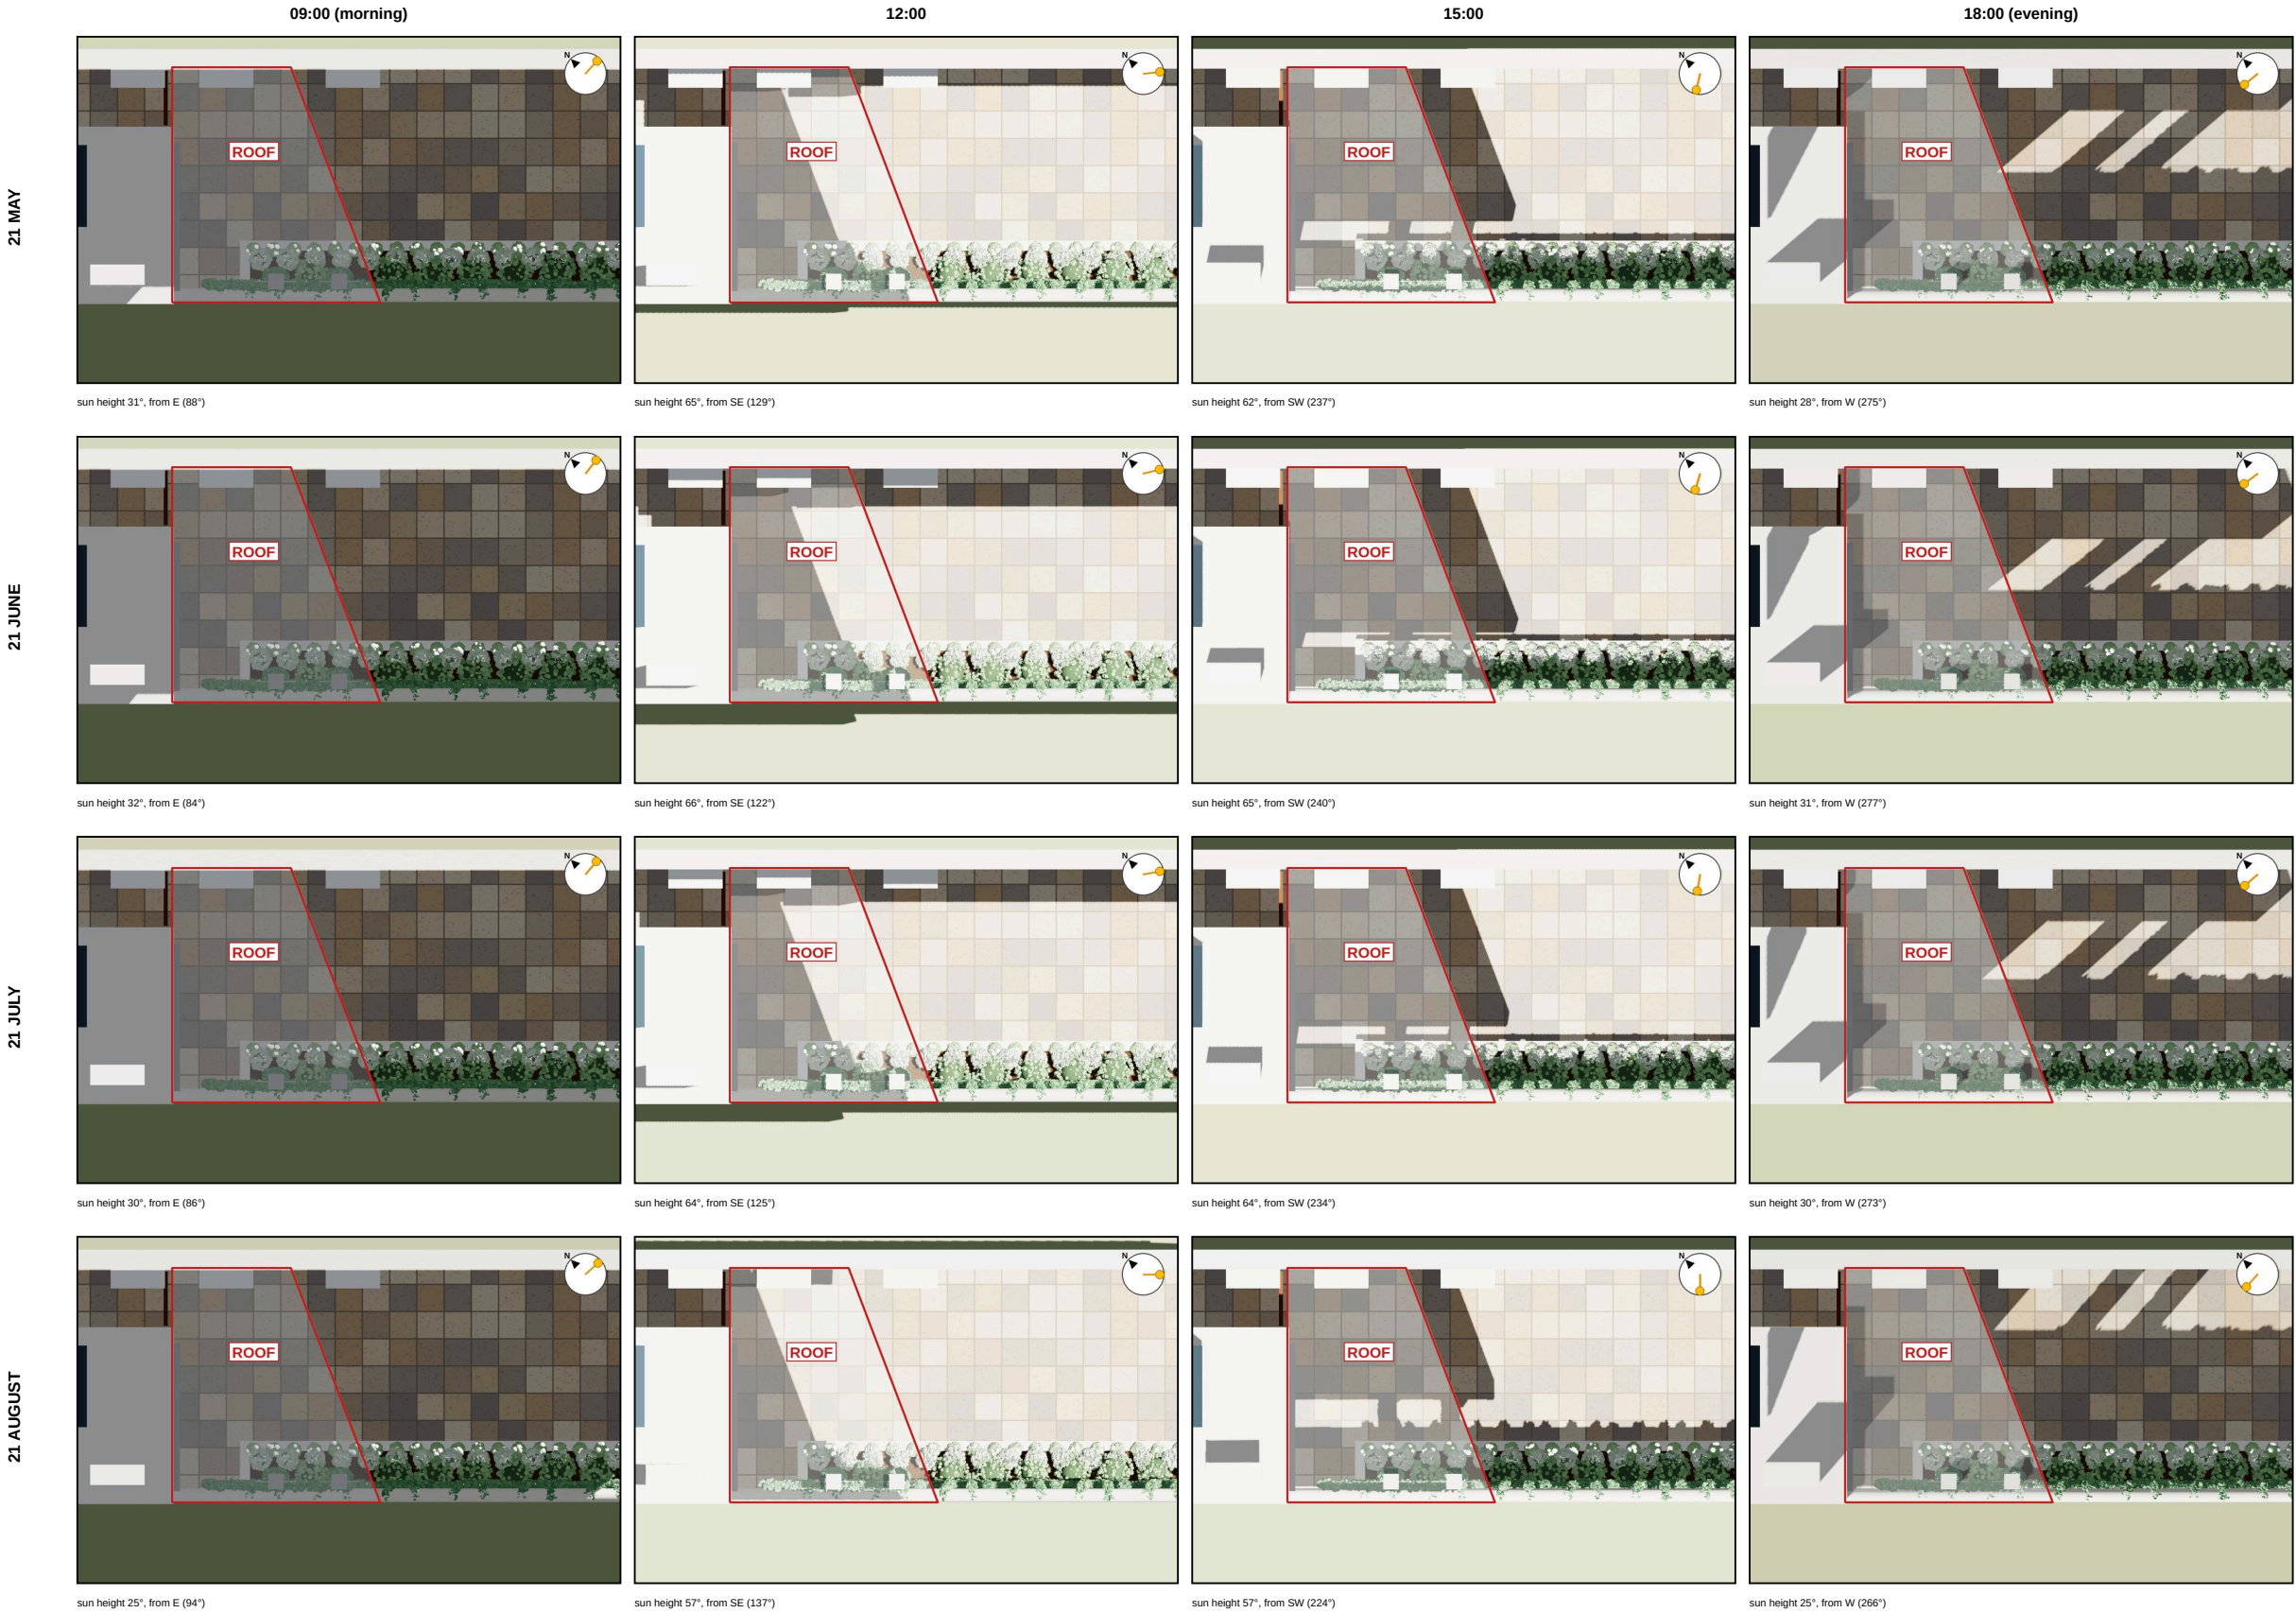

HOW TO READ (both versions behave the same way; only the size of the shaded patch changes)

09:00 — sun low in the EAST (25-32°), coming over the TALL WALL: the tall wall shades the whole courtyard, roof included — cool, shaded mornings in all four months.

12:00 — sun high (57-66°) from the SOUTH-EAST = from the open end of the courtyard: the roof's shade falls under it, shifted ~1 m towards the annex door; the rest of the paving is in sun. 15:00 — sun high from the SOUTH-WEST = over the low garden wall: the shade shifts ~1 m towards the tall wall; the planter is partly shaded by the low wall.

18:00 — sun low in the WEST, over the annex and the garden wall: they shade most of the courtyard, with sunny diagonal strips further along. Triangle C2: 3.06 along the planter, 1.75 at the wall — longer shade along the planter / columns side.

Assumptions: Athens 37.98 N, 21st of each month, summer time (EEST); NORTH towards the upper-left corner of the plan (client) — the tall wall faces north-east, the garden wall south-west. Existing trees not included (they add shade).

COURTYARD ROOF — SHADOW STUDY

Sun & shadow, 21 May - 21 August, Athens 37.98 N; TRIANGLE — option C2 (tip at the AC line); roof supported by the tall wall, no void

Client: Owner / Client

Design & drawings: Claude Code

- DRAWING NOTES
- Do not scale from this drawing. Use figured dimensions only.
 - All dimensions in millimetres; levels in metres relative to internal FFL ± 0.000 (datum to be tied to site survey).
 - Contractor to verify all dimensions, levels & existing structure on site before fabrication or ordering.
 - Read with all other architectural, structural & services drawings and the specification notes (A-001).
 - Structural members are preliminary: final design, connections & calculations by a licensed structural engineer to local code before construction.
 - Report any discrepancy to the designer before proceeding.

REVISIONS		
Rev	Date	Description
C19	08.10.2026	Shadow study re-run: north towards the upper-left of the plan
C18	08.10.2026	Shadow study May-Aug: triangle C2 / square D
C17	08.10.2026	Option C2: tip at the AC line

SHADOW STUDY — orientation per client: NORTH towards the upper-left corner of the plan (tall wall faces NE)

DRAWING TITLE

SHADOW STUDY

TRIANGLE roof

SCALE @ A3	DATE
NTS (plan views)	08.10.2026
DRAWN / CHECKED	SERIES
CC / —	SUN / SHADOW

DRAWING No. REV


SH-02 C19

WHERE THE SHADOW FALLS — SQUARE — option D (2.20 x 3.44)

Top views as the drawings — NORTH = upper-left (dial). ROOF = see-through white with red outline; dark = shade on the ground (roof + annex + walls); sun dial top-right of each view shows where the sun is.


21 MAY

09:00 (morning)

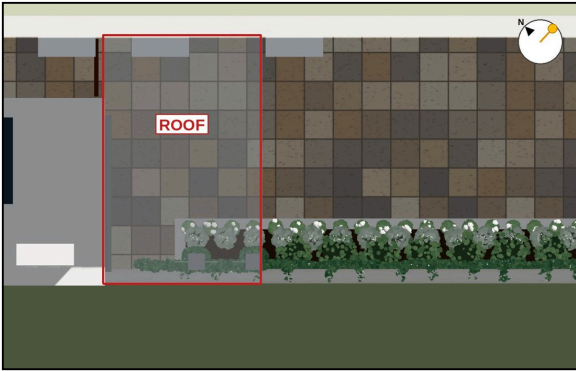


sun height 31°, from E (88°)

12:00

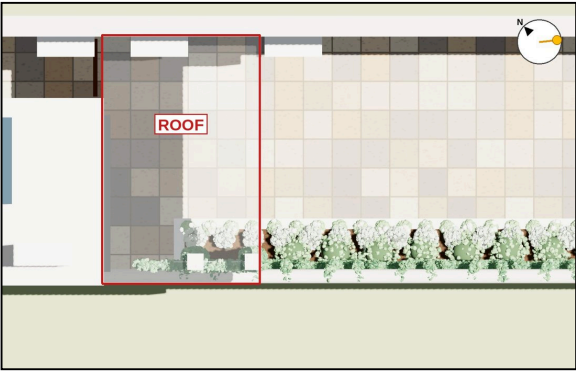


sun height 65°, from SE (129°)

15:00

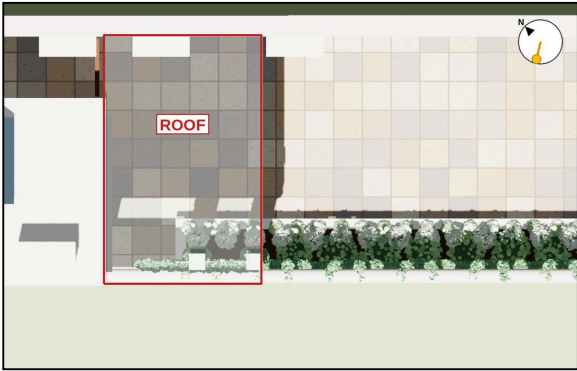


sun height 62°, from SW (237°)

18:00 (evening)

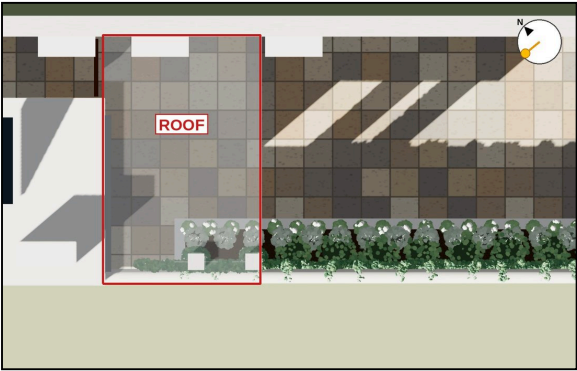


sun height 28°, from W (275°)


21 JUNE

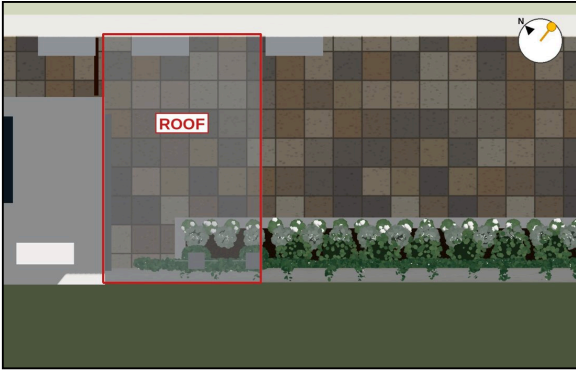


sun height 32°, from E (84°)

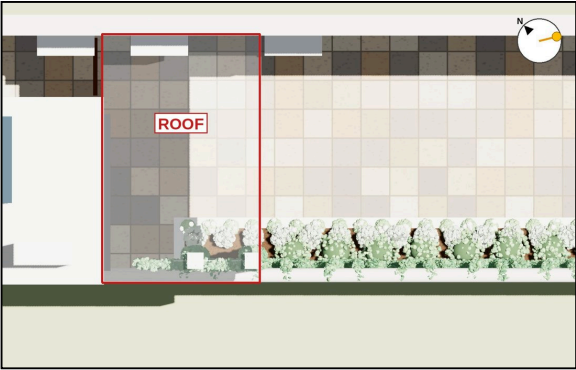

sun height 66°, from SE (122°)

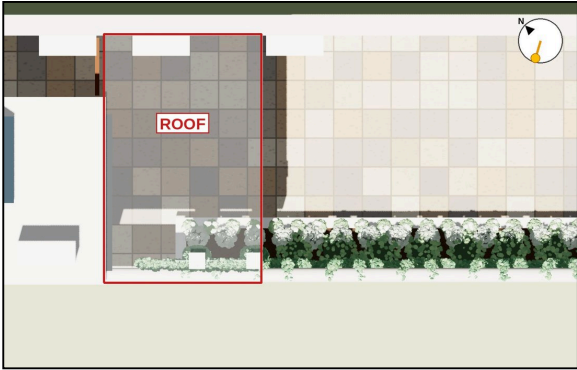


sun height 65°, from SW (240°)

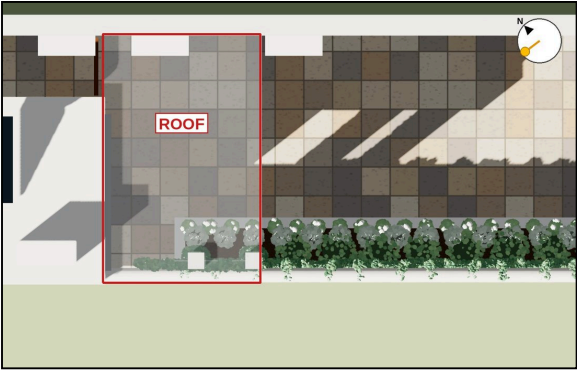


sun height 31°, from W (277°)


21 JULY

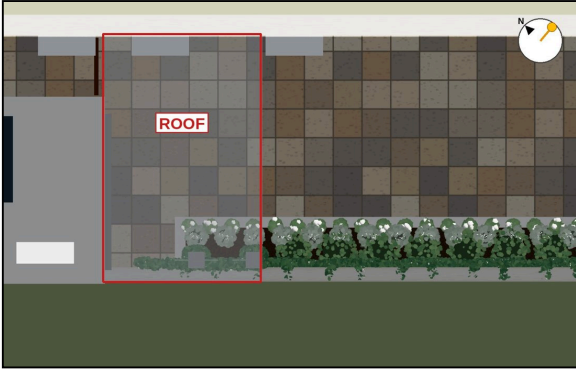


sun height 30°, from E (86°)

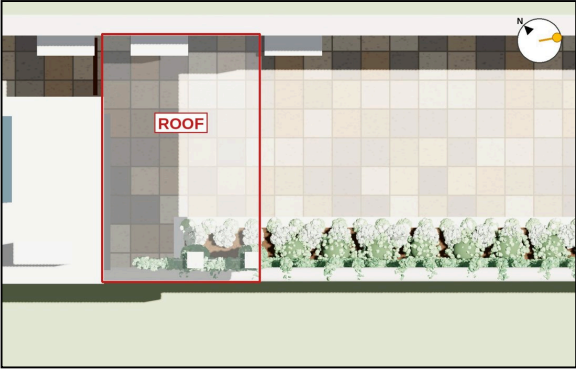

sun height 64°, from SE (125°)

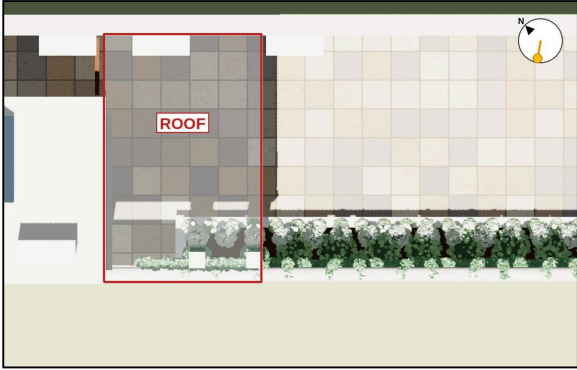


sun height 64°, from SW (234°)

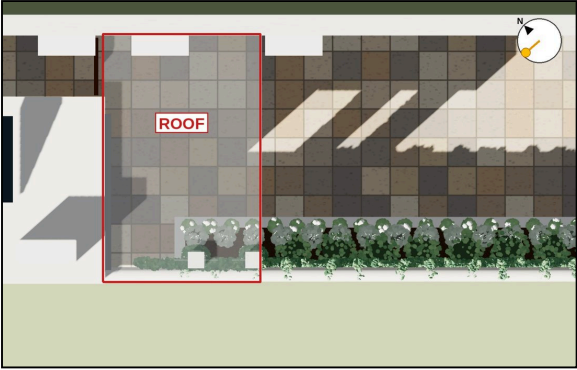


sun height 30°, from W (273°)


21 AUGUST

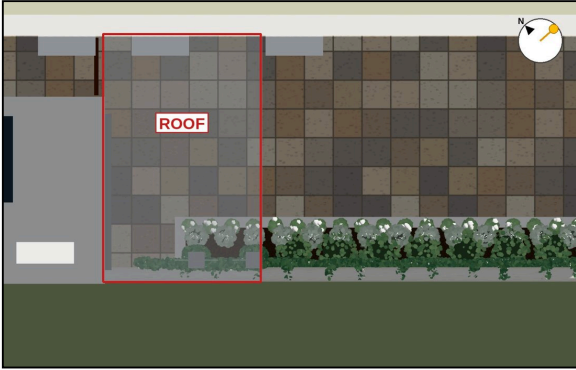


sun height 25°, from E (94°)

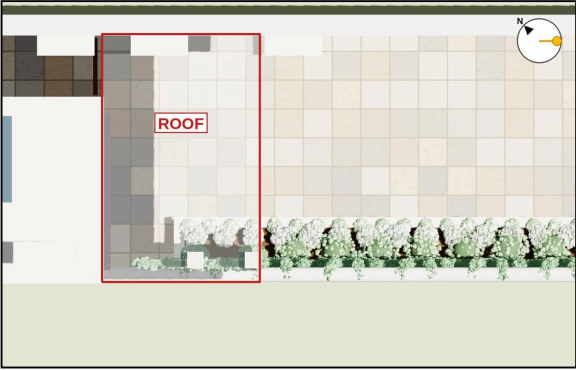

sun height 57°, from SE (137°)

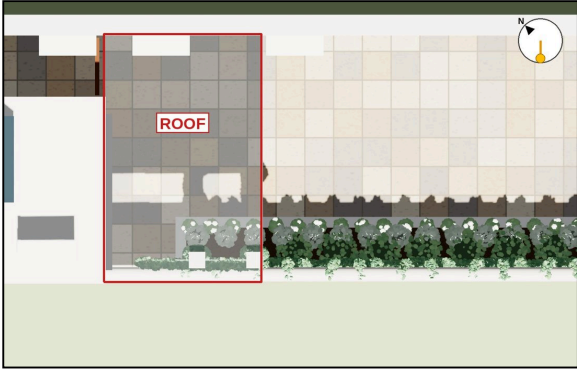

sun height 57°, from SW (224°)

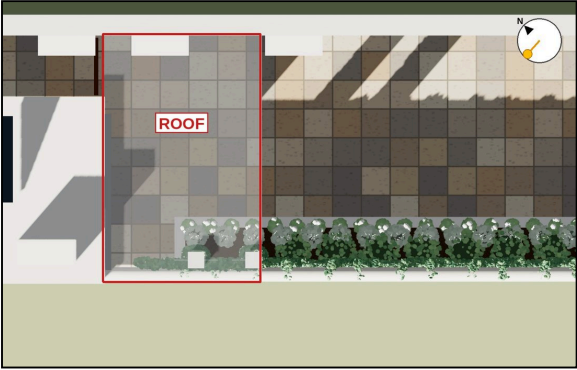

sun height 25°, from W (266°)

HOW TO READ (both versions behave the same way; only the size of the shaded patch changes)
09:00 — sun low in the EAST (25-32°), coming over the TALL WALL: the tall wall shades the whole courtyard, roof included — cool, shaded mornings in all four months.
12:00 — sun high (57-66°) from the SOUTH-EAST = from the open end of the courtyard: the roof's shade falls under it, shifted ~1 m towards the annex door; the rest of the paving is in sun. 15:00 — sun high from the SOUTH-WEST = over the low garden wall: the shade shifts ~1 m towards the tall wall; the planter is partly shaded by the low wall.
18:00 — sun low in the WEST, over the annex and the garden wall: they shade most of the courtyard, with sunny diagonal strips further along. Square D: 2.20 along the planter and 2.20 at the wall — more shade at the tall-wall side, less along the planter.
Assumptions: Athens 37.98 N, 21st of each month, summer time (EEST); NORTH towards the upper-left corner of the plan (client) — the tall wall faces north-east, the garden wall south-west. Existing trees not included (they add shade).

COURTYARD ROOF — SHADOW STUDY

Sun & shadow, 21 May - 21 August, Athens 37.98 N; SQUARE — option D (2.20 x 3.44); roof supported by the tall wall, no void
Client: Owner / Client
Design & drawings: Claude Code

- DRAWING NOTES
- Do not scale from this drawing. Use figured dimensions only.
 - All dimensions in millimetres; levels in metres relative to internal FFL ± 0.000 (datum to be tied to site survey).
 - Contractor to verify all dimensions, levels & existing structure on site before fabrication or ordering.
 - Read with all other architectural, structural & services drawings and the specification notes (A-001).
 - Structural members are preliminary: final design, connections & calculations by a licensed structural engineer to local code before construction.
 - Report any discrepancy to the designer before proceeding.

REVISIONS		
Rev	Date	Description
C19	08.10.2026	Shadow study re-run: north towards the upper-left of the plan
C18	08.10.2026	Shadow study May-Aug: triangle C2 / square D
C17	08.10.2026	Option C2: tip at the AC line

SHADOW STUDY — orientation per client: NORTH towards the upper-left corner of the plan (tall wall faces NE)

DRAWING TITLE
SHADOW STUDY
SQUARE roof

SCALE @ A3	DATE
NTS (plan views)	08.10.2026
DRAWN / CHECKED	SERIES
CC / —	SUN / SHADOW

DRAWING No. REV

SH-03 C19