


OPTION F — TRIANGLE, WALL EDGE 3.06 (as E), PLANTS EDGE 4.37


TALL HOUSE WALL (exist., AC units)

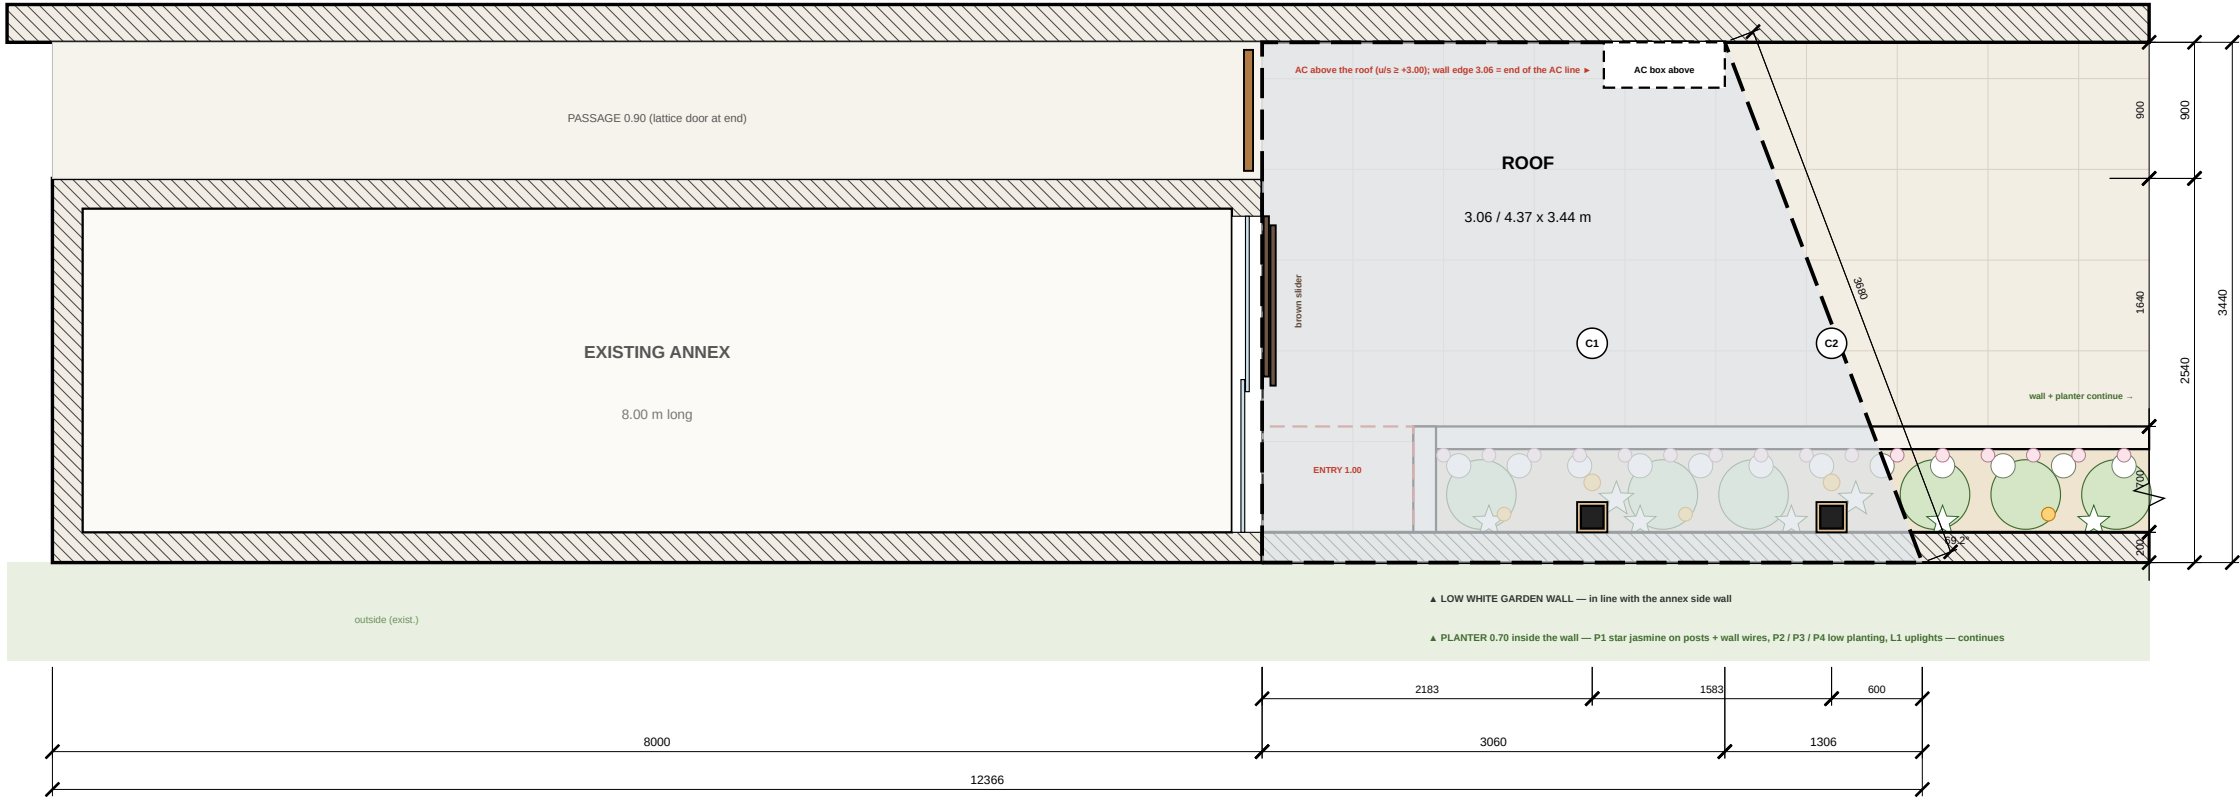

1 TOP VIEW — ANNEX, GARDEN & ROOF

1:50 @ A3 — annex + garden wall in one line; planter 0.70 continues; entry 1.00 at the door


2/V1T-01 ROOF FRAMING PLAN — 1:30

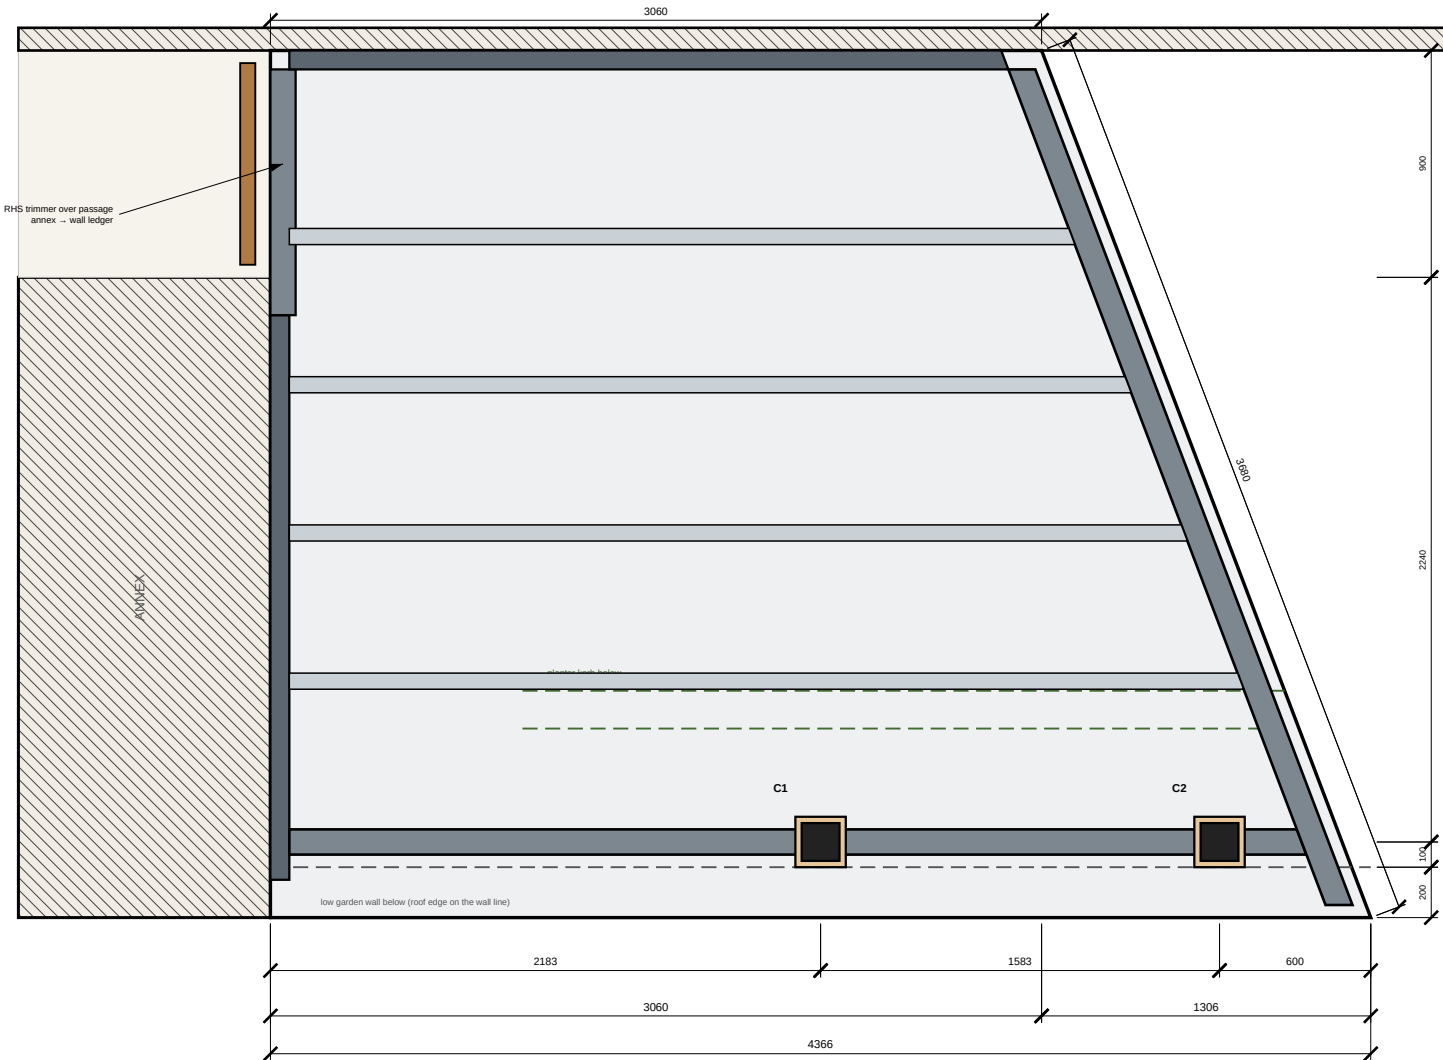


THIS VERSION

triangular roof to the tall wall, no void: edge at the tall wall 3.06 (same as option E, to the end of the AC line, AC above the roof); plants edge 4.37 (C2 angle); columns end flush under the roof (nothing above the fascia); 2 columns against the garden wall.
Roof fixed to the annex end façade AND to the tall house wall (steel ledgers, resin anchors); covers the passage in front of the lattice door (RHS trimmer over the passage, annex — wall ledger).
Triangle: edge at the tall wall 3.06 m (same as option E, to the end of the AC line); plants edge 4.37 m; edge at the annex line 3.40 m; raked edge 3.68 m at 69.2° to the plants edge.
C1 in the middle of the 4.37 edge (2.18 from the façade); C2 0.60 m in from the tip (the tip cantilevers 0.60).
Joists run from the annex ledger to the raked edge beam (max. span = 3.2 m); over the passage they bear on the RHS trimmer + wall ledger.
COMMON
Annex side wall and low white garden wall are ONE line; the roof's plants edge (fascia) is on it.
Planter 0.70 inside the wall (soil + white kerb), continues along the wall; paved entry space 1.00 between the façade and the planter (walk in to the left glass door).
Entrance opening runs to the side wall (no pier).
C1 / C2: SHS 150 clad 200x200 thermo-ash, against the garden wall, 2 SS brackets each into the wall; edge beam on the column line, roof cantilevers 0.30 to the fascia over the wall.
Underside +2.36, fascia 0.43 (top +2.79); columns flush under the roof. Falls 1.70 to the box gutter on the raked edge; rainwater down C2.

3/V1T-01 3D — BIRD'S EYE (from outside, over the low garden wall)

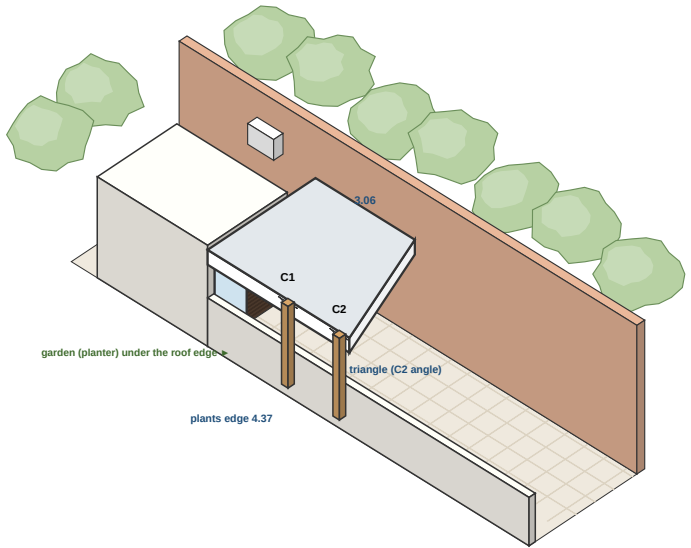

SCALE BAR 1:50 (top view)

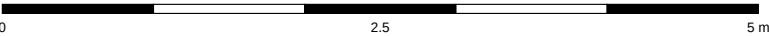

COURTYARD ROOF — V1T

OPTION F — TRIANGLE, WALL EDGE 3.06 (as E), PLANTS EDGE 4.37:
triangular roof to the tall wall, no void: edge at the tall wall 3.06 (same as option E, to the end of the AC line, AC above the roof); plants edge 4.37 (C2 angle); columns end flush under the roof (nothing above the fascia); 2 columns against the garden wall
Client: Owner / Client
Design & drawings: Claude Code

DRAWING NOTES

- Do not scale from this drawing. Use figured dimensions only.
- All dimensions in millimetres; levels in metres relative to internal FFL ± 0.000 (datum to be tied to site survey).
- Contractor to verify all dimensions, levels & existing structure on site before fabrication or ordering.
- Read with all other architectural, structural & services drawings and the specification notes (A-001).
- Structural members are preliminary: final design, connections & calculations by a licensed structural engineer to local code before construction.
- Report any discrepancy to the designer before proceeding.

REVISIONS

Rev	Date	Description
C22	08.10.2026	Option F triangle (wall edge 3.06 as E); columns flush under the roof (E + F)
C21	08.10.2026	Column tops painted like the roof front (fascia RAL 9010)

FOR CLIENT CHECK — options E (rectangle) and F (triangle), wall edge 3.06, AC above, columns flush under the roof

DRAWING TITLE

OPTION F — TRIANGLE
top view & roof framing

SCALE @ A3

1:50 / 1:30

DRAWN / CHECKED

CC / —

DATE

08.10.2026

SERIES

ARCHITECTURAL

DRAWING No.


REV

C22-F

C22

OPTION E — RECTANGLE 3.06 x 3.44 TO THE AC LINE


TALL HOUSE WALL (exist., AC units)

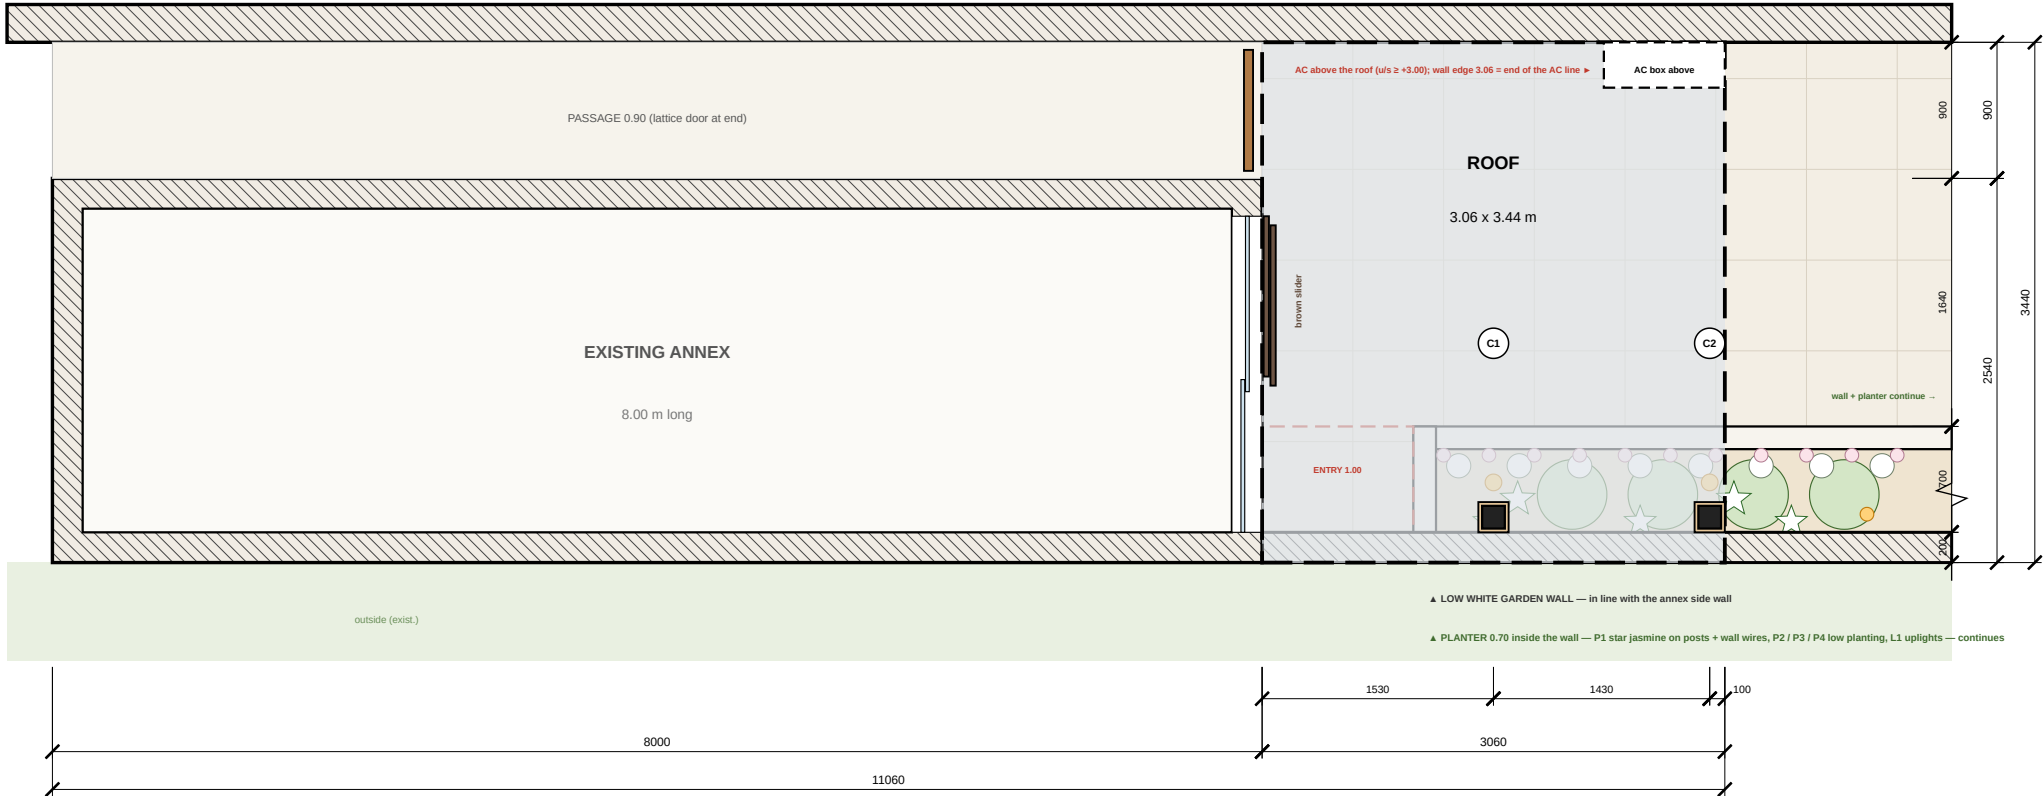

1 TOP VIEW — ANNEX, GARDEN & ROOF

V1-01 1:50 @ A3 — annex + garden wall in one line; planter 0.70 continues; entry 1.00 at the door

2/V1-01 ROOF FRAMING PLAN — 1:30

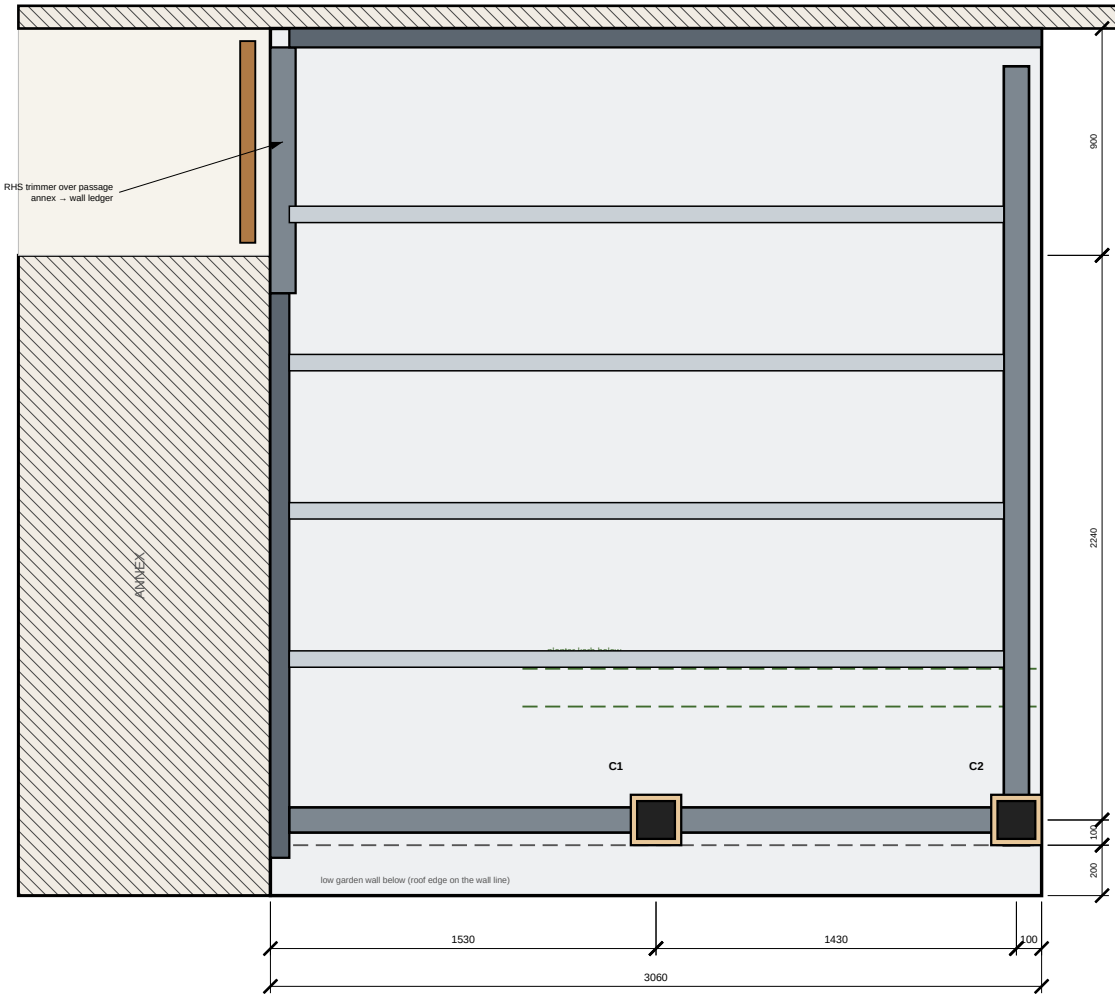

THIS VERSION

roof made longer: 3.06 x 3.44 to the tall wall, no void; right edge in line with the end of the AC box, the AC sits above the roof; bears on the annex ledger + a ledger on the tall wall; 2 columns against the garden wall.

Roof fixed to the annex end façade AND to the tall house wall (steel ledgers, resin anchors); covers the passage in front of the lattice door (RHS trimmer over the passage, annex — wall ledger).

Columns end under the roof surface — nothing sticks out above the fascia (top +2.79); the part above the soffits is painted RAL 9010.

C1 in the middle of the plants edge, C2 at the corner; roof 3.06 long on both sides — right edge in line with the end of the AC box; the AC sits above the roof (u/s ≥ +3.00, verify / re-hang on brackets).

COMMON


Annex side wall and low white garden wall are ONE line; the roof's plants edge (fascia) is on it.

Planter 0.70 inside the wall (soil + white kerb), continues along the wall; paved entry space 1.00 between the façade and the planter (walk in to the left glass door). Entrance opening runs to the side wall (no pier).

C1 / C2: SHS 150 clad 200x200 thermo-ash, against the garden wall, 2 SS brackets each into the wall; edge beam on the column line, roof cantilevers 0.30 to the fascia over the wall.

Underside +2.36, fascia 0.43 (top +2.79); columns flush under the roof. Falls 1.70 to the box gutter on the raked edge; rainwater down C2.

3/V1-01 3D — BIRD'S EYE (from outside, over the low garden wall)

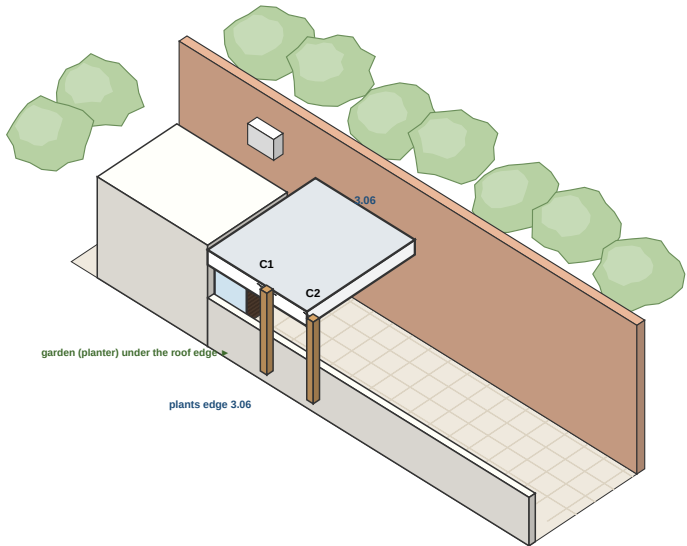

SCALE BAR 1:50 (top view)



COURTYARD ROOF — V1

OPTION E — RECTANGLE 3.06 x 3.44 TO THE AC LINE: roof made longer:

3.06 x 3.44 to the tall wall, no void; right edge in line with the end of the AC box, the AC sits above the roof; bears on the annex

ledger + a ledger on the tall wall; 2 columns against the garden wall

Client: Owner / Client

Design & drawings: Claude Code

DRAWING NOTES

- Do not scale from this drawing. Use figured dimensions only.
- All dimensions in millimetres; levels in metres relative to internal FFL ±0.000 (datum to be tied to site survey).
- Contractor to verify all dimensions, levels & existing structure on site before fabrication or ordering.
- Read with all other architectural, structural & services drawings and the specification notes (A-001).
- Structural members are preliminary: final design, connections & calculations by a licensed structural engineer to local code before construction.
- Report any discrepancy to the designer before proceeding.

REVISIONS

Rev	Date	Description
C22	08.10.2026	Option F triangle (wall edge 3.06 as E); columns flush under the roof (E + F)
C21	08.10.2026	Column tops painted like the roof front (fascia RAL 9010)

FOR CLIENT CHECK — options E (rectangle) and F (triangle), wall edge 3.06, AC above, columns flush under the roof

DRAWING TITLE

OPTION E — RECTANGLE 3.06
top view & roof framing

SCALE @ A3

1:50 / 1:30

DATE

08.10.2026

DRAWN / CHECKED

CC / —

SERIES

ARCHITECTURAL

DRAWING No.

REV

C22-E

C22