


VERSION 1 — ROOF TO THE WALL


TALL HOUSE WALL (exist., AC units)

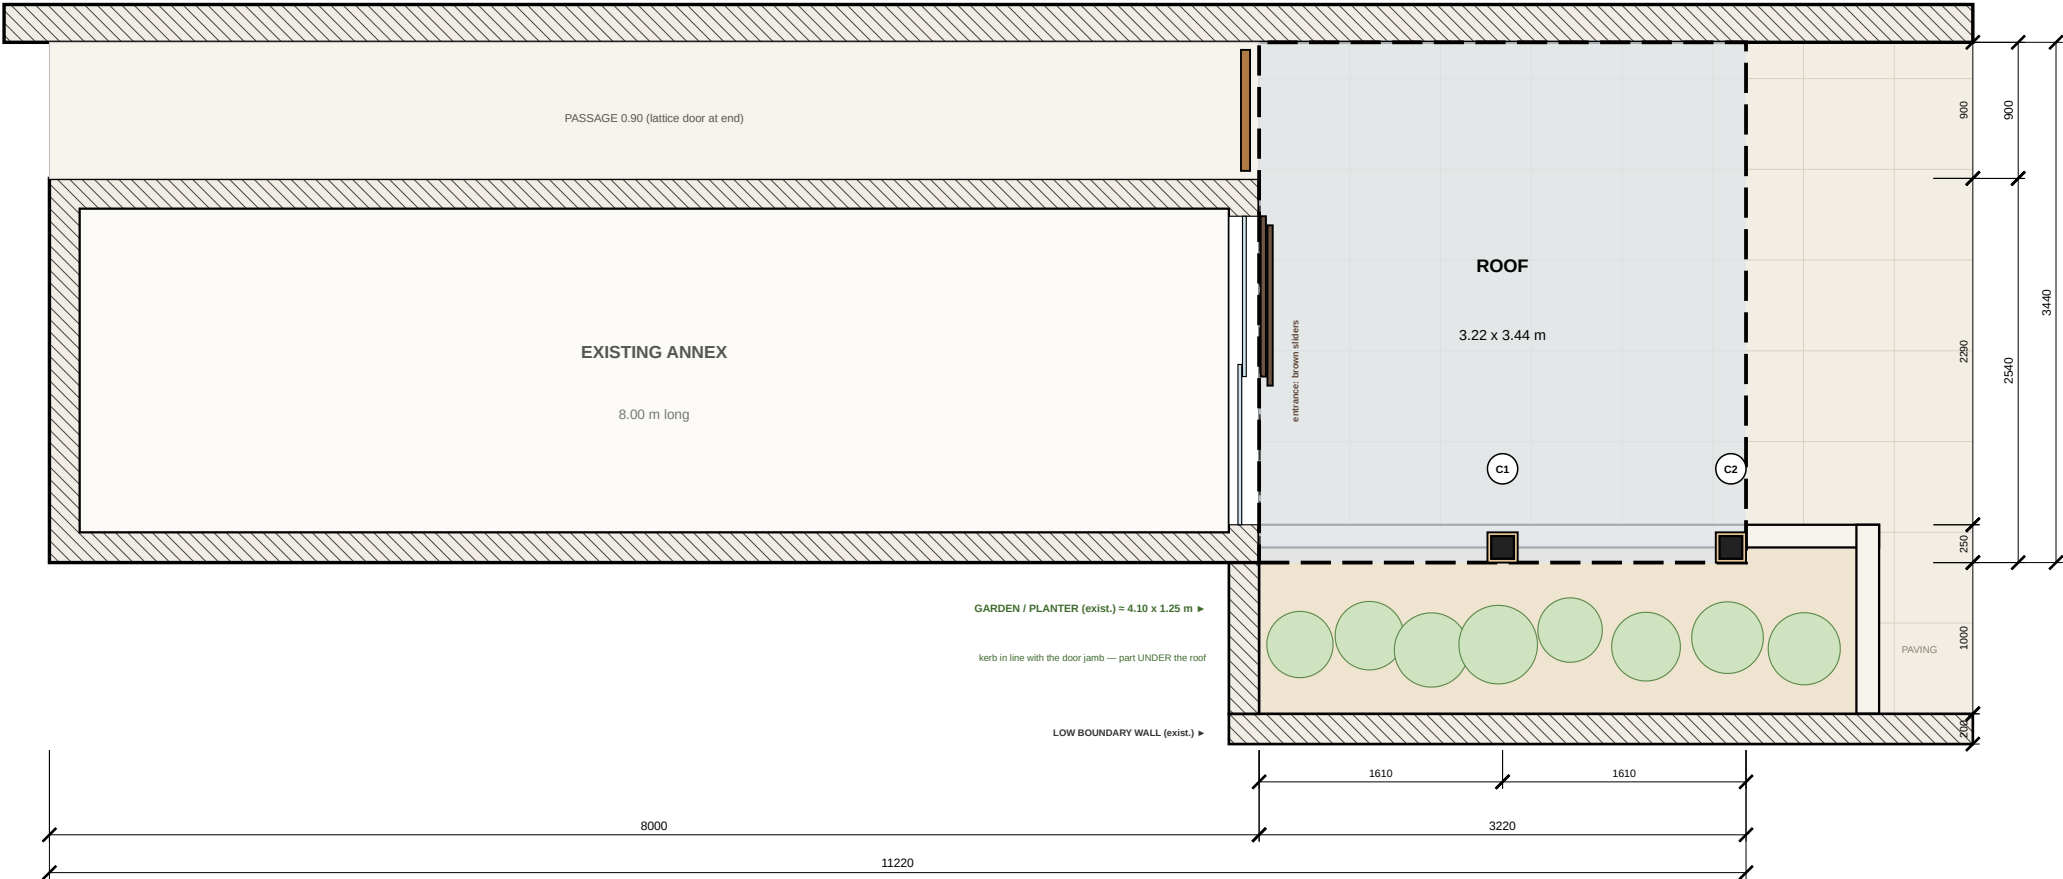

1 TOP VIEW — ANNEX, GARDEN & ROOF
V1-01

1:50 @ A3 — garden = planter in front of the façade, left of the door; trees = background


2/V1-01 ROOF FRAMING PLAN — 1:30

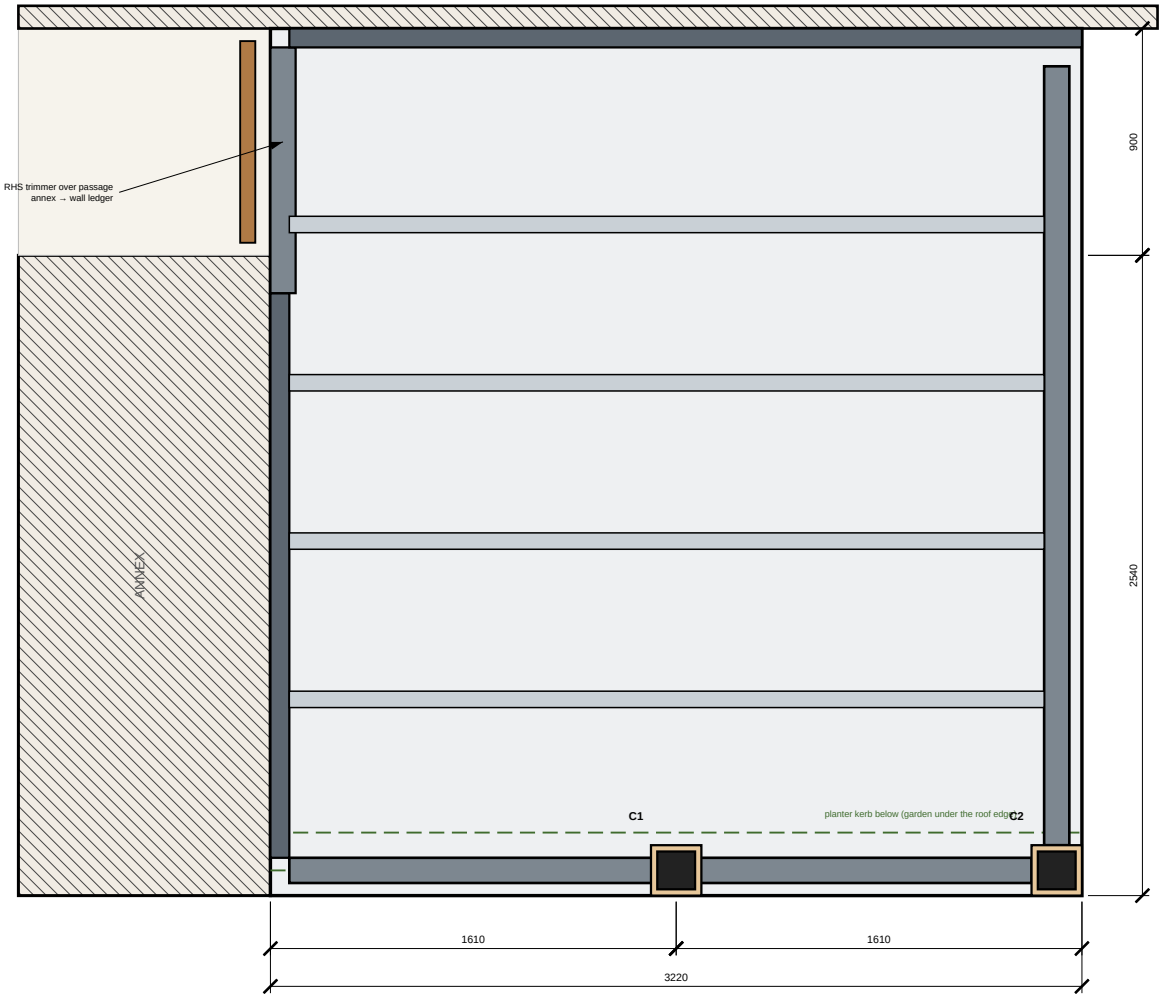


THIS VERSION

roof 3.22 x 3.44 up to the tall wall (bears on wall ledger + curved brackets); 2 columns on the plants side.
Roof fixed to the annex end façade AND to the tall house wall (steel ledgers, resin anchors); covers the passage in front of the lattice door (RHS trimmer over the passage, annex - wall ledger).
C1 in the middle of the plants edge, C2 at the corner.
COMMON
Roof 3.22 m from the annex façade along the top edge. Underside +2.36, fascia 0.43 (top +2.79); columns 200x200, 0.13 above roof, curved bracket under the junction (client section).
Garden = existing planter in front of the façade, left of the door: white kerb in line with the door jamb (0.25 from the corner), so kerb + edge of the planter are UNDER the roof. C1 + C2 stand in the planter. Planter length = 4.10 m (from site photo — confirm).
Falls 1:70 to the concealed gutter at the free edge; rainwater down C2.

3/V1-01 3D — BIRD'S EYE (from the plants side, over the low wall)

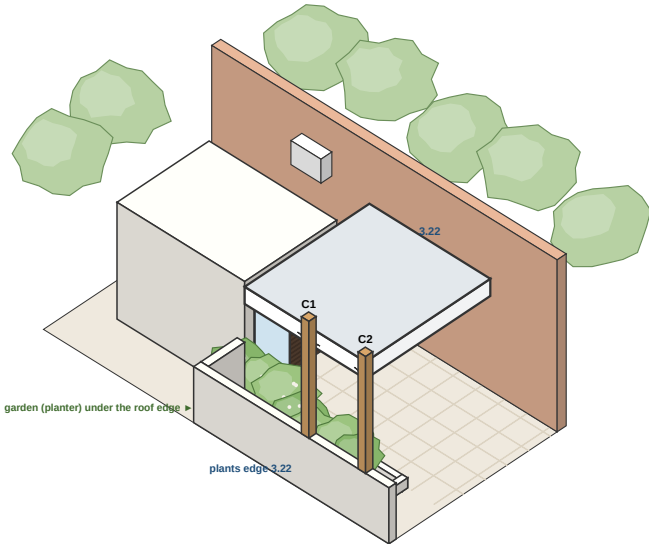

SCALE BAR 1:50 (top view)

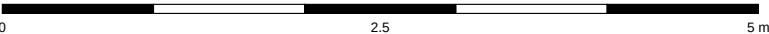

COURTYARD ROOF — V1

VERSION 1 — ROOF TO THE WALL: roof 3.22 x 3.44 up to the tall wall (bears on wall ledger + curved brackets); 2 columns on the plants side
Client: Owner / Client
Design & drawings: Claude Code

DRAWING NOTES

- Do not scale from this drawing. Use figured dimensions only.
- All dimensions in millimetres; levels in metres relative to internal FFL ± 0.000 (datum to be tied to site survey).
- Contractor to verify all dimensions, levels & existing structure on site before fabrication or ordering.
- Read with all other architectural, structural & services drawings and the specification notes (A-001).
- Structural members are preliminary: final design, connections & calculations by a licensed structural engineer to local code before construction.
- Report any discrepancy to the designer before proceeding.

REVISIONS

Rev	Date	Description
C06	07.10.2026	Garden = planter in front of the façade, left of the door, partly under roof
C05	07.10.2026	Triangular versions V1T/V2T; 3D views; details D3
C04	07.10.2026	Two versions V1/V2 per client sections & site photo
C02	07.10.2026	Canopy to client sketch: 8.00 house, roof 3.22, u/s 2.36, fascia 0.43

PREVIEW FOR CLIENT REVIEW — per client sketch, mark-ups & site photo; not for construction

DRAWING TITLE

V1 ROOF TO WALL
top view & roof framing

SCALE @ A3

1:50 / 1:30

DRAWN / CHECKED

CC / —

DATE

07.10.2026

SERIES

ARCHITECTURAL

DRAWING No.


V1-01

REV


C06

VERSION 1 — ROOF TO THE WALL

1/V1-02 VIEW TO ANNEX FAÇADE (as site photo) — 1:50

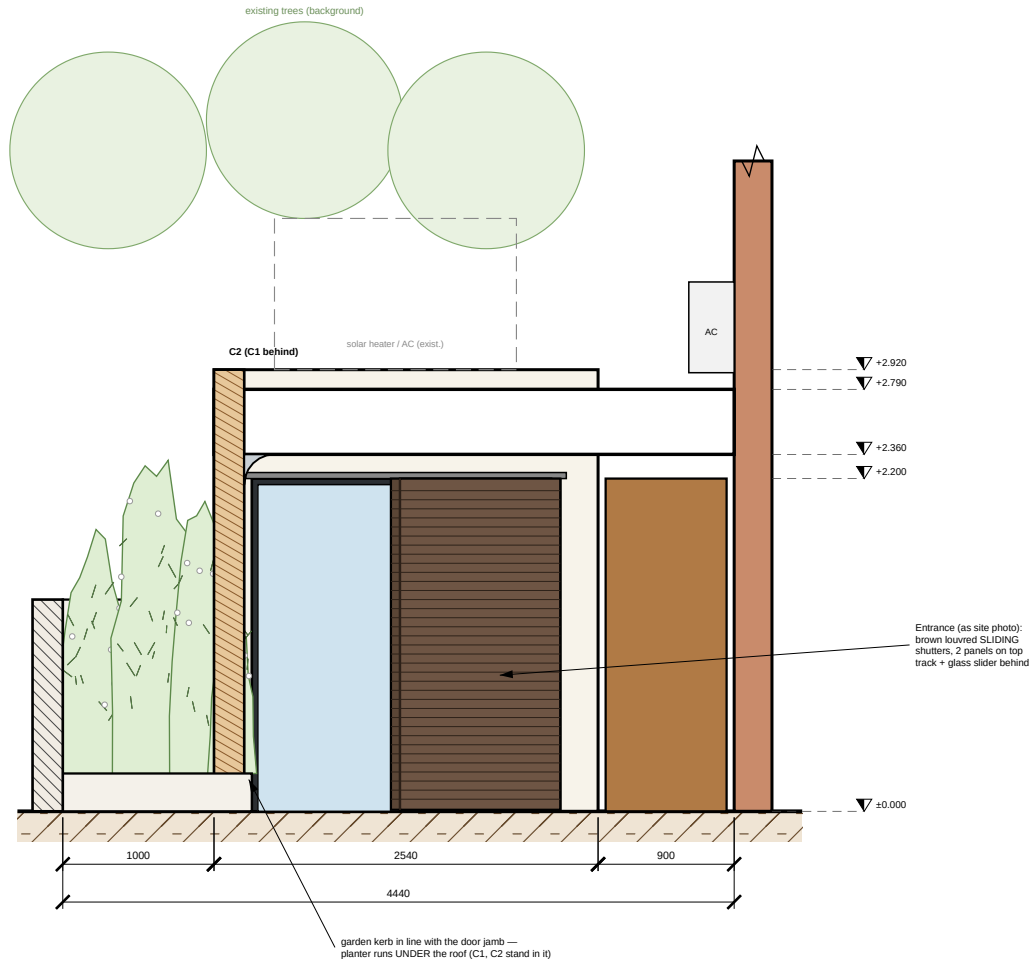


2/V1-02 PLANTS-SIDE ELEVATION — C1 + C2 — 1:50

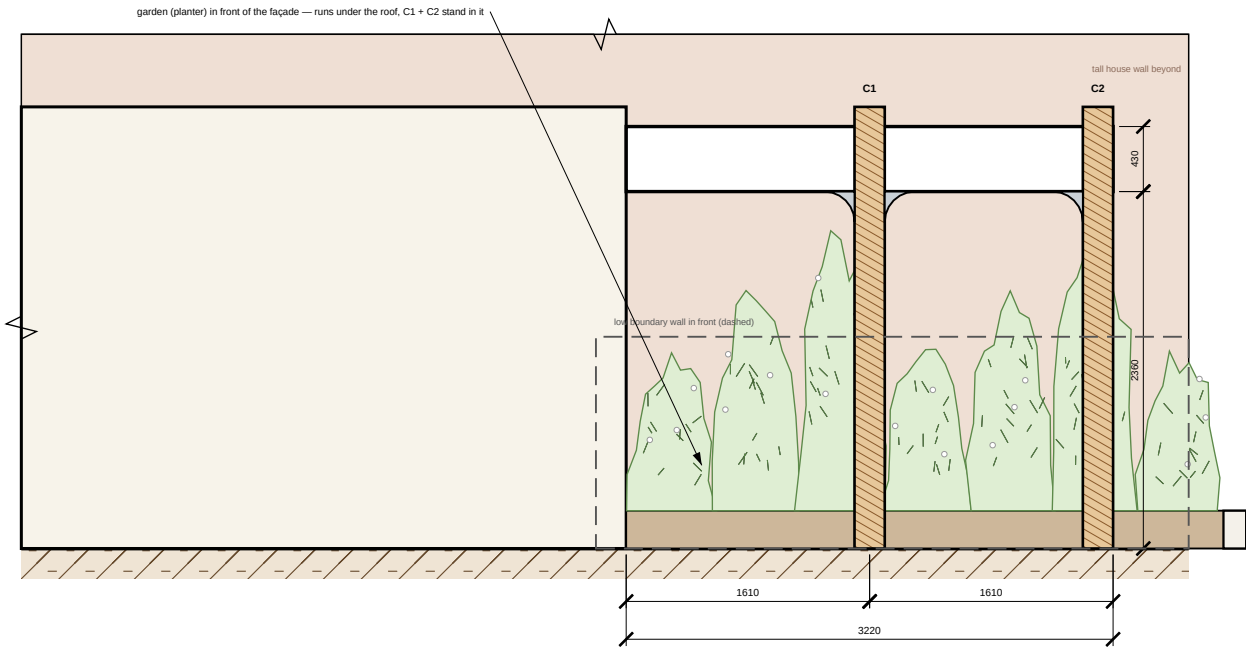


NOTES
roof 3.22 x 3.44 up to the tall wall (bears on wall ledger + curved brackets); 2 columns on the plants side.
Underside +2.36, fascia 0.43 (top +2.79); columns 0.13 above roof.
Garden = existing planter in front of the façade, left of the door; its kerb is in line with the door jamb, so part of it is UNDER the roof (C1 + C2 stand in it). Trees are existing, in the background.
Refined roof section & details: sheet V1-03.

3/V1-02 SECTION ACROSS AT C1 — 1:50 (refined: V1-03)

tall wall left — plants side right

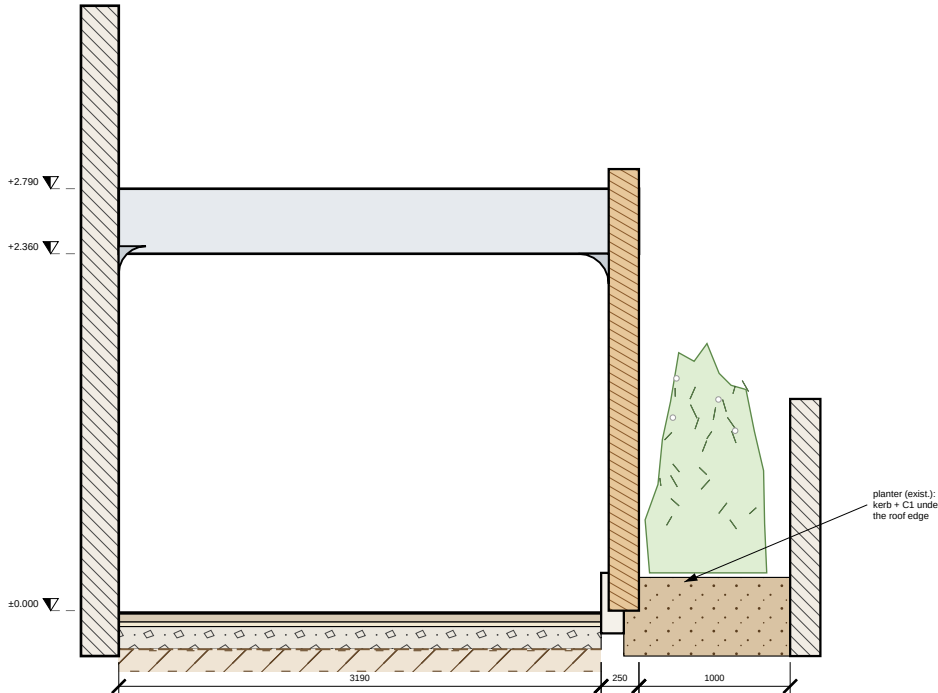

4/V1-02 3D — EYE LEVEL, SAME DIRECTION AS THE SITE PHOTO

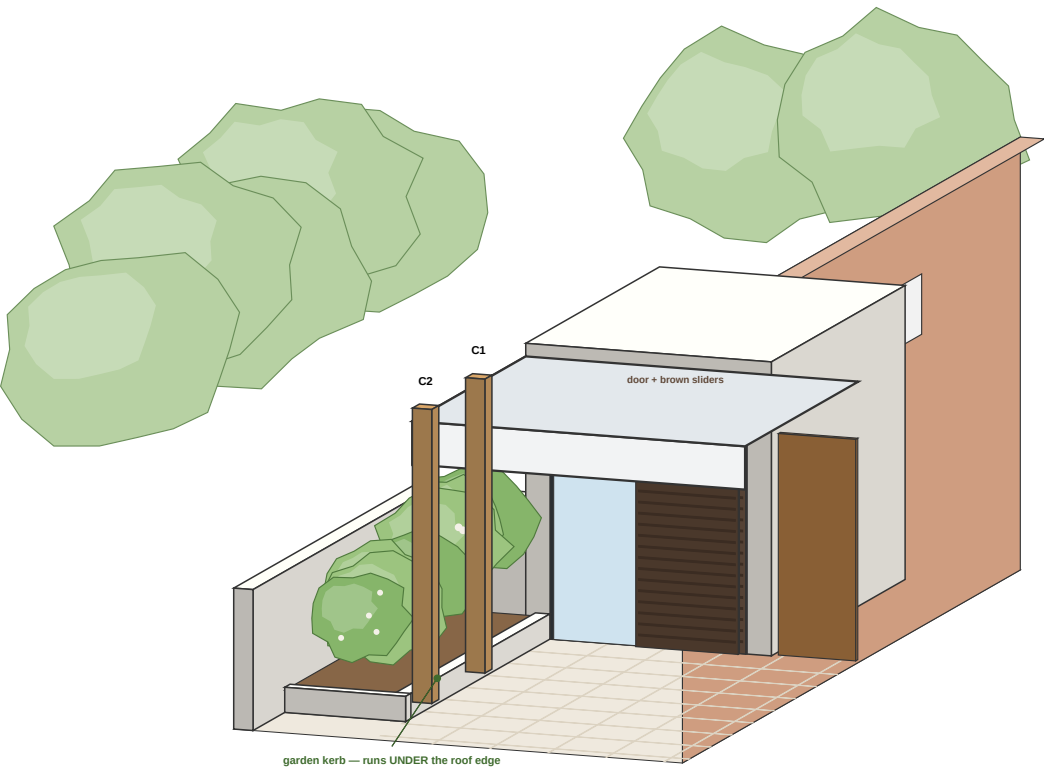

COURTYARD ROOF — V1

VERSION 1 — ROOF TO THE WALL: roof 3.22 x 3.44 up to the tall wall (bears on wall ledger + curved brackets); 2 columns on the plants side
Client: Owner / Client
Design & drawings: Claude Code

- DRAWING NOTES**
- Do not scale from this drawing. Use figured dimensions only.
 - All dimensions in millimetres; levels in metres relative to internal FFL ±0.000 (datum to be tied to site survey).
 - Contractor to verify all dimensions, levels & existing structure on site before fabrication or ordering.
 - Read with all other architectural, structural & services drawings and the specification notes (A-001).
 - Structural members are preliminary: final design, connections & calculations by a licensed structural engineer to local code before construction.
 - Report any discrepancy to the designer before proceeding.

REVISIONS		
Rev	Date	Description
C06	07.10.2026	Garden = planter in front of the façade, left of the door, partly under roof
C05	07.10.2026	Triangular versions V1T/V2T; 3D views; details D3
C04	07.10.2026	Two versions V1/V2 per client sections & site photo
C02	07.10.2026	Canopy to client sketch: 8.00 house, roof 3.22, u/s 2.36, fascia 0.43

PREVIEW FOR CLIENT REVIEW — per client sketch, mark-ups & site photo; not for construction

DRAWING TITLE
V1 ROOF TO WALL
views, section & 3D view

SCALE @ A3 1:50	DATE 07.10.2026
DRAWN / CHECKED CC / —	SERIES ARCHITECTURAL


DRAWING No. REV

V1-02 **C06**


VERSION 1 — ROOF TO THE WALL

1/V1-03 ROOF SECTION ACROSS AT C1 — 1:30 (planter under the roof edge)


(as client sketch A: roof runs to the wall)

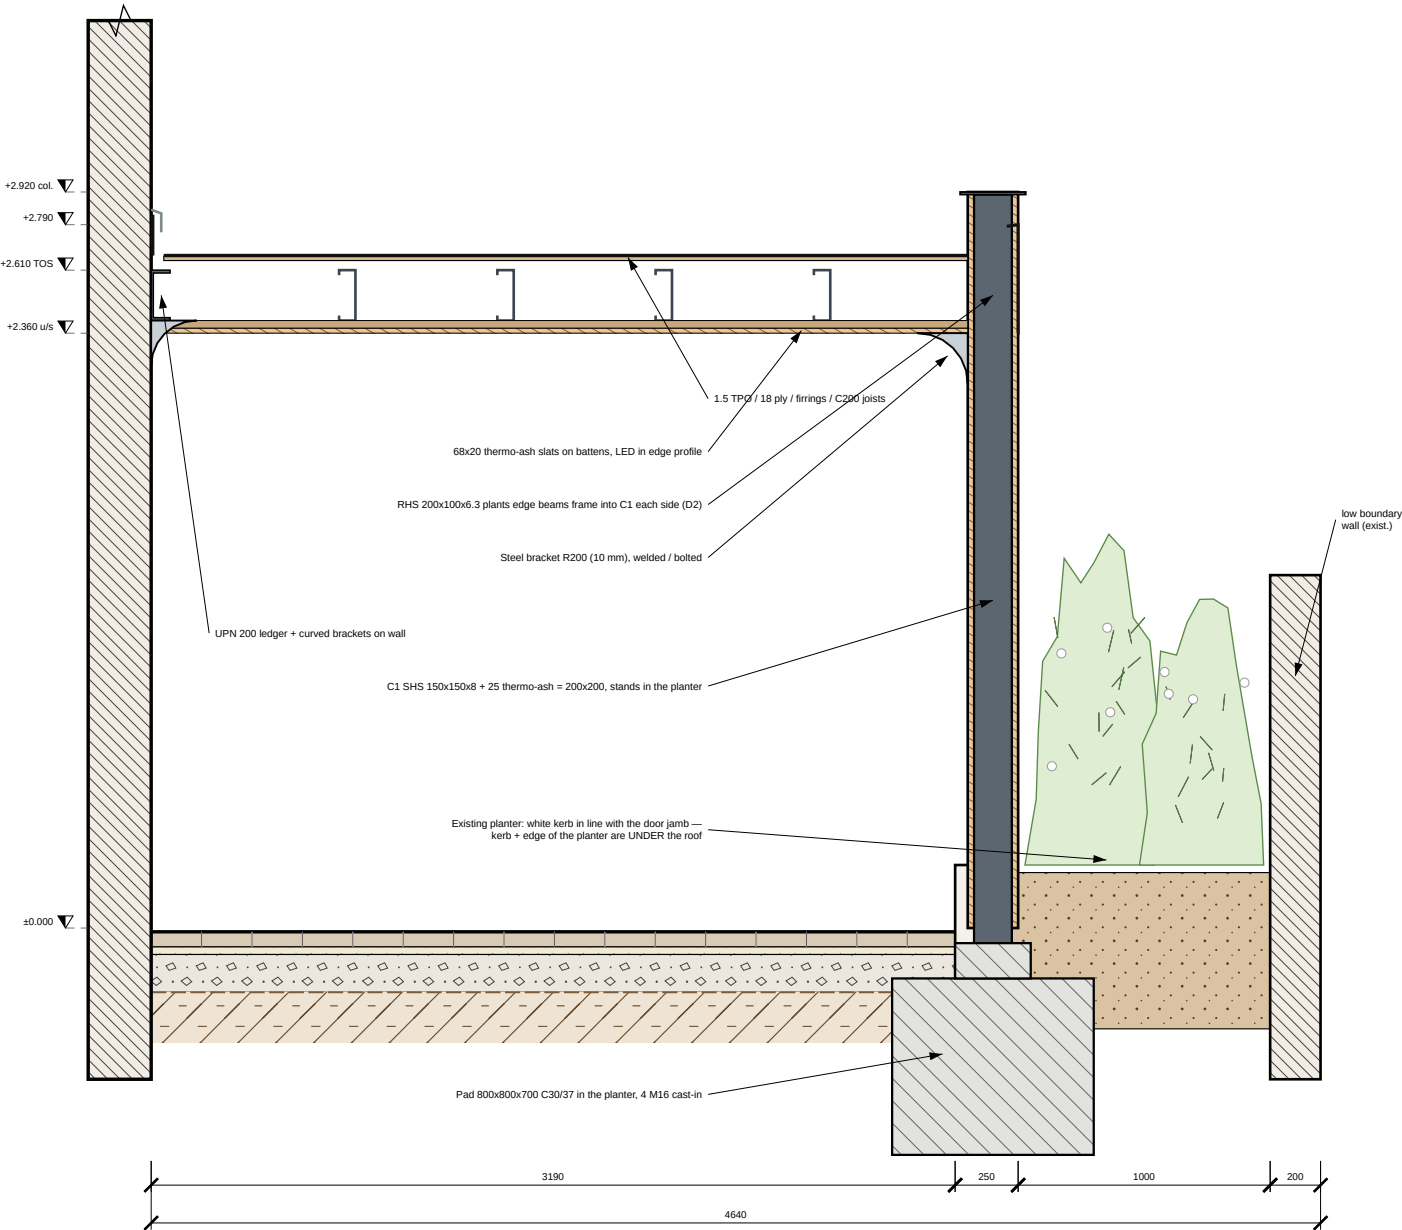


SPECIFICATION
Steel S355, hot-dip galvanised; columns & brackets powder-coated RAL 9010 or timber-clad (thermo-ash).
Roof: TPO 1.5 on 18 mm marine ply on tapered firings (fall 1:70 to the free-edge box gutter).
Soffit: thermo-ash 68x20 slats, LED 2700 K in perimeter profile. Fascia 3 mm aluminium RAL 9010, 0.43 m.
Wall ledger & brackets into sound masonry/RC — engineer to confirm anchors.

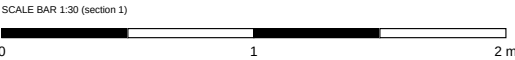


D1 ROOF TO WALL (client sketch A) — 1:15

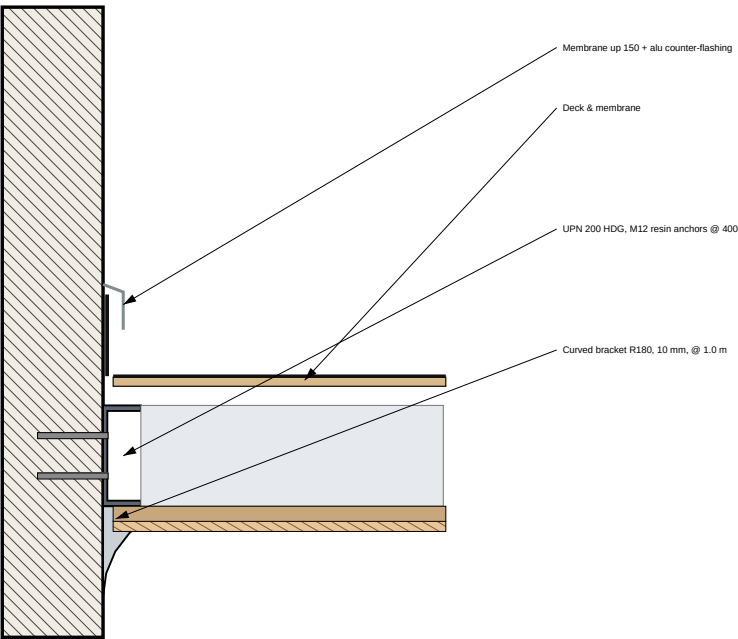

D2 COLUMN / ROOF JUNCTION (plants side) — 1:15

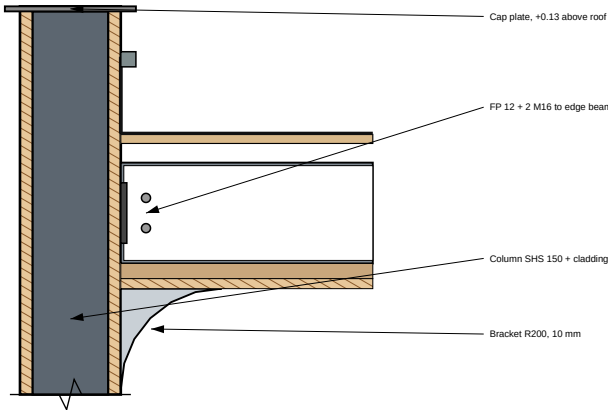

D3 CORNER AT C2 — PLAN 1:15

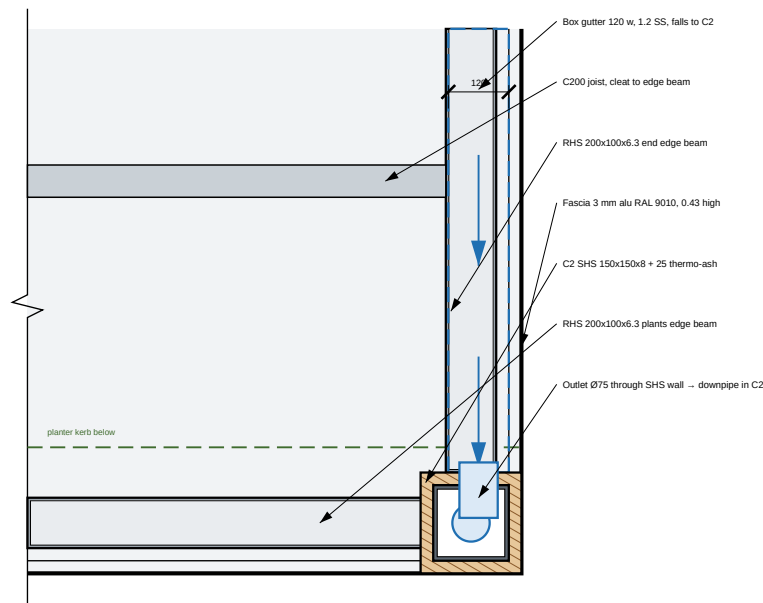

COURTYARD ROOF — V1

VERSION 1 — ROOF TO THE WALL: roof 3.22 x 3.44 up to the tall wall (bears on wall ledger + curved brackets); 2 columns on the plants side
Client: Owner / Client
Design & drawings: Claude Code

- DRAWING NOTES**
- Do not scale from this drawing. Use figured dimensions only.
 - All dimensions in millimetres; levels in metres relative to internal FFL ±0.000 (datum to be tied to site survey).
 - Contractor to verify all dimensions, levels & existing structure on site before fabrication or ordering.
 - Read with all other architectural, structural & services drawings and the specification notes (A-001).
 - Structural members are preliminary: final design, connections & calculations by a licensed structural engineer to local code before construction.
 - Report any discrepancy to the designer before proceeding.

REVISIONS		
Rev	Date	Description
C06	07.10.2026	Garden = planter in front of the façade, left of the door, partly under roof
C05	07.10.2026	Triangular versions V1T/V2T; 3D views; details D3
C04	07.10.2026	Two versions V1/V2 per client sections & site photo
C02	07.10.2026	Canopy to client sketch: 8.00 house, roof 3.22, u/s 2.36, fascia 0.43


PREVIEW FOR CLIENT REVIEW — per client sketch, mark-ups & site photo; not for construction

DRAWING TITLE	
V1 ROOF TO WALL roof section & details	
SCALE @ A3 1:30 / 1:15 / 1:20	DATE 07.10.2026
DRAWN / CHECKED CC / —	SERIES ARCHITECTURAL

DRAWING No. V1-03
REV C06

VERSION 2 — 0.90 m VOID + 2 STEEL RODS


TALL HOUSE WALL (exist., AC units)

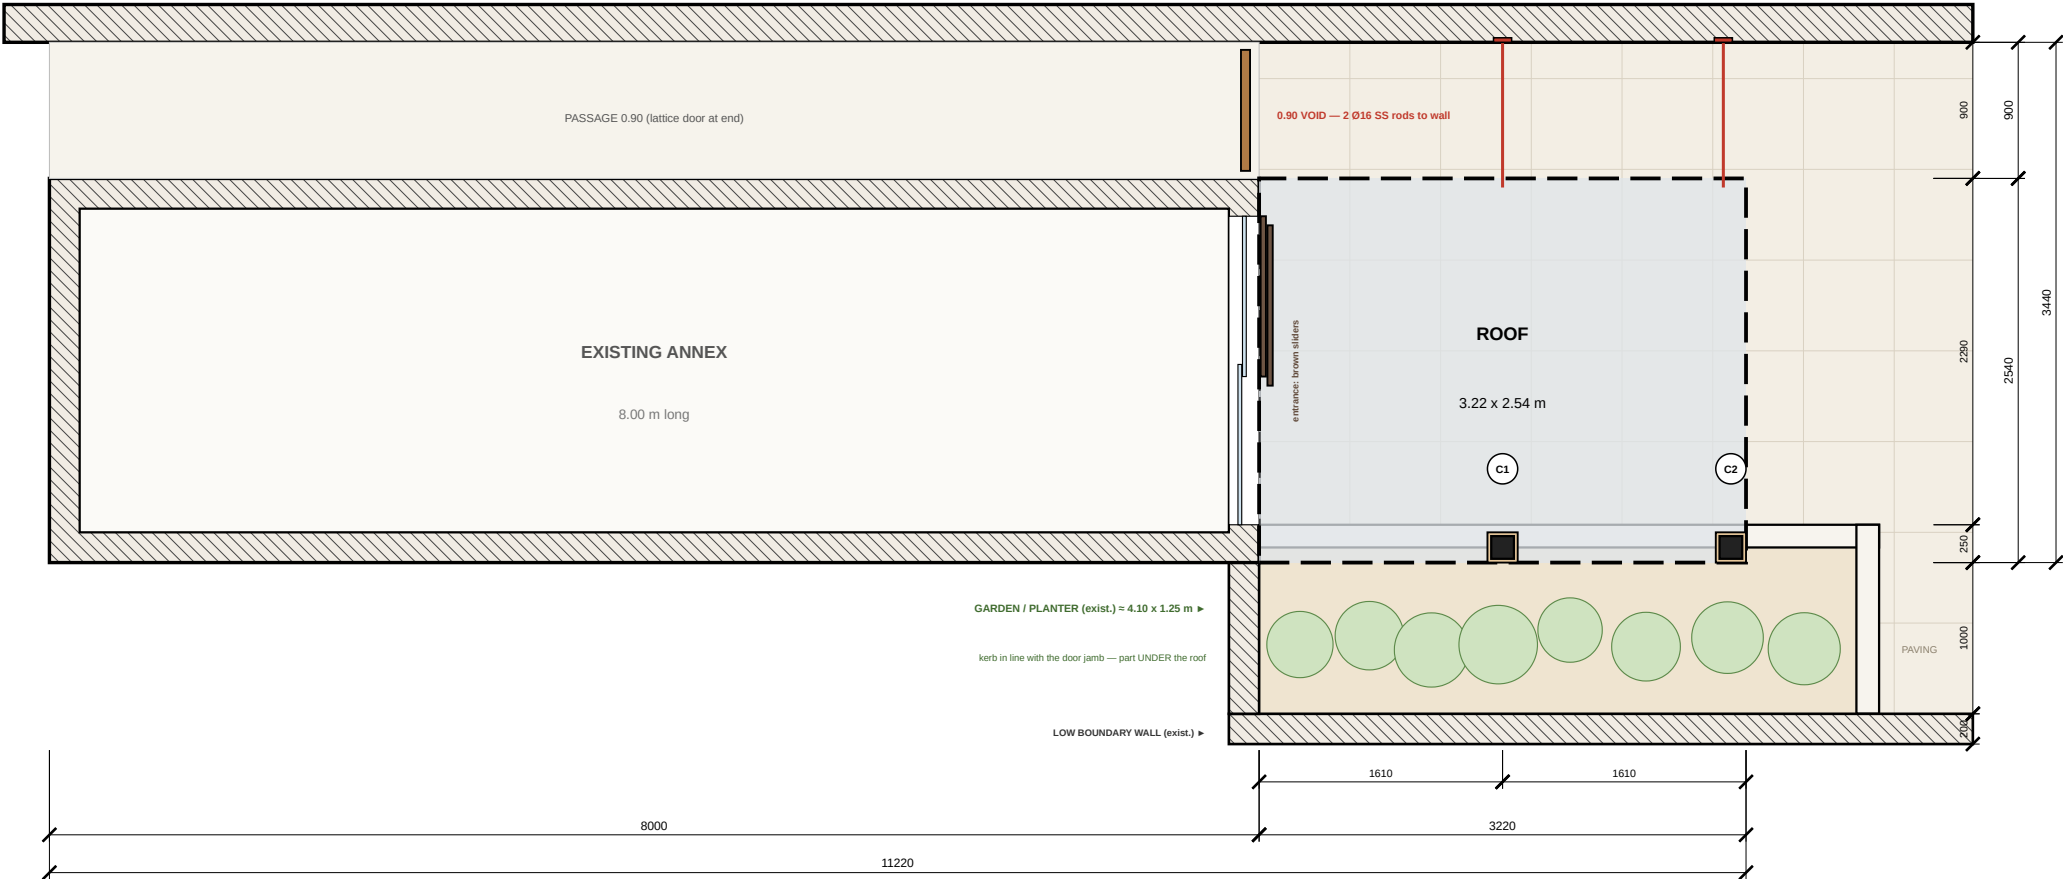

1 TOP VIEW — ANNEX, GARDEN & ROOF

1:50 @ A3 — garden = planter in front of the façade, left of the door; trees = background


2/V2-01 ROOF FRAMING PLAN — 1:30

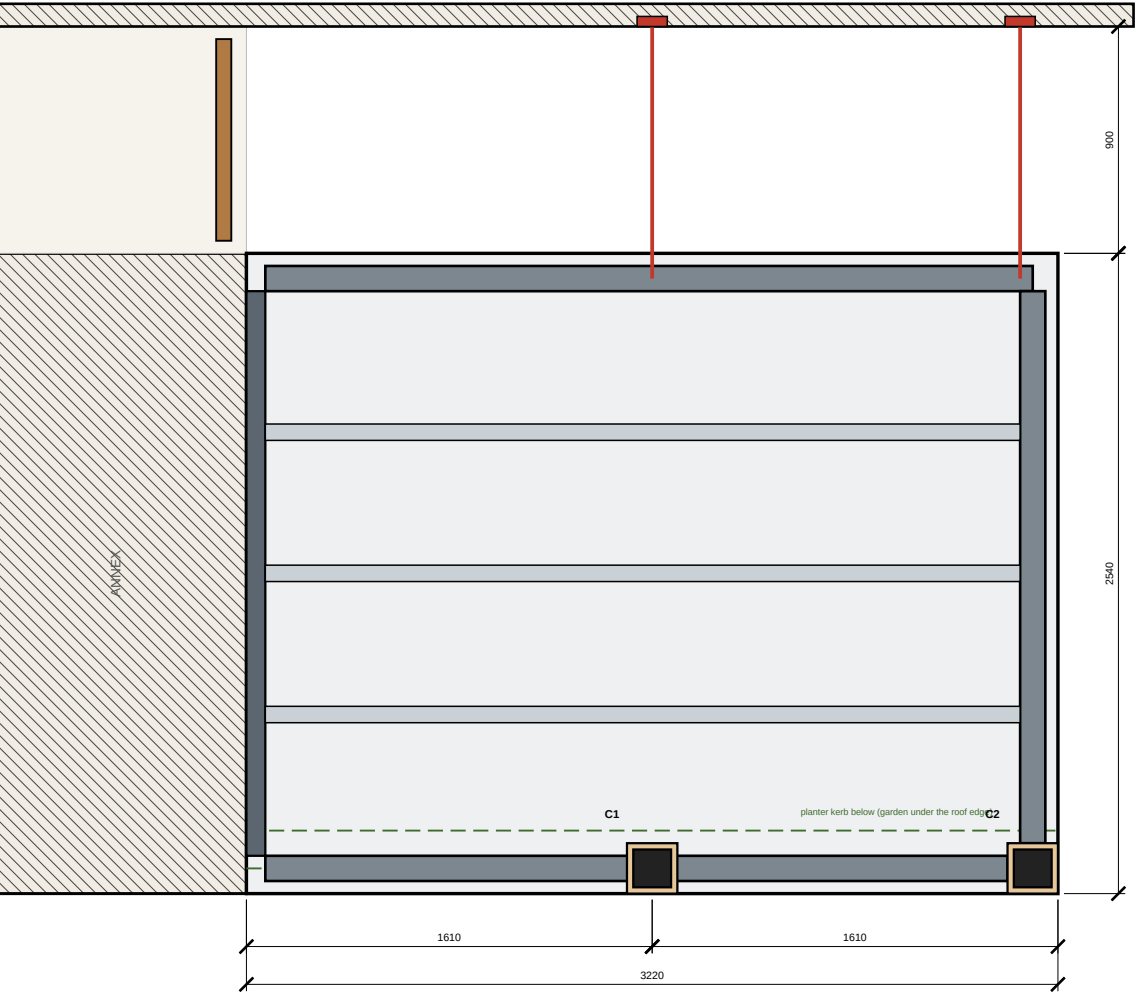

THIS VERSION
roof 3.22 x 2.54; 0.90 m void left open; void edge tied to the tall wall with 2 slim Ø16 stainless rods (rising ≈ 30°); 2 columns on the plants side.
Roof fixed to the annex end façade (ledger). The 0.90 m passage to the lattice door stays open.
Void edge hung from the tall house wall on 2 Ø16 stainless rods (turnbuckles, wall plates) — slim, almost invisible.
C1 in the middle of the plants edge, C2 at the corner.

COMMON
Roof 3.22 m from the annex façade along the top edge. Underside +2.36, fascia 0.43 (top +2.79); columns 200x200, 0.13 above roof, curved bracket under the junction (client section).
Garden = existing planter in front of the façade, left of the door; white kerb in line with the door jamb (0.25 from the corner), so kerb + edge of the planter are UNDER the roof. C1 + C2 stand in the planter. Planter length = 4.10 m (from site photo — confirm).
Falls 1:70 to the concealed gutter at the free edge; rainwater down C2.

3/V2-01 3D — BIRD'S EYE (from the plants side, over the low wall)

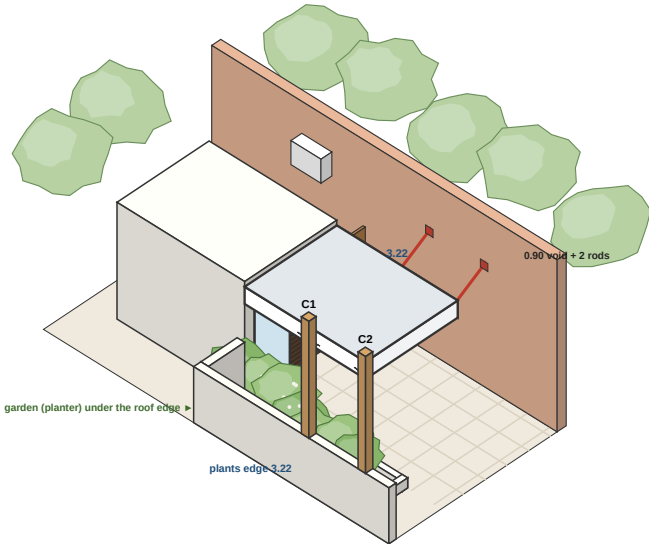

COURTYARD ROOF — V2

VERSION 2 — 0.90 m VOID + 2 STEEL RODS: roof 3.22 x 2.54; 0.90 m void left open; void edge tied to the tall wall with 2 slim Ø16 stainless rods (rising ≈ 30°); 2 columns on the plants side
Client: Owner / Client
Design & drawings: Claude Code

- DRAWING NOTES**
- Do not scale from this drawing. Use figured dimensions only.
 - All dimensions in millimetres; levels in metres relative to internal FFL ±0.000 (datum to be tied to site survey).
 - Contractor to verify all dimensions, levels & existing structure on site before fabrication or ordering.
 - Read with all other architectural, structural & services drawings and the specification notes (A-001).
 - Structural members are preliminary: final design, connections & calculations by a licensed structural engineer to local code before construction.
 - Report any discrepancy to the designer before proceeding.

REVISIONS		
Rev	Date	Description
C06	07.10.2026	Garden = planter in front of the façade, left of the door, partly under roof
C05	07.10.2026	Triangular versions V1T/V2T; 3D views; details D3
C04	07.10.2026	Two versions V1/V2 per client sections & site photo
C02	07.10.2026	Canopy to client sketch: 8.00 house, roof 3.22, u/s 2.36, fascia 0.43

PREVIEW FOR CLIENT REVIEW — per client sketch, mark-ups & site photo; not for construction


DRAWING TITLE
V2 VOID + RODS
top view & roof framing

SCALE @ A3 1:50 / 1:30	DATE 07.10.2026
DRAWN / CHECKED CC / —	SERIES ARCHITECTURAL


DRAWING No. **V2-01** REV **C06**

VERSION 2 — 0.90 m VOID + 2 STEEL RODS

1/V2-02 VIEW TO ANNEX FAÇADE (as site photo) — 1:50

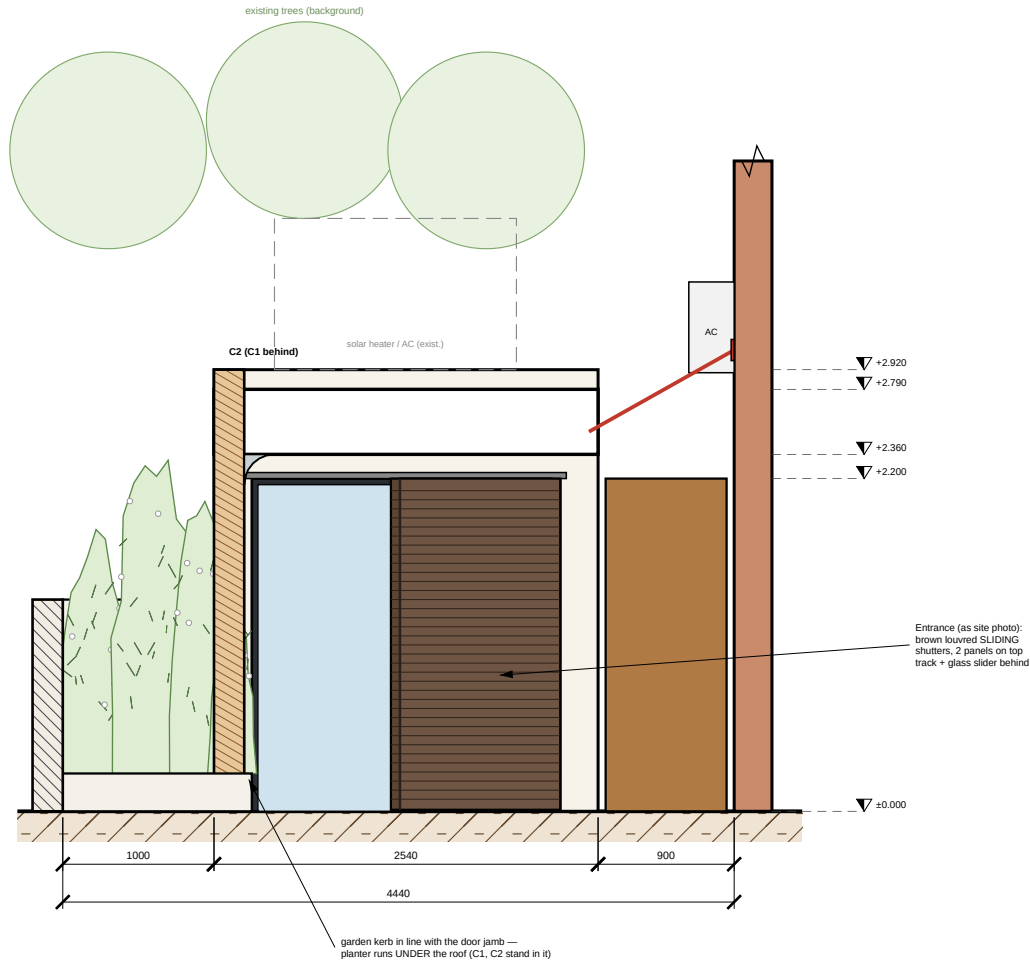


2/V2-02 PLANTS-SIDE ELEVATION — C1 + C2 — 1:50

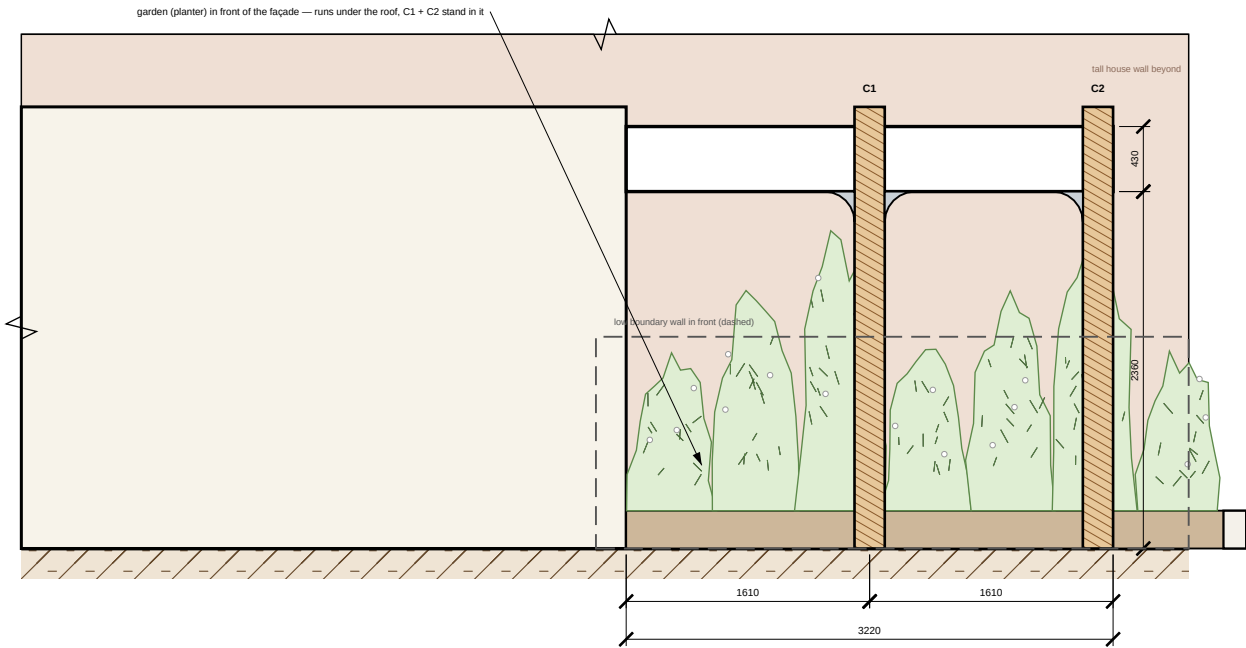


NOTES
roof 3.22 x 2.54; 0.90 m void left open; void edge tied to the tall wall with 2 slim Ø16 stainless rods (rising = 30°); 2 columns on the plants side.
Underside +2.36, fascia 0.43 (top +2.79); columns 0.13 above roof.
Garden = existing planter in front of the façade, left of the door; its kerb is in line with the door jamb, so part of it is UNDER the roof (C1 + C2 stand in it). Trees are existing, in the background.
Refined roof section & details: sheet V2-03.

3/V2-02 SECTION ACROSS AT C1 — 1:50 (refined: V2-03)

tall wall left — plants side right

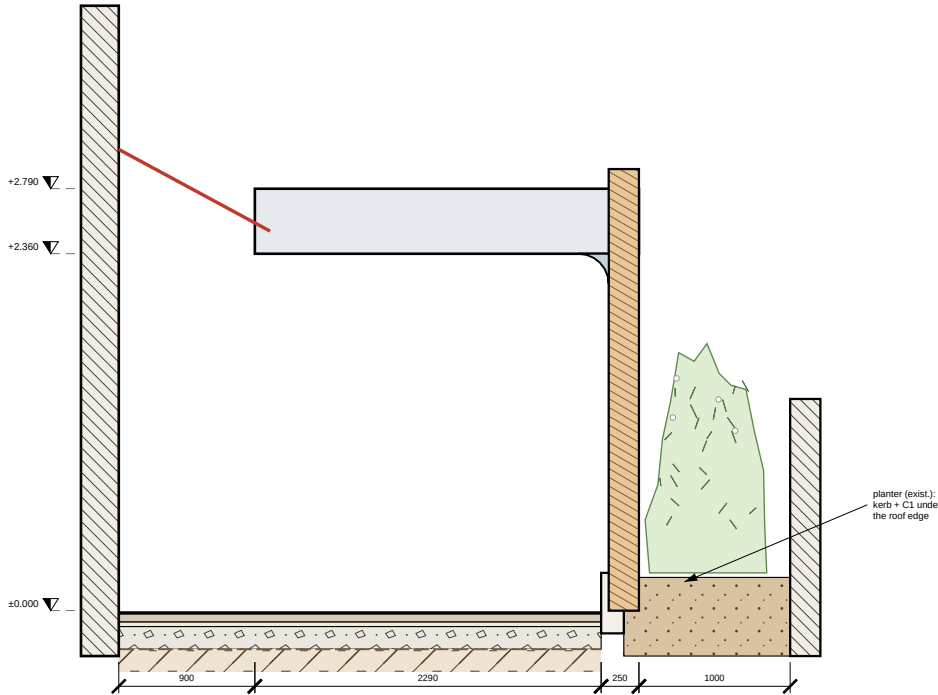

4/V2-02 3D — EYE LEVEL, SAME DIRECTION AS THE SITE PHOTO

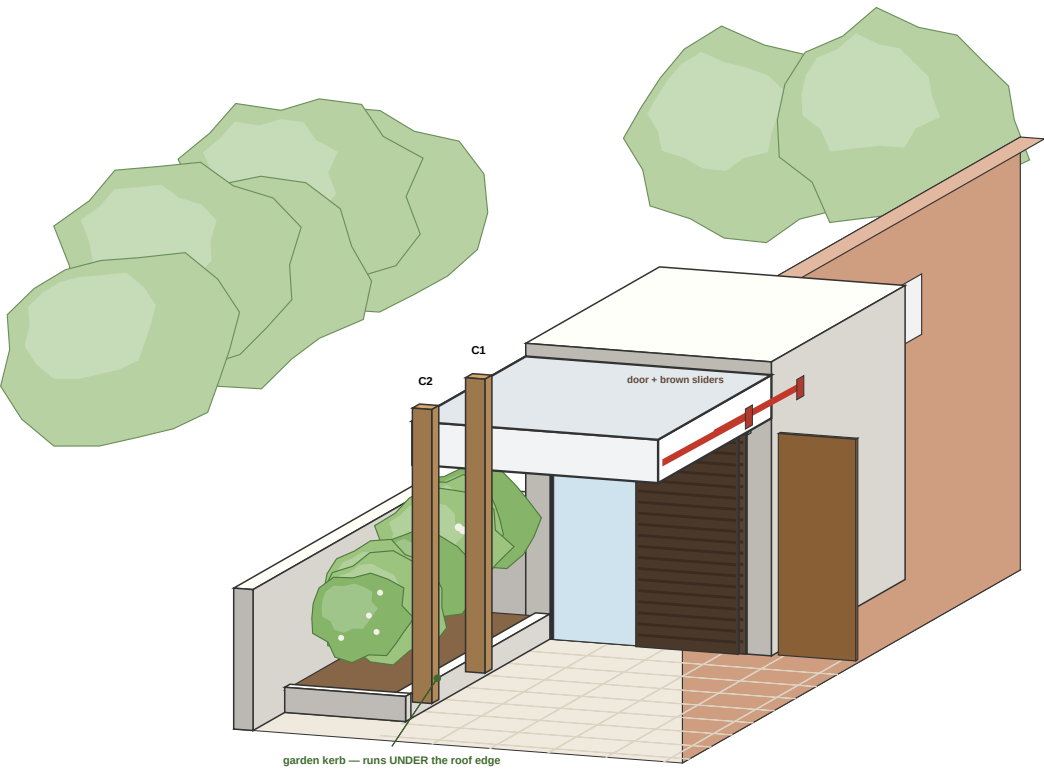

COURTYARD ROOF — V2

VERSION 2 — 0.90 m VOID + 2 STEEL RODS: roof 3.22 x 2.54; 0.90 m void left open; void edge tied to the tall wall with 2 slim Ø16 stainless rods (rising = 30°); 2 columns on the plants side
Client: Owner / Client
Design & drawings: Claude Code

DRAWING NOTES

- Do not scale from this drawing. Use figured dimensions only.
- All dimensions in millimetres; levels in metres relative to internal FFL ±0.000 (datum to be tied to site survey).
- Contractor to verify all dimensions, levels & existing structure on site before fabrication or ordering.
- Read with all other architectural, structural & services drawings and the specification notes (A-001).
- Structural members are preliminary: final design, connections & calculations by a licensed structural engineer to local code before construction.
- Report any discrepancy to the designer before proceeding.

REVISIONS

Rev	Date	Description
C06	07.10.2026	Garden = planter in front of the façade, left of the door, partly under roof
C05	07.10.2026	Triangular versions V1T/V2T; 3D views; details D3
C04	07.10.2026	Two versions V1/V2 per client sections & site photo
C02	07.10.2026	Canopy to client sketch: 8.00 house, roof 3.22, u/s 2.36, fascia 0.43

PREVIEW FOR CLIENT REVIEW — per client sketch, mark-ups & site photo; not for construction

DRAWING TITLE

V2 VOID + RODS
views, section & 3D view

SCALE @ A3

1:50

DRAWN / CHECKED

CC / —

DATE

07.10.2026

SERIES

ARCHITECTURAL

DRAWING No.

REV


V2-02

C06


VERSION 2 — 0.90 m VOID + 2 STEEL RODS

1/V2-03 ROOF SECTION ACROSS AT C1 — 1:30 (planter under the roof edge)


(as client sketch B: roof stops, rods to the wall)

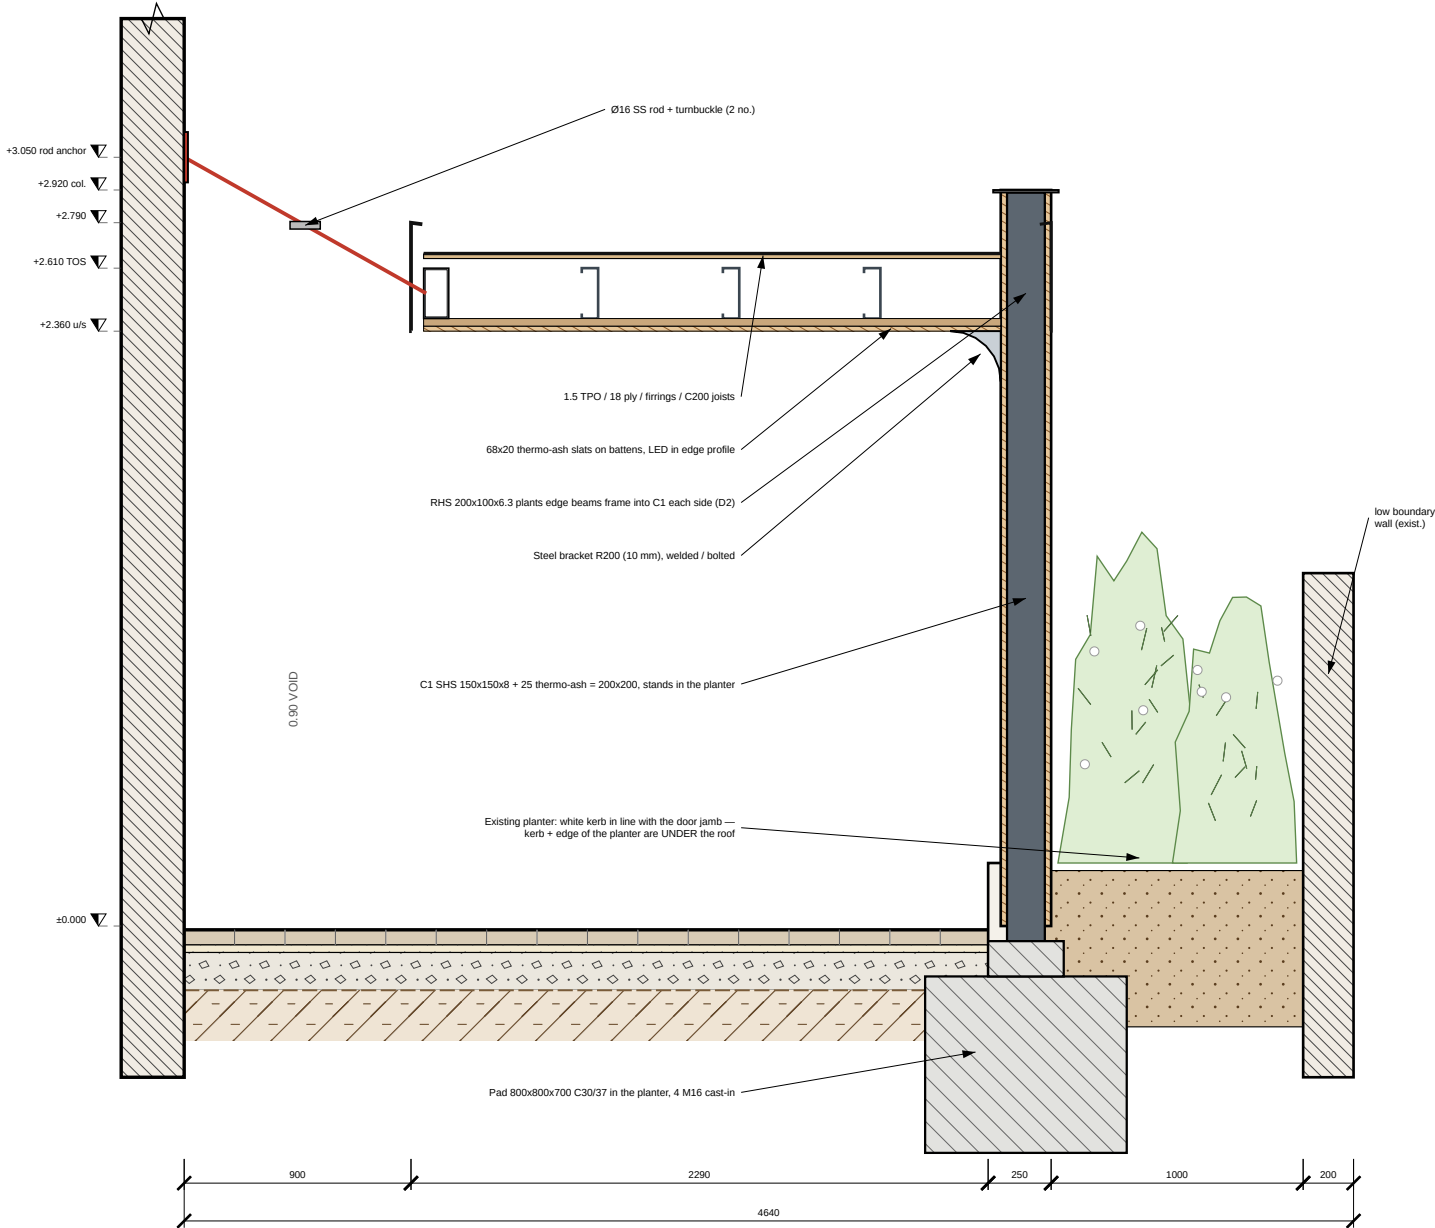


SPECIFICATION
Steel S355, hot-dip galvanised; columns & brackets powder-coated RAL 9010 or timber-clad (thermo-ash).
Roof: TPO 1.5 on 18 mm marine ply on tapered firrings (fall 1:70 to the free-edge box gutter).
Soffit: thermo-ash 68x20 slats, LED 2700 K in perimeter profile. Fascia 3 mm aluminium RAL 9010, 0.43 m.
Rods: Ø16 stainless 316, fork ends, turnbuckle, = 30° rise; engineer to confirm wall anchors.

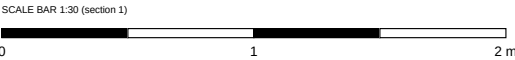


D1 ROD TO WALL (client sketch B) — 1:20

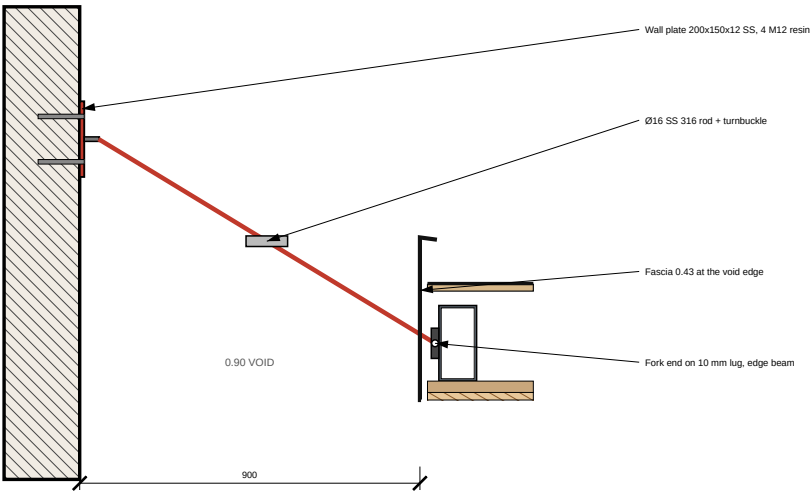

D2 COLUMN / ROOF JUNCTION (plants side) — 1:15

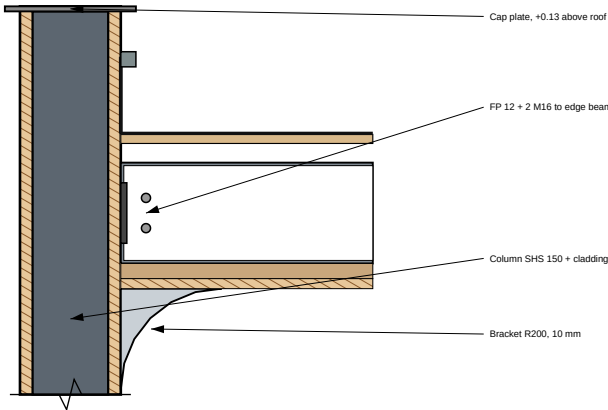

D3 CORNER AT C2 — PLAN 1:15

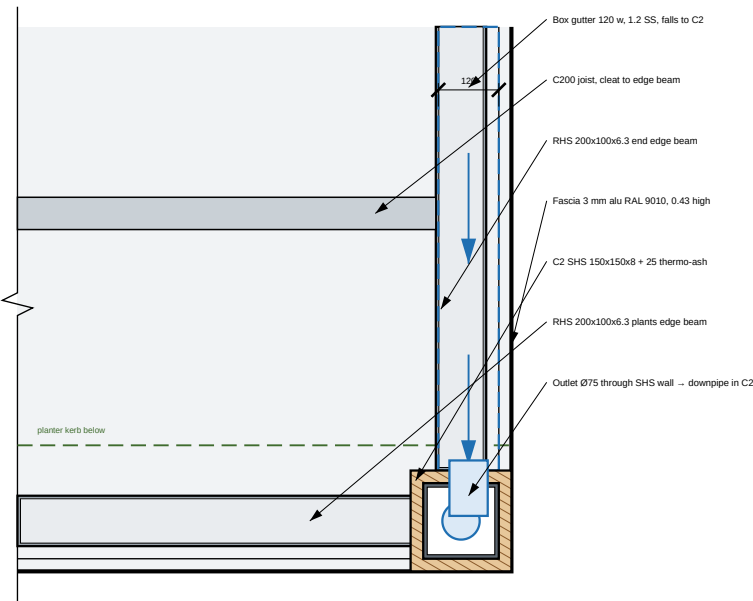

COURTYARD ROOF — V2

VERSION 2 — 0.90 m VOID + 2 STEEL RODS: roof 3.22 x 2.54; 0.90 m void left open; void edge tied to the tall wall with 2 slim Ø16 stainless rods (rising ≈ 30°); 2 columns on the plants side
Client: Owner / Client
Design & drawings: Claude Code

DRAWING NOTES

- Do not scale from this drawing. Use figured dimensions only.
- All dimensions in millimetres; levels in metres relative to internal FFL ±0.000 (datum to be tied to site survey).
- Contractor to verify all dimensions, levels & existing structure on site before fabrication or ordering.
- Read with all other architectural, structural & services drawings and the specification notes (A-001).
- Structural members are preliminary: final design, connections & calculations by a licensed structural engineer to local code before construction.
- Report any discrepancy to the designer before proceeding.

REVISIONS

Rev	Date	Description
C06	07.10.2026	Garden = planter in front of the façade, left of the door, partly under roof
C05	07.10.2026	Triangular versions V1/V2; 3D views; details D3
C04	07.10.2026	Two versions V1/V2 per client sections & site photo
C02	07.10.2026	Canopy to client sketch: 8.00 house, roof 3.22, u/s 2.36, fascia 0.43

PREVIEW FOR CLIENT REVIEW — per client sketch, mark-ups & site photo; not for construction

DRAWING TITLE
V2 VOID + RODS
roof section & details


SCALE @ A3 1:30 / 1:15 / 1:20	DATE 07.10.2026
DRAWN / CHECKED CC / —	SERIES ARCHITECTURAL

DRAWING No. REV

V2-03 **C06**

VERSION 1T — TRIANGLE, ROOF TO THE WALL


TALL HOUSE WALL (exist., AC units)

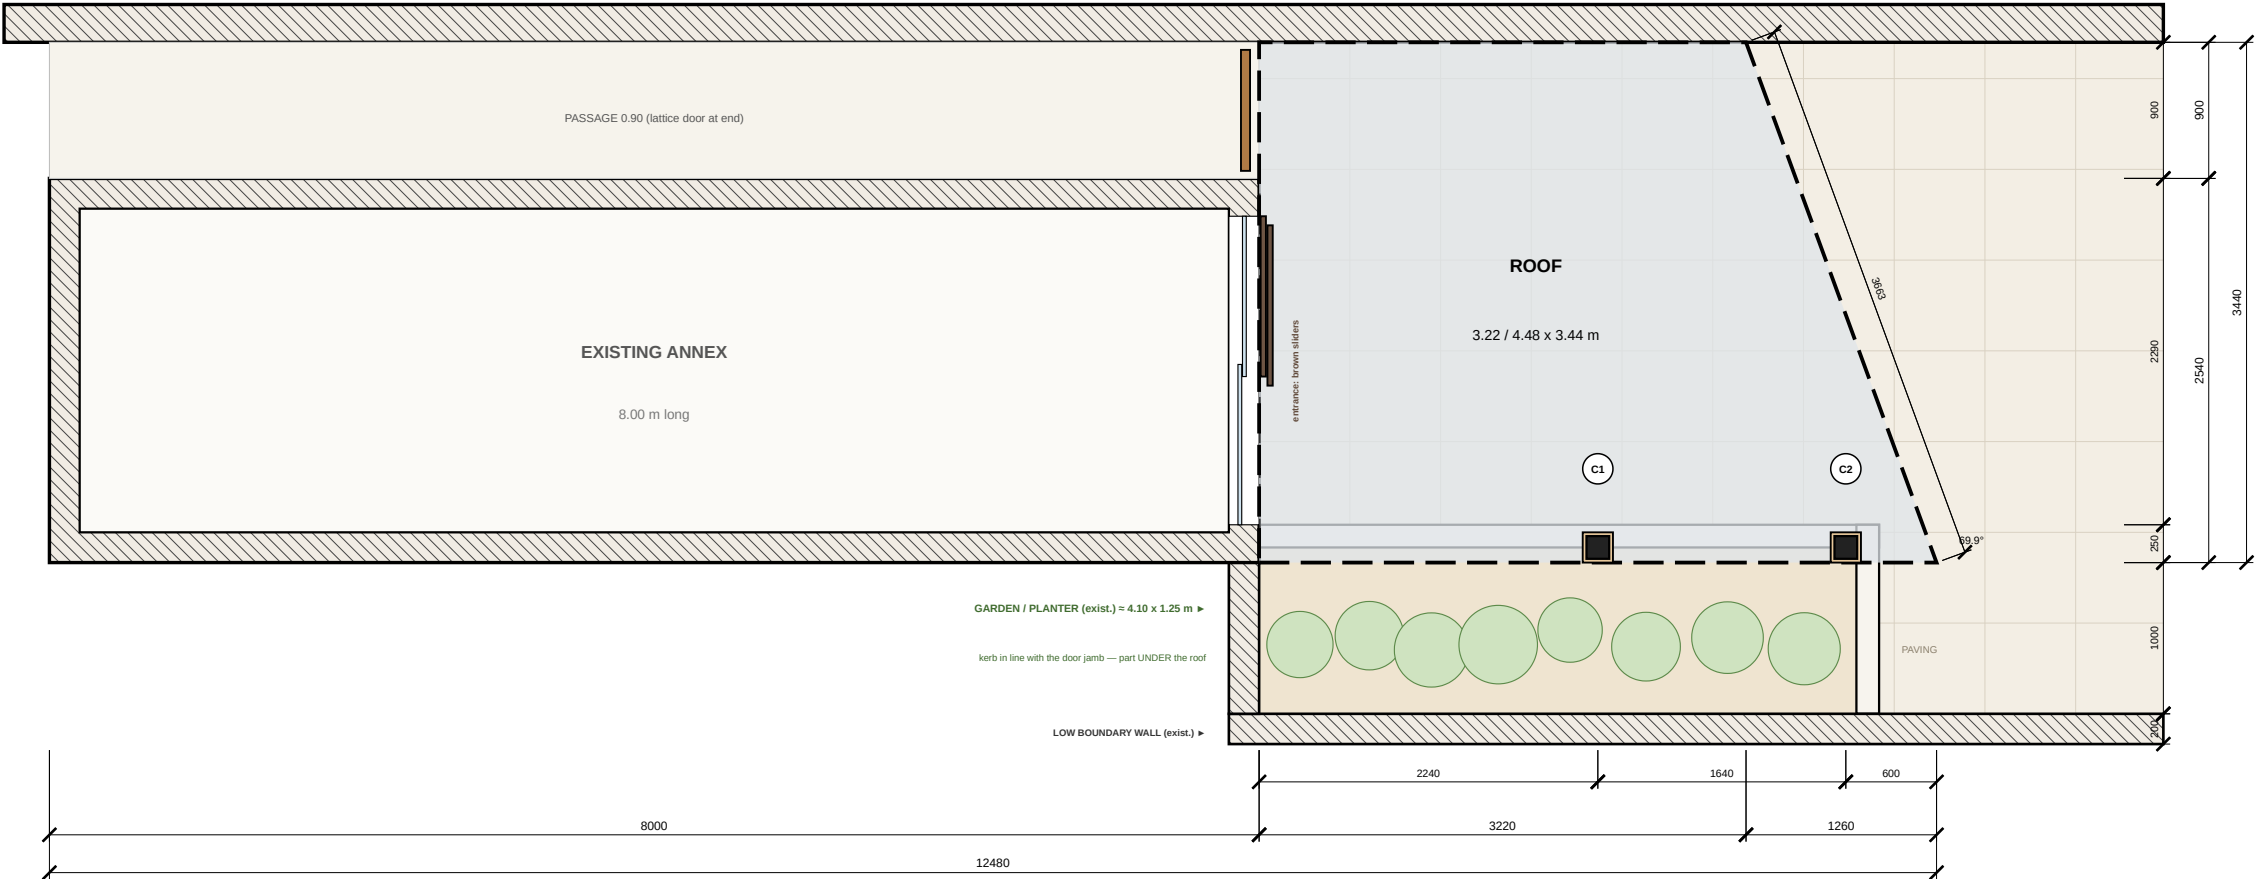

1 TOP VIEW — ANNEX, GARDEN & ROOF
V1T-01


1:50 @ A3 — garden = planter in front of the façade, left of the door; trees = background

2/V1T-01 ROOF FRAMING PLAN — 1:30

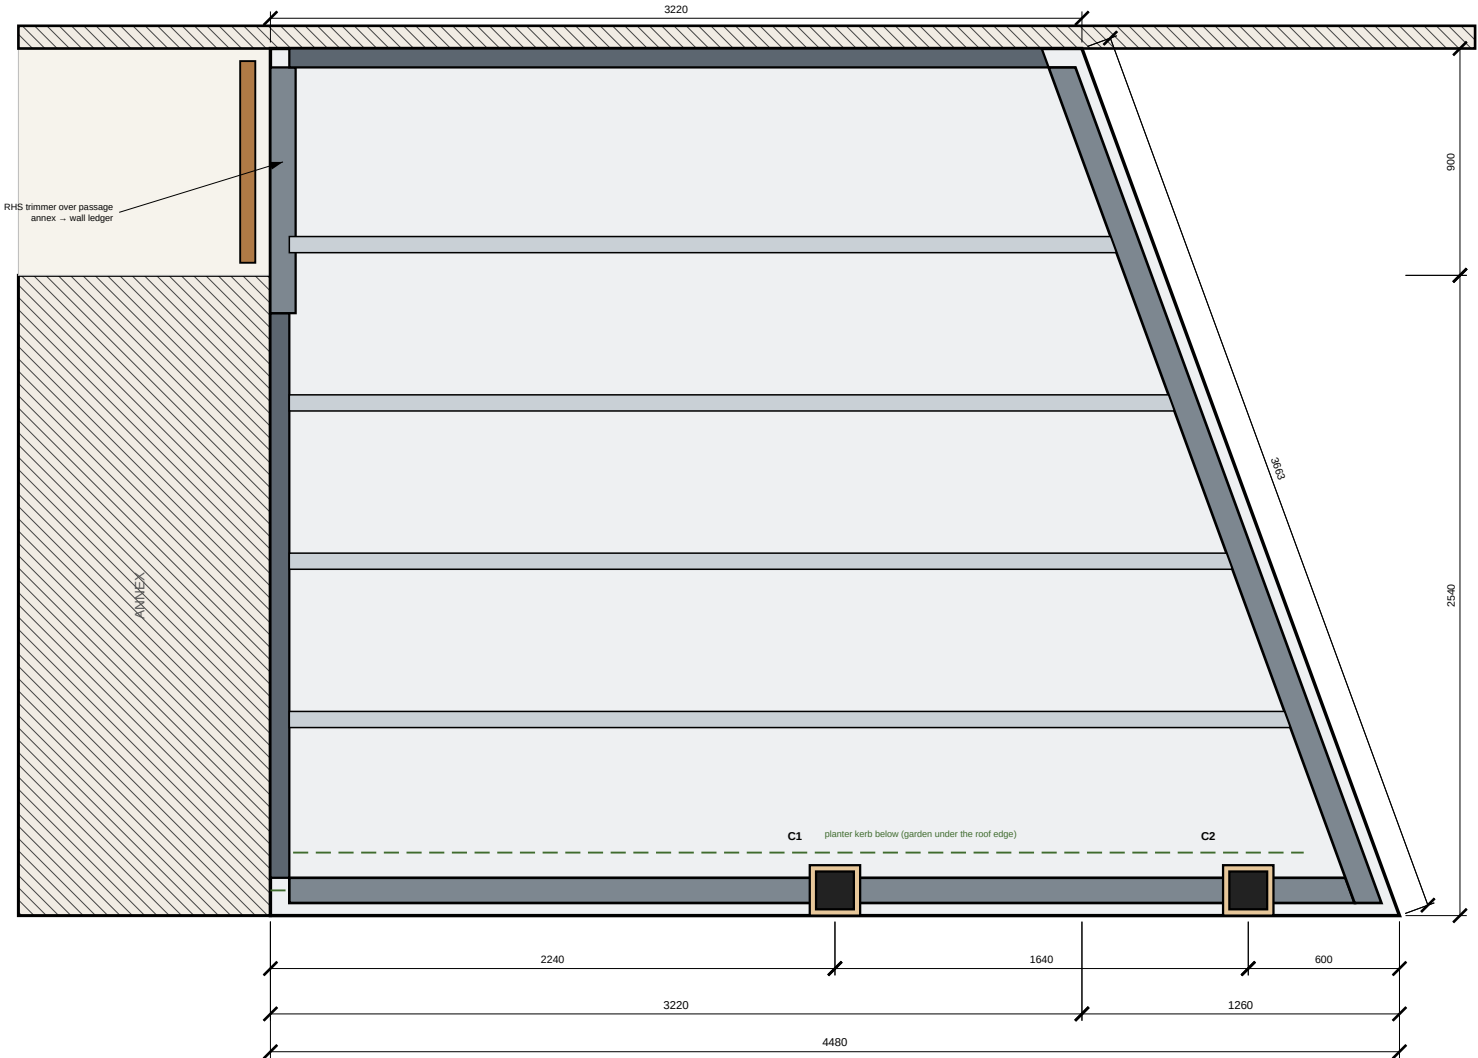

THIS VERSION
triangular roof: plants edge 3.22 + 1.26 = 4.48, wall edge 3.22, raked edge 3.66; runs to the tall wall (ledger + brackets); 2 columns on the plants side.
Roof fixed to the annex end façade AND to the tall house wall (steel ledgers, resin anchors); covers the passage in front of the lattice door (RHS trimmer over the passage, annex - wall ledger).
Triangle: plants edge 3.22 + 1.26 = 4.48 m; raked edge 3.66 m at 69.9° to the plants edge.
C1 in the middle of the 4.48 edge (2.24 from the façade); C2 0.60 m in from the tip (the tip cantilevers 0.60).
Joists run from the annex ledger to the raked edge beam (max. span = 4.2 m).
COMMON
Roof 3.22 m from the annex façade along the top edge. Underside +2.36, fascia 0.43 (top +2.79); columns 200x200, 0.13 above roof, curved bracket under the junction (client section).
Garden = existing planter in front of the façade, left of the door: white kerb in line with the door jamb (0.25 from the corner), so kerb + edge of the planter are UNDER the roof; C1 + C2 stand in the planter. Planter length = 4.10 m (from site photo — confirm).
Falls 1:70 to the concealed gutter at the free edge; rainwater down C2.

3/V1T-01 3D — BIRD'S EYE (from the plants side, over the low wall)

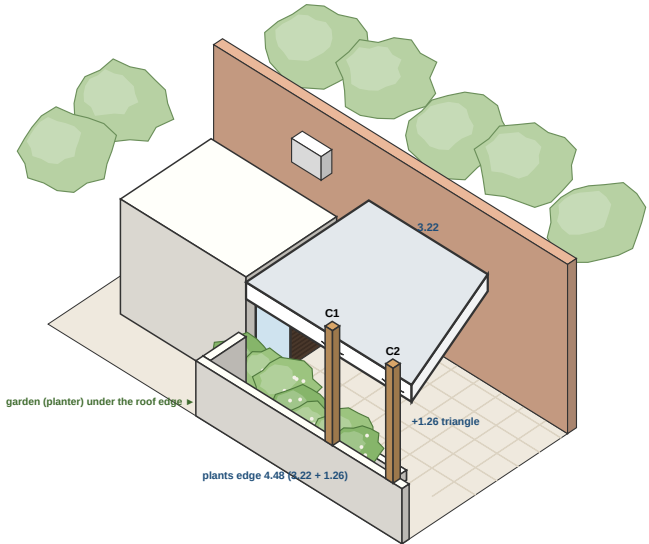

SCALE BAR 1:50 (top view)
0 2.5 5 m

COURTYARD ROOF — V1T

VERSION 1T — TRIANGLE, ROOF TO THE WALL: triangular roof: plants edge 3.22 + 1.26 = 4.48, wall edge 3.22, raked edge 3.66; runs to the tall wall (ledger + brackets); 2 columns on the plants side
Client: Owner / Client
Design & drawings: Claude Code

- DRAWING NOTES**
- Do not scale from this drawing. Use figured dimensions only.
 - All dimensions in millimetres; levels in metres relative to internal FFL ±0.000 (datum to be tied to site survey).
 - Contractor to verify all dimensions, levels & existing structure on site before fabrication or ordering.
 - Read with all other architectural, structural & services drawings and the specification notes (A-001).
 - Structural members are preliminary: final design, connections & calculations by a licensed structural engineer to local code before construction.
 - Report any discrepancy to the designer before proceeding.

REVISIONS		
Rev	Date	Description
C06	07.10.2026	Garden = planter in front of the façade, left of the door, partly under roof
C05	07.10.2026	Triangular versions V1T/V2T; 3D views; details D3
C04	07.10.2026	Two versions V1/V2 per client sections & site photo
C02	07.10.2026	Canopy to client sketch: 8.00 house, roof 3.22, u/s 2.36, fascia 0.43


PREVIEW FOR CLIENT REVIEW — per client sketch, mark-ups & site photo; not for construction

DRAWING TITLE	
V1T TRIANGLE TO WALL top view & roof framing	
SCALE @ A3 1:50 / 1:30	DATE 07.10.2026
DRAWN / CHECKED CC / —	SERIES ARCHITECTURAL


DRAWING No. V1T-01
REV C06

VERSION 1T — TRIANGLE, ROOF TO THE WALL

1/V1T-02 VIEW TO ANNEX FAÇADE (as site photo) — 1:50

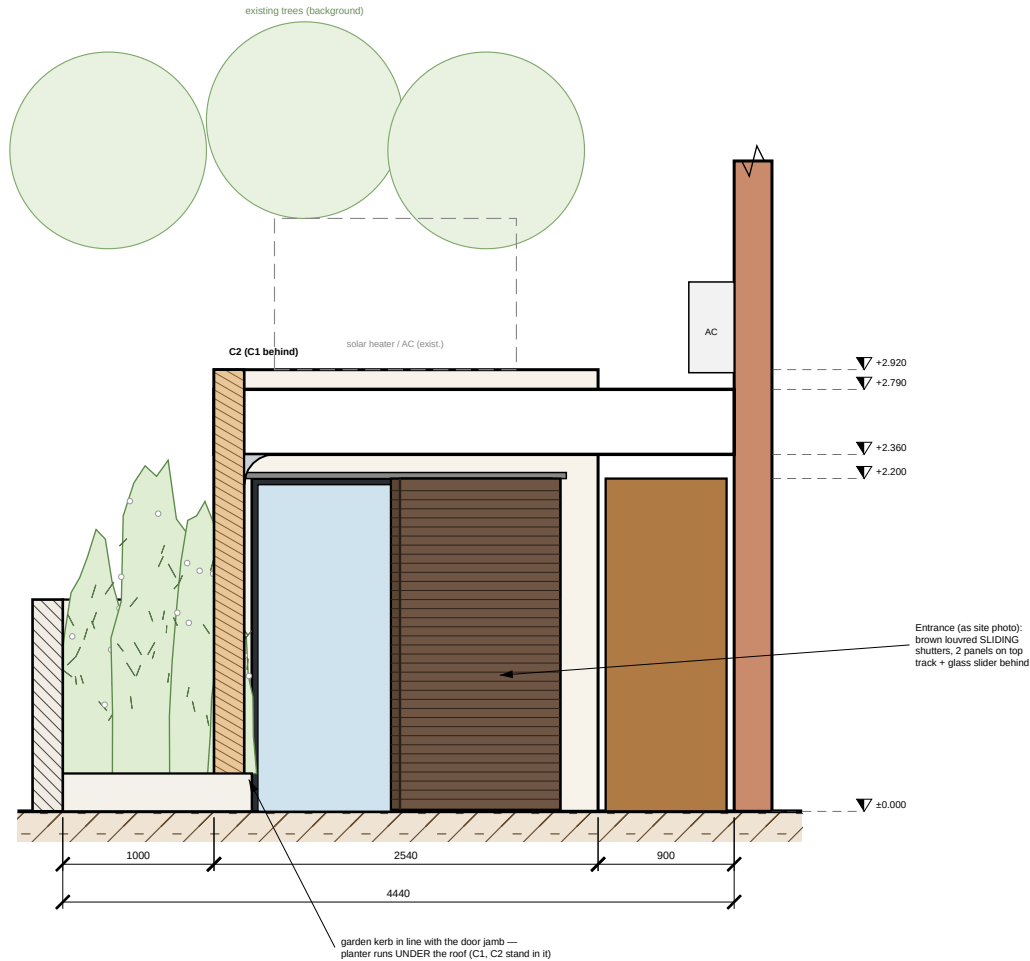


2/V1T-02 PLANTS-SIDE ELEVATION — C1 + C2 — 1:50 (plants edge 3.22 + 1.26 = 4.48)

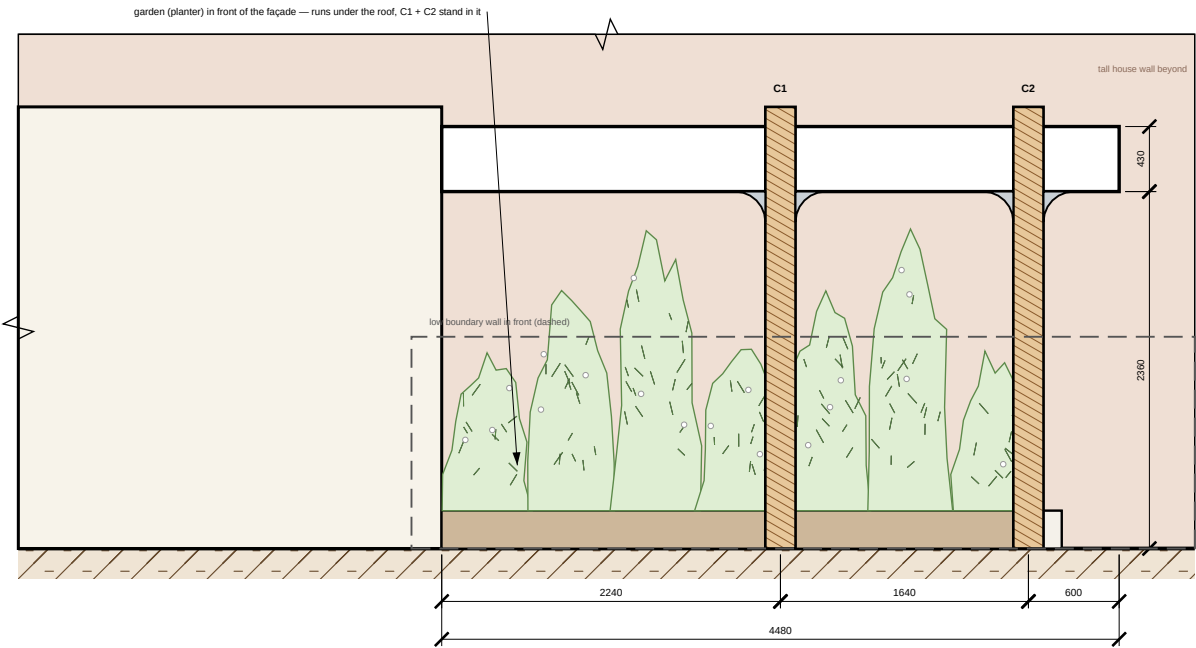


NOTES
triangular roof: plants edge 3.22 + 1.26 = 4.48, wall edge 3.22, raked edge 3.66; runs to the tall wall (ledger + brackets); 2 columns on the plants side.
Underside +2.36, fascia 0.43 (top +2.79); columns 0.13 above roof.
Garden = existing planter in front of the façade, left of the door; its kerb is in line with the door jamb, so part of it is UNDER the roof (C1 + C2 stand in it). Trees are existing, in the background.
Refined roof section & details: sheet V1T-03.

3/V1T-02 SECTION ACROSS AT C1 — 1:50 (refined: V1T-03)

tall wall left — plants side right

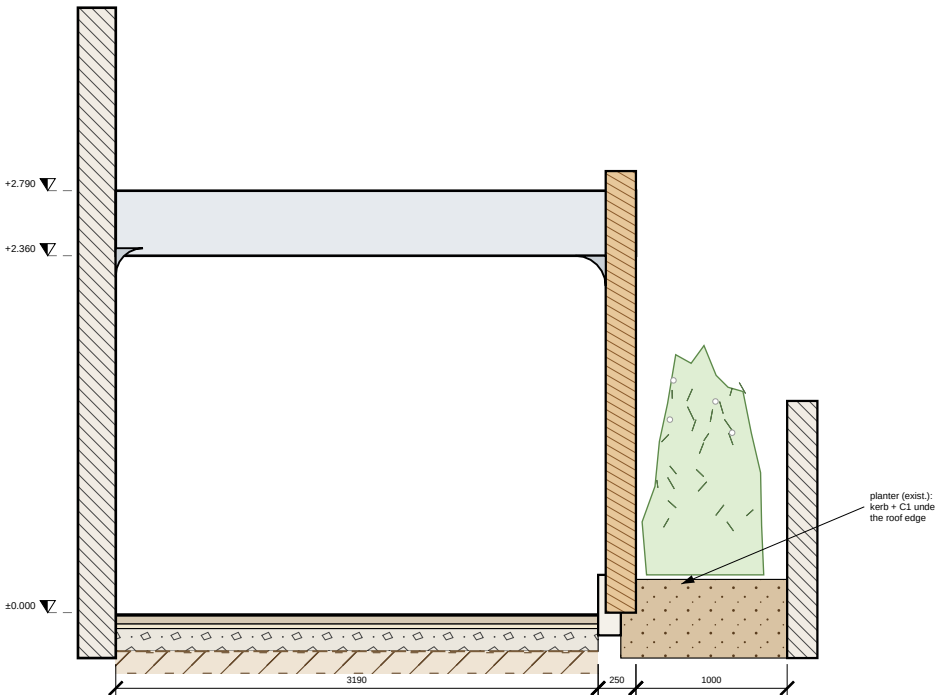

4/V1T-02 3D — EYE LEVEL, SAME DIRECTION AS THE SITE PHOTO

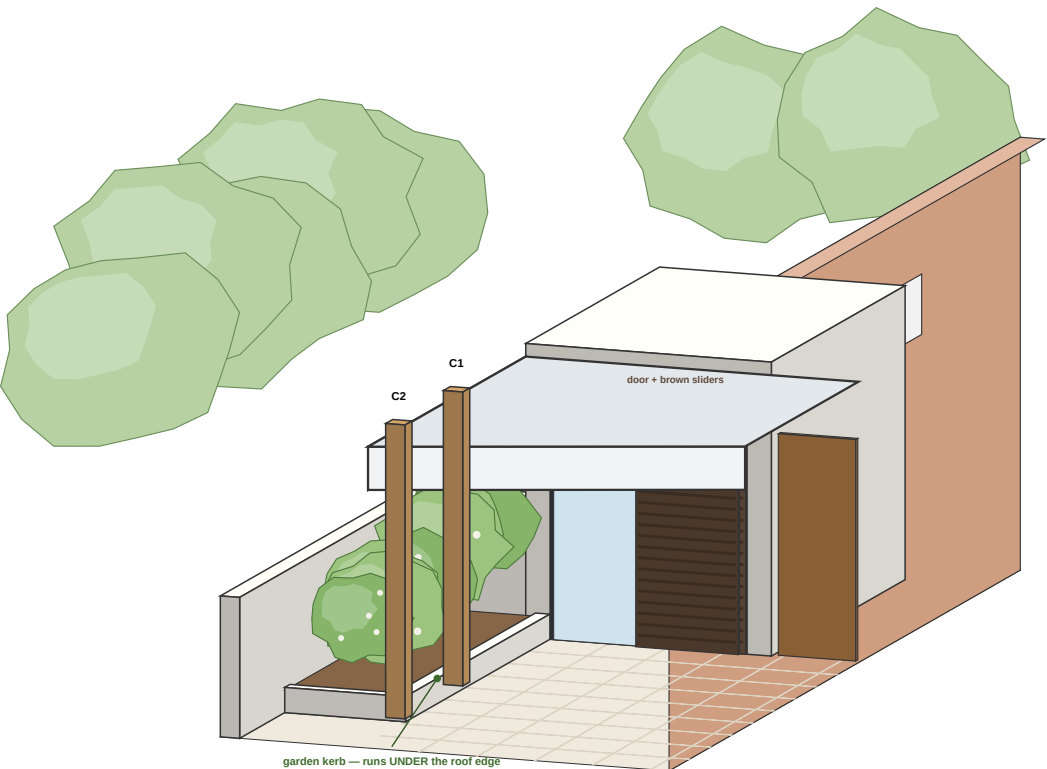

COURTYARD ROOF — V1T

VERSION 1T — TRIANGLE, ROOF TO THE WALL: triangular roof: plants edge 3.22 + 1.26 = 4.48, wall edge 3.22, raked edge 3.66; runs to the tall wall (ledger + brackets); 2 columns on the plants side
Client: Owner / Client
Design & drawings: Claude Code

- DRAWING NOTES**
- Do not scale from this drawing. Use figured dimensions only.
 - All dimensions in millimetres; levels in metres relative to internal FFL ±0.000 (datum to be tied to site survey).
 - Contractor to verify all dimensions, levels & existing structure on site before fabrication or ordering.
 - Read with all other architectural, structural & services drawings and the specification notes (A-001).
 - Structural members are preliminary: final design, connections & calculations by a licensed structural engineer to local code before construction.
 - Report any discrepancy to the designer before proceeding.

REVISIONS		
Rev	Date	Description
C06	07.10.2026	Garden = planter in front of the façade, left of the door, partly under roof
C05	07.10.2026	Triangular versions V1T/V2T; 3D views; details D3
C04	07.10.2026	Two versions V1/V2 per client sections & site photo
C02	07.10.2026	Canopy to client sketch: 8.00 house, roof 3.22, u/s 2.36, fascia 0.43

PREVIEW FOR CLIENT REVIEW — per client sketch, mark-ups & site photo; not for construction

DRAWING TITLE	
V1T TRIANGLE TO WALL views, section & 3D view	
SCALE @ A3 1:50	DATE 07.10.2026
DRAWN / CHECKED CC / —	SERIES ARCHITECTURAL


DRAWING No. REV

V1T-02 C06


VERSION 1T — TRIANGLE, ROOF TO THE WALL

1/V1T-03 ROOF SECTION ACROSS AT C1 — 1:30 (planter under the roof edge)


(as client sketch A: roof runs to the wall)

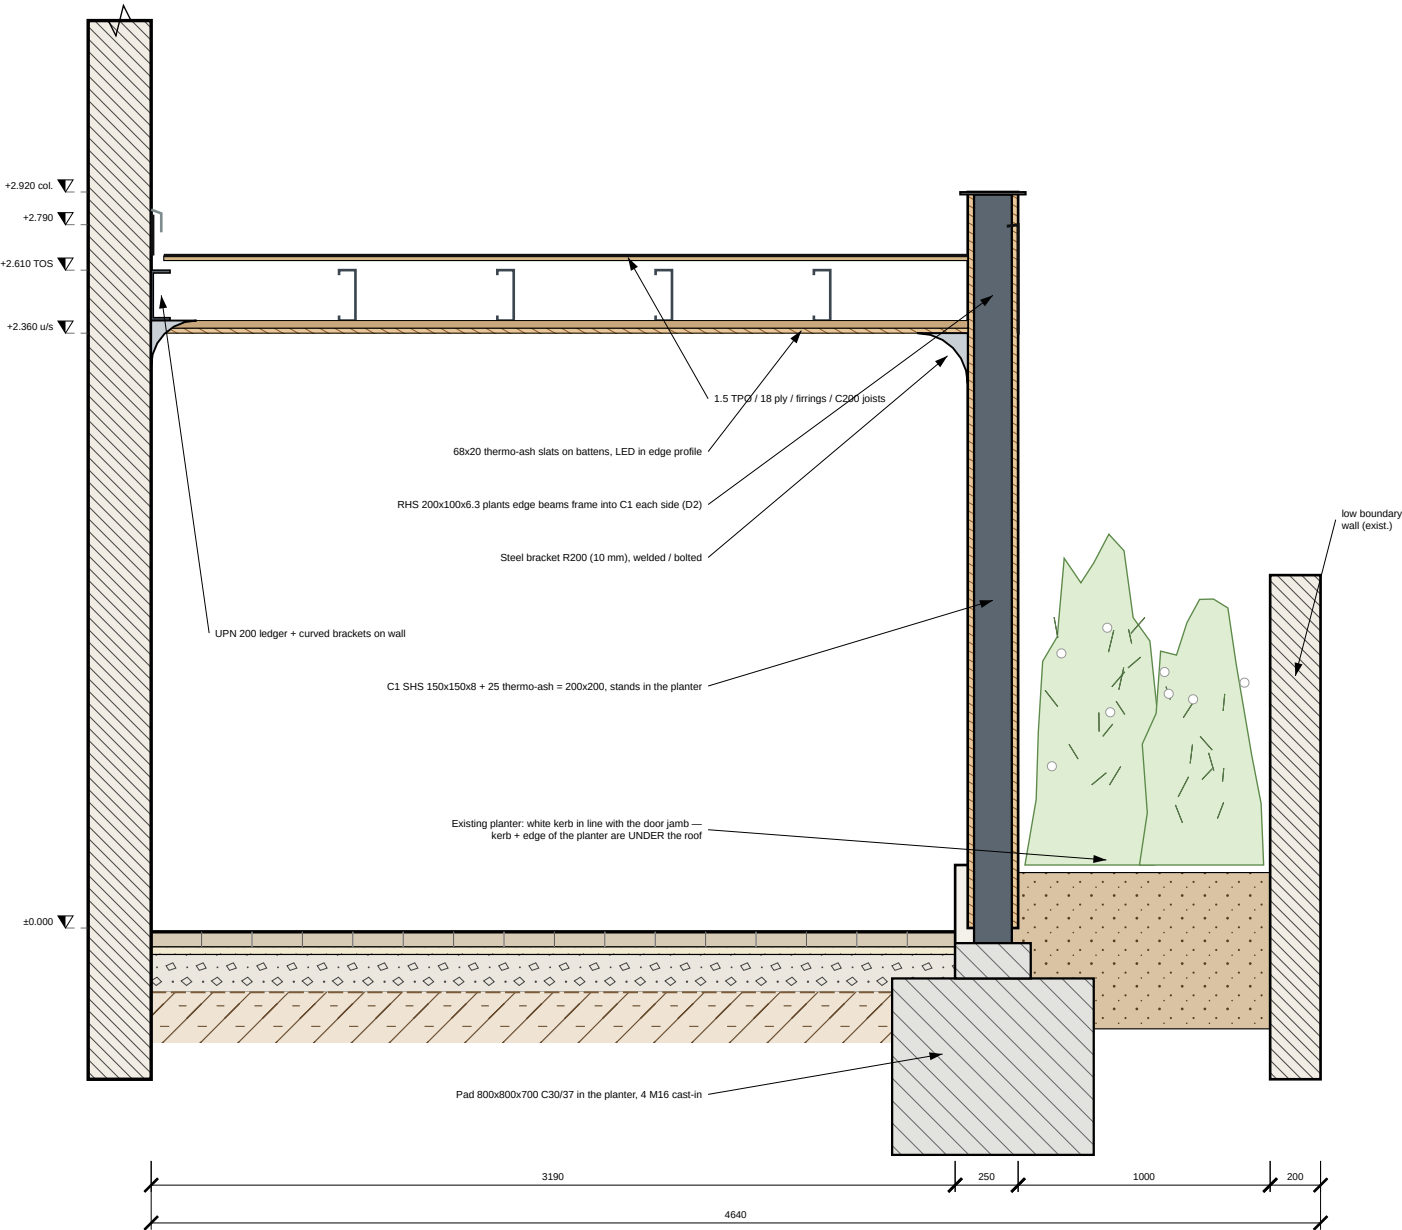


SPECIFICATION
Steel S355, hot-dip galvanised; columns & brackets powder-coated RAL 9010 or timber-clad (thermo-ash).
Roof: TPO 1.5 on 18 mm marine ply on tapered firings (fall 1:70 to the free-edge box gutter).
Soffit: thermo-ash 68x20 slats, LED 2700 K in perimeter profile. Fascia 3 mm aluminium RAL 9010, 0.43 m.
Wall ledger & brackets into sound masonry/RC — engineer to confirm anchors.

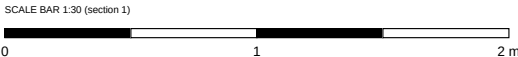


D1 ROOF TO WALL (client sketch A) — 1:15

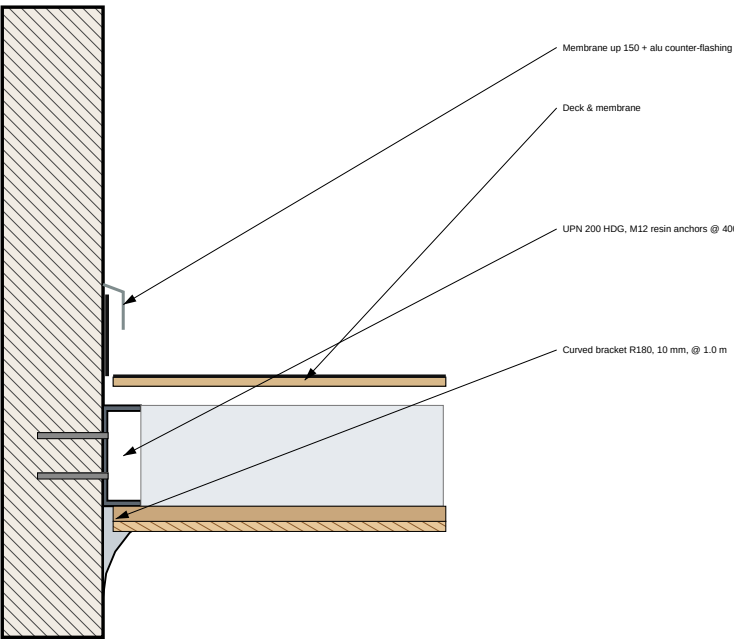

D2 COLUMN / ROOF JUNCTION (plants side) — 1:15

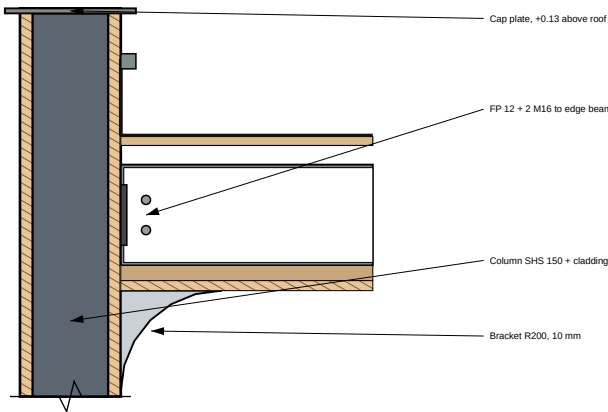

D3 TIP AT C2 (triangle) — PLAN 1:15

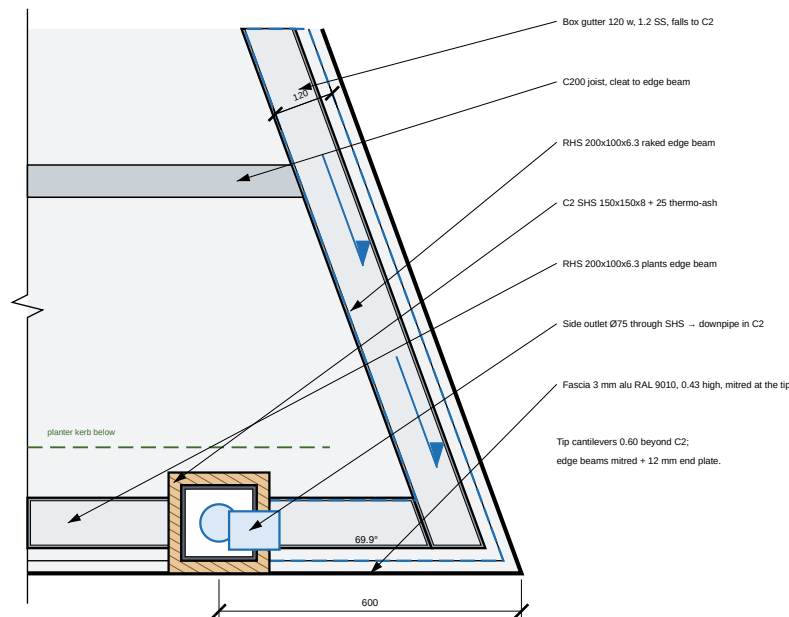

COURTYARD ROOF — V1T

VERSION 1T — TRIANGLE, ROOF TO THE WALL: triangular roof; plants edge 3.22 + 1.26 = 4.48, wall edge 3.22, raked edge 3.66; runs to the tall wall (ledger + brackets); 2 columns on the plants side
Client: Owner / Client
Design & drawings: Claude Code

- DRAWING NOTES**
- Do not scale from this drawing. Use figured dimensions only.
 - All dimensions in millimetres; levels in metres relative to internal FFL ±0.000 (datum to be tied to site survey).
 - Contractor to verify all dimensions, levels & existing structure on site before fabrication or ordering.
 - Read with all other architectural, structural & services drawings and the specification notes (A-001).
 - Structural members are preliminary: final design, connections & calculations by a licensed structural engineer to local code before construction.
 - Report any discrepancy to the designer before proceeding.

REVISIONS		
Rev	Date	Description
C06	07.10.2026	Garden = planter in front of the façade, left of the door, partly under roof
C05	07.10.2026	Triangular versions V1T/V2T; 3D views; details D3
C04	07.10.2026	Two versions V1/V2 per client sections & site photo
C02	07.10.2026	Canopy to client sketch: 8.00 house, roof 3.22, u/s 2.36, fascia 0.43

PREVIEW FOR CLIENT REVIEW — per client sketch, mark-ups & site photo; not for construction


DRAWING TITLE	
V1T TRIANGLE TO WALL roof section & details	
SCALE @ A3 1:30 / 1:15 / 1:20	DATE 07.10.2026
DRAWN / CHECKED CC / —	SERIES ARCHITECTURAL

DRAWING No. REV

V1T-03 C06

VERSION 2T — TRIANGLE, 0.90 m VOID + 2 RODS


TALL HOUSE WALL (exist., AC units)

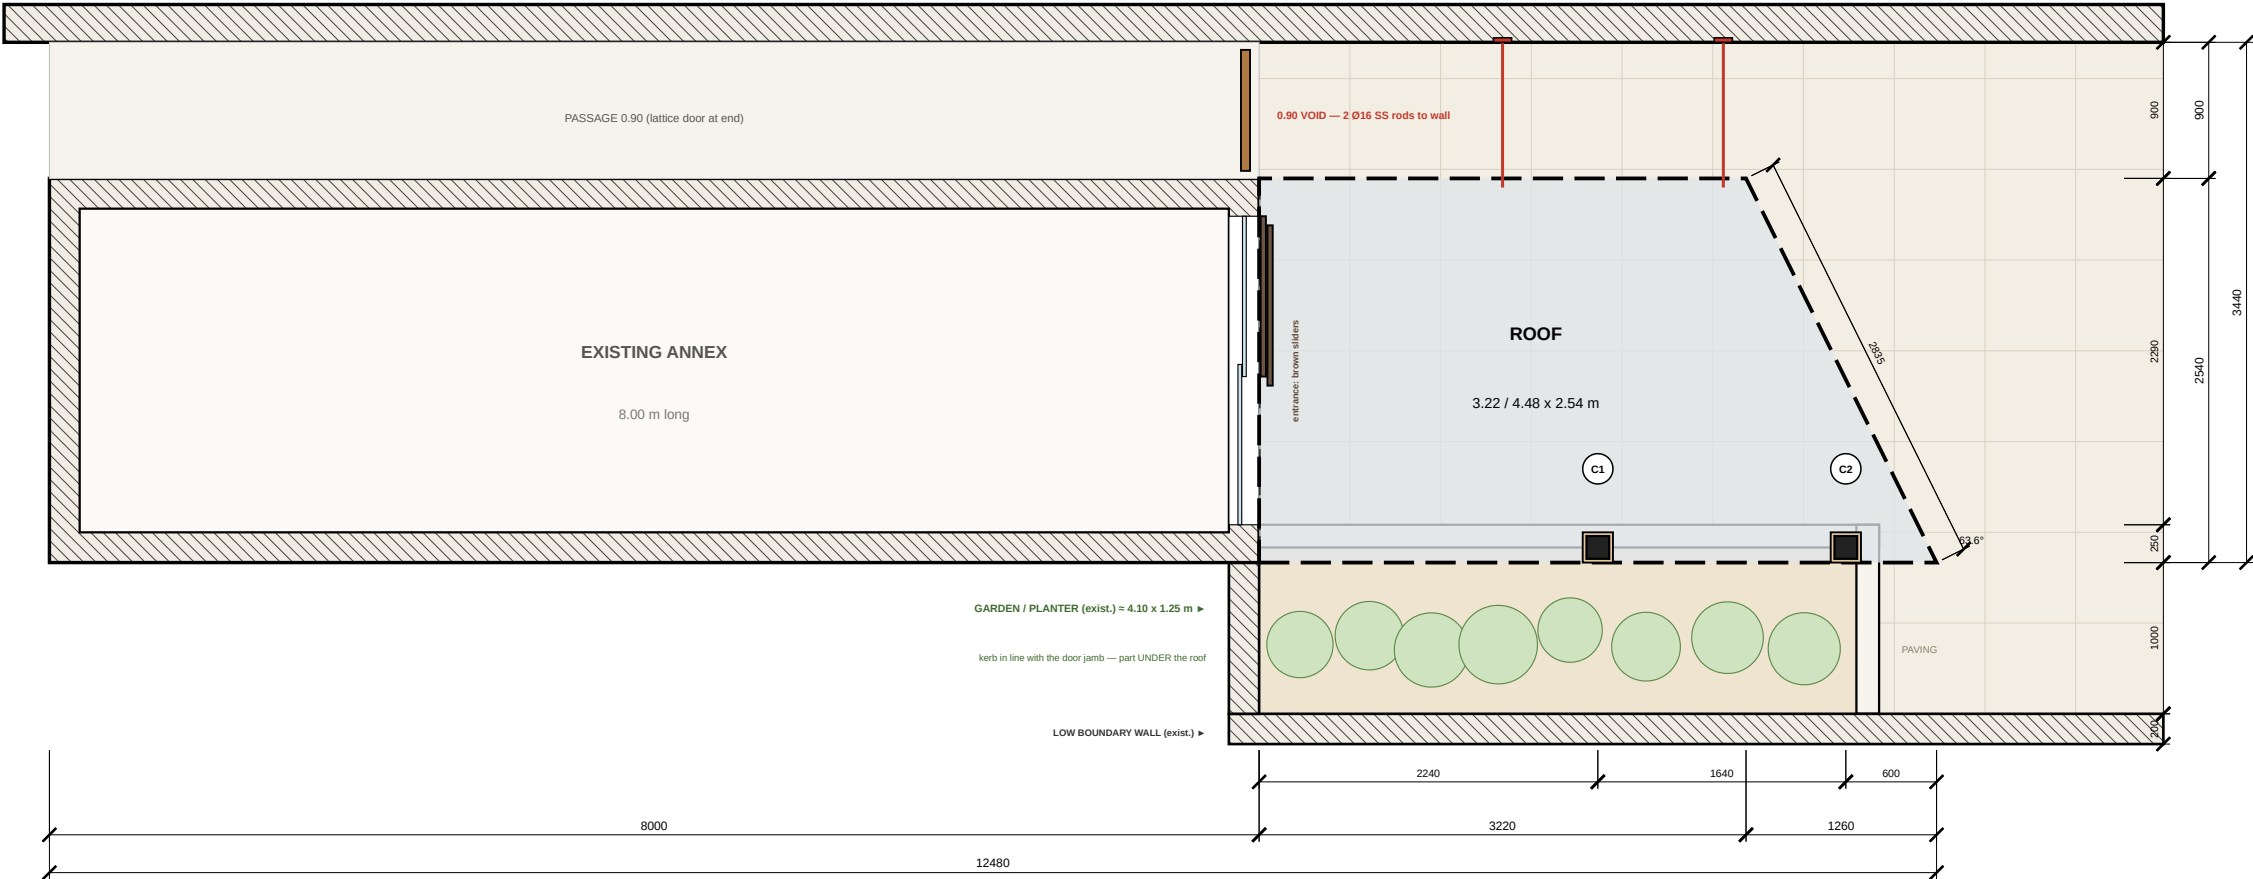

1 TOP VIEW — ANNEX, GARDEN & ROOF


V2T-01 1:50 @ A3 — garden = planter in front of the façade, left of the door; trees = background

2/V2T-01 ROOF FRAMING PLAN — 1:30

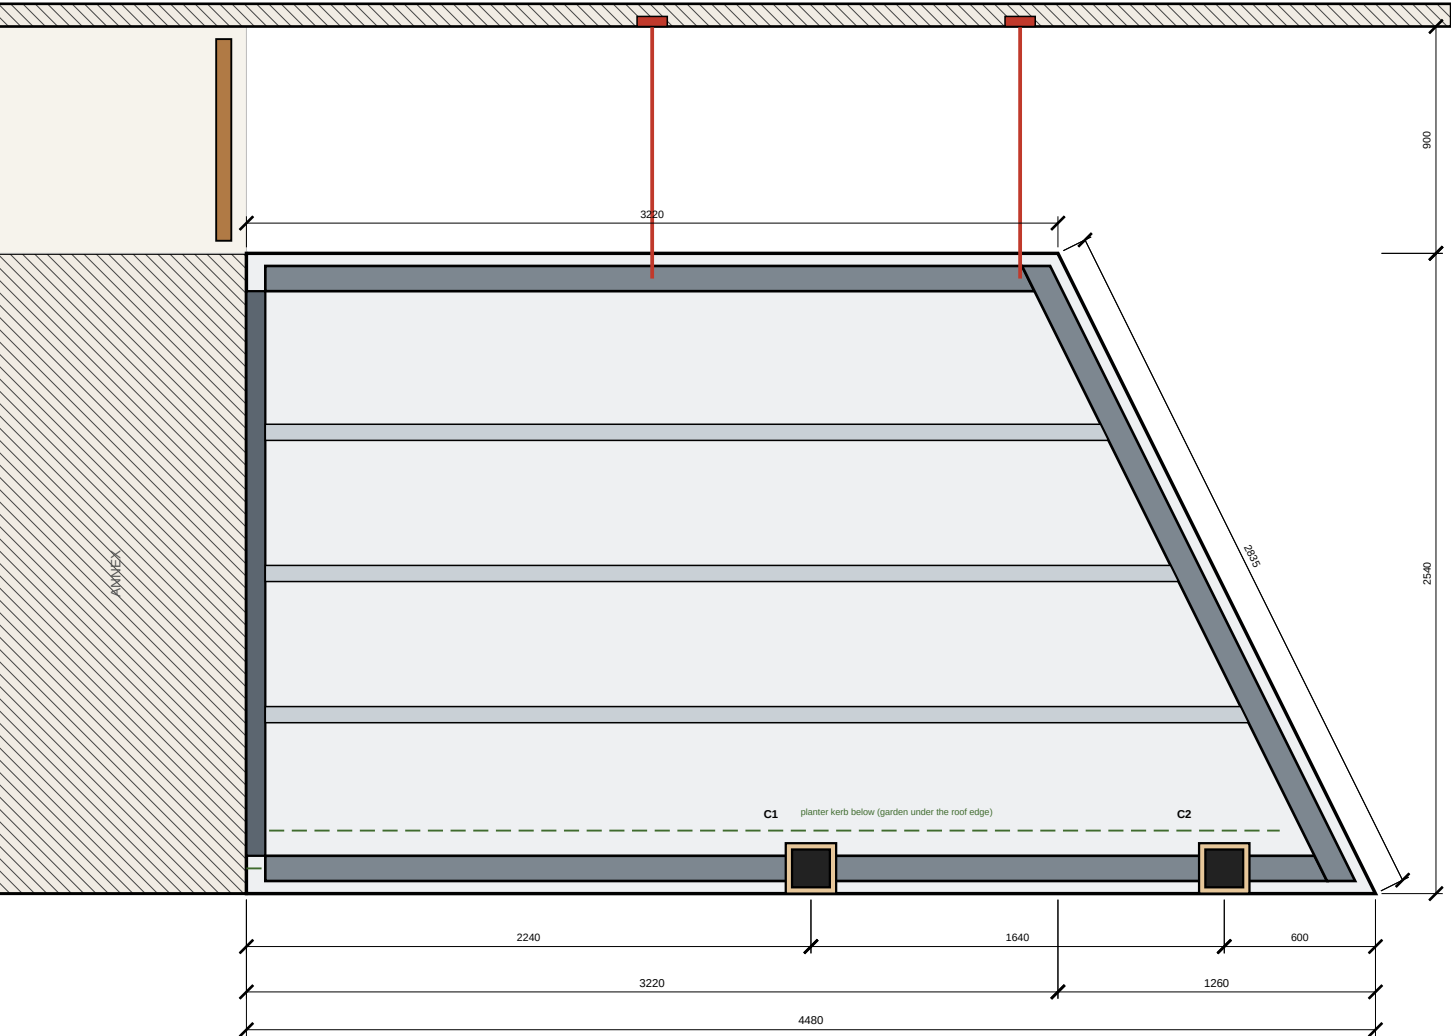

THIS VERSION
triangular roof: plants edge 3.22 + 1.26 = 4.48, void edge 3.22, raked edge 2.84; 0.90 m void open, 2 Ø16 stainless rods to the wall; 2 columns on the plants side. Roof fixed to the annex end façade (ledger). The 0.90 m passage to the lattice door stays open. Void edge hung from the tall house wall on 2 Ø16 stainless rods (turnbuckles, wall plates) — slim, almost invisible. Triangle: plants edge 3.22 + 1.26 = 4.48 m; raked edge 2.84 m at 63.6° to the plants edge. C1 in the middle of the 4.48 edge (2.24 from the façade); C2 0.60 m in from the tip (the tip cantilevers 0.60). Joists run from the annex ledger to the raked edge beam (max. span = 4.2 m).
COMMON
Roof 3.22 m from the annex façade along the top edge. Underside +2.36, fascia 0.43 (top +2.79); columns 200x200, 0.13 above roof, curved bracket under the junction (client section). Garden = existing planter in front of the façade, left of the door: white kerb in line with the door jamb (0.25 from the corner), so kerb + edge of the planter are UNDER the roof. C1 + C2 stand in the planter. Planter length = 4.10 m (from site photo — confirm). Falls 1:70 to the concealed gutter at the free edge; rainwater down C2.

3/V2T-01 3D — BIRD'S EYE (from the plants side, over the low wall)

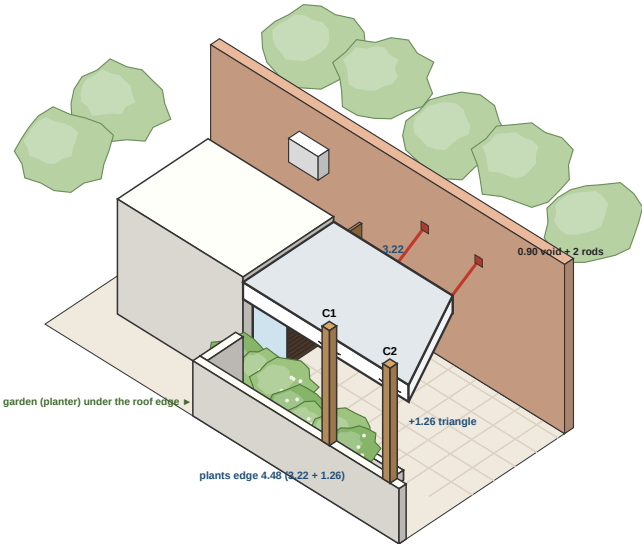

COURTYARD ROOF — V2T

VERSION 2T — TRIANGLE, 0.90 m VOID + 2 RODS: triangular roof: plants edge 3.22 + 1.26 = 4.48, void edge 3.22, raked edge 2.84; 0.90 m void open, 2 Ø16 stainless rods to the wall; 2 columns on the plants side
Client: Owner / Client
Design & drawings: Claude Code

- DRAWING NOTES**
- Do not scale from this drawing. Use figured dimensions only.
 - All dimensions in millimetres; levels in metres relative to internal FFL ±0.000 (datum to be tied to site survey).
 - Contractor to verify all dimensions, levels & existing structure on site before fabrication or ordering.
 - Read with all other architectural, structural & services drawings and the specification notes (A-001).
 - Structural members are preliminary: final design, connections & calculations by a licensed structural engineer to local code before construction.
 - Report any discrepancy to the designer before proceeding.

REVISIONS		
Rev	Date	Description
C06	07.10.2026	Garden = planter in front of the façade, left of the door, partly under roof
C05	07.10.2026	Triangular versions V1T/V2T; 3D views; details D3
C04	07.10.2026	Two versions V1/V2 per client sections & site photo
C02	07.10.2026	Canopy to client sketch: 8.00 house, roof 3.22, u/s 2.36, fascia 0.43


PREVIEW FOR CLIENT REVIEW — per client sketch, mark-ups & site photo; not for construction

DRAWING TITLE	
V2T TRIANGLE + RODS top view & roof framing	
SCALE @ A3 1:50 / 1:30	DATE 07.10.2026
DRAWN / CHECKED CC / —	SERIES ARCHITECTURAL
DRAWING No.	REV


V2T-01 C06

VERSION 2T — TRIANGLE, 0.90 m VOID + 2 RODS

1/V2T-02 VIEW TO ANNEX FAÇADE (as site photo) — 1:50

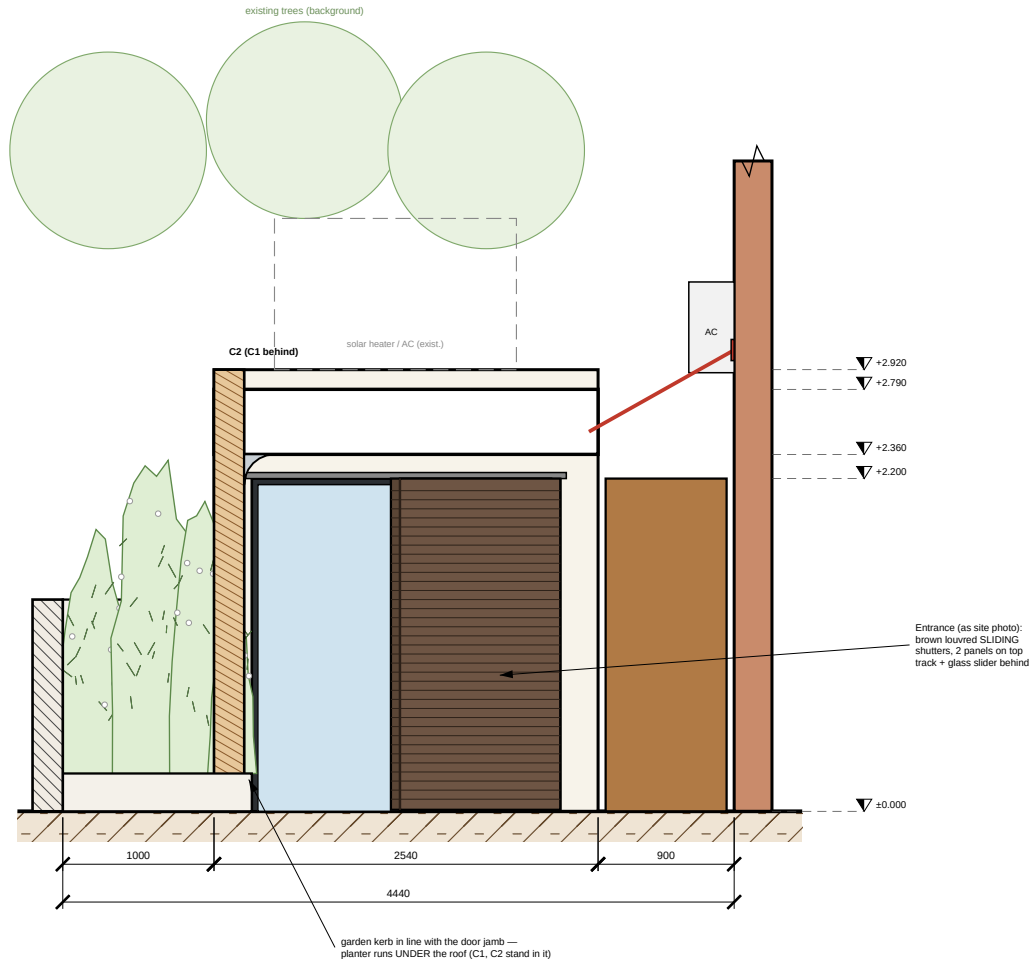


2/V2T-02 PLANTS-SIDE ELEVATION — C1 + C2 — 1:50 (plants edge 3.22 + 1.26 = 4.48)

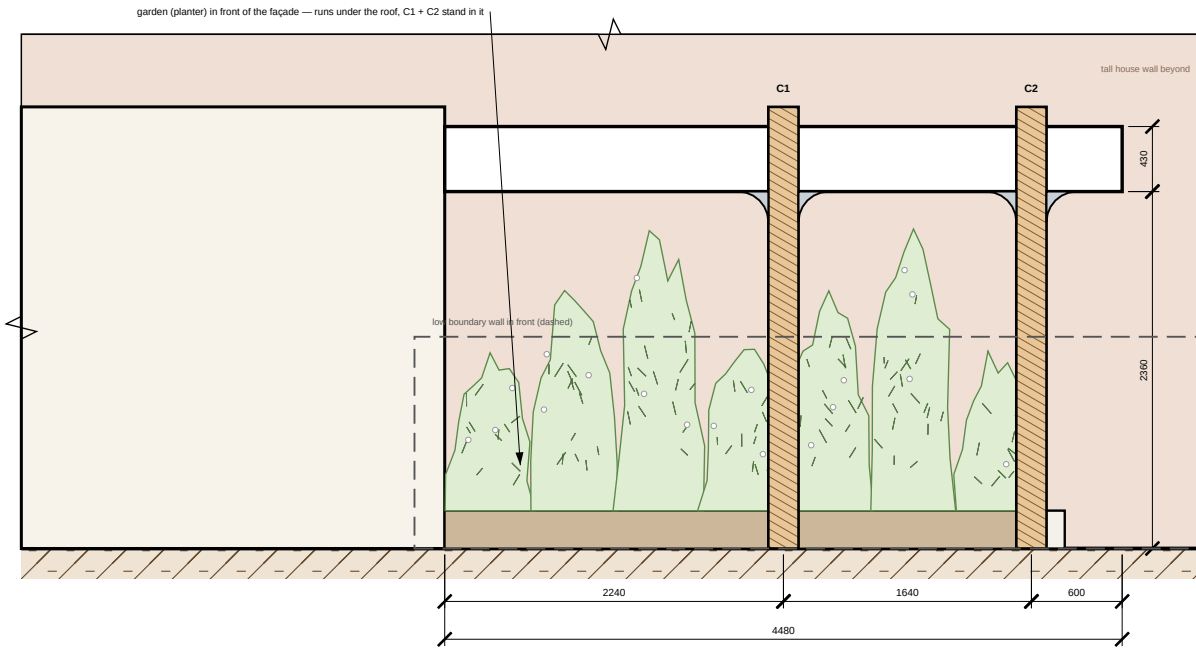


NOTES
triangular roof: plants edge 3.22 + 1.26 = 4.48, void edge 3.22, raked edge 2.84; 0.90 m void open, 2 Ø16 stainless rods to the wall; 2 columns on the plants side.
Underside +2.36, fascia 0.43 (top +2.79); columns 0.13 above roof.
Garden = existing planter in front of the façade, left of the door; its kerb is in line with the door jamb, so part of it is UNDER the roof (C1 + C2 stand in it). Trees are existing, in the background.
Refined roof section & details: sheet V2T-03.

3/V2T-02 SECTION ACROSS AT C1 — 1:50 (refined: V2T-03)

tall wall left — plants side right

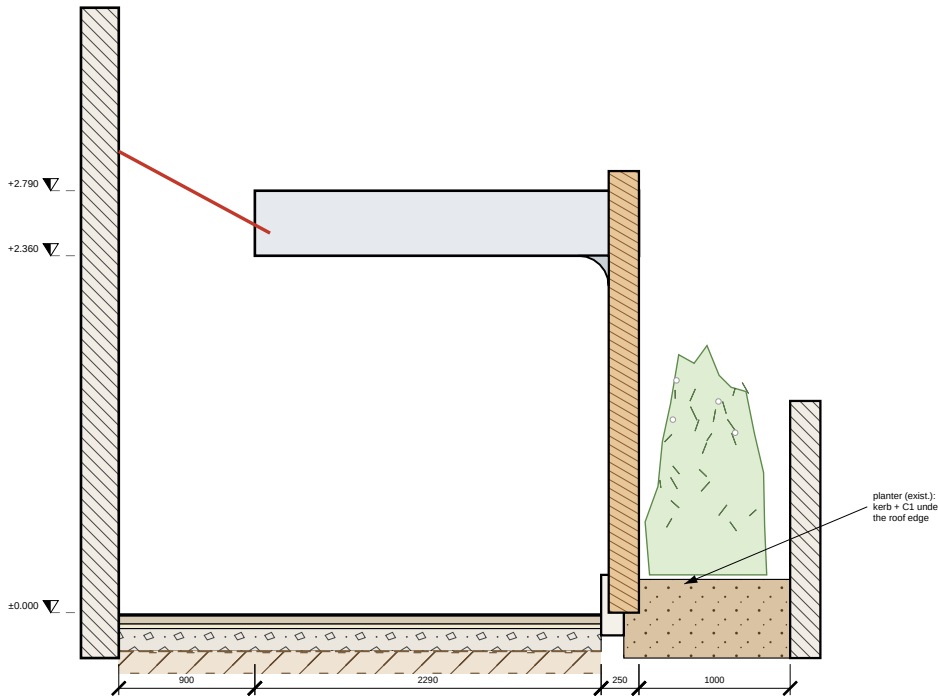

4/V2T-02 3D — EYE LEVEL, SAME DIRECTION AS THE SITE PHOTO

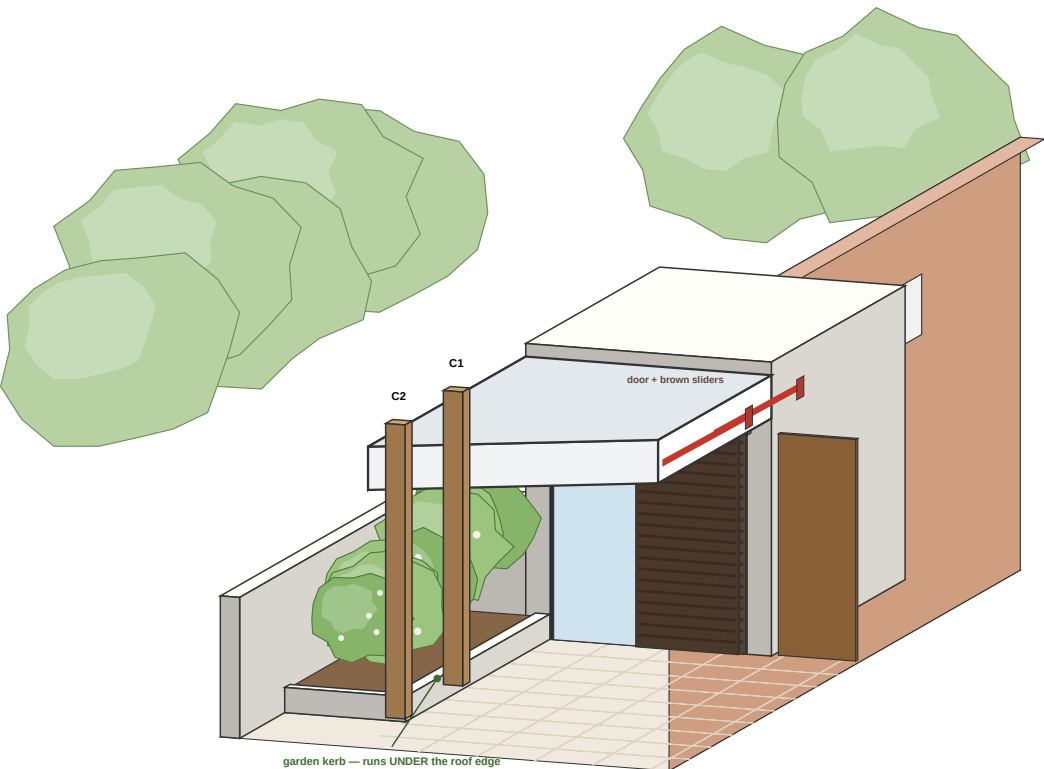

COURTYARD ROOF — V2T

VERSION 2T — TRIANGLE, 0.90 m VOID + 2 RODS: triangular roof: plants edge 3.22 + 1.26 = 4.48, void edge 3.22, raked edge 2.84; 0.90 m void open, 2 Ø16 stainless rods to the wall; 2 columns on the plants side
Client: Owner / Client
Design & drawings: Claude Code

DRAWING NOTES

- Do not scale from this drawing. Use figured dimensions only.
- All dimensions in millimetres; levels in metres relative to internal FFL ±0.000 (datum to be tied to site survey).
- Contractor to verify all dimensions, levels & existing structure on site before fabrication or ordering.
- Read with all other architectural, structural & services drawings and the specification notes (A-001).
- Structural members are preliminary: final design, connections & calculations by a licensed structural engineer to local code before construction.
- Report any discrepancy to the designer before proceeding.

REVISIONS

Rev	Date	Description
C06	07.10.2026	Garden = planter in front of the façade, left of the door, partly under roof
C05	07.10.2026	Triangular versions V1T/V2T; 3D views; details D3
C04	07.10.2026	Two versions V1/V2 per client sections & site photo
C02	07.10.2026	Canopy to client sketch: 8.00 house, roof 3.22, u/s 2.36, fascia 0.43

PREVIEW FOR CLIENT REVIEW — per client sketch, mark-ups & site photo; not for construction

DRAWING TITLE

V2T TRIANGLE + RODS
views, section & 3D view

SCALE @ A3

1:50

DRAWN / CHECKED

CC / —

DATE

07.10.2026

SERIES

ARCHITECTURAL

DRAWING No.

REV


V2T-02

C06


VERSION 2T — TRIANGLE, 0.90 m VOID + 2 RODS

1/V2T-03 ROOF SECTION ACROSS AT C1 — 1:30 (planter under the roof edge)


(as client sketch B: roof stops, rods to the wall)

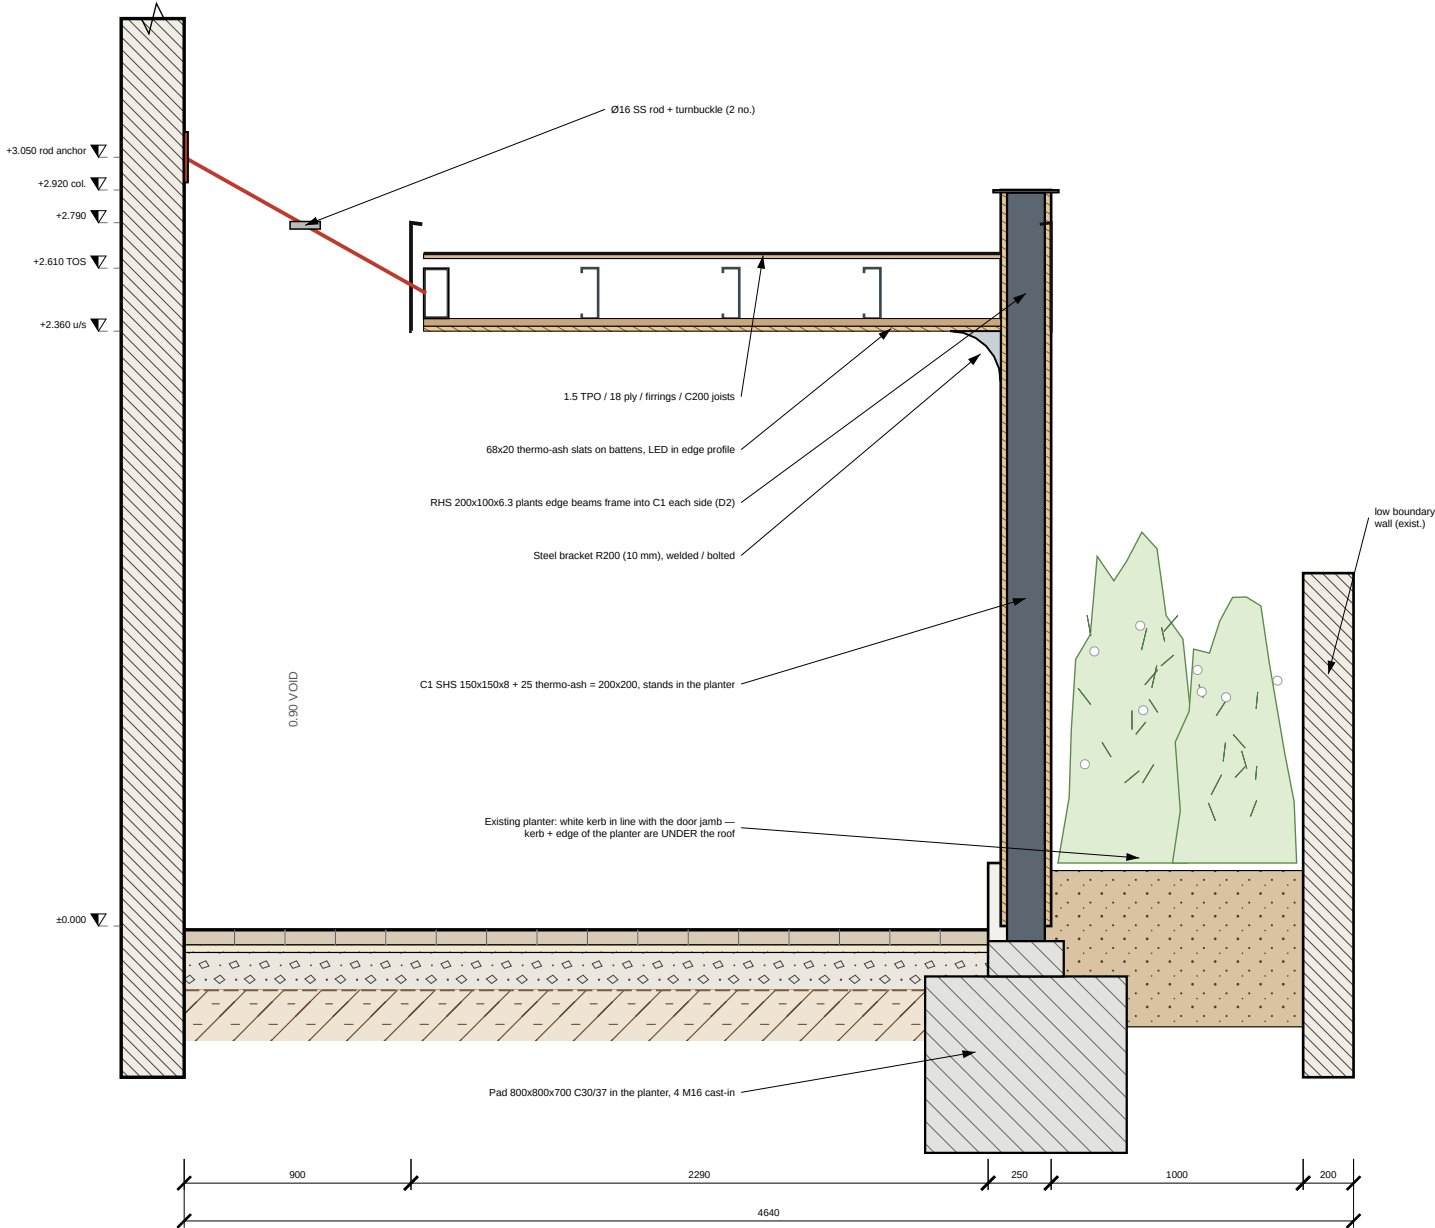


SPECIFICATION
Steel S355, hot-dip galvanised; columns & brackets powder-coated RAL 9010 or timber-clad (thermo-ash).
Roof: TPO 1.5 on 18 mm marine ply on tapered firrings (fall 1:70 to the free-edge box gutter).
Soffit: thermo-ash 68x20 slats, LED 2700 K in perimeter profile. Fascia 3 mm aluminium RAL 9010, 0.43 m.
Rods: Ø16 stainless 316, fork ends, turnbuckle, = 30° rise; engineer to confirm wall anchors.

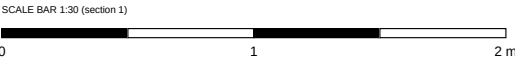


D1 ROD TO WALL (client sketch B) — 1:20

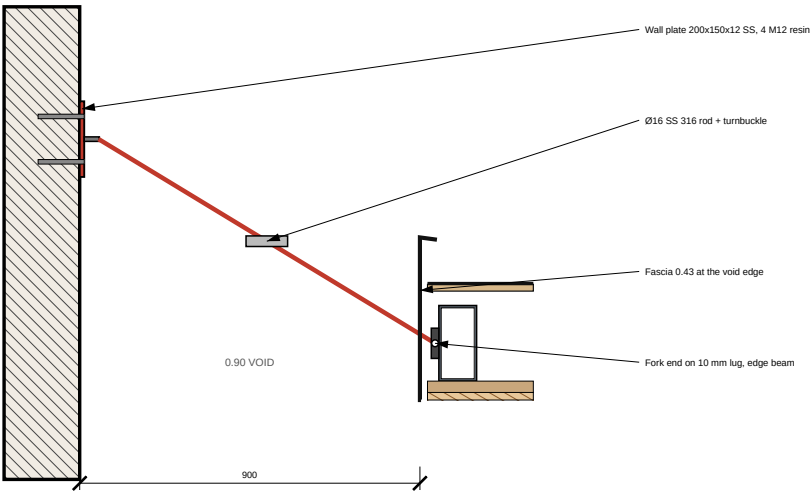

D2 COLUMN / ROOF JUNCTION (plants side) — 1:15

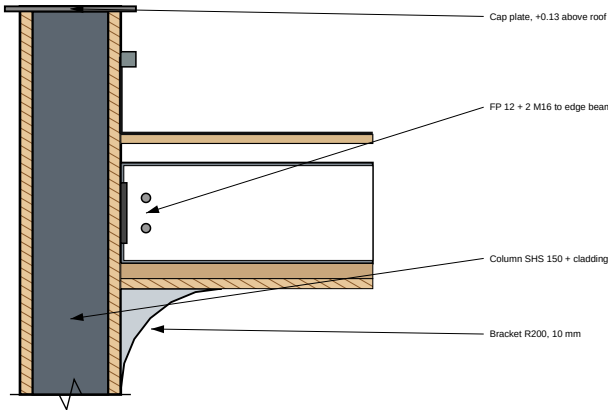

D3 TIP AT C2 (triangle) — PLAN 1:15

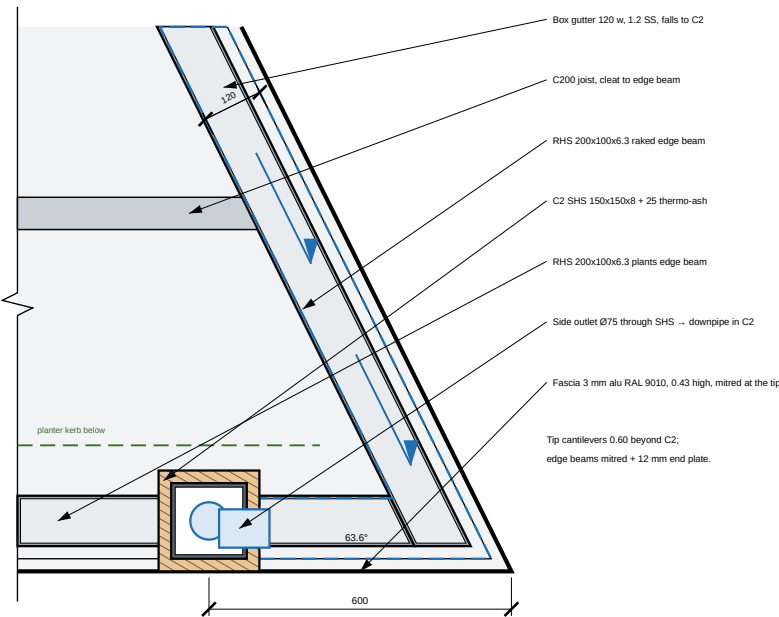

COURTYARD ROOF — V2T

VERSION 2T — TRIANGLE, 0.90 m VOID + 2 RODS: triangular roof: plants edge 3.22 + 1.26 = 4.48, void edge 3.22, raked edge 2.84; 0.90 m void open, 2 Ø16 stainless rods to the wall; 2 columns on the plants side
Client: Owner / Client
Design & drawings: Claude Code

DRAWING NOTES

- Do not scale from this drawing. Use figured dimensions only.
- All dimensions in millimetres; levels in metres relative to internal FFL ±0.000 (datum to be tied to site survey).
- Contractor to verify all dimensions, levels & existing structure on site before fabrication or ordering.
- Read with all other architectural, structural & services drawings and the specification notes (A-001).
- Structural members are preliminary: final design, connections & calculations by a licensed structural engineer to local code before construction.
- Report any discrepancy to the designer before proceeding.

REVISIONS

Rev	Date	Description
C06	07.10.2026	Garden = planter in front of the façade, left of the door, partly under roof
C05	07.10.2026	Triangular versions V1T/V2T; 3D views; details D3
C04	07.10.2026	Two versions V1/V2 per client sections & site photo
C02	07.10.2026	Canopy to client sketch: 8.00 house, roof 3.22, u/s 2.36, fascia 0.43

PREVIEW FOR CLIENT REVIEW — per client sketch, mark-ups & site photo; not for construction

DRAWING TITLE

V2T TRIANGLE + RODS
roof section & details

SCALE @ A3

1:30 / 1:15 / 1:20

DRAWN / CHECKED

CC / —

DATE

07.10.2026

SERIES

ARCHITECTURAL

DRAWING No.

V2T-03

REV

C06