



OPTION E — RECTANGLE 3.06 x 3.44 TO THE AC LINE

TALL HOUSE WALL (exist., AC units)

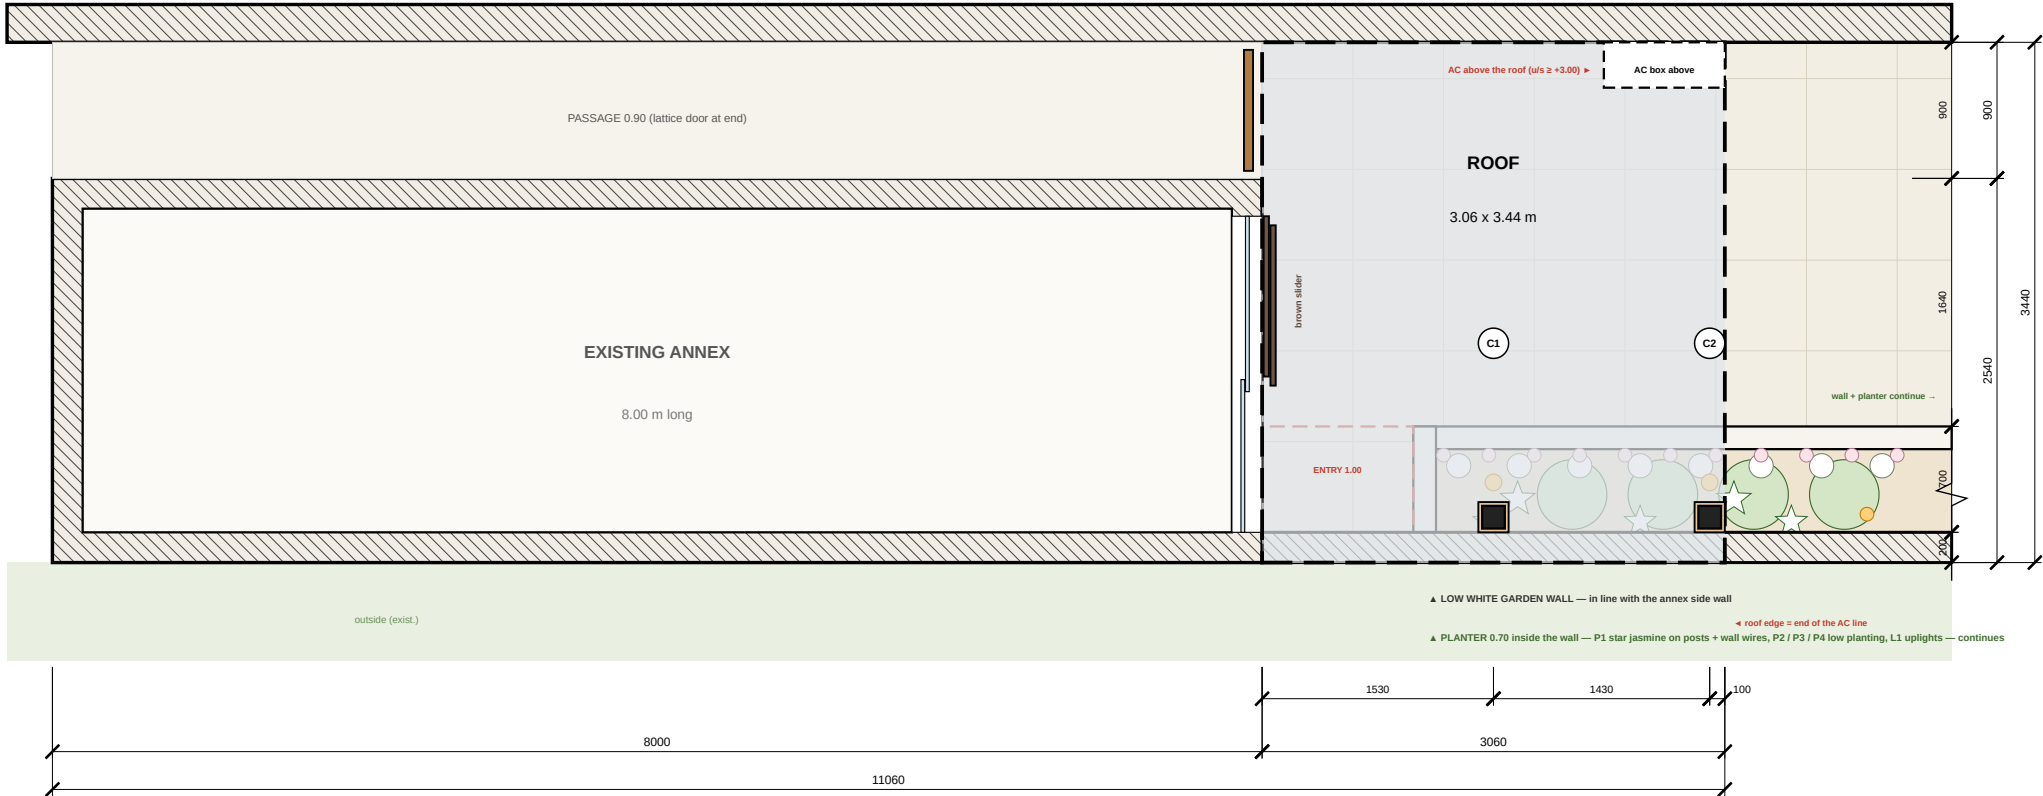


1 TOP VIEW — ANNEX, GARDEN & ROOF

2/V1-01 ROOF FRAMING PLAN — 1:30

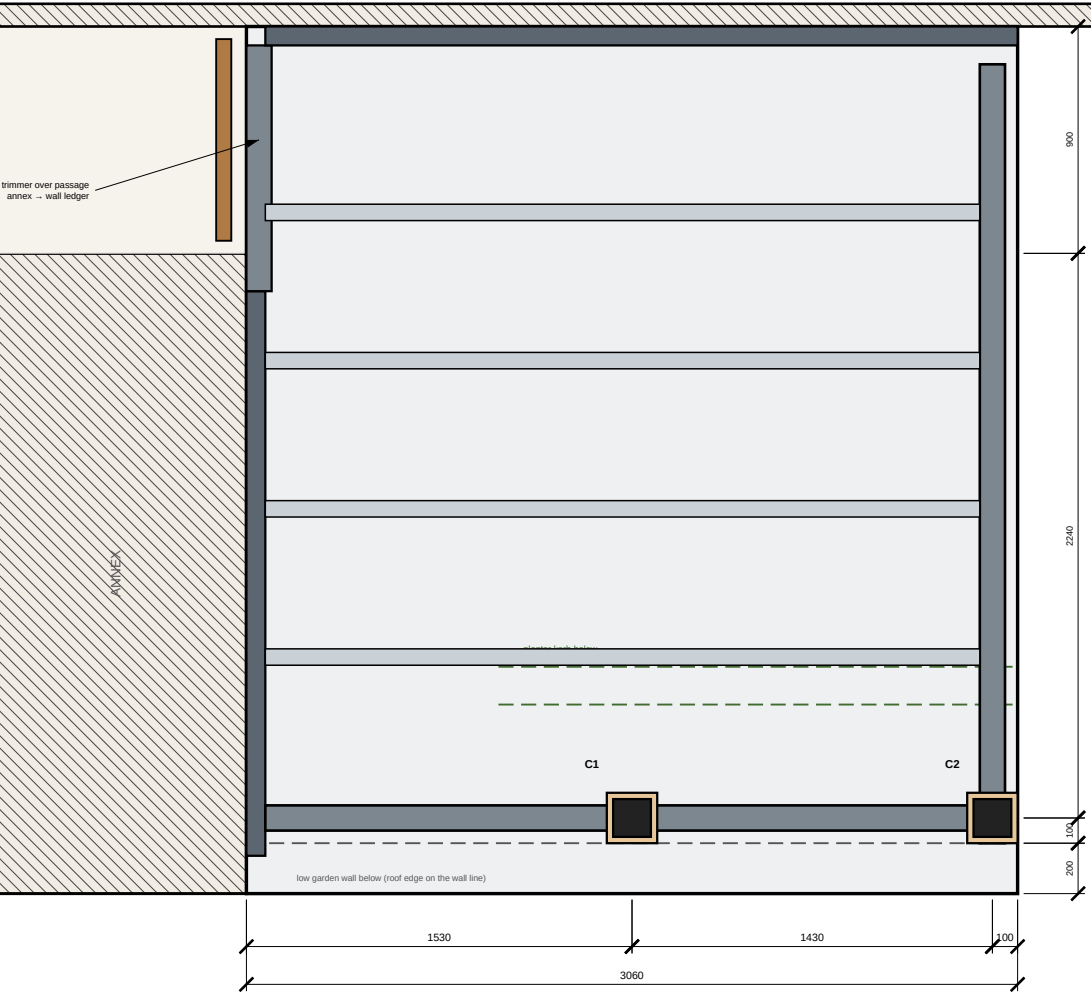

THIS VERSION
roof made longer: 3.06 x 3.44 to the tall wall, no void; right edge in line with the end of the AC box, the AC sits above the roof; bears on the annex ledger + a ledger on the tall wall; 2 columns against the garden wall.
Roof fixed to the annex end façade AND to the tall house wall (steel ledgers, resin anchors); covers the passage in front of the lattice door (RHS trimmer over the passage, annex ... wall ledger).
Column tops (from the roof underside up, incl. the 0.13 above the roof + cap) painted RAL 9010 like the fascia.
C1 in the middle of the plants edge, C2 at the corner; roof 3.06 long on both sides — right edge in line with the end of the AC box; the AC sits above the roof (u/s ≥ +3.00, verify / re-hang on brackets).
COMMON
Annex side wall and low white garden wall are ONE line; the roof's plants edge (fascia) is on it.
Planter 0.70 inside the wall (soil + white kerb), continues along the wall; paved entry space 1.00 between the façade and the planter (walk in to the left glass door).
Entrance opening runs to the side wall (no pier).
C1 / C2: SHS 150 clad 200x200 thermo-ash, against the garden wall, 2 SS brackets each into the wall; edge beam on the column line, roof cantilevers 0.30 to the fascia over the wall.
Underside +2.36, fascia 0.43 (top +2.79); columns 0.13 above roof. Falls 1:70 to the box gutter on the raked edge; rainwater down C2.

3/V1-01 3D — BIRD'S EYE (from outside, over the low garden wall)

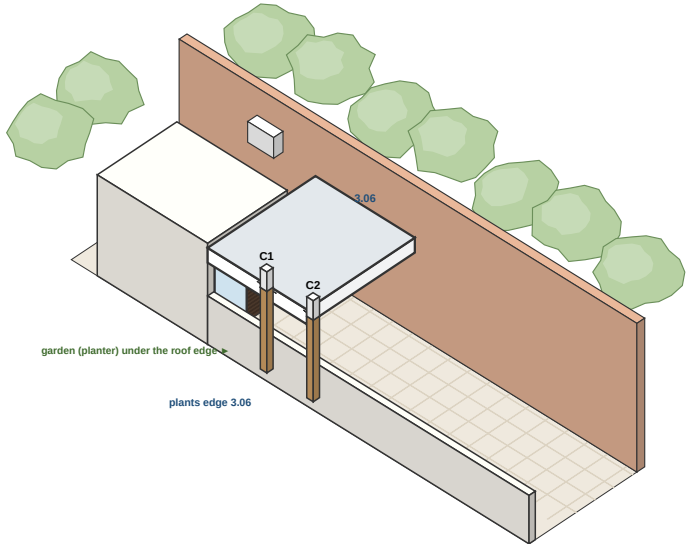

COURTYARD ROOF — V1

OPTION E — RECTANGLE 3.06 x 3.44 TO THE AC LINE: roof made longer: 3.06 x 3.44 to the tall wall, no void; right edge in line with the end of the AC box, the AC sits above the roof; bears on the annex ledger + a ledger on the tall wall; 2 columns against the garden wall
Client: Owner / Client
Design & drawings: Claude Code

- DRAWING NOTES**
- Do not scale from this drawing. Use figured dimensions only.
 - All dimensions in millimetres; levels in metres relative to internal FFL ±0.000 (datum to be tied to site survey).
 - Contractor to verify all dimensions, levels & existing structure on site before fabrication or ordering.
 - Read with all other architectural, structural & services drawings and the specification notes (A-001).
 - Structural members are preliminary: final design, connections & calculations by a licensed structural engineer to local code before construction.
 - Report any discrepancy to the designer before proceeding.

REVISIONS		
Rev	Date	Description
C21	08.10.2026	Column tops painted like the roof front (fascia RAL 9010)
C20	08.10.2026	Option E: rectangle 3.06 x 3.44 to the end of the AC line; AC above the roof

FOR CLIENT CHECK — option E: column tops painted like the roof front (fascia white)

DRAWING TITLE

OPTION E — RECTANGLE 3.06
top view & roof framing

SCALE @ A3 1:50 / 1:30	DATE 08.10.2026
DRAWN / CHECKED CC / —	SERIES ARCHITECTURAL

DRAWING No. REV

C21-E C21