

COURTYARD CANOPY & GARDEN TERRACE

Roof 3.22 x 2.54 m at end of existing 8.00 m house; 0.90 m strip to plants kept free
Client: Owner / Client
Design & drawings: Claude Code

- DRAWING NOTES
- Do not scale from this drawing. Use figured dimensions only.
 - All dimensions in millimetres; levels in metres relative to internal FFL ±0.000 (datum to be tied to site survey).
 - Contractor to verify all dimensions, levels & existing structure on site before fabrication or ordering.
 - Read with all other architectural, structural & services drawings and the specification notes (A-001).
 - Structural members are preliminary: final design, connections & calculations by a licensed structural engineer to local code before construction.
 - Report any discrepancy to the designer before proceeding.

REVISIONS		
Rev	Date	Description
C02	07.10.2026	Canopy to client sketch: 8.00x3.44, u/s 2.36, fascia 0.43
C01	06.10.2026	Issued for construction / tender
P01	05.10.2026	Concept (client renders)

PREVIEW FOR CLIENT REVIEW — per client sketch & mark-up; not for construction until confirmed


DRAWING TITLE

Top view — site plan & roof plan (Rev C03 preview)

SCALE @ A3	DATE
1:50 / 1:25	07.10.2026
DRAWN / CHECKED	SERIES
CC / —	ARCHITECTURAL

DRAWING No. REV


P-01 C03

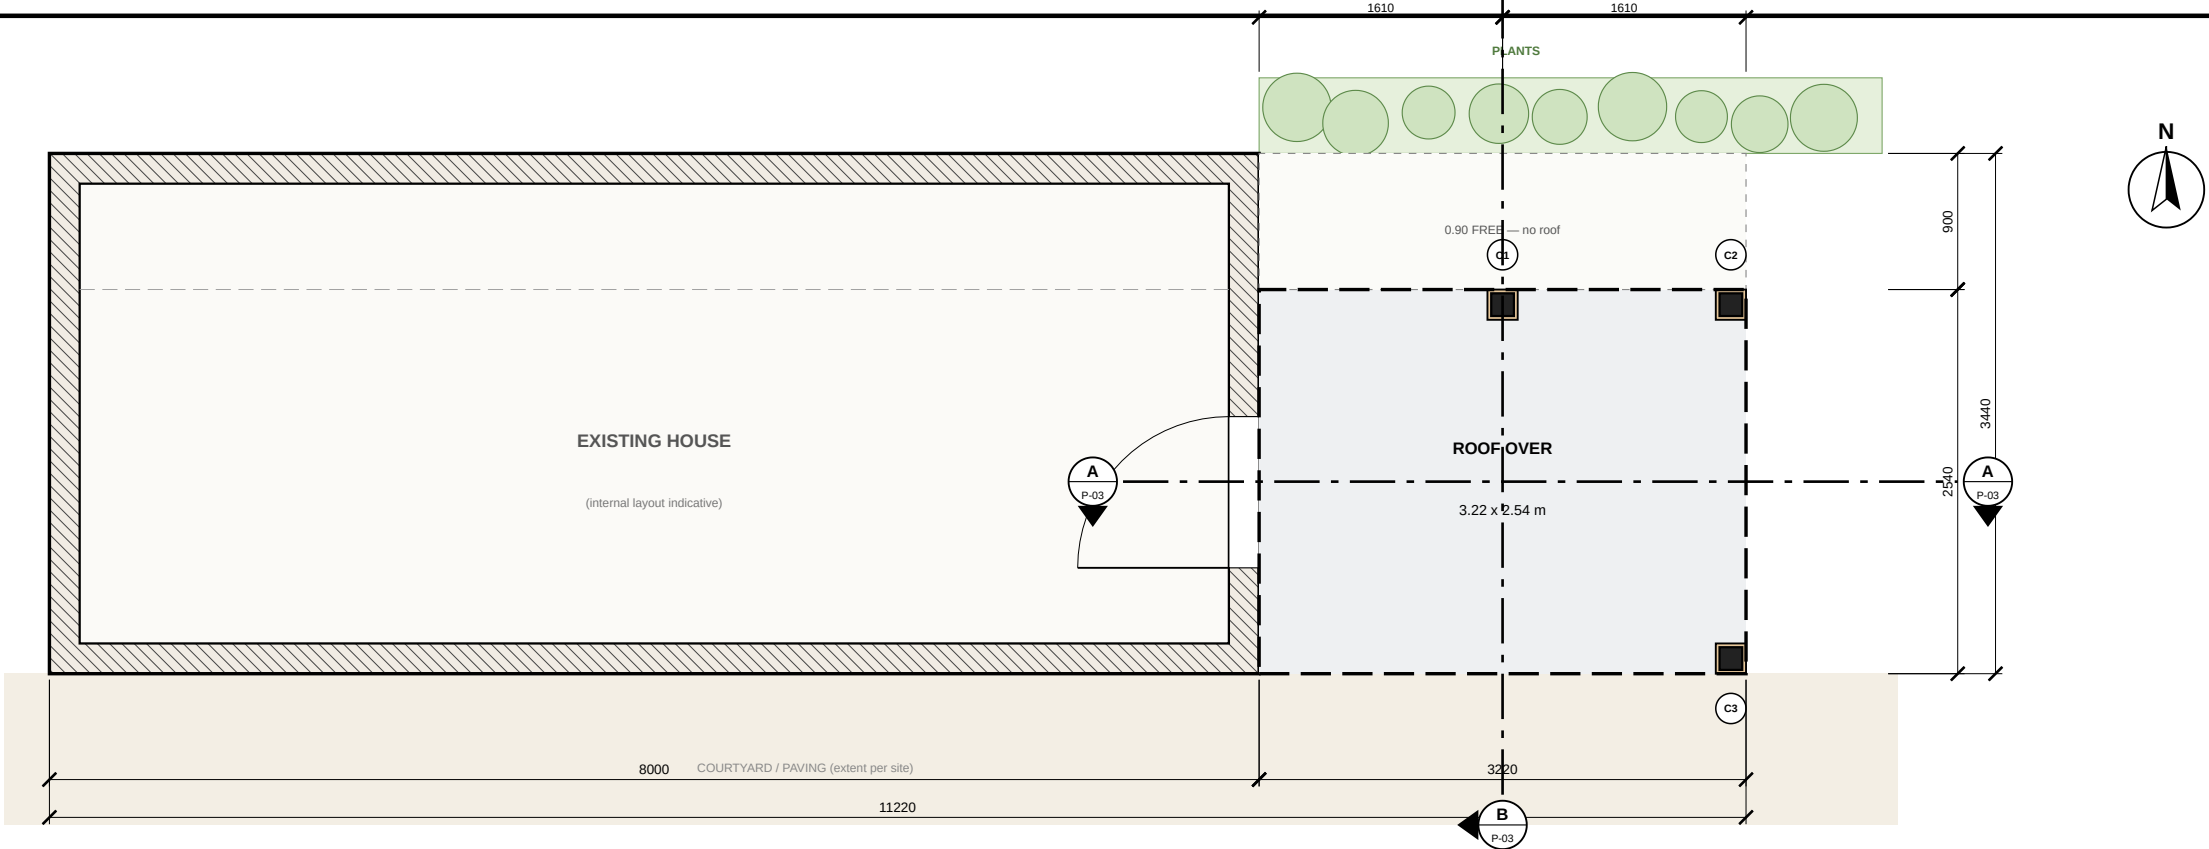

1 TOP VIEW — HOUSE & ROOF



P-01 1:50 @ A3 roof edge on client's marked line

2/P-01 ROOF PLAN — 1:25

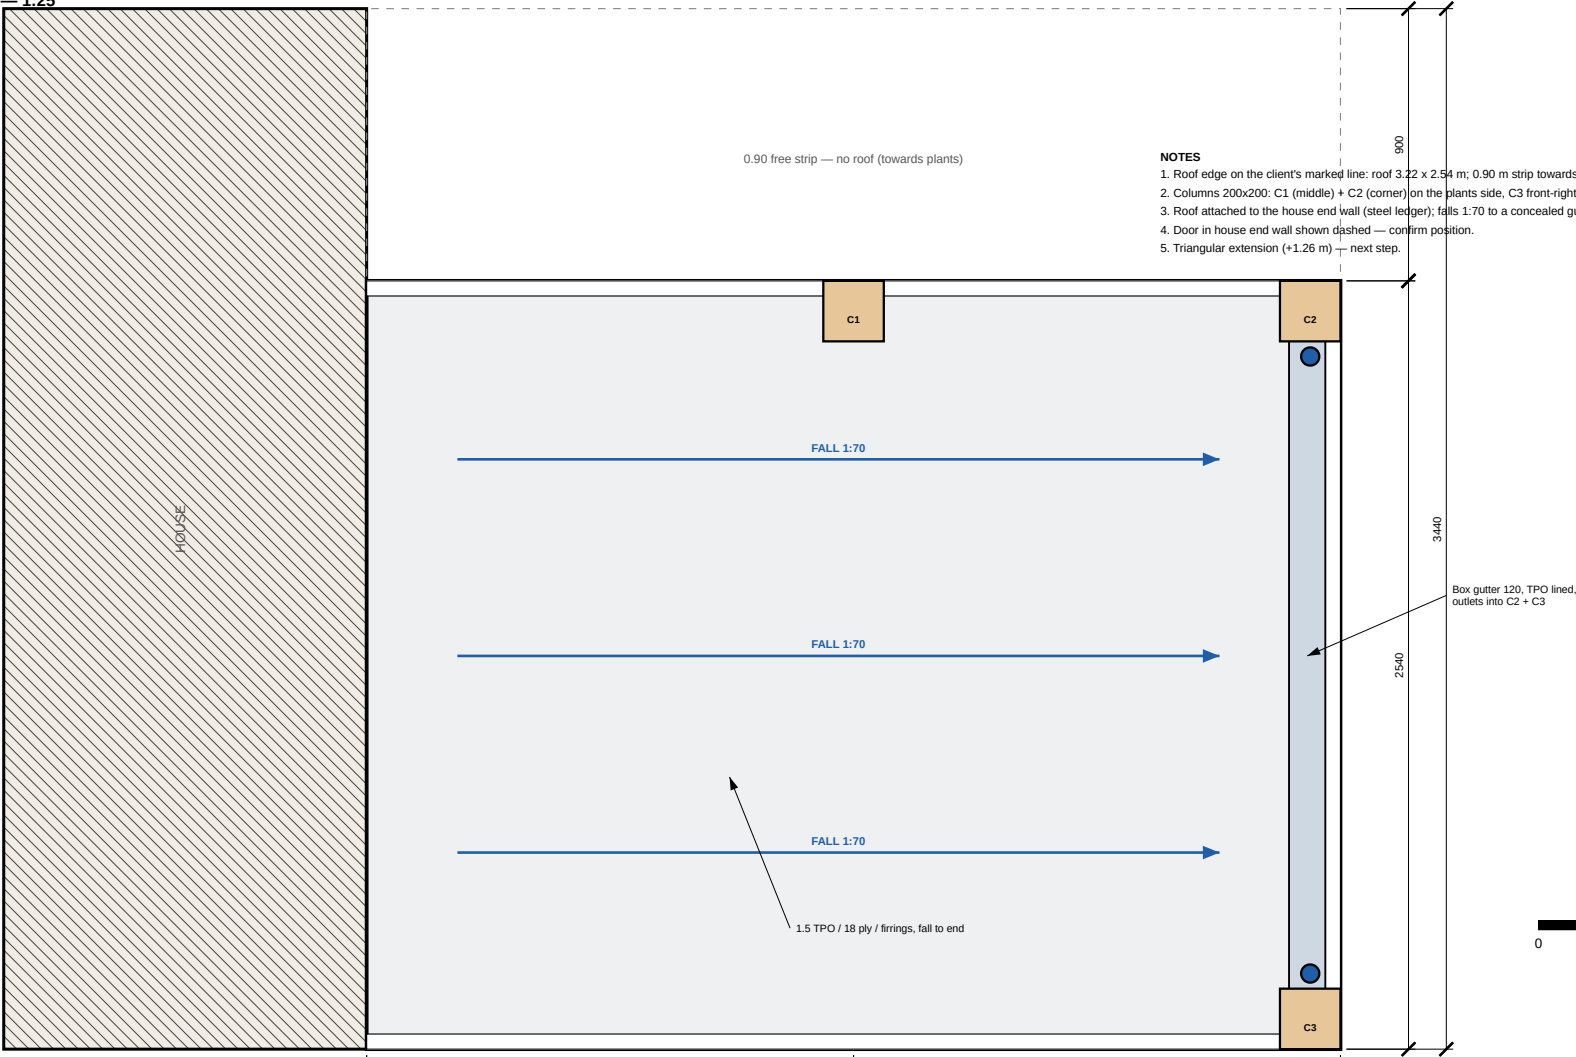


- NOTES
- Roof edge on the client's marked line: roof 3.22 x 2.54 m; 0.90 m strip towards the plants left free.
 - Columns 200x200: C1 (middle) + C2 (corner) on the plants side, C3 front-right. Roof frames into the column sides; columns rise 0.13 above the roof.
 - Roof attached to the house end wall (steel ledger); falls 1:70 to a concealed gutter at the free end; rainwater down C2 and C3.
 - Door in house end wall shown dashed — confirm position.
 - Triangular extension (+1.26 m) — next step.


Box gutter 120, TPO lined, outlets into C2 + C3

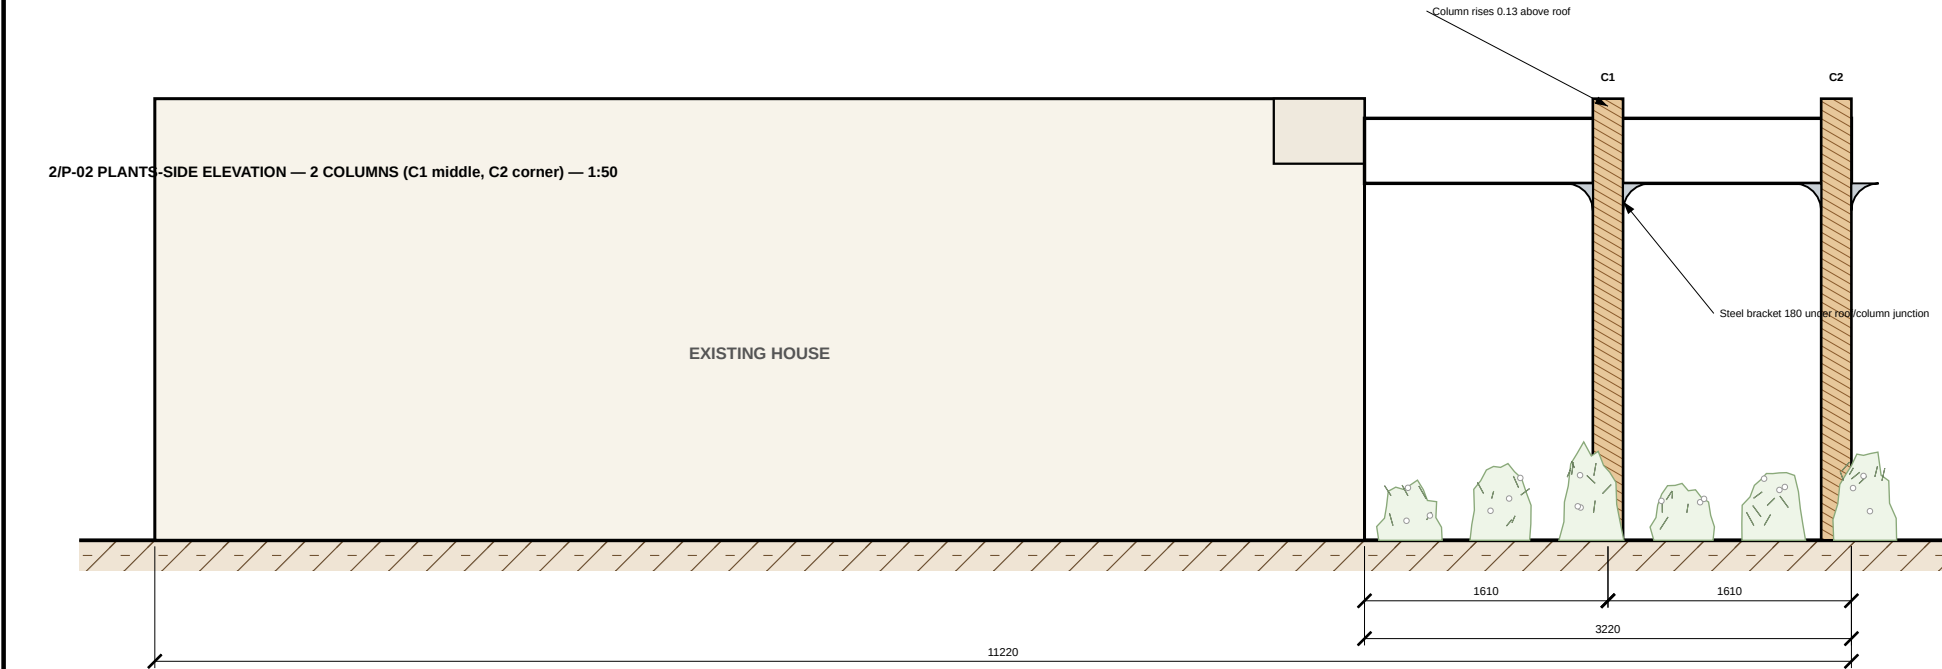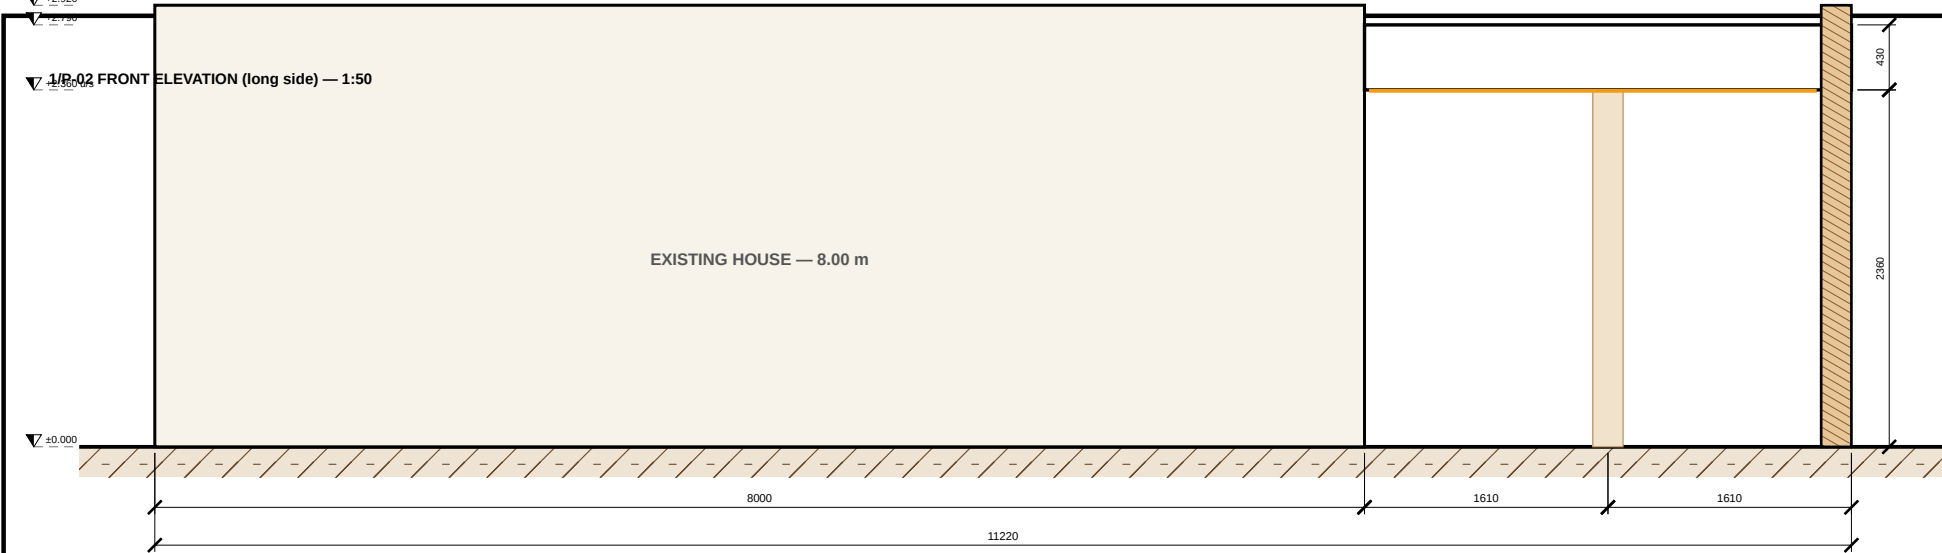

3/P-02 END VIEW (free end) — 1:50

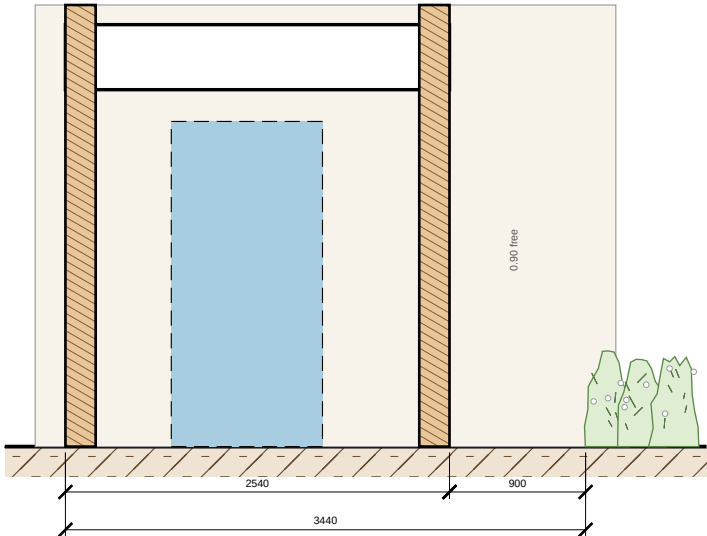

CLIENT DIMENSIONS (m)
House 8.00 · Roof 3.22 x 2.54 (edge on marked line) · free strip to plants 0.90 · columns 0.20
· roof underside 2.36 · fascia band 0.43 (top 2.79) · column top +2.92.
Columns: C1 middle + C2 corner on plants side; C3 front-right corner.
Triangular extension (+1.26) — next step, not shown.

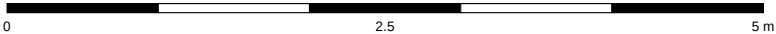

COURTYARD CANOPY & GARDEN TERRACE

Roof 3.22 x 2.54 m at end of existing 8.00 m house; 0.90 m strip to plants kept free
Client: Owner / Client
Design & drawings: Claude Code

DRAWING NOTES

- Do not scale from this drawing. Use figured dimensions only.
- All dimensions in millimetres; levels in metres relative to internal FFL ± 0.000 (datum to be tied to site survey).
- Contractor to verify all dimensions, levels & existing structure on site before fabrication or ordering.
- Read with all other architectural, structural & services drawings and the specification notes (A-001).
- Structural members are preliminary: final design, connections & calculations by a licensed structural engineer to local code before construction.
- Report any discrepancy to the designer before proceeding.

REVISIONS

Rev	Date	Description
C02	07.10.2026	Canopy to client sketch: 8.00x3.44, u/s 2.36, fascia 0.43
C01	06.10.2026	Issued for construction / tender
P01	05.10.2026	Concept (client renders)

PREVIEW FOR CLIENT REVIEW — per client sketch & mark-up; not for construction until confirmed

DRAWING TITLE

Elevations — front, plants side & end (Rev C03 preview)


SCALE @ A3 1:50	DATE 07.10.2026
DRAWN / CHECKED CC / —	SERIES ARCHITECTURAL

DRAWING No. REV

P-02

C03

1/P-03 SECTION A-A — ALONG ROOF (house → free end), columns C1/C2 beyond — 1:20

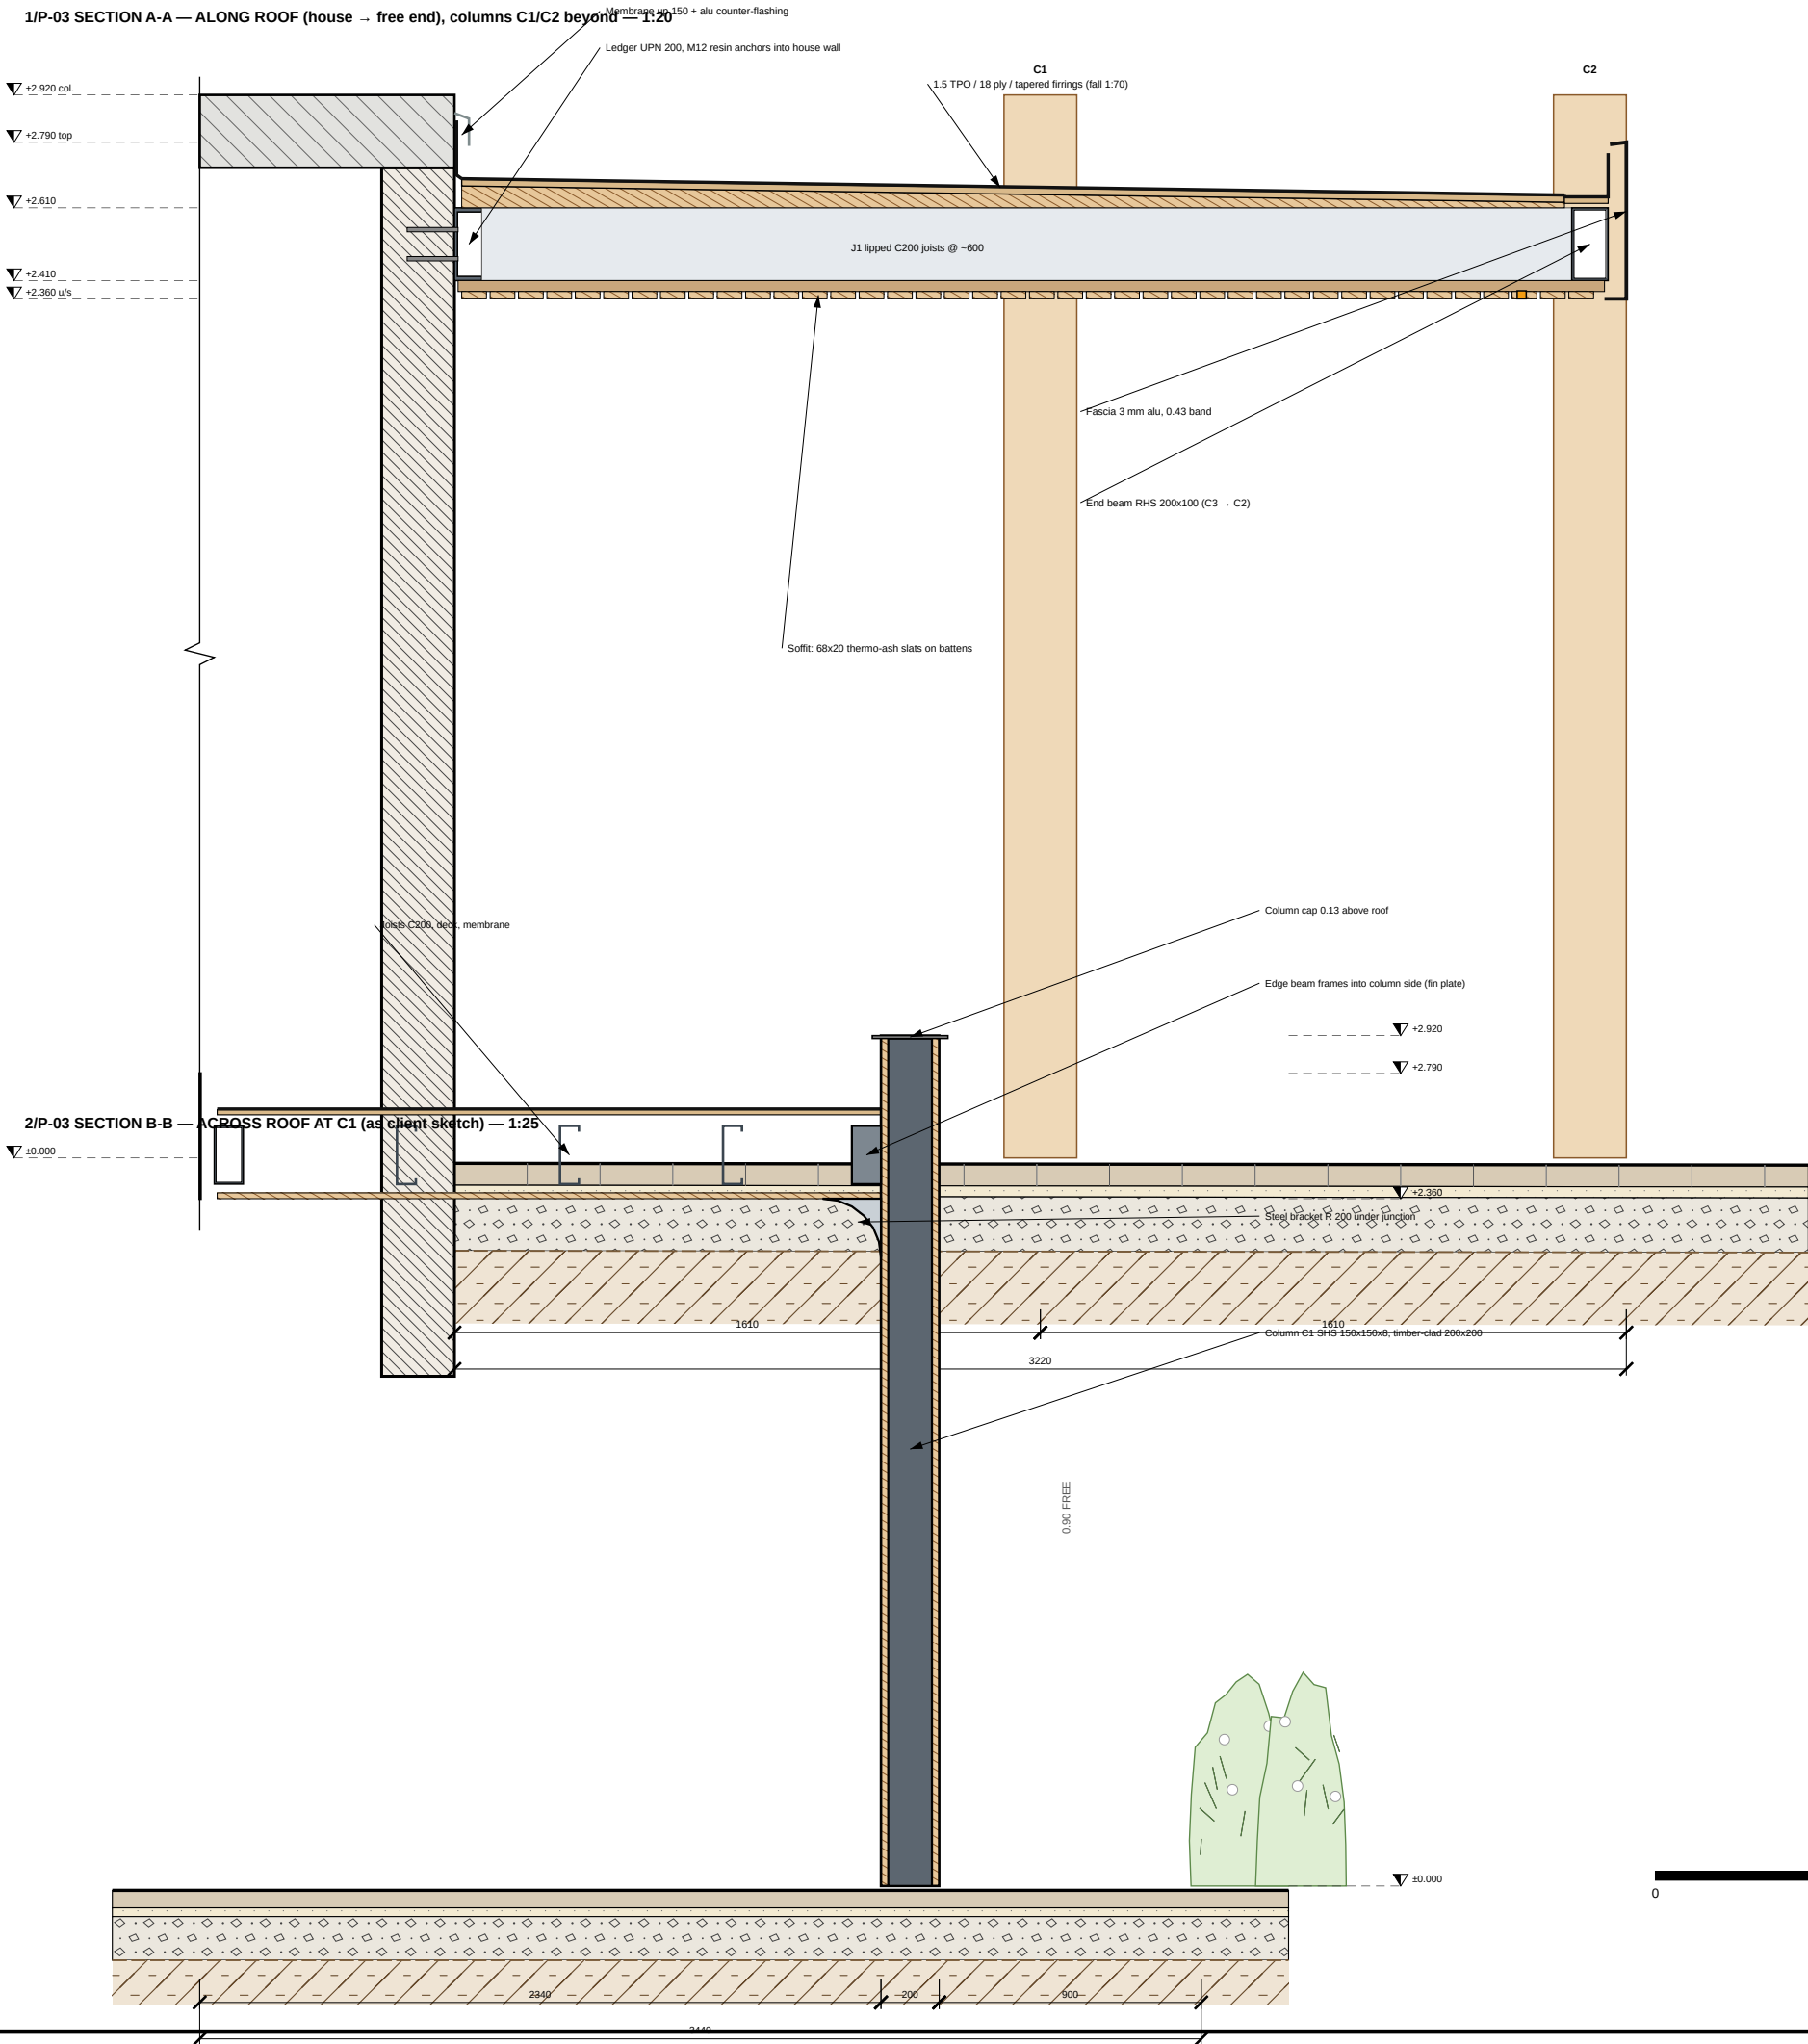

COURTYARD CANOPY & GARDEN TERRACE

Roof 3.22 x 2.54 m at end of existing 8.00 m house; 0.90 m strip to plants kept free
Client: Owner / Client
Design & drawings: Claude Code

- DRAWING NOTES**
- Do not scale from this drawing. Use figured dimensions only.
 - All dimensions in millimetres; levels in metres relative to internal FFL ± 0.000 (datum to be tied to site survey).
 - Contractor to verify all dimensions, levels & existing structure on site before fabrication or ordering.
 - Read with all other architectural, structural & services drawings and the specification notes (A-001).
 - Structural members are preliminary: final design, connections & calculations by a licensed structural engineer to local code before construction.
 - Report any discrepancy to the designer before proceeding.

REVISIONS		
Rev	Date	Description
C02	07.10.2026	Canopy to client sketch: 8.00x3.44, u/s 2.36, fascia 0.43
C01	06.10.2026	Issued for construction / tender
P01	05.10.2026	Concept (client renders)

PREVIEW FOR CLIENT REVIEW — per client sketch & mark-up; not for construction until confirmed

DRAWING TITLE

Sections A-A (along roof) & B-B (across roof at C1) — Rev C03 preview

SCALE @ A3	DATE
1:20 / 1:25	07.10.2026
DRAWN / CHECKED	SERIES
CC / —	ARCHITECTURAL

DRAWING No. REV

P-03 **C03**

1/P-04 ROOF FRAMING PLAN @ TOS +2.610 — 1:25

D1 ROOF / COLUMN JUNCTION — 1:10

(as client section sketch)

Mark	Member	No.	Length	Note
L1	UPN 200 S275 HDG ledger on house wall	1	2.24 m	M12 resin anchors @ 400
B1	RHS 200x100x6.3 end beam	1	2.14 m	C3 → C2
B2	RHS 200x100x6.3 plants-side edge beam	2	1.4 / 1.3	house → C1 → C2
B3	RHS 200x100x6.3 front edge beam	1	3.0 m	house → C3
J1	Lipped C 200x65x20x1.8	3	2.99 m	@ -600 c/c
C1-C3	SHS 150x150x8, clad to 200x200	3	2.92 m	RWP in C2 + C3; pads 800x800x700

STRUCTURE (preliminary — engineer to confirm)

Roof 3.22 x 2.54 m, G 0.65 + snow 1.0 kN/m² (assumed). Max beam span 3.0 m: M = 4 kNm (= 5 % capacity). Columns N = 8 kN. Plywood deck acts as diaphragm to house wall. All steel hot-dip galvanised.

COURTYARD CANOPY & GARDEN TERRACE

Roof 3.22 x 2.54 m at end of existing 8.00 m house; 0.90 m strip to

plants kept free

Client: Owner / Client

Design & drawings: Claude Code

DRAWING NOTES

- Do not scale from this drawing. Use figured dimensions only.
- All dimensions in millimetres; levels in metres relative to internal FFL ±0.000 (datum to be tied to site survey).
- Contractor to verify all dimensions, levels & existing structure on site before fabrication or ordering.
- Read with all other architectural, structural & services drawings and the specification notes (A-001).
- Structural members are preliminary: final design, connections & calculations by a licensed structural engineer to local code before construction.
- Report any discrepancy to the designer before proceeding.

D2 COLUMN BASE — 1:10

REVISIONS

Rev	Date	Description
C02	07.10.2026	Canopy to client sketch: 8.00x3.44, u/s 2.36, fascia 0.43
C01	06.10.2026	Issued for construction / tender
P01	05.10.2026	Concept (client renders)

PREVIEW FOR CLIENT REVIEW — per client sketch & mark-up; not for construction until confirmed

DRAWING TITLE

Roof framing plan & column details (Rev C03 preview)

SCALE @ A3 1:25 / 1:10	DATE 07.10.2026
DRAWN / CHECKED CC / —	SERIES ARCHITECTURAL

DRAWING No.

REV

P-04

C03