

VERSION 1

TALL HOUSE WALL (exist., AC units) — top side

PASSAGE 0.90 (lattice door at end)

EXISTING ANNEX

8.00 m long

ROOF

3.22 x 3.44 m

PLANTER + TREES (plants side)

8000

LOW BOUNDARY WALL (exist.)

11220

1


TOP VIEW — ANNEX, ROOF & PLANTER

V1-01

1:50 @ A3 trees behind low wall & annex (background)



2/V1-01 ROOF FRAMING PLAN — 1:25

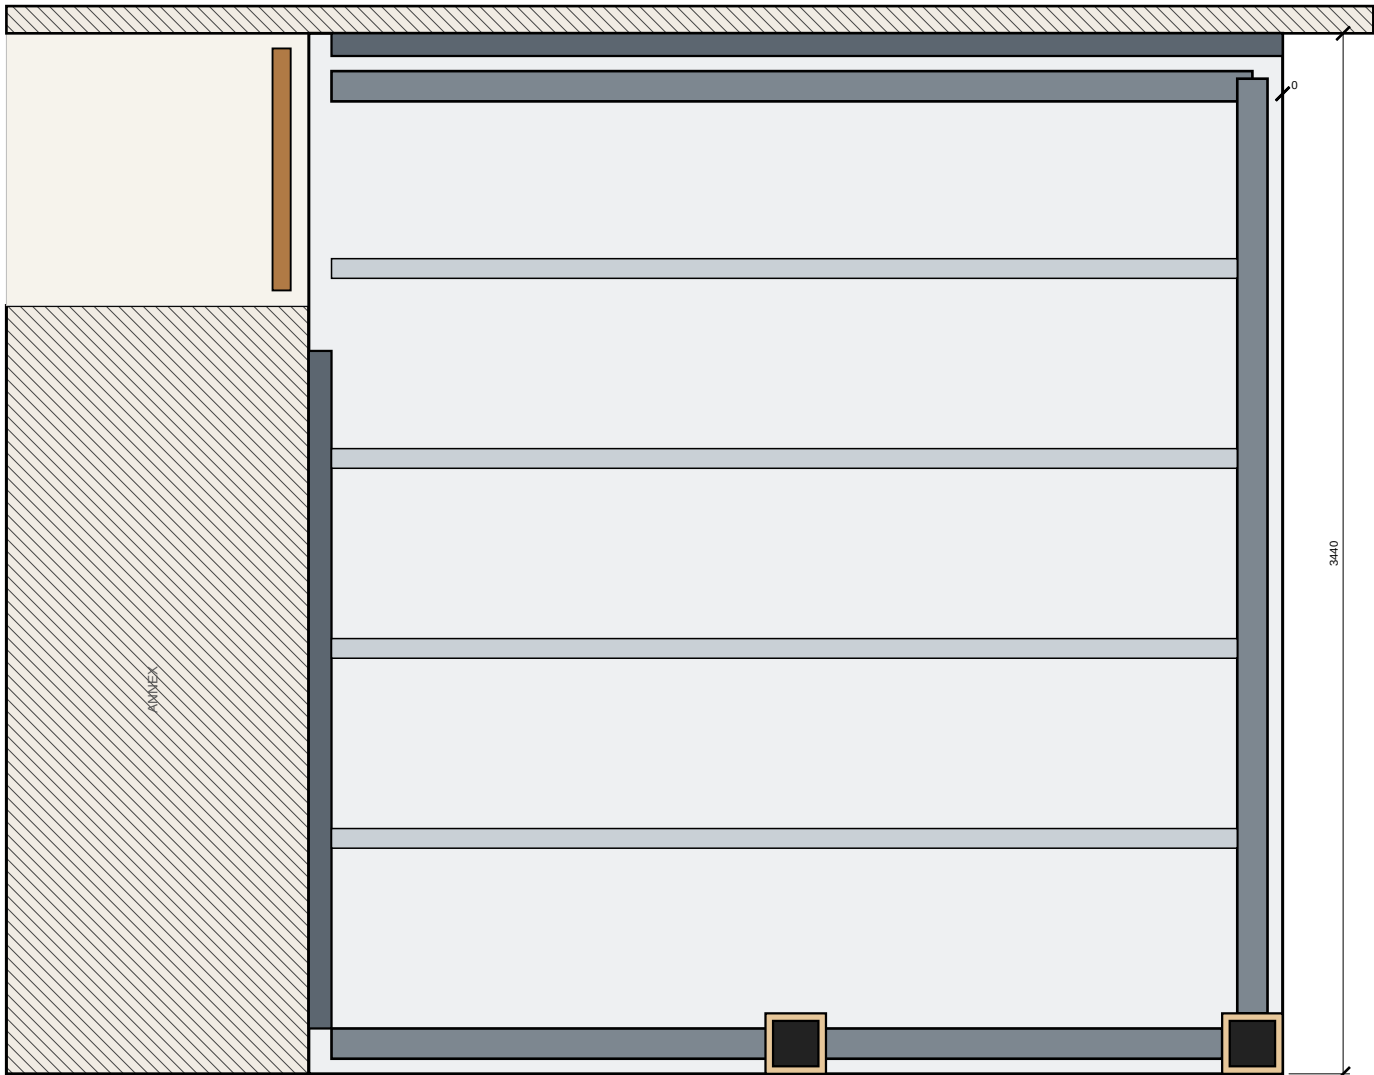

THIS VERSION

roof 3.22 x 3.44 up to the tall wall (bears on wall ledger + curved brackets); 2 columns on the plants side.

Roof fixed to the annex end façade AND to the tall house wall (steel ledgers, resin anchors); covers the passage in front of the lattice door.

Plants side: 2 columns (C1 middle, C2 corner) at the planter edge.

COMMON

Roof 3.22 m from the annex façade. Underside +2.36, fascia 0.43 (top +2.79); columns 200x200, 0.13 above roof, bracket under junction (client section).

Falls 1:70 to concealed gutter at free end; rainwater down C2.

Triangular extension (+1.26) — next step.

COURTYARD ROOF — V1

VERSION 1 — ROOF TO THE WALL: roof 3.22 x 3.44 up to the tall wall (bears on wall ledger + curved brackets); 2 columns on the plants side

Client: Owner / Client

Design & drawings: Claude Code

DRAWING NOTES

- Do not scale from this drawing. Use figured dimensions only.
- All dimensions in millimetres; levels in metres relative to internal FFL ± 0.000 (datum to be tied to site survey).
- Contractor to verify all dimensions, levels & existing structure on site before fabrication or ordering.
- Read with all other architectural, structural & services drawings and the specification notes (A-001).
- Structural members are preliminary: final design, connections & calculations by a licensed structural engineer to local code before construction.
- Report any discrepancy to the designer before proceeding.

REVISIONS

Rev	Date	Description
C02	07.10.2026	Canopy to client sketch: 8.00x3.44, u/s 2.36, fascia 0.43
C01	06.10.2026	Issued for construction / tender
P01	05.10.2026	Concept (client renders)

PREVIEW FOR CLIENT REVIEW — per client sketch, mark-up & site photo; not for construction

DRAWING TITLE

VERSION 1 — ROOF TO THE WALL — top view & roof plan

SCALE @ A3

1:50 / 1:25

DATE

07.10.2026

DRAWN / CHECKED

CC / —

SERIES


ARCHITECTURAL

DRAWING No.


REV

V1-01


C04

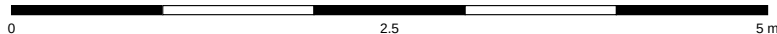

VERSION 1 — ROOF TO THE WALL

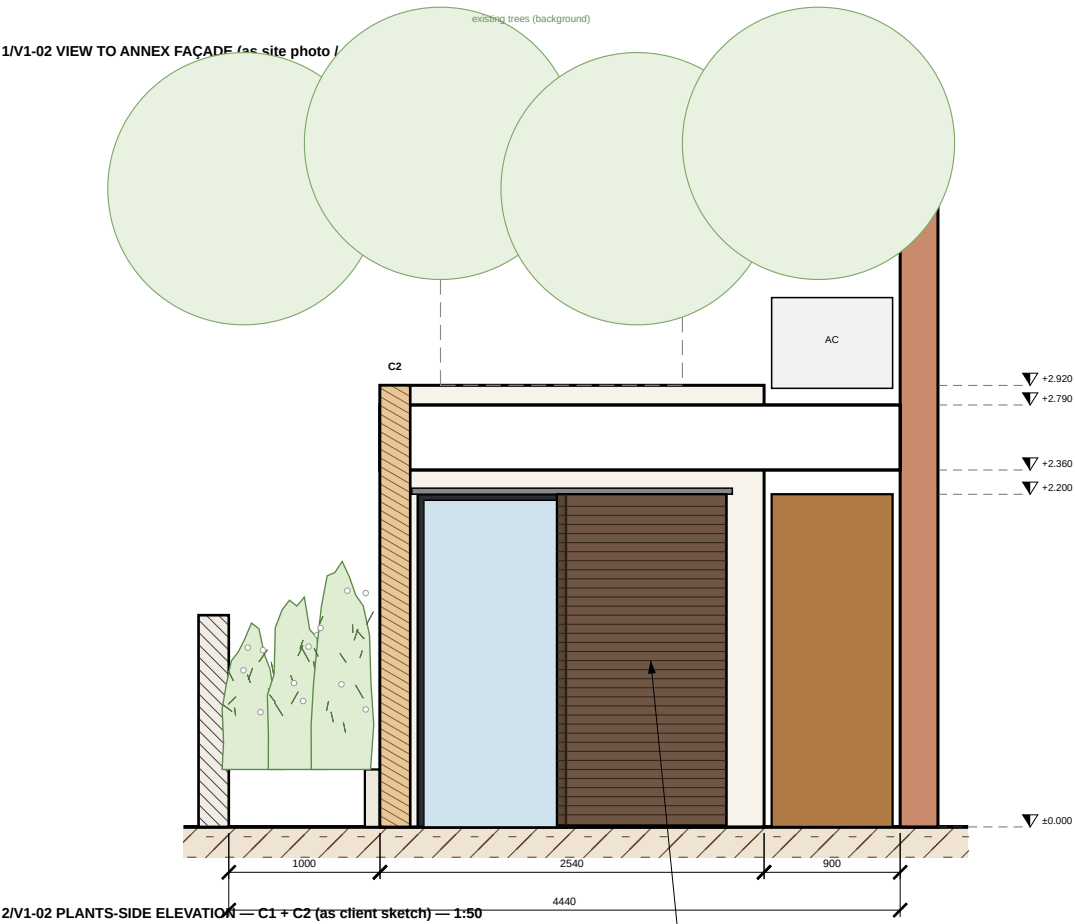


2/V1-02 PLANTS-SIDE ELEVATION — C1 + C2 (as client sketch) — 1:50

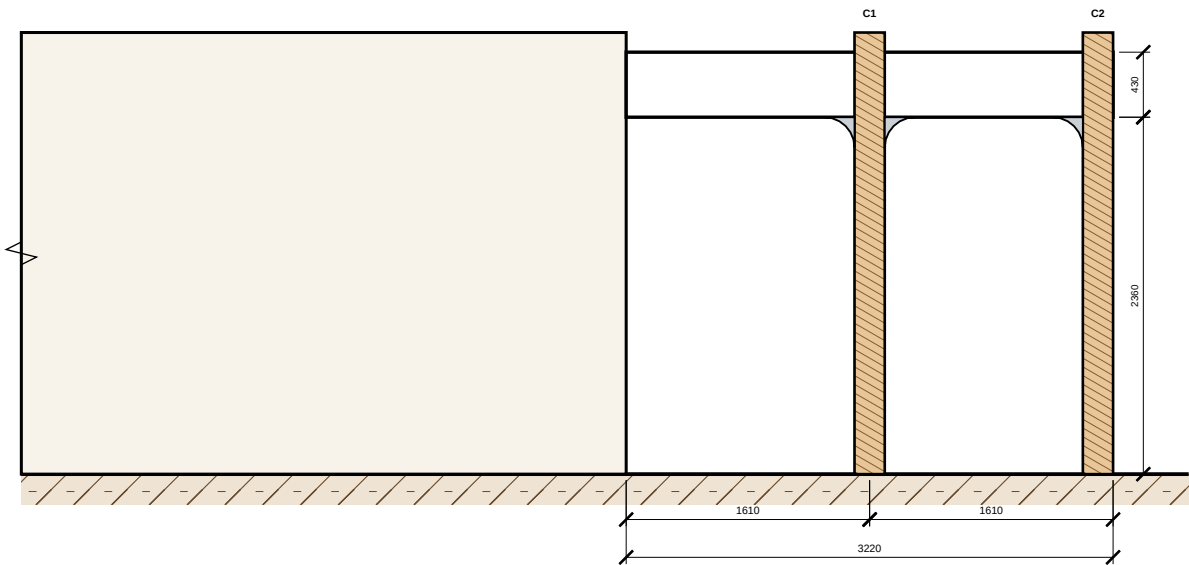

3/V1-02 SECTION ACROSS AT C1 — 1:50 (see V1-03)

tall wall left — plants right (as client sketch)

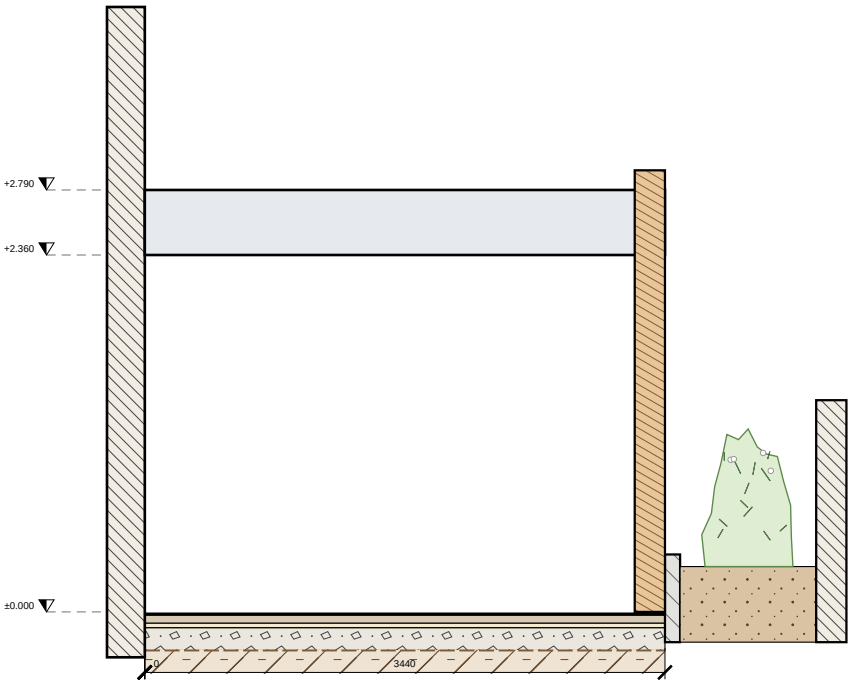

NOTES
roof 3.22 x 3.44 up to the tall wall (bears on wall ledger + curved brackets); 2 columns on the plants side.
Underside +2.36, fascia 0.43 (top +2.79); columns 0.13 above roof.
Trees are existing, behind the low boundary wall and the annex (background).
Refined roof section & details: sheet V1-03.

COURTYARD ROOF — V1

VERSION 1 — ROOF TO THE WALL: roof 3.22 x 3.44 up to the tall wall (bears on wall ledger + curved brackets); 2 columns on the plants side
Client: Owner / Client
Design & drawings: Claude Code

- DRAWING NOTES**
- Do not scale from this drawing. Use figured dimensions only.
 - All dimensions in millimetres; levels in metres relative to internal FFL ±0.000 (datum to be tied to site survey).
 - Contractor to verify all dimensions, levels & existing structure on site before fabrication or ordering.
 - Read with all other architectural, structural & services drawings and the specification notes (A-001).
 - Structural members are preliminary: final design, connections & calculations by a licensed structural engineer to local code before construction.
 - Report any discrepancy to the designer before proceeding.

REVISIONS		
Rev	Date	Description
C02	07.10.2026	Canopy to client sketch: 8.00x3.44, u/s 2.36, fascia 0.43
C01	06.10.2026	Issued for construction / tender
P01	05.10.2026	Concept (client renders)


PREVIEW FOR CLIENT REVIEW — per client sketch, mark-up & site photo; not for construction

DRAWING TITLE
VERSION 1 — ROOF TO THE WALL — view as photo, plants-side elevation & section

SCALE @ A3 1:50 / 1:25	DATE 07.10.2026
DRAWN / CHECKED CC / —	SERIES ARCHITECTURAL

DRAWING No. REV


V1-02 **C04**

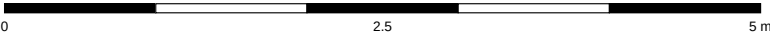


VERSION 1 — ROOF TO THE WALL

1/V1-03 ROOF SECTION ACROSS AT C1 — 1:25


(as client sketch A: roof runs to the wall)

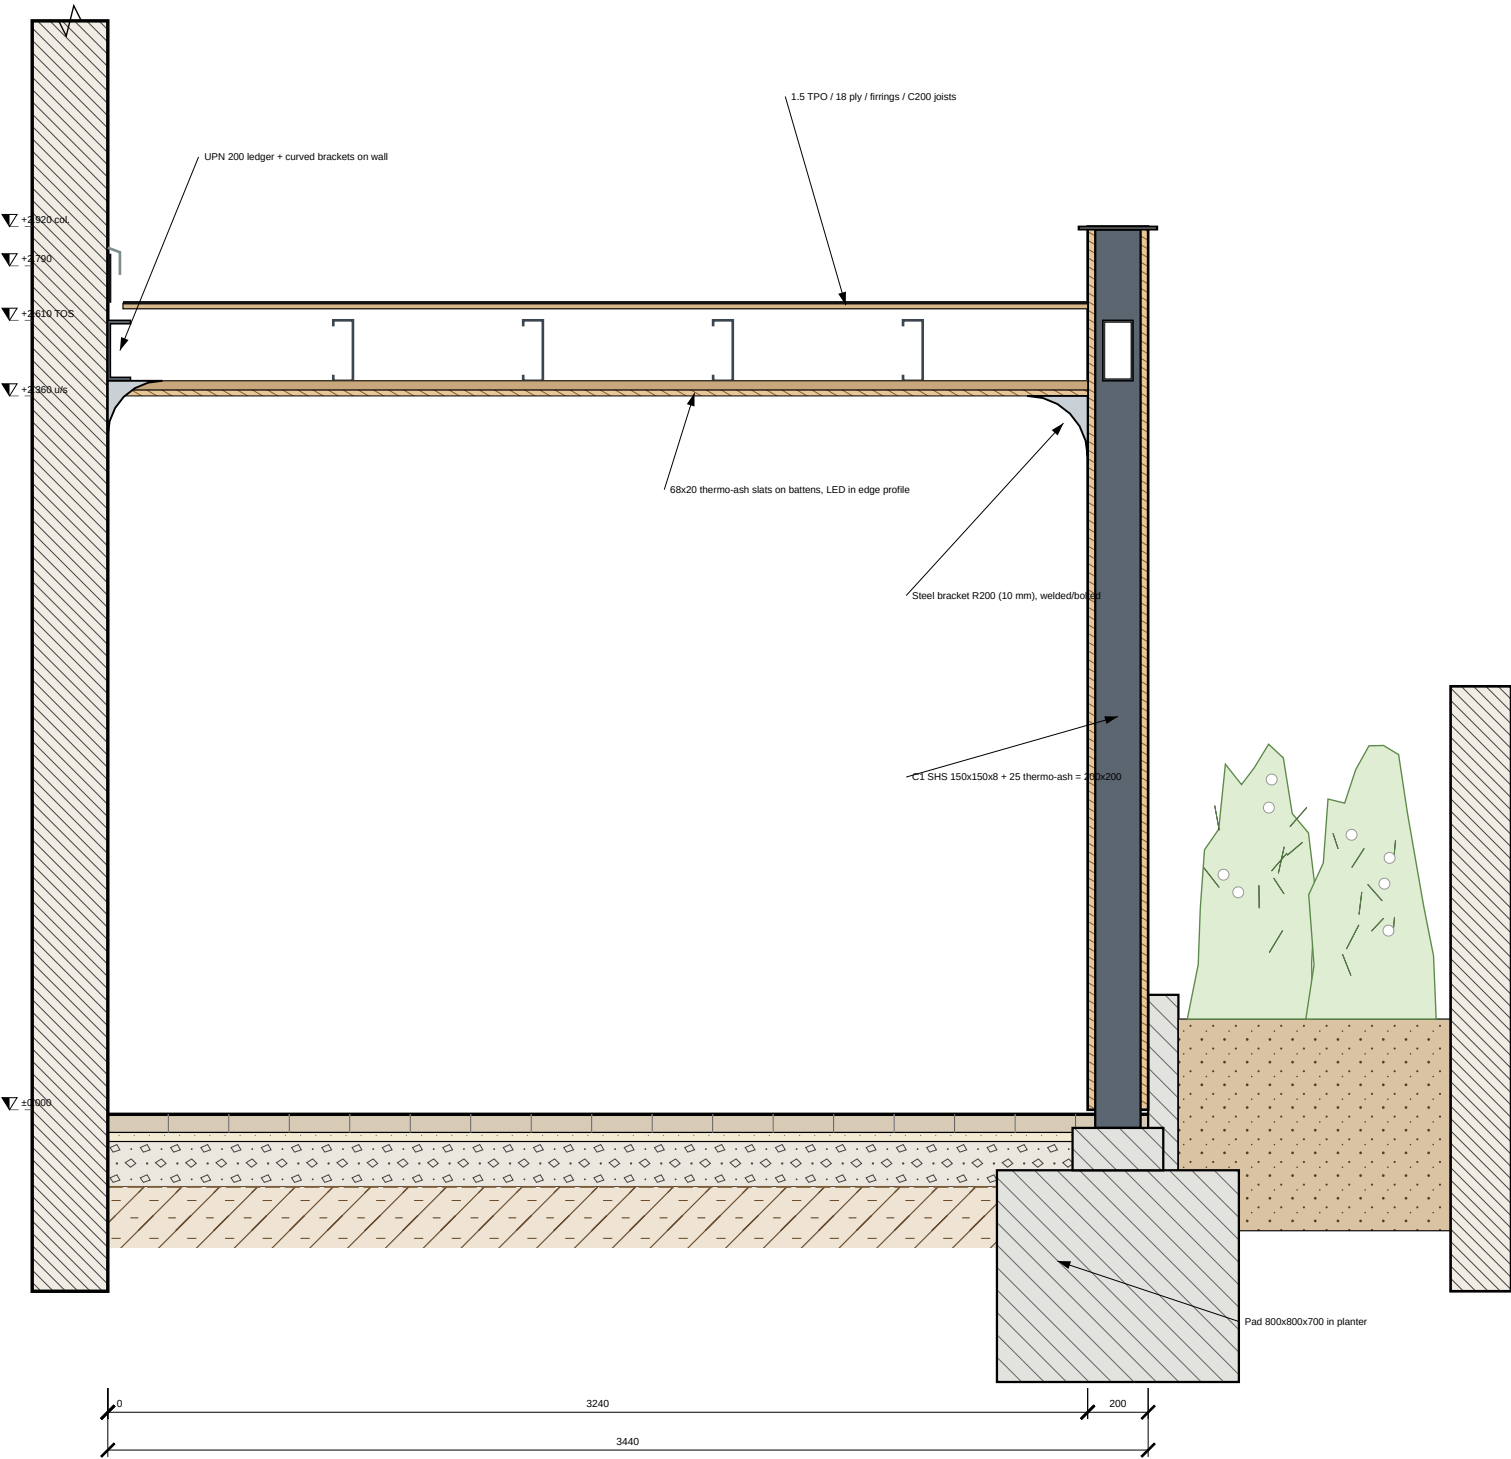


D1 ROOF TO WALL (client sketch A) — 1:15

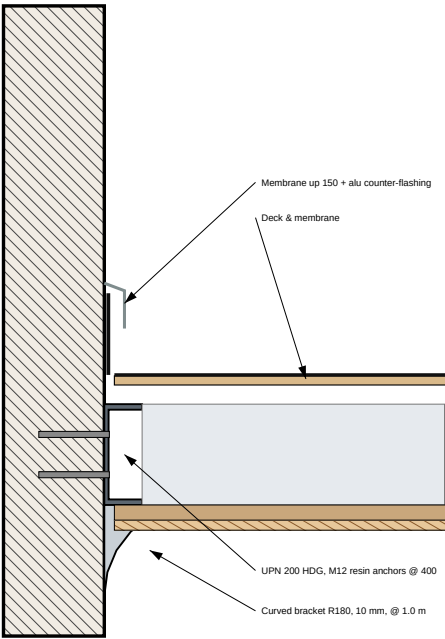

D2 COLUMN / ROOF JUNCTION (plants side) — 1:10

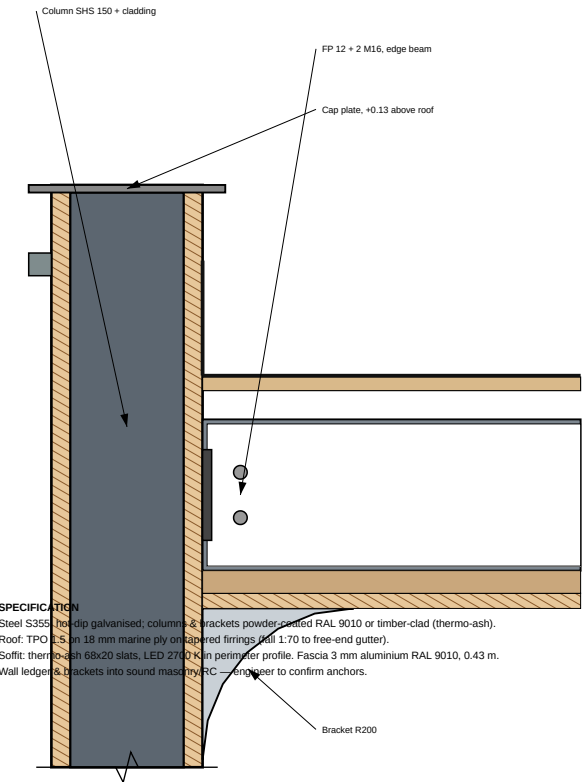

SPECIFICATION
Steel S355 hot-dip galvanised; columns & brackets powder-coated RAL 9010 or timber-clad (thermo-ash).
Roof: TPO 1.5 m 18 mm marine ply on tapered firings (pad 1:70 to free-end gutter).
Soffit: thermo-ash 68x20 slats, LED 2700 K in perimeter profile. Fascia 3 mm aluminium RAL 9010, 0.43 m.
Wall ledgers & brackets into sound masonry/RC — engineer to confirm anchors.

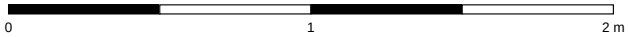

COURTYARD ROOF — V1

VERSION 1 — ROOF TO THE WALL: roof 3.22 x 3.44 up to the tall wall (bears on wall ledger + curved brackets); 2 columns on the plants side
Client: Owner / Client
Design & drawings: Claude Code

- DRAWING NOTES**
- Do not scale from this drawing. Use figured dimensions only.
 - All dimensions in millimetres; levels in metres relative to internal FFL ± 0.000 (datum to be tied to site survey).
 - Contractor to verify all dimensions, levels & existing structure on site before fabrication or ordering.
 - Read with all other architectural, structural & services drawings and the specification notes (A-001).
 - Structural members are preliminary: final design, connections & calculations by a licensed structural engineer to local code before construction.
 - Report any discrepancy to the designer before proceeding.

REVISIONS		
Rev	Date	Description
C02	07.10.2026	Canopy to client sketch: 8.00x3.44, u/s 2.36, fascia 0.43
C01	06.10.2026	Issued for construction / tender
P01	05.10.2026	Concept (client renders)

PREVIEW FOR CLIENT REVIEW — per client sketch, mark-up & site photo; not for construction

DRAWING TITLE
VERSION 1 — ROOF TO THE WALL — roof section & construction details

SCALE @ A3 1:25 / 1:10	DATE 07.10.2026
DRAWN / CHECKED CC / —	SERIES ARCHITECTURAL

DRAWING No. REV

V1-03 **C04**

VERSION 2

TALL HOUSE WALL (exist., AC units) — top side

PASSAGE 0.90 (lattice door at end)

EXISTING ANNEX

8.00 m long

PLANTER + TREES (plants side)

8000

LOW BOUNDARY WALL (exist.)

11220

ROOF

3.22 x 2.54 m

2 Ø16 SS rods to wall

N


1

TOP VIEW — ANNEX, ROOF & PLANTER

V2-01

1610 1610
1:50 @ A3 trees behind low wall & annex (background)

2/V2-01 ROOF FRAMING PLAN — 1:25

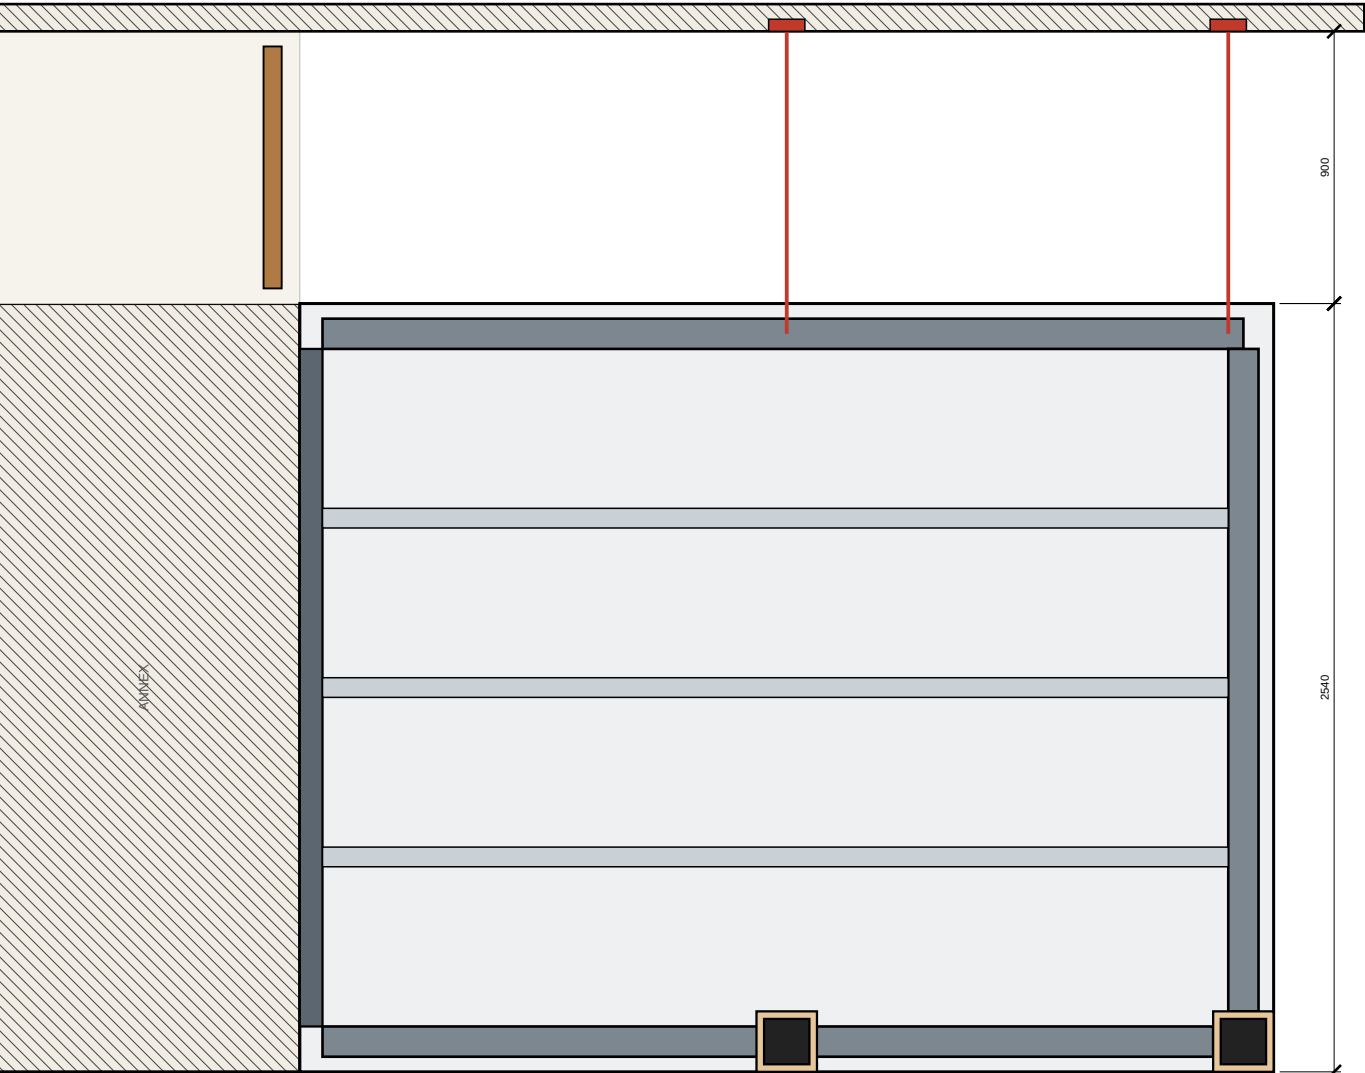

THIS VERSION

roof 3.22 x 2.54; 0.90 m void left open; void edge tied to the tall wall with 2 slim Ø16 stainless rods (rising ≈ 30°, almost horizontal); 2 columns on the plants side.
Roof fixed to the annex end façade (ledger). The 0.90 m passage to the lattice door stays open.
Top edge hung from the tall house wall on 2 Ø16 stainless rods (= 50°, turnbuckles, wall plates) — slim, almost invisible.
Plants side: 2 columns (C1 middle, C2 corner) at the planter edge.

COMMON

Roof 3.22 m from the annex façade. Underside +2.36, fascia 0.43 (top +2.79); columns 200x200, 0.13 above roof, bracket under junction (client section).
Falls 1:70 to concealed gutter at free end; rainwater down C2.
Triangular extension (+1.26) — next step.

0 2.5 5 m

COURTYARD ROOF — V2

VERSION 2 — 0.90 m VOID + 2 STEEL RODS: roof 3.22 x 2.54; 0.90 m void left open; void edge tied to the tall wall with 2 slim Ø16 stainless rods (rising ≈ 30°, almost horizontal); 2 columns on the plants side
Client: Owner / Client
Design & drawings: Claude Code

DRAWING NOTES

- Do not scale from this drawing. Use figured dimensions only.
- All dimensions in millimetres; levels in metres relative to internal FFL ±0.000 (datum to be tied to site survey).
- Contractor to verify all dimensions, levels & existing structure on site before fabrication or ordering.
- Read with all other architectural, structural & services drawings and the specification notes (A-001).
- Structural members are preliminary: final design, connections & calculations by a licensed structural engineer to local code before construction.
- Report any discrepancy to the designer before proceeding.

REVISIONS

Rev	Date	Description
C02	07.10.2026	Canopy to client sketch: 8.00x3.44, u/s 2.36, fascia 0.43
C01	06.10.2026	Issued for construction / tender
P01	05.10.2026	Concept (client renders)

PREVIEW FOR CLIENT REVIEW — per client sketch, mark-up & site photo; not for construction

DRAWING TITLE

VERSION 2 — 0.90 m VOID + 2 STEEL RODS — top view & roof plan

SCALE @ A3

1:50 / 1:25

DRAWN / CHECKED

CC / —

DATE

07.10.2026

SERIES

ARCHITECTURAL


DRAWING No.

V2-01


REV

C04

VERSION 2 — 0.90 m VOID + 2 STEEL RODS

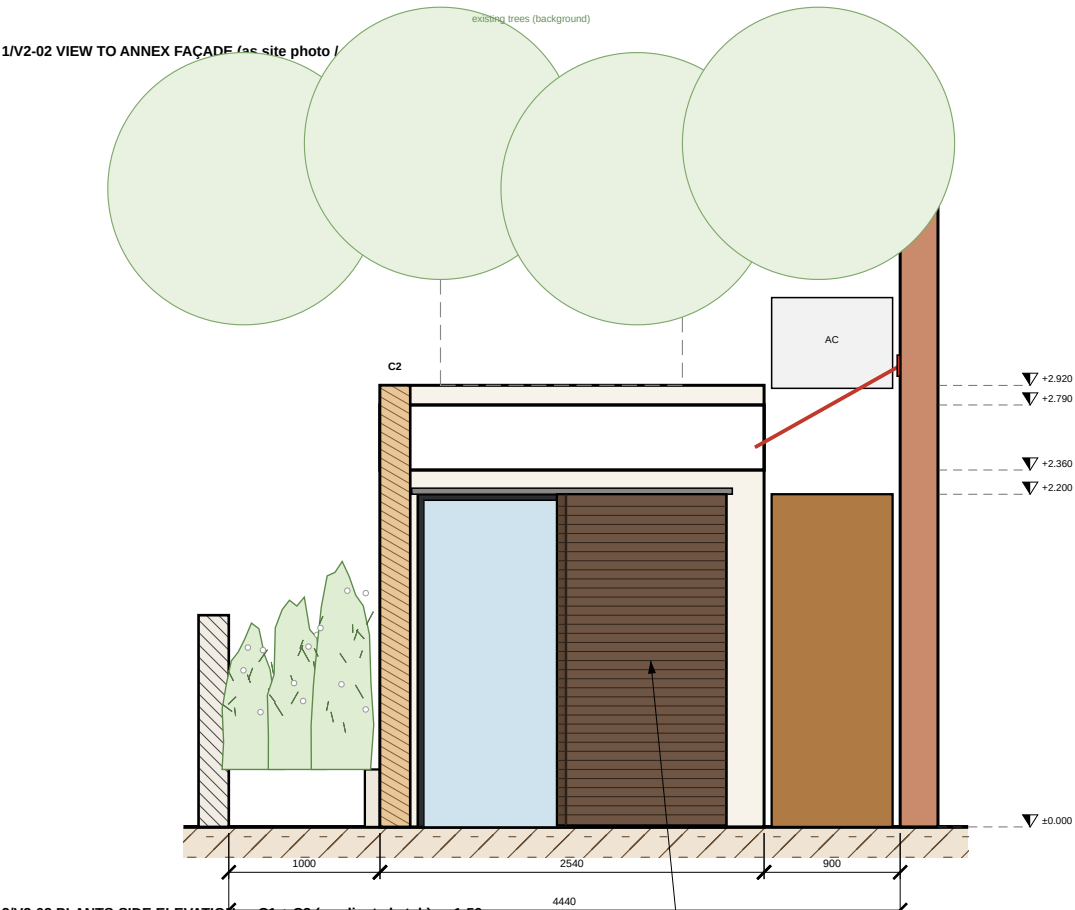


2/V2-02 PLANTS-SIDE ELEVATION — C1 + C2 (as client sketch) — 1:50

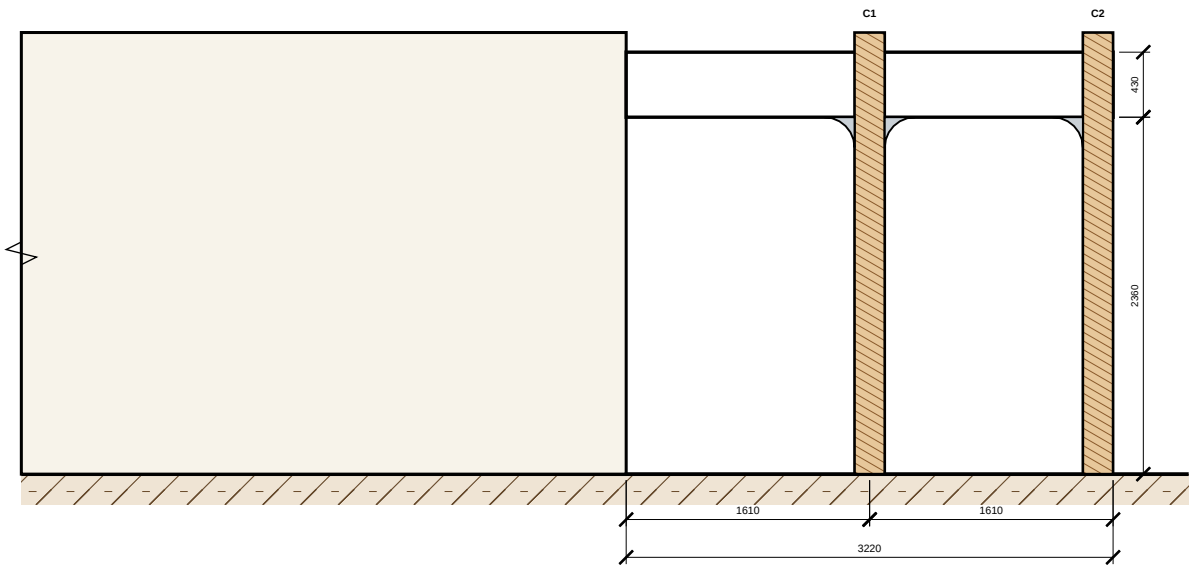


3/V2-02 SECTION ACROSS AT C1 — 1:50 (see V2-03)

tall wall left — plants right (as client sketch)

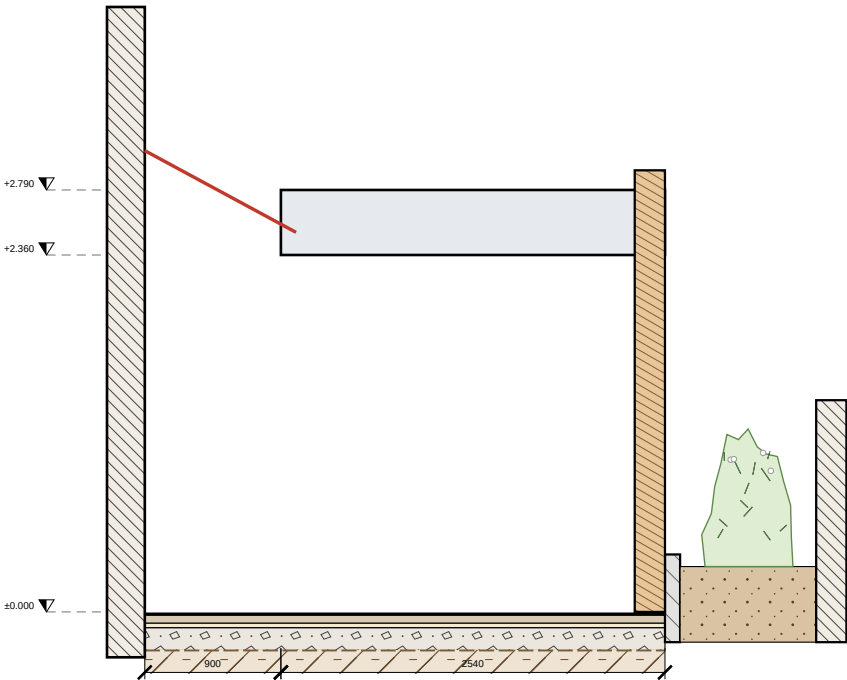

NOTES
roof 3.22 x 2.54; 0.90 m void left open; void edge tied to the tall wall with 2 slim Ø16 stainless rods (rising = 30°, almost horizontal); 2 columns on the plants side.
Underside +2.36, fascia 0.43 (top +2.79); columns 0.13 above roof.
Trees are existing, behind the low boundary wall and the annex (background).
Refined roof section & details: sheet V2-03.

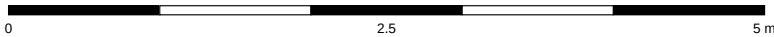

COURTYARD ROOF — V2

VERSION 2 — 0.90 m VOID + 2 STEEL RODS: roof 3.22 x 2.54; 0.90 m void left open; void edge tied to the tall wall with 2 slim Ø16 stainless rods (rising ≈ 30°, almost horizontal); 2 columns on the plants side
Client: Owner / Client
Design & drawings: Claude Code

- DRAWING NOTES**
- Do not scale from this drawing. Use figured dimensions only.
 - All dimensions in millimetres; levels in metres relative to internal FFL ±0.000 (datum to be tied to site survey).
 - Contractor to verify all dimensions, levels & existing structure on site before fabrication or ordering.
 - Read with all other architectural, structural & services drawings and the specification notes (A-001).
 - Structural members are preliminary: final design, connections & calculations by a licensed structural engineer to local code before construction.
 - Report any discrepancy to the designer before proceeding.

REVISIONS		
Rev	Date	Description
C02	07.10.2026	Canopy to client sketch: 8.00x3.44, u/s 2.36, fascia 0.43
C01	06.10.2026	Issued for construction / tender
P01	05.10.2026	Concept (client renders)

PREVIEW FOR CLIENT REVIEW — per client sketch, mark-up & site photo; not for construction

DRAWING TITLE

VERSION 2 — 0.90 m VOID + 2 STEEL RODS — view as photo, plants-side elevation & section

SCALE @ A3	DATE
1:50 / 1:25	07.10.2026
DRAWN / CHECKED	SERIES
CC / —	ARCHITECTURAL


DRAWING No. REV

V2-02 **C04**


VERSION 2 — 0.90 m VOID + 2 STEEL RODS

1/2-03 ROOF SECTION ACROSS AT C1 — 1:25


(as client sketch B: roof stops, rods to the wall)

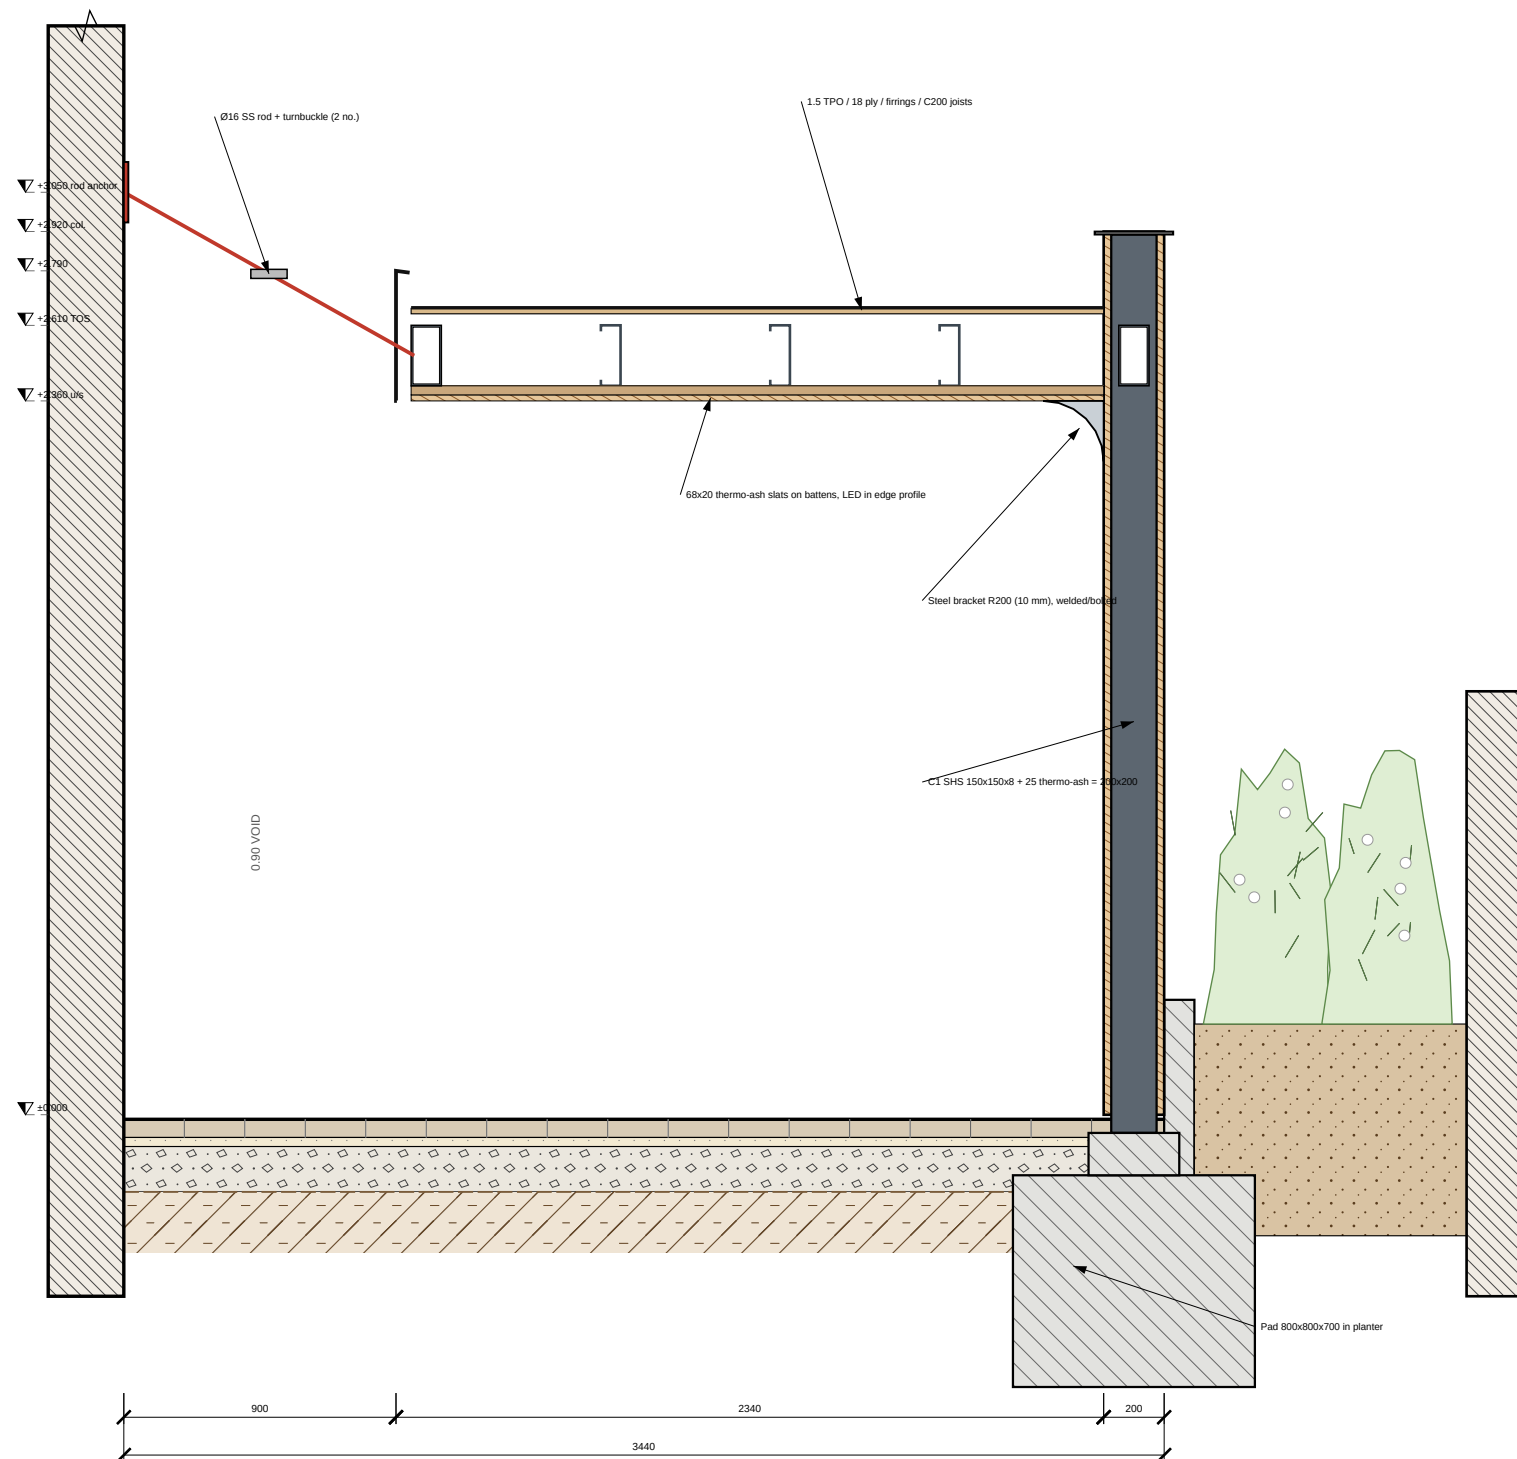

D1 ROD TO WALL (client sketch B) — 1:15

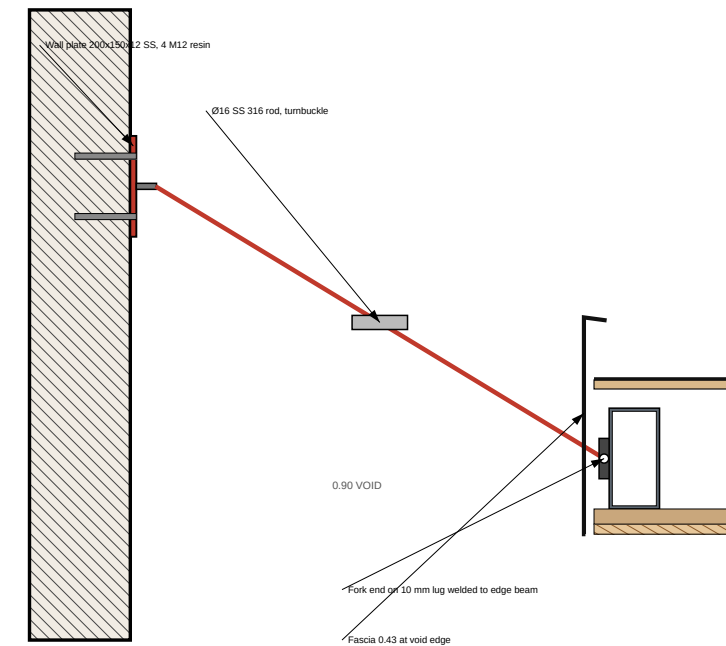

D2 COLUMN / ROOF JUNCTION (plants side) — 1:10

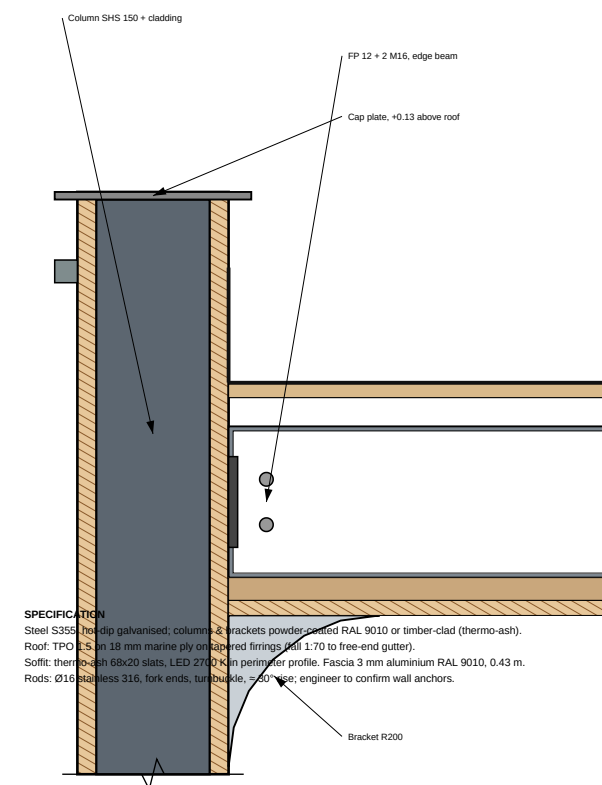

SPECIFICATION

Steel S355, hot dip galvanised; columns & brackets powder-coated RAL 9010 or timber-clad (thermo-ash).
Roof: TPO 1.5 on 18 mm marine ply on tapered firings (fall 1:70 to free-end gutter).
Soffit: timber-ash 68x20 slats, LED 2700 K pin perimeter profile. Fascia 316 mm aluminium RAL 9010, 0.43 m.
Rods: Ø16 stainless 316, fork ends, turnbuckle, $\approx 50^\circ$ rise; engineer to confirm wall anchors.



COURTYARD ROOF — V2

VERSION 2 — 0.90 m VOID + 2 STEEL RODS: roof 3.22 x 2.54; 0.90 m void left open; void edge tied to the tall wall with 2 slim Ø16 stainless rods (rising = 30°, almost horizontal); 2 columns on the plants side
Client: Owner / Client
Design & drawings: Claude Code

DRAWING NOTES

1. Do not scale from this drawing. Use figured dimensions only.
2. All dimensions in millimetres; levels in metres relative to internal FFL ± 0.000 (datum to be tied to site survey).
3. Contractor to verify all dimensions, levels & existing structure on site before fabrication or ordering.
4. Read with all other architectural, structural & services drawings and the specification notes (A-001).
5. Structural members are preliminary: final design, connections & calculations by a licensed structural engineer to local code before construction.
6. Report any discrepancy to the designer before proceeding.

REVISIONS

Rev	Date	Description
C02	07.10.2026	Canopy to client sketch: 8.00x3.44, u/s 2.36, fascia 0.43
C01	06.10.2026	Issued for construction / tender
P01	05.10.2026	Concept (client renders)

PREVIEW FOR CLIENT REVIEW — per client sketch, mark-up & site photo; not for construction

DRAWING TITLE

**VERSION 2 — 0.90 m VOID + 2 STEEL RODS —
roof section & construction details**

SCALE @ A3	DATE
1:25 / 1:10	07.10.2026
DRAWN / CHECKED	SERIES
CC / —	ARCHITECTURAL

DRAWING No.

EV

V2-03

C04