


OPTION C2 — TRIANGLE TO THE WALL, TIP AT THE AC LINE: plants edge 3.06


TALL HOUSE WALL (exist., AC units)

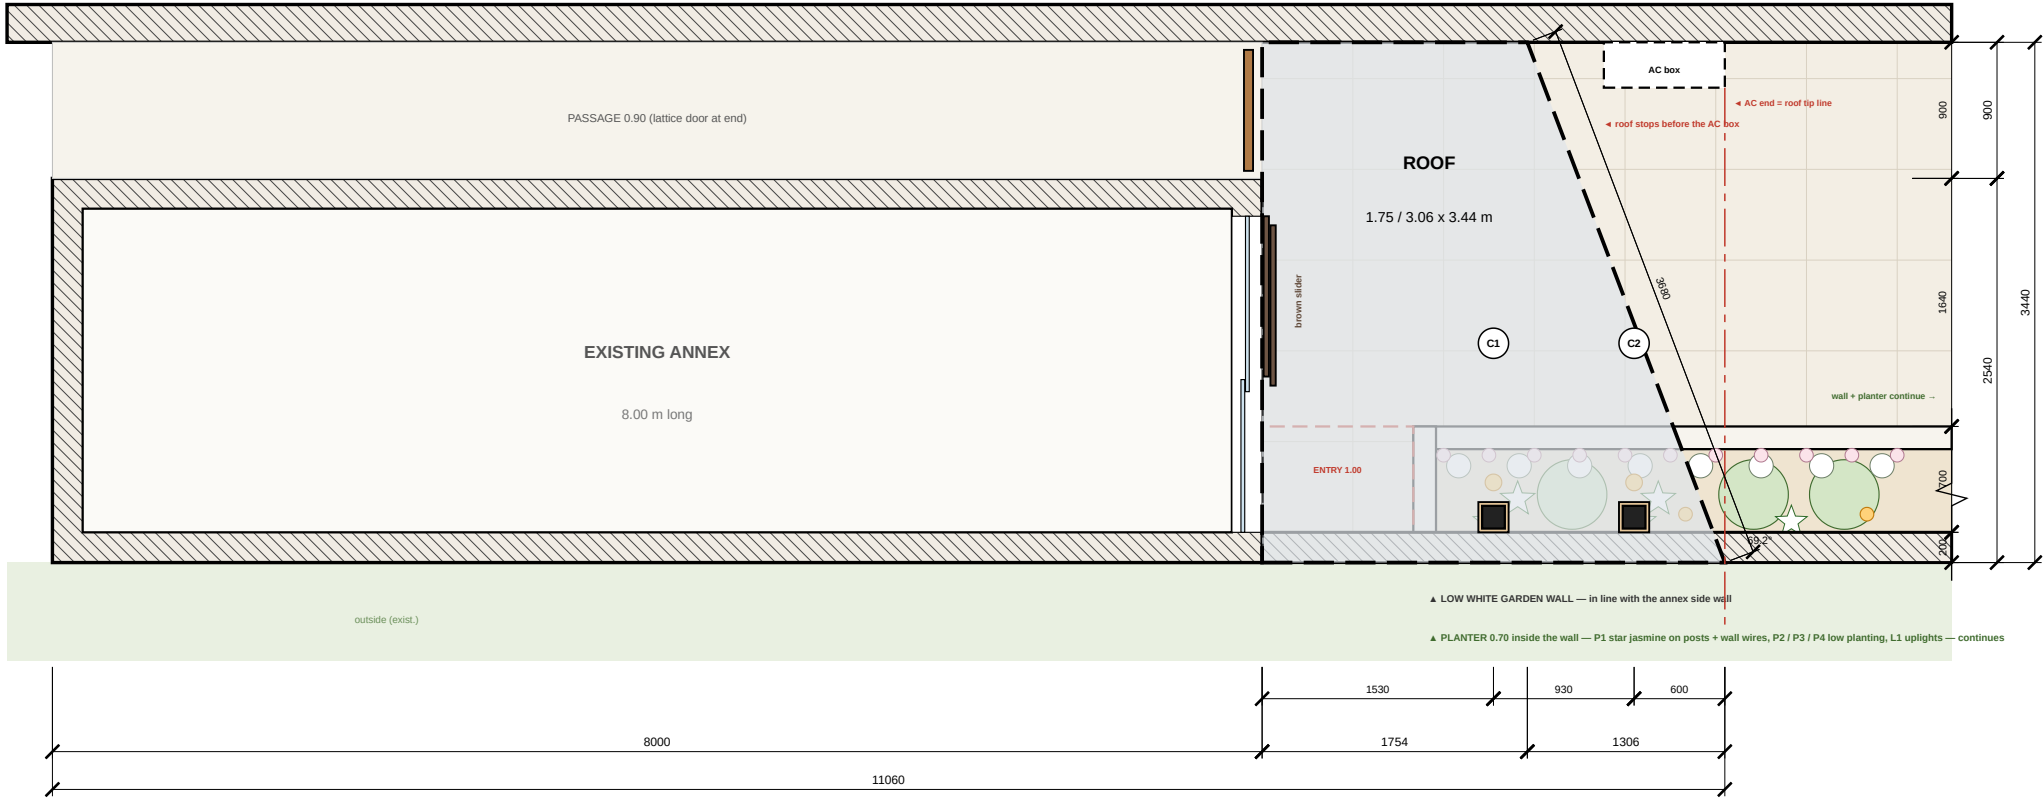

1 TOP VIEW — ANNEX, GARDEN & ROOF
V1T-01

1:50 @ A3 — annex + garden wall in one line; planter 0.70 continues; entry 1.00 at the door

2/V1T-01 ROOF FRAMING PLAN — 1:30

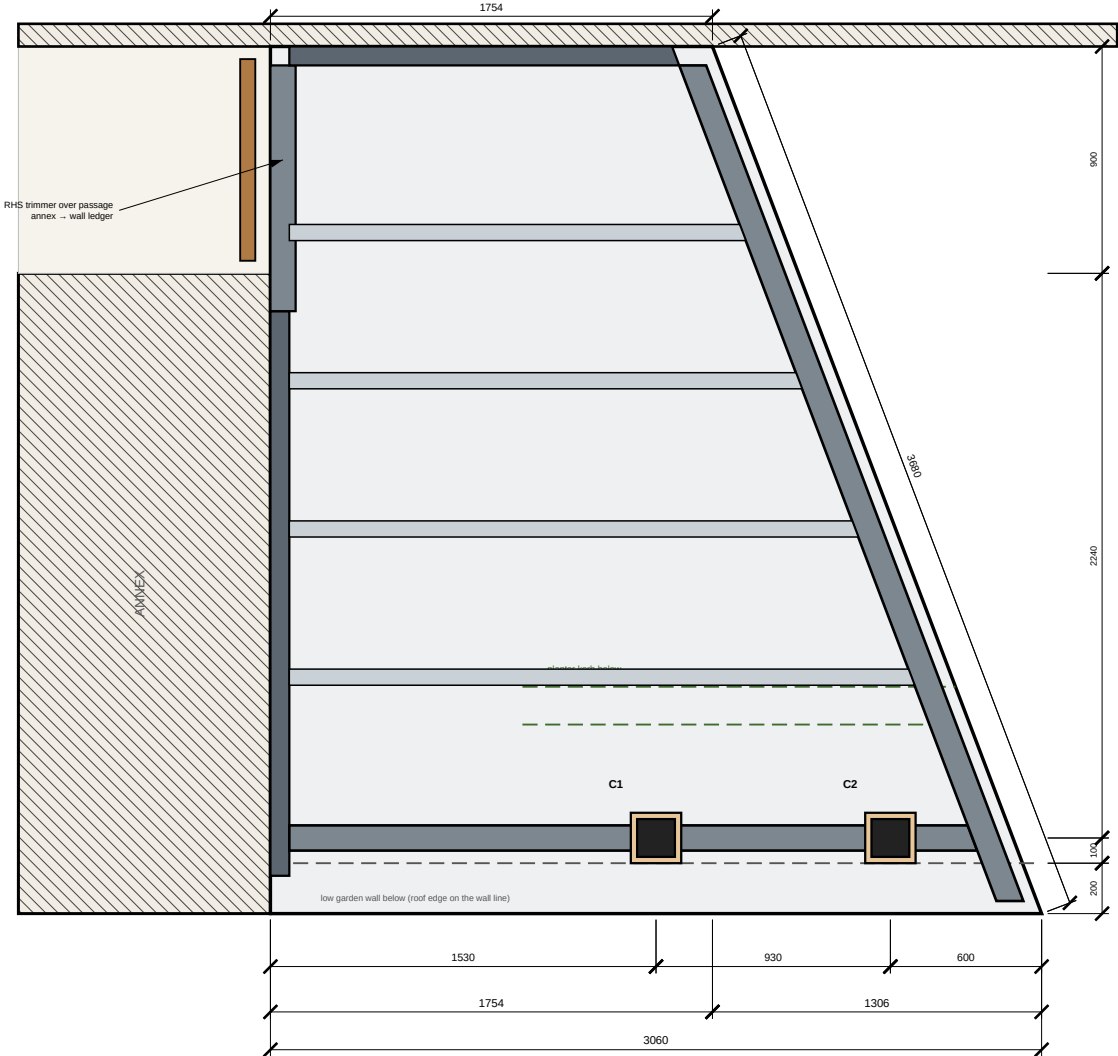


THIS VERSION

roof to the tall wall, no void; plants edge 3.06 ending in line with the end of the AC box; edge at the tall wall 1.75 (kept); new raked angle; bears on the annex ledger + a ledger on the tall wall; 2 columns against the garden wall on a shorter edge beam.
Roof fixed to the annex end façade AND to the tall house wall (steel ledgers, resin anchors); covers the passage in front of the lattice door (RHS trimmer over the passage, annex — wall ledger).
Triangle to the tall wall: plants edge 3.06 m — tip in line with the end of the AC box; edge at the tall wall 1.75 m (unchanged); edge at the annex line 2.10 m; raked edge 3.68 m at 69.2° to the plants edge.
C1 in the middle of the 3.06 edge (1.53 from the façade); C2 0.60 m in from the tip (the tip cantilevers 0.60).
Joists run from the annex ledger to the raked edge beam (max. span = 3.2 m); over the passage they bear on the RHS trimmer + wall ledger.

COMMON

Annex side wall and low white garden wall are ONE line; the roof's plants edge (fascia) is on it.
Planter 0.70 inside the wall (soil + white kerb), continues along the wall; paved entry space 1.00 between the façade and the planter (walk in to the left glass door).
Entrance opening runs to the side wall (no pier).
C1 / C2: SHS 150 clad 200x200 thermo-ash, against the garden wall, 2 SS brackets each into the wall; edge beam on the column line, roof cantilevers 0.30 to the fascia over the wall.
Underside +2.36, fascia 0.43 (top +2.79); columns 0.13 above roof. Falls 1.70 to the box gutter on the raked edge; rainwater down C2.

3/V1T-01 3D — BIRD'S EYE (from outside, over the low garden wall)

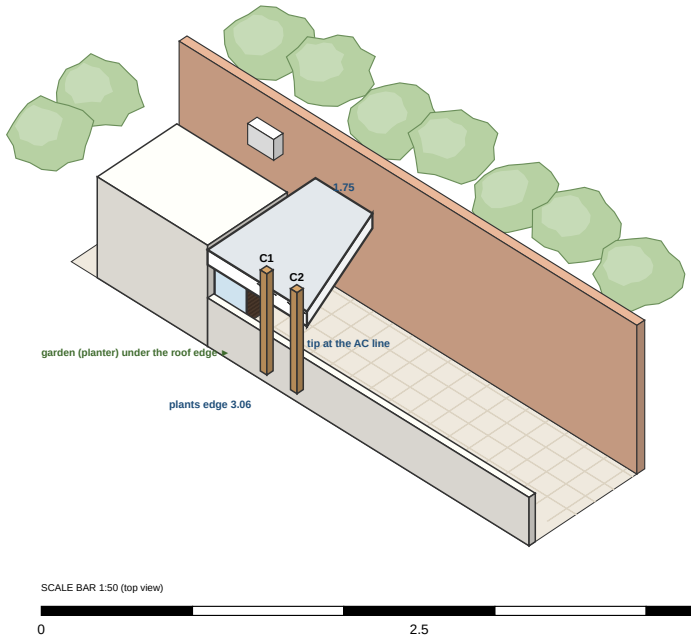

COURTYARD ROOF — V1T

OPTION C2 — TRIANGLE TO THE WALL, TIP AT THE AC LINE: plants edge 3.06; roof to the tall wall, no void; plants edge 3.06 ending in line with the end of the AC box; edge at the tall wall 1.75 (kept); new raked angle; bears on the annex ledger + a ledger on the tall wall; 2 columns against the garden wall on a shorter edge beam
Client: Owner / Client
Design & drawings: Claude Code

DRAWING NOTES

- Do not scale from this drawing. Use figured dimensions only.
- All dimensions in millimetres; levels in metres relative to internal FFL ±0.000 (datum to be tied to site survey).
- Contractor to verify all dimensions, levels & existing structure on site before fabrication or ordering.
- Read with all other architectural, structural & services drawings and the specification notes (A-001).
- Structural members are preliminary: final design, connections & calculations by a licensed structural engineer to local code before construction.
- Report any discrepancy to the designer before proceeding.

REVISIONS

Rev	Date	Description
C17	08.10.2026	Option C2: tip at the AC line, wall edge kept, angle + edge beam adjusted
C16	08.10.2026	Roof supported by the tall wall, no void: C triangle / D rectangle 2.20
C15	08.10.2026	Void edge max 2.20 (before the AC box): A triangle same angle / B rectangle 2.20

FOR CLIENT CHECK — option C revised: roof tip ends at the AC line; edge at the tall wall unchanged

DRAWING TITLE

OPTION C2 — TIP AT AC LINE
top view & roof framing

SCALE @ A3 1:50 / 1:30	DATE 08.10.2026
DRAWN / CHECKED CC / —	SERIES ARCHITECTURAL

DRAWING No. REV

C17-C2 C17