



VERSION 1T — TRIANGLE, ROOF TO THE WALL

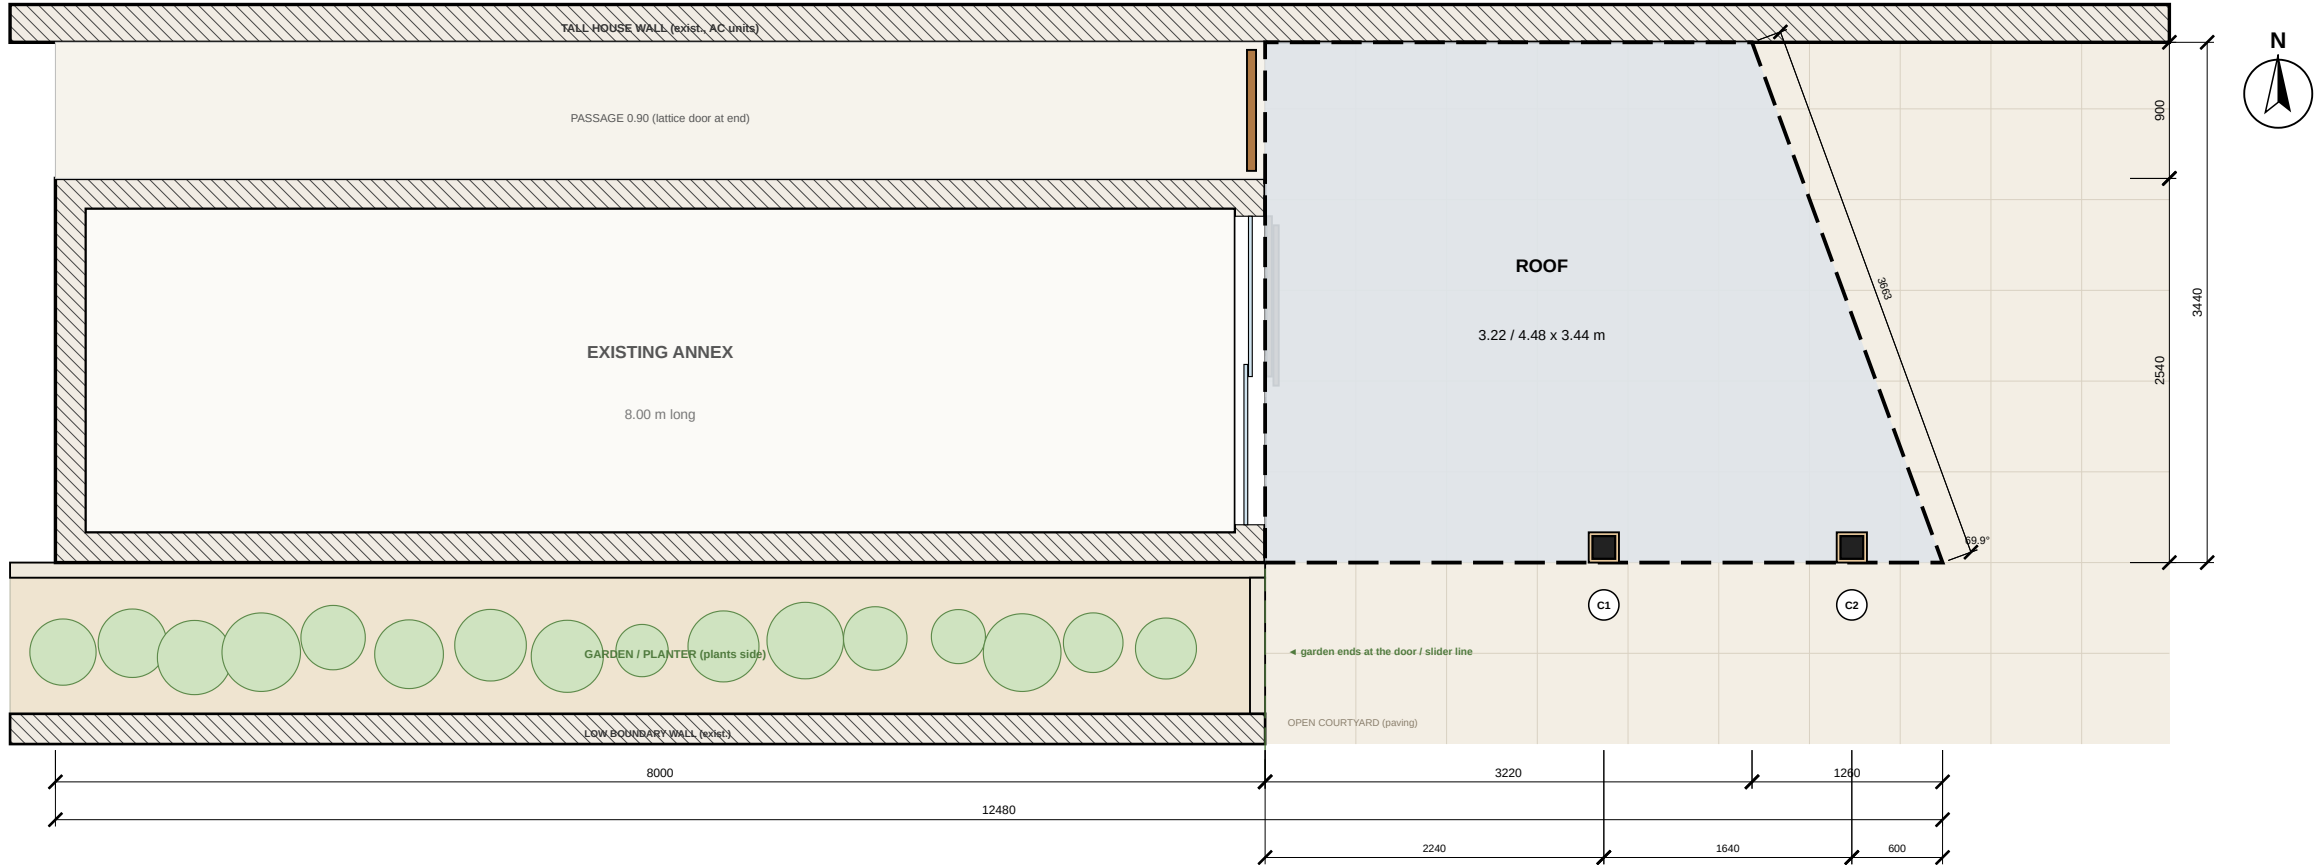

1 TOP VIEW — ANNEX, GARDEN & ROOF
V1T-01
1:50 @ A3 garden ends at the door line; trees = background

2/V1T-01 ROOF FRAMING PLAN — 1:30

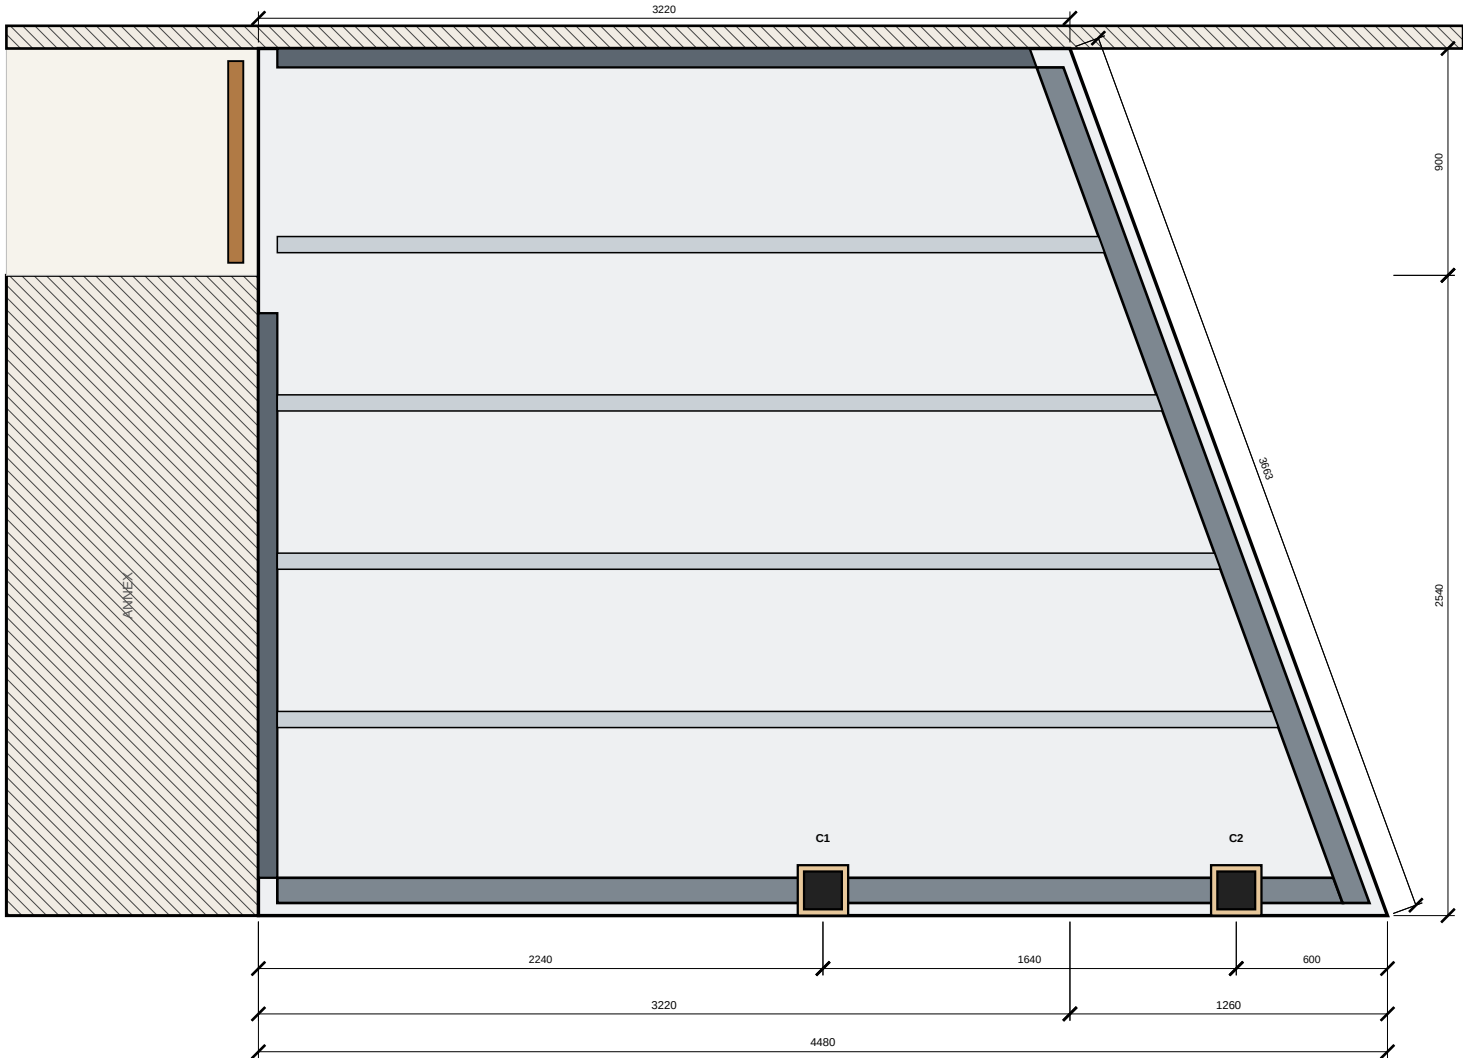

THIS VERSION
triangular roof: plants edge 3.22 + 1.26 = 4.48, wall edge 3.22, raked edge 3.66; runs to the tall wall (ledger + brackets); 2 columns on the plants side.
Roof fixed to the annex end façade AND to the tall house wall (steel ledgers, resin anchors); covers the passage in front of the lattice door.
Triangle: plants edge 3.22 + 1.26 = 4.48 m; raked edge 3.66 m at 69.9° to the plants edge.
C1 in the middle of the 4.48 edge (2.24 from the façade); C2 0.60 m in from the tip (the tip cantilevers 0.60).
Joists run from the annex ledger to the raked edge beam (max. span = 4.2 m).

COMMON
Roof 3.22 m from the annex façade along the top edge. Underside +2.36, fascia 0.43 (top +2.79); columns 200x200, 0.13 above roof, curved bracket under the junction (client section).
Garden & low wall stop at the annex end façade (door / slider line); beyond it open paving.
Falls 1:70 to the concealed gutter at the free edge; rainwater down C2.



COURTYARD ROOF — V1T

VERSION 1T — TRIANGLE, ROOF TO THE WALL: triangular roof: plants edge 3.22 + 1.26 = 4.48, wall edge 3.22, raked edge 3.66; runs to the tall wall (ledger + brackets); 2 columns on the plants side
Client: Owner / Client
Design & drawings: Claude Code

- DRAWING NOTES**
- Do not scale from this drawing. Use figured dimensions only.
 - All dimensions in millimetres; levels in metres relative to internal FFL ±0.000 (datum to be tied to site survey).
 - Contractor to verify all dimensions, levels & existing structure on site before fabrication or ordering.
 - Read with all other architectural, structural & services drawings and the specification notes (A-001).
 - Structural members are preliminary: final design, connections & calculations by a licensed structural engineer to local code before construction.
 - Report any discrepancy to the designer before proceeding.

REVISIONS		
Rev	Date	Description
C05	07.10.2026	Garden ends at door/slider line; triangular versions V1T/V2T; 3D views
C04	07.10.2026	Two versions V1/V2 per client sections & site photo
C02	07.10.2026	Canopy to client sketch: 8.00 house, roof 3.22, u/s 2.36, fascia 0.43


PREVIEW FOR CLIENT REVIEW — per client sketch, mark-ups & site photo; not for construction

DRAWING TITLE	
V1T TRIANGLE TO WALL top view & roof framing	
SCALE @ A3 1:50 / 1:30	DATE 07.10.2026
DRAWN / CHECKED CC / —	SERIES ARCHITECTURAL
DRAWING No.	REV


V1T-01 C05

VERSION 1T — TRIANGLE, ROOF TO THE WALL

1/V1T-02 VIEW TO ANNEX FAÇADE (as site photo) — 1:50

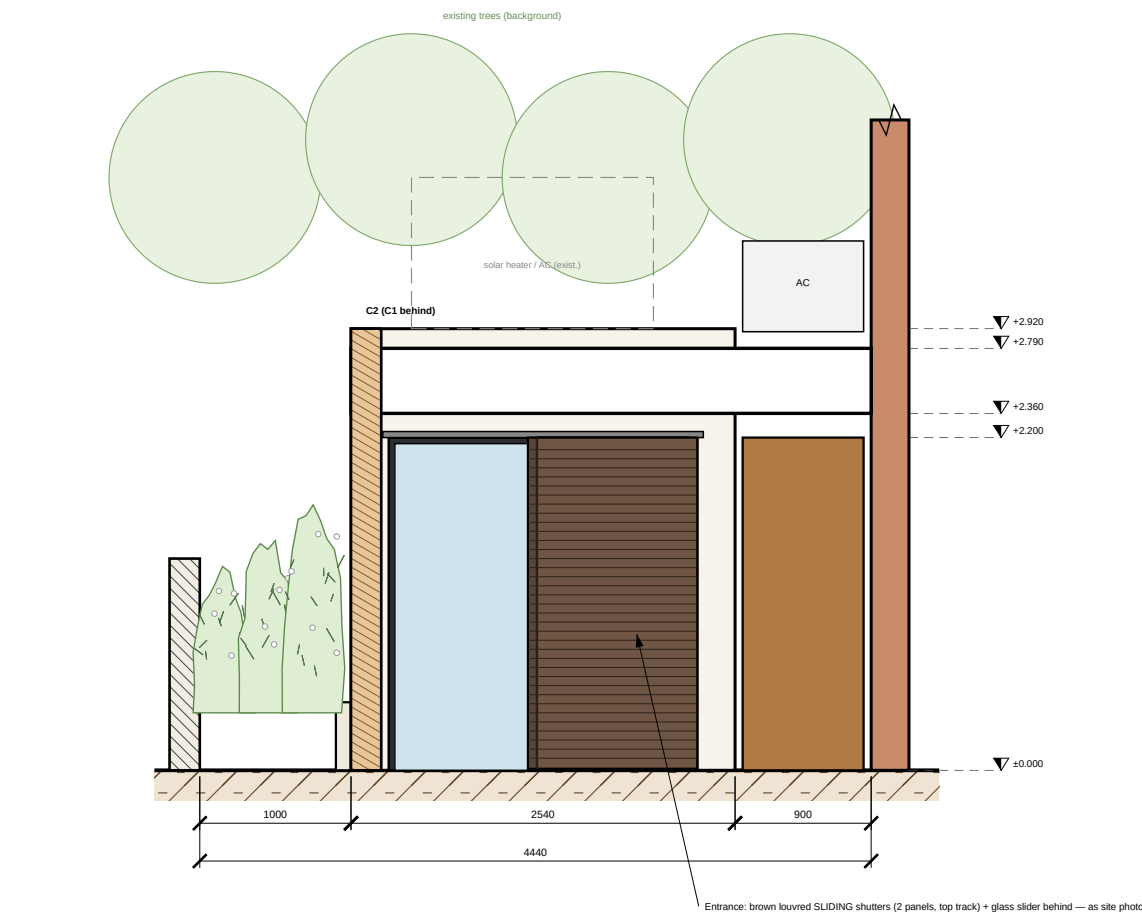


2/V1T-02 PLANTS-SIDE ELEVATION — C1 + C2 — 1:50 (plants edge 3.22 + 1.26 = 4.48)

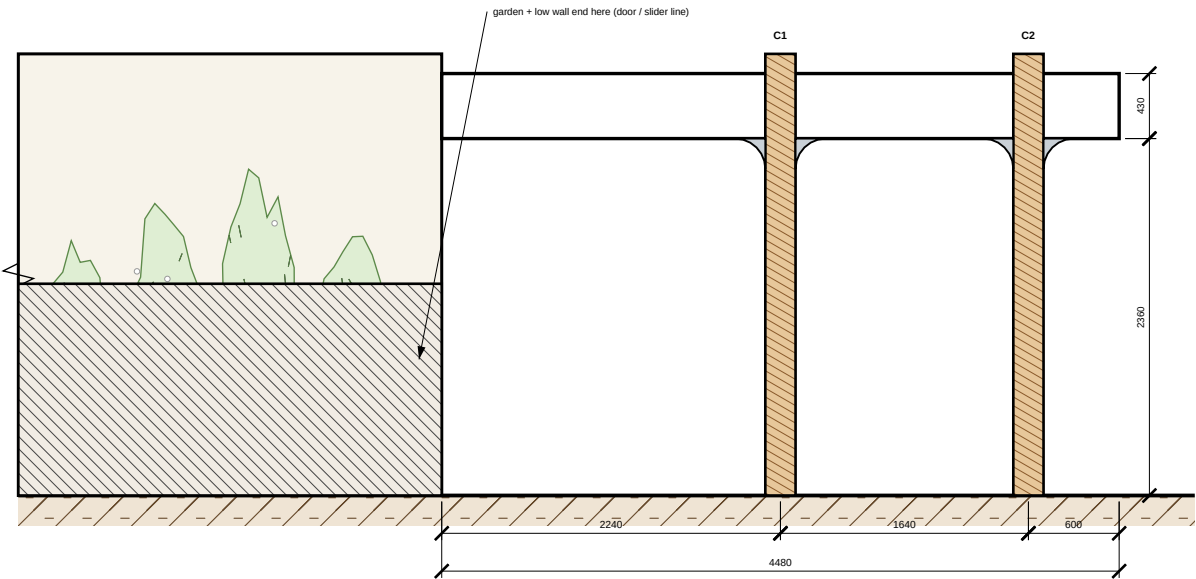


NOTES
triangular roof: plants edge 3.22 + 1.26 = 4.48, wall edge 3.22, raked edge 3.66; runs to the tall wall (ledger + brackets); 2 columns on the plants side.
Underside +2.36, fascia 0.43 (top +2.79); columns 0.13 above roof.
Garden + low wall end at the annex end façade (door / slider line). Trees are existing, in the background.
Refined roof section & details: sheet V1T-03.

3/V1T-02 SECTION ACROSS AT C1 — 1:50 (refined: V1T-03)

tall wall left — plants side right

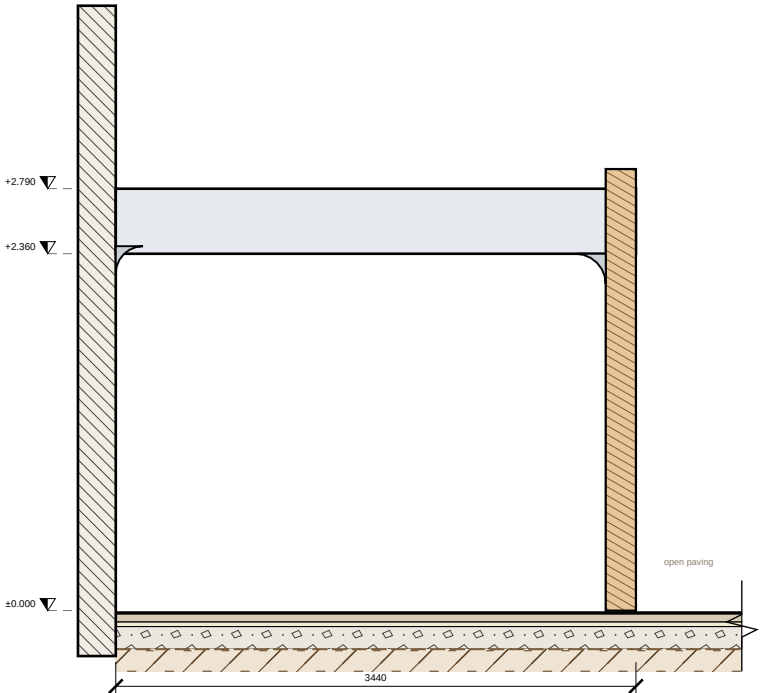

4/V1T-02 3D VIEW — from the plants side (courtyard)

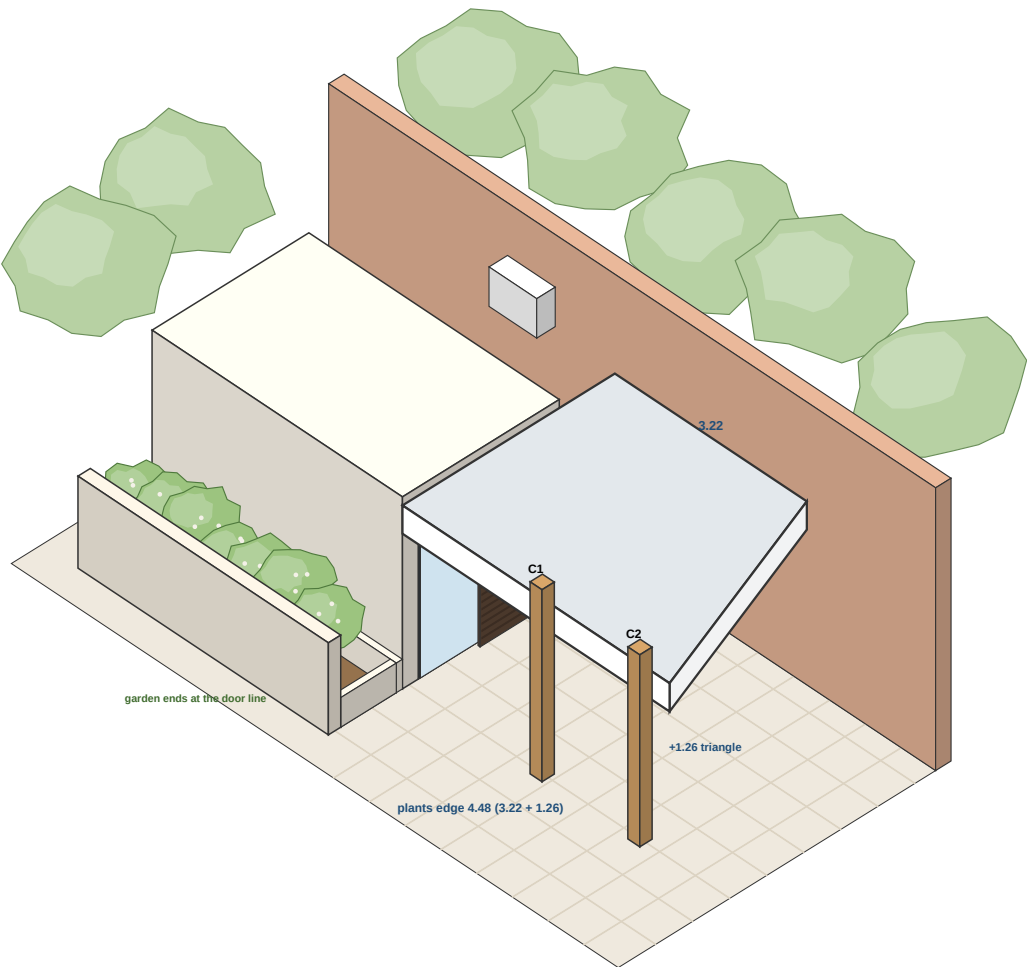

COURTYARD ROOF — V1T

VERSION 1T — TRIANGLE, ROOF TO THE WALL: triangular roof: plants edge 3.22 + 1.26 = 4.48, wall edge 3.22, raked edge 3.66; runs to the tall wall (ledger + brackets); 2 columns on the plants side
Client: Owner / Client
Design & drawings: Claude Code

DRAWING NOTES

- Do not scale from this drawing. Use figured dimensions only.
- All dimensions in millimetres; levels in metres relative to internal FFL ±0.000 (datum to be tied to site survey).
- Contractor to verify all dimensions, levels & existing structure on site before fabrication or ordering.
- Read with all other architectural, structural & services drawings and the specification notes (A-001).
- Structural members are preliminary: final design, connections & calculations by a licensed structural engineer to local code before construction.
- Report any discrepancy to the designer before proceeding.

REVISIONS

Rev	Date	Description
C05	07.10.2026	Garden ends at door/slider line; triangular versions V1T/V2T; 3D views
C04	07.10.2026	Two versions V1/V2 per client sections & site photo
C02	07.10.2026	Canopy to client sketch: 8.00 house, roof 3.22, u/s 2.36, fascia 0.43

PREVIEW FOR CLIENT REVIEW — per client sketch, mark-ups & site photo; not for construction

DRAWING TITLE

V1T TRIANGLE TO WALL
views, section & 3D view

SCALE @ A3 1:50	DATE 07.10.2026
DRAWN / CHECKED CC / —	SERIES ARCHITECTURAL

DRAWING No. REV


V1T-02

C05


VERSION 1T — TRIANGLE, ROOF TO THE WALL

1/V1T-03 ROOF SECTION ACROSS AT C1 — 1:25


(as client sketch A: roof runs to the wall)

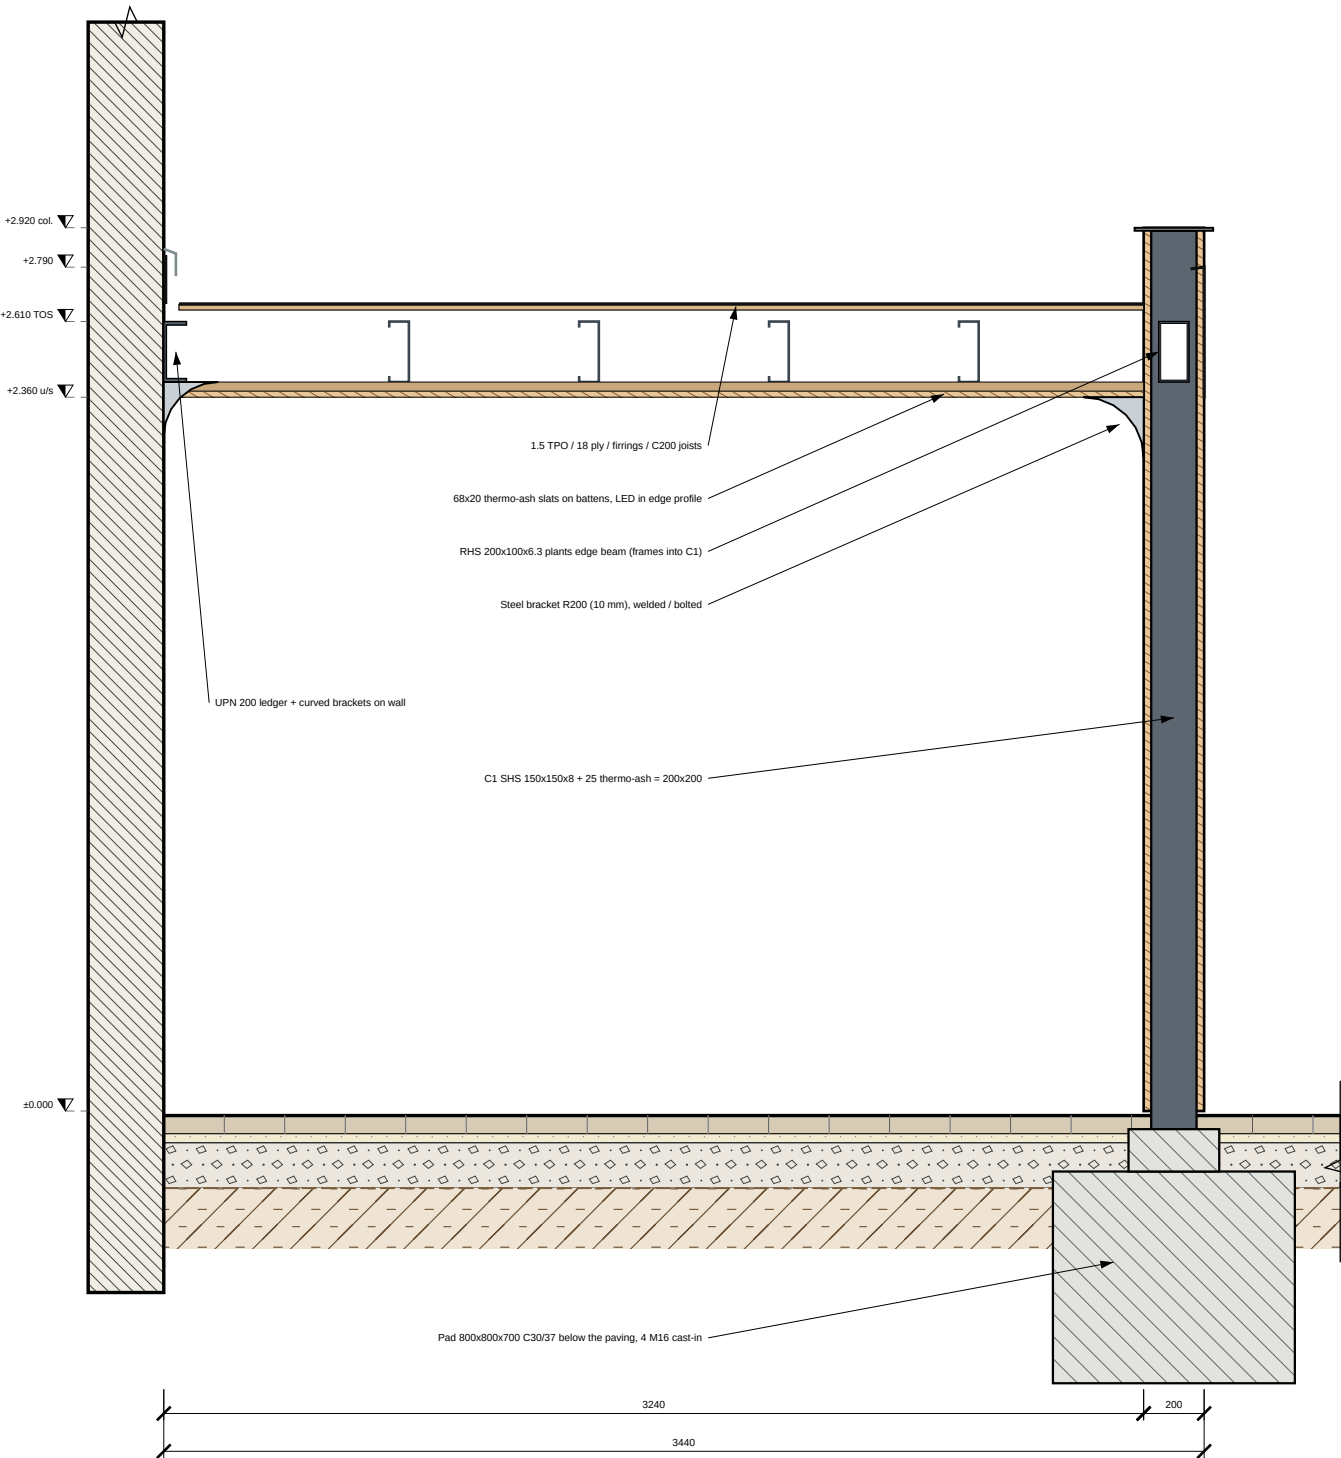


SPECIFICATION
Steel S355, hot-dip galvanised; columns & brackets powder-coated RAL 9010 or timber-clad (thermo-ash).
Roof: TPO 1.5 on 18 mm marine ply on tapered firrings (fall 1:70 to the free-edge box gutter).
Soffit: thermo-ash 68x20 slats, LED 2700 K in perimeter profile. Fascia 3 mm aluminium RAL 9010, 0.43 m.
Wall ledger & brackets into sound masonry/RC — engineer to confirm anchors.

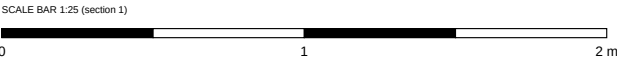


D1 ROOF TO WALL (client sketch A) — 1:15

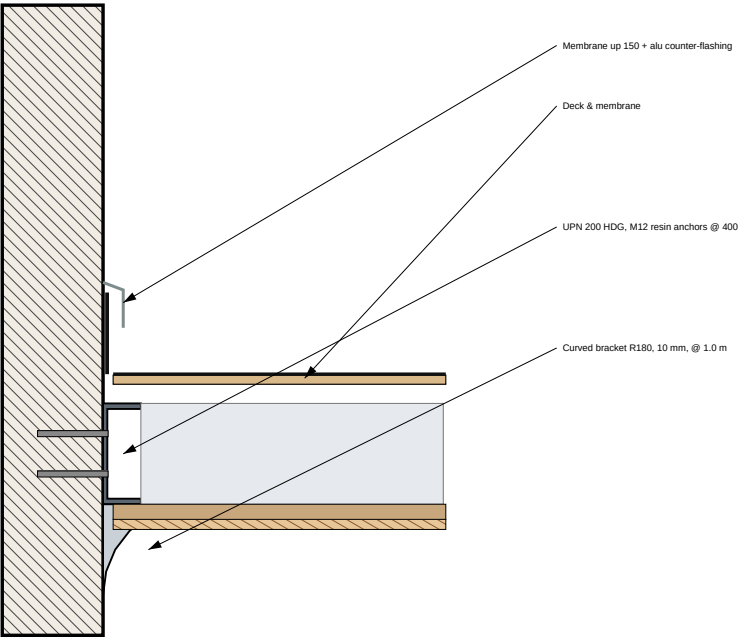

D2 COLUMN / ROOF JUNCTION (plants side) — 1:15

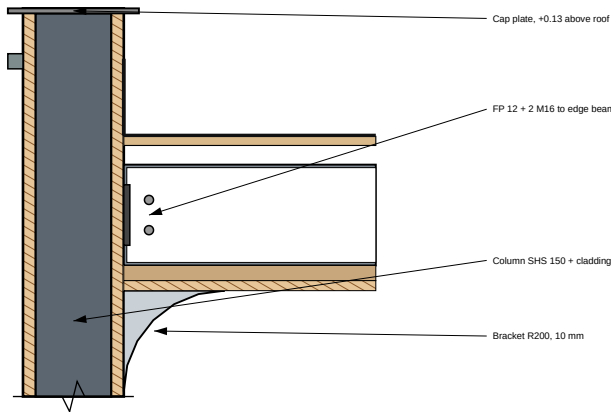

D3 TIP AT C2 (triangle) — PLAN 1:15

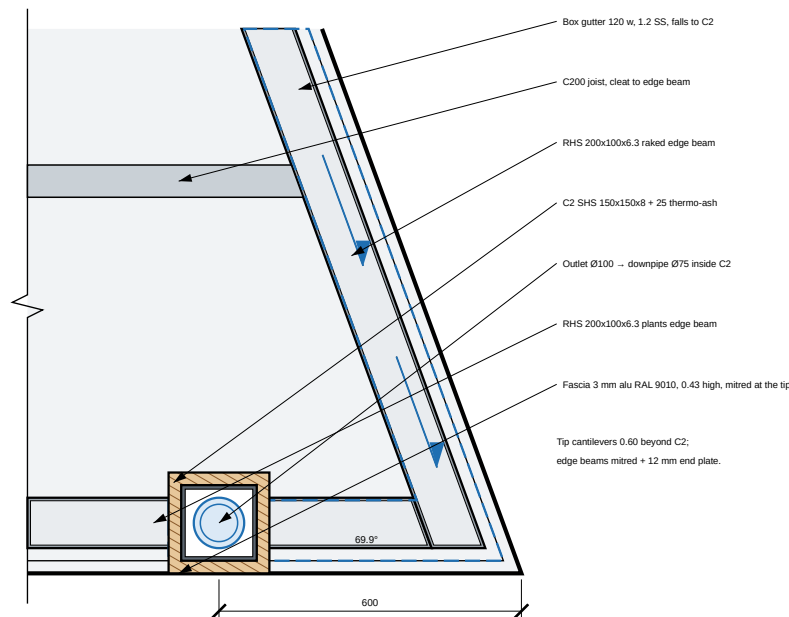

COURTYARD ROOF — V1T

VERSION 1T — TRIANGLE, ROOF TO THE WALL: triangular roof; plants edge 3.22 + 1.26 = 4.48, wall edge 3.22, raked edge 3.66; runs to the tall wall (ledger + brackets); 2 columns on the plants side
Client: Owner / Client
Design & drawings: Claude Code

DRAWING NOTES

- Do not scale from this drawing. Use figured dimensions only.
- All dimensions in millimetres; levels in metres relative to internal FFL ±0.000 (datum to be tied to site survey).
- Contractor to verify all dimensions, levels & existing structure on site before fabrication or ordering.
- Read with all other architectural, structural & services drawings and the specification notes (A-001).
- Structural members are preliminary: final design, connections & calculations by a licensed structural engineer to local code before construction.
- Report any discrepancy to the designer before proceeding.

REVISIONS

Rev	Date	Description
C05	07.10.2026	Garden ends at door/slider line; triangular versions V1T/V2T; 3D views
C04	07.10.2026	Two versions V1/V2 per client sections & site photo
C02	07.10.2026	Canopy to client sketch: 8.00 house, roof 3.22, u/s 2.36, fascia 0.43

PREVIEW FOR CLIENT REVIEW — per client sketch, mark-ups & site photo; not for construction

DRAWING TITLE

V1T TRIANGLE TO WALL
roof section & details

SCALE @ A3

1:25 / 1:15 / 1:20

DRAWN / CHECKED

CC / —

DRAWING No.

V1T-03

DATE

07.10.2026


SERIES

ARCHITECTURAL

REV


C05

VERSION 2T — TRIANGLE, 0.90 m VOID + 2 RODS

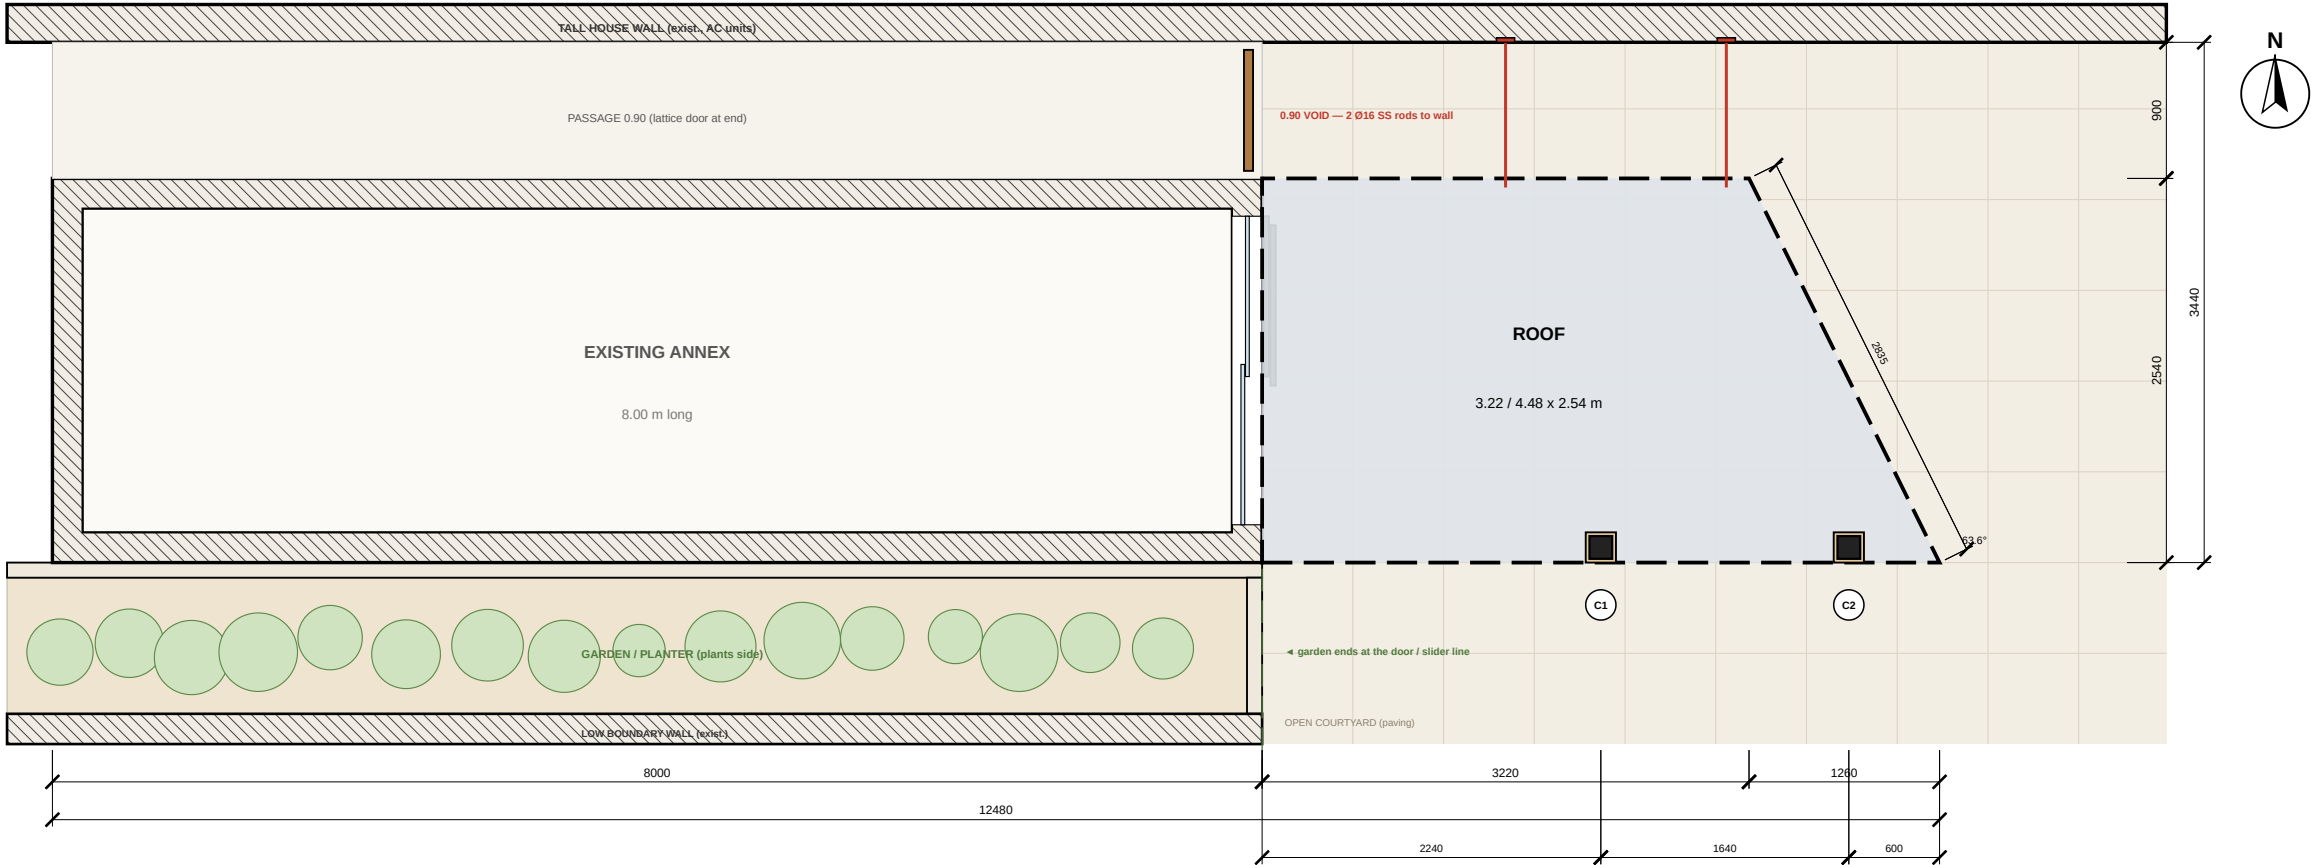

1 TOP VIEW — ANNEX, GARDEN & ROOF
V2T-01 1:50 @ A3 garden ends at the door line; trees = background

2/V2T-01 ROOF FRAMING PLAN — 1:30

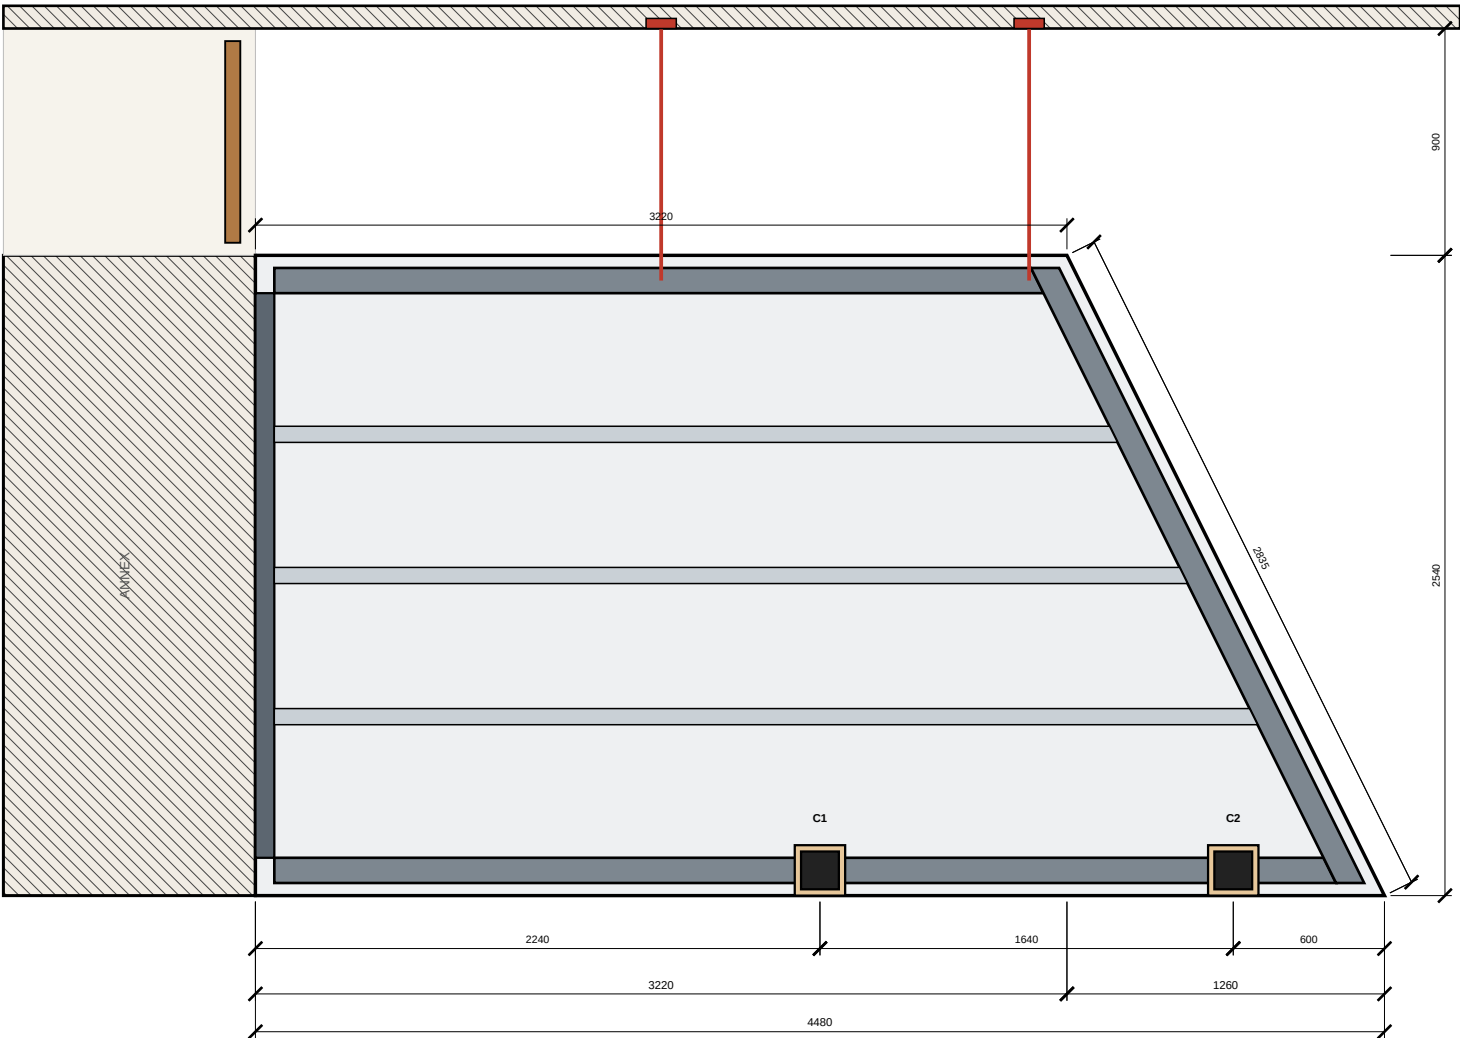

THIS VERSION
triangular roof: plants edge 3.22 + 1.26 = 4.48, void edge 3.22, raked edge 2.84; 0.90 m void open, 2 Ø16 stainless rods to the wall; 2 columns on the plants side.
Roof fixed to the annex end façade (ledger). The 0.90 m passage to the lattice door stays open.
Void edge hung from the tall house wall on 2 Ø16 stainless rods (turnbuckles, wall plates) — slim, almost invisible.
Triangle: plants edge 3.22 + 1.26 = 4.48 m; raked edge 2.84 m at 63.6° to the plants edge.
C1 in the middle of the 4.48 edge (2.24 from the façade); C2 0.60 m in from the tip (the tip cantilevers 0.60).
Joists run from the annex ledger to the raked edge beam (max. span = 4.2 m).
COMMON
Roof 3.22 m from the annex façade along the top edge. Underside +2.36, fascia 0.43 (top +2.79); columns 200x200, 0.13 above roof, curved bracket under the junction (client section).
Garden & low wall stop at the annex end façade (door / slider line); beyond it open paving.
Falls 1:70 to the concealed gutter at the free edge; rainwater down C2.



COURTYARD ROOF — V2T

VERSION 2T — TRIANGLE, 0.90 m VOID + 2 RODS: triangular roof: plants edge 3.22 + 1.26 = 4.48, void edge 3.22, raked edge 2.84; 0.90 m void open, 2 Ø16 stainless rods to the wall; 2 columns on the plants side
Client: Owner / Client
Design & drawings: Claude Code

- DRAWING NOTES**
- Do not scale from this drawing. Use figured dimensions only.
 - All dimensions in millimetres; levels in metres relative to internal FFL ±0.000 (datum to be tied to site survey).
 - Contractor to verify all dimensions, levels & existing structure on site before fabrication or ordering.
 - Read with all other architectural, structural & services drawings and the specification notes (A-001).
 - Structural members are preliminary: final design, connections & calculations by a licensed structural engineer to local code before construction.
 - Report any discrepancy to the designer before proceeding.

REVISIONS		
Rev	Date	Description
C05	07.10.2026	Garden ends at door/slider line; triangular versions V1T/V2T; 3D views
C04	07.10.2026	Two versions V1/V2 per client sections & site photo
C02	07.10.2026	Canopy to client sketch: 8.00 house, roof 3.22, u/s 2.36, fascia 0.43


PREVIEW FOR CLIENT REVIEW — per client sketch, mark-ups & site photo; not for construction

DRAWING TITLE	
V2T TRIANGLE + RODS top view & roof framing	
SCALE @ A3 1:50 / 1:30	DATE 07.10.2026
DRAWN / CHECKED CC / —	SERIES ARCHITECTURAL
DRAWING No.	REV


V2T-01 C05

VERSION 2T — TRIANGLE, 0.90 m VOID + 2 RODS

1/V2T-02 VIEW TO ANNEX FAÇADE (as site photo) — 1:50

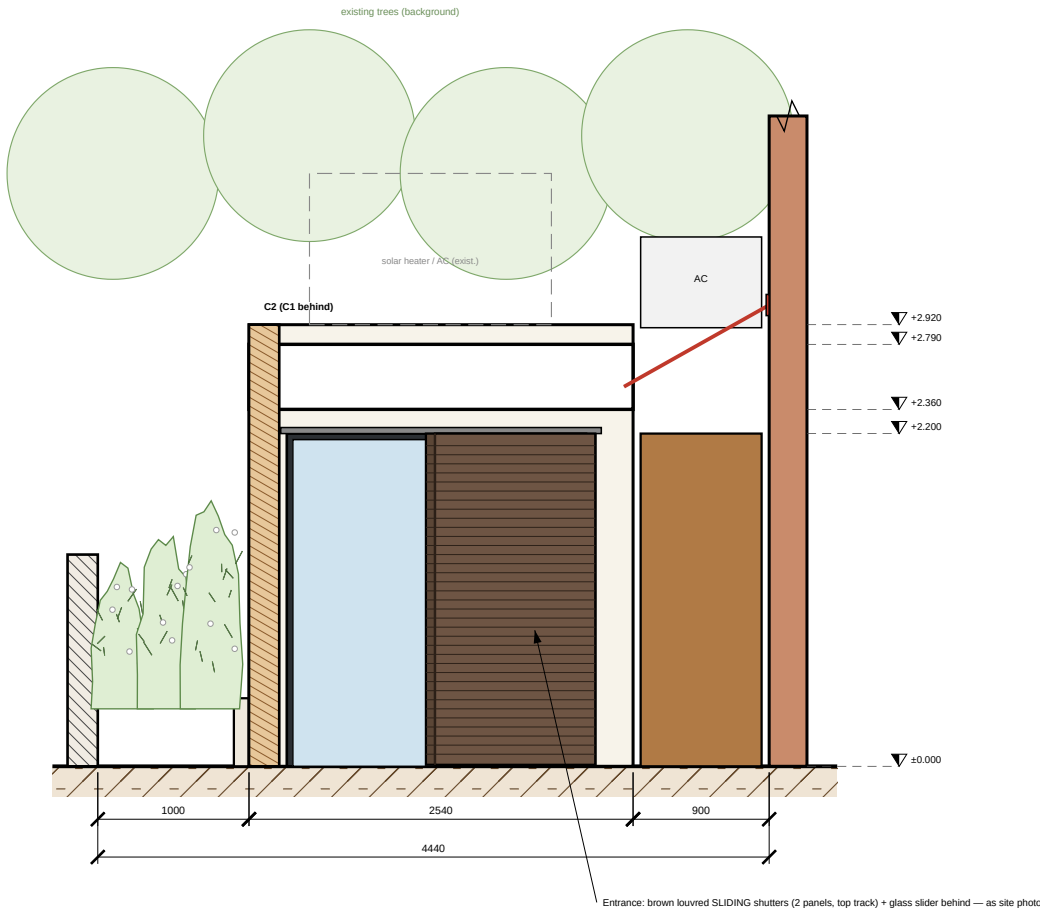


2/V2T-02 PLANTS-SIDE ELEVATION — C1 + C2 — 1:50 (plants edge 3.22 + 1.26 = 4.48)

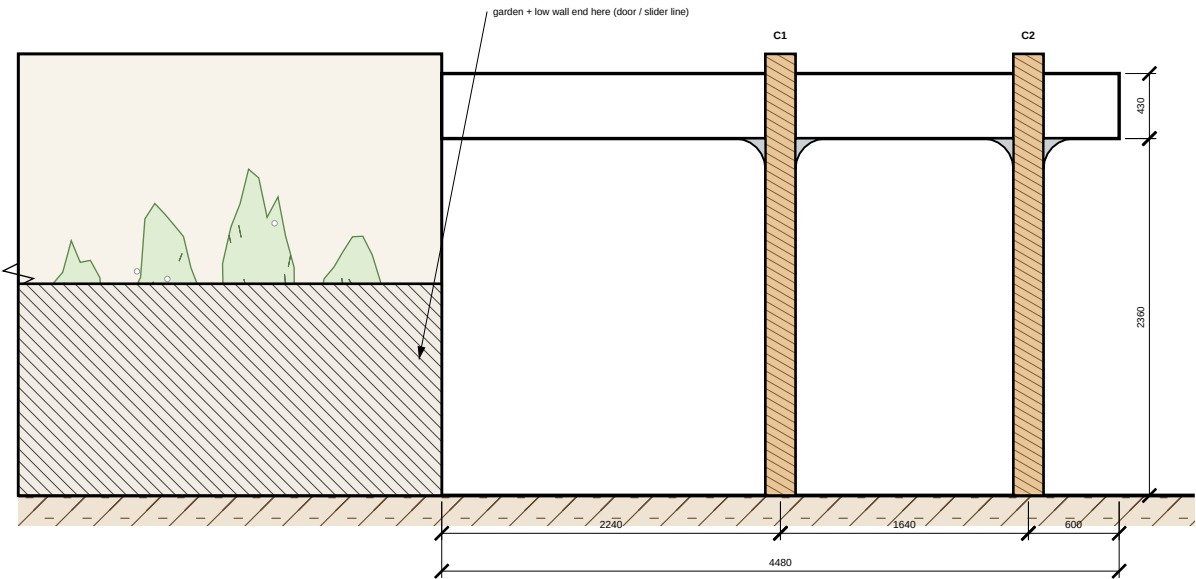


NOTES
triangular roof: plants edge 3.22 + 1.26 = 4.48, void edge 3.22, raked edge 2.84; 0.90 m void open, 2 Ø16 stainless rods to the wall; 2 columns on the plants side.
Underside +2.36, fascia 0.43 (top +2.79); columns 0.13 above roof.
Garden + low wall end at the annex end façade (door / slider line). Trees are existing, in the background.
Refined roof section & details: sheet V2T-03.

3/V2T-02 SECTION ACROSS AT C1 — 1:50 (refined: V2T-03)

tall wall left — plants side right

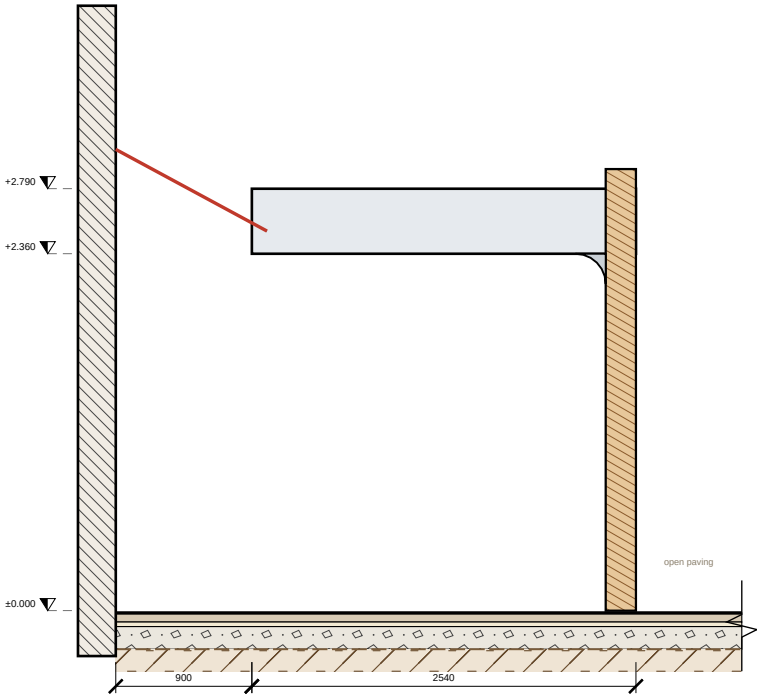

4/V2T-02 3D VIEW — from the plants side (courtyard)

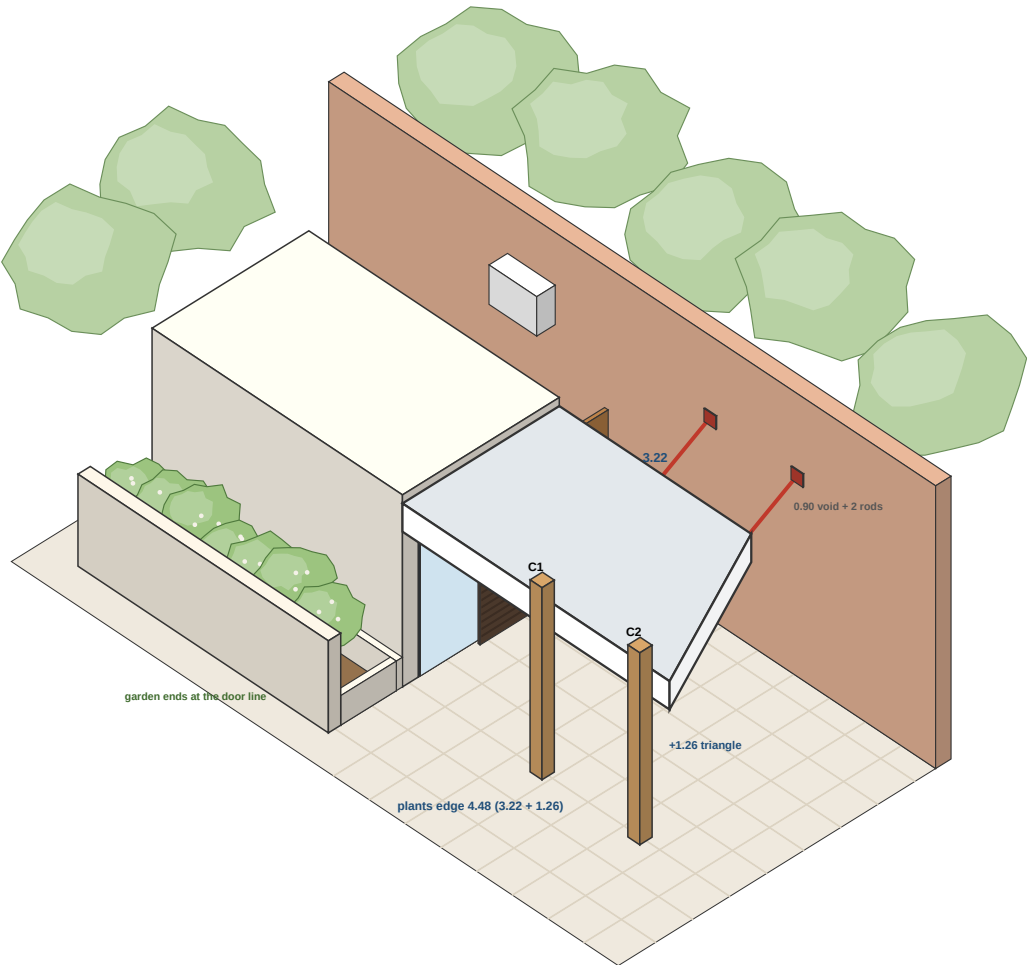

COURTYARD ROOF — V2T

VERSION 2T — TRIANGLE, 0.90 m VOID + 2 RODS: triangular roof: plants edge 3.22 + 1.26 = 4.48, void edge 3.22, raked edge 2.84; 0.90 m void open, 2 Ø16 stainless rods to the wall; 2 columns on the plants side
Client: Owner / Client
Design & drawings: Claude Code

DRAWING NOTES

- Do not scale from this drawing. Use figured dimensions only.
- All dimensions in millimetres; levels in metres relative to internal FFL ±0.000 (datum to be tied to site survey).
- Contractor to verify all dimensions, levels & existing structure on site before fabrication or ordering.
- Read with all other architectural, structural & services drawings and the specification notes (A-001).
- Structural members are preliminary: final design, connections & calculations by a licensed structural engineer to local code before construction.
- Report any discrepancy to the designer before proceeding.

REVISIONS

Rev	Date	Description
C05	07.10.2026	Garden ends at door/slider line; triangular versions V1T/V2T; 3D views
C04	07.10.2026	Two versions V1/V2 per client sections & site photo
C02	07.10.2026	Canopy to client sketch: 8.00 house, roof 3.22, u/s 2.36, fascia 0.43

PREVIEW FOR CLIENT REVIEW — per client sketch, mark-ups & site photo; not for construction

DRAWING TITLE

V2T TRIANGLE + RODS
views, section & 3D view

SCALE @ A3

1:50

DRAWN / CHECKED

CC / —

DATE

07.10.2026

SERIES

ARCHITECTURAL

DRAWING No.

REV


V2T-02

C05

VERSION 2T — TRIANGLE, 0.90 m VOID + 2 RODS

1/V2T-03 ROOF SECTION ACROSS AT C1 — 1:25

(as client sketch B: roof stops, rods to the wall)

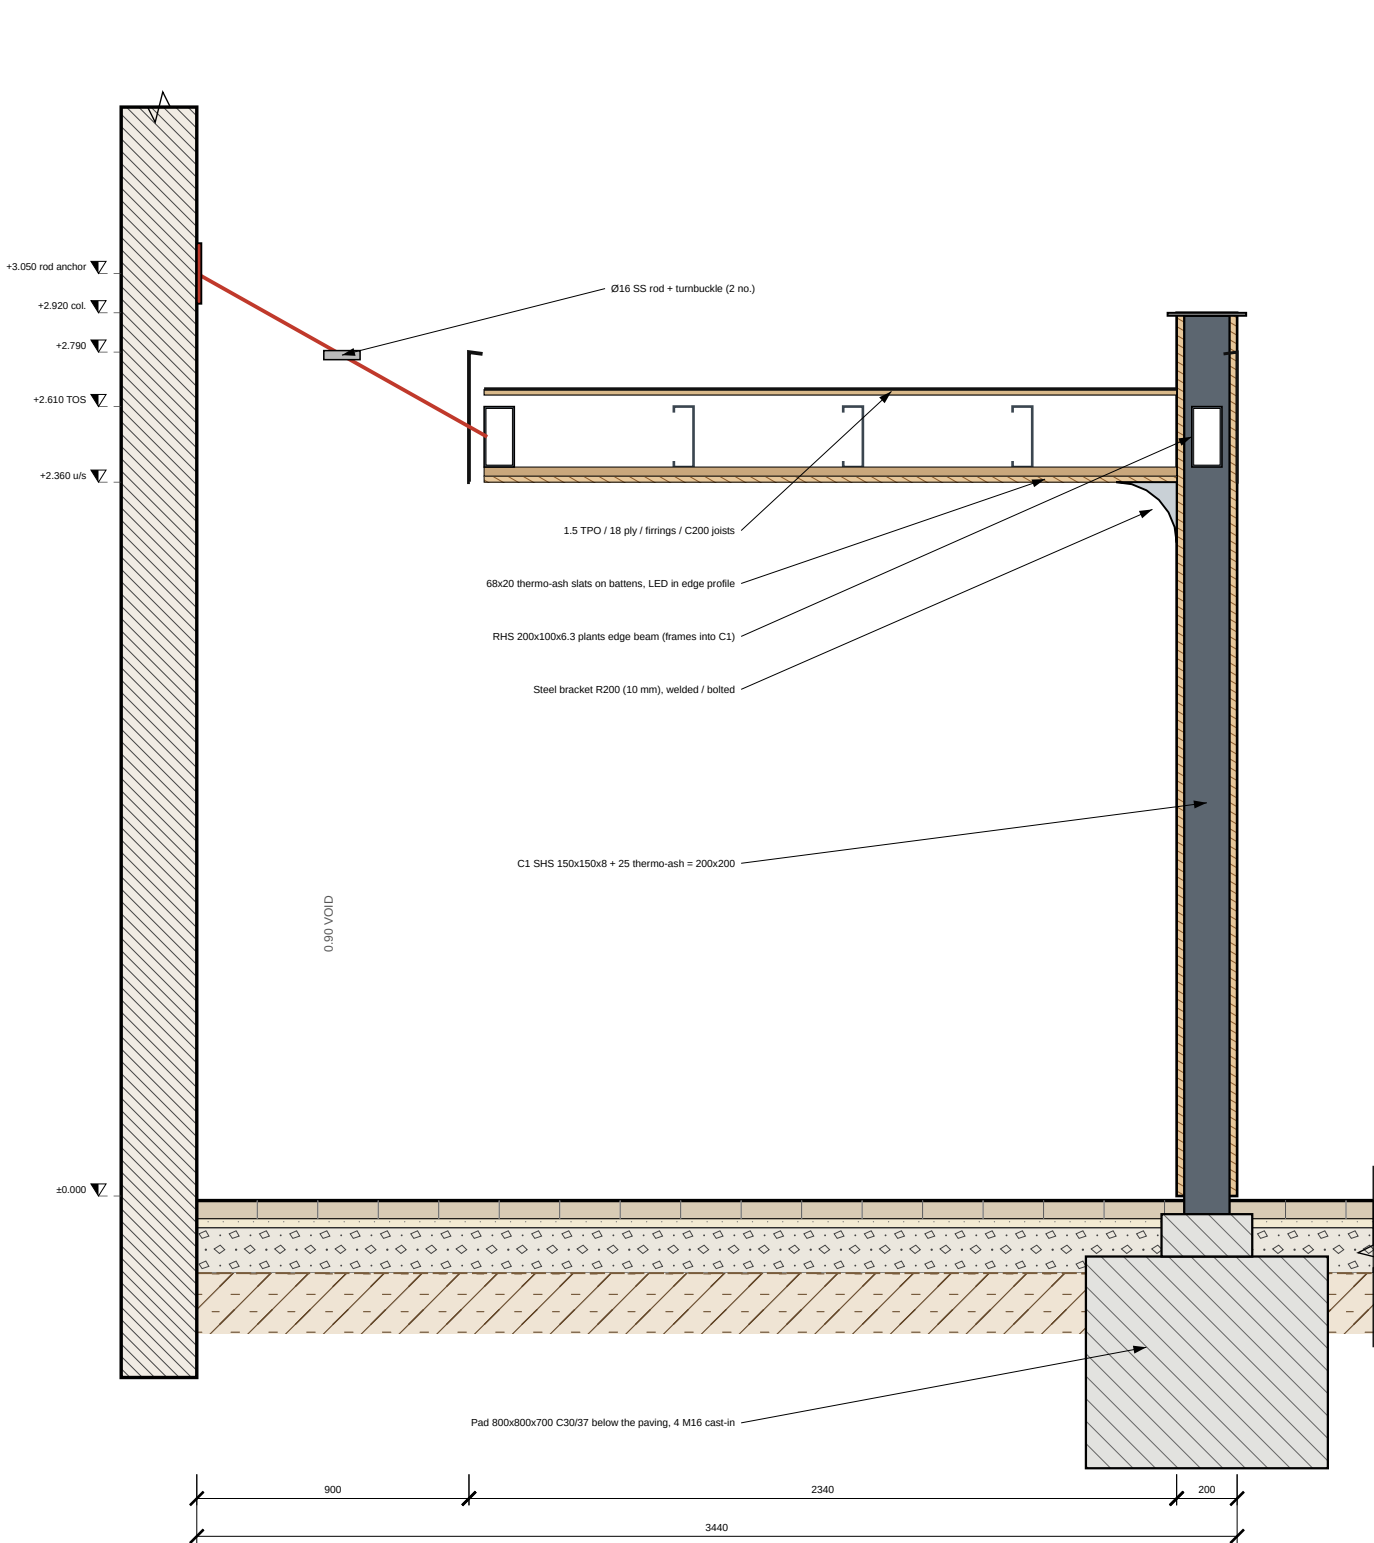


SPECIFICATION
Steel S355, hot-dip galvanised; columns & brackets powder-coated RAL 9010 or timber-clad (thermo-ash).
Roof: TPO 1.5 on 18 mm marine ply on tapered firrings (fall 1:70 to the free-edge box gutter).
Soffit: thermo-ash 68x20 slats, LED 2700 K in perimeter profile. Fascia 3 mm aluminium RAL 9010, 0.43 m.
Rods: Ø16 stainless 316, fork ends, turnbuckle, = 30° rise; engineer to confirm wall anchors.


SCALE BAR 1:25 (section 1)




D1 ROD TO WALL (client sketch B) — 1:20

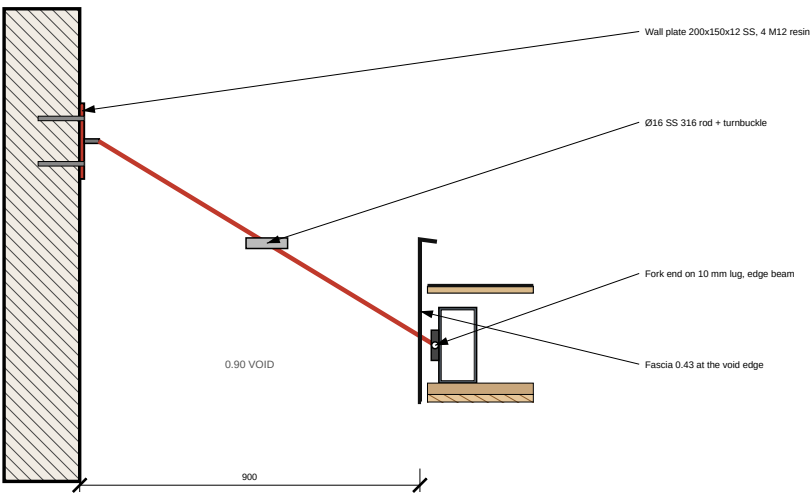

D2 COLUMN / ROOF JUNCTION (plants side) — 1:15

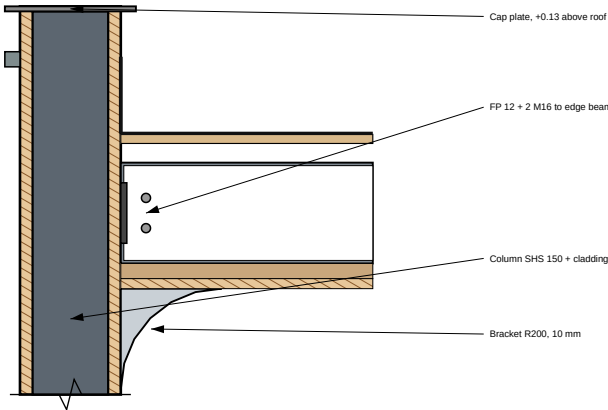

D3 TIP AT C2 (triangle) — PLAN 1:15

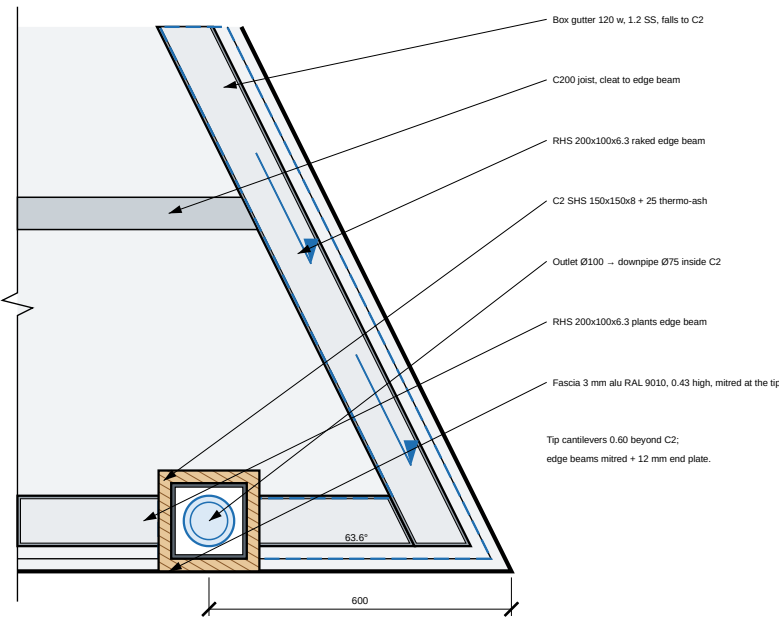

COURTYARD ROOF — V2T

VERSION 2T — TRIANGLE, 0.90 m VOID + 2 RODS: triangular roof: plants edge 3.22 + 1.26 = 4.48, void edge 3.22, raked edge 2.84; 0.90 m void open, 2 Ø16 stainless rods to the wall; 2 columns on the plants side
Client: Owner / Client
Design & drawings: Claude Code

DRAWING NOTES

- Do not scale from this drawing. Use figured dimensions only.
- All dimensions in millimetres; levels in metres relative to internal FFL ±0.000 (datum to be tied to site survey).
- Contractor to verify all dimensions, levels & existing structure on site before fabrication or ordering.
- Read with all other architectural, structural & services drawings and the specification notes (A-001).
- Structural members are preliminary: final design, connections & calculations by a licensed structural engineer to local code before construction.
- Report any discrepancy to the designer before proceeding.

REVISIONS

Rev	Date	Description
C05	07.10.2026	Garden ends at door/slider line; triangular versions V1T/V2T; 3D views
C04	07.10.2026	Two versions V1/V2 per client sections & site photo
C02	07.10.2026	Canopy to client sketch: 8.00 house, roof 3.22, u/s 2.36, fascia 0.43

PREVIEW FOR CLIENT REVIEW — per client sketch, mark-ups & site photo; not for construction

DRAWING TITLE

V2T TRIANGLE + RODS
roof section & details

SCALE @ A3

1:25 / 1:15 / 1:20

DRAWN / CHECKED

CC / —

DATE

07.10.2026

SERIES

ARCHITECTURAL

DRAWING No.

V2T-03

REV

C05