


OPTION C — TRIANGLE TO THE WALL (no void): plants edge 3.46, same raked line


TALL HOUSE WALL (exist., AC units)

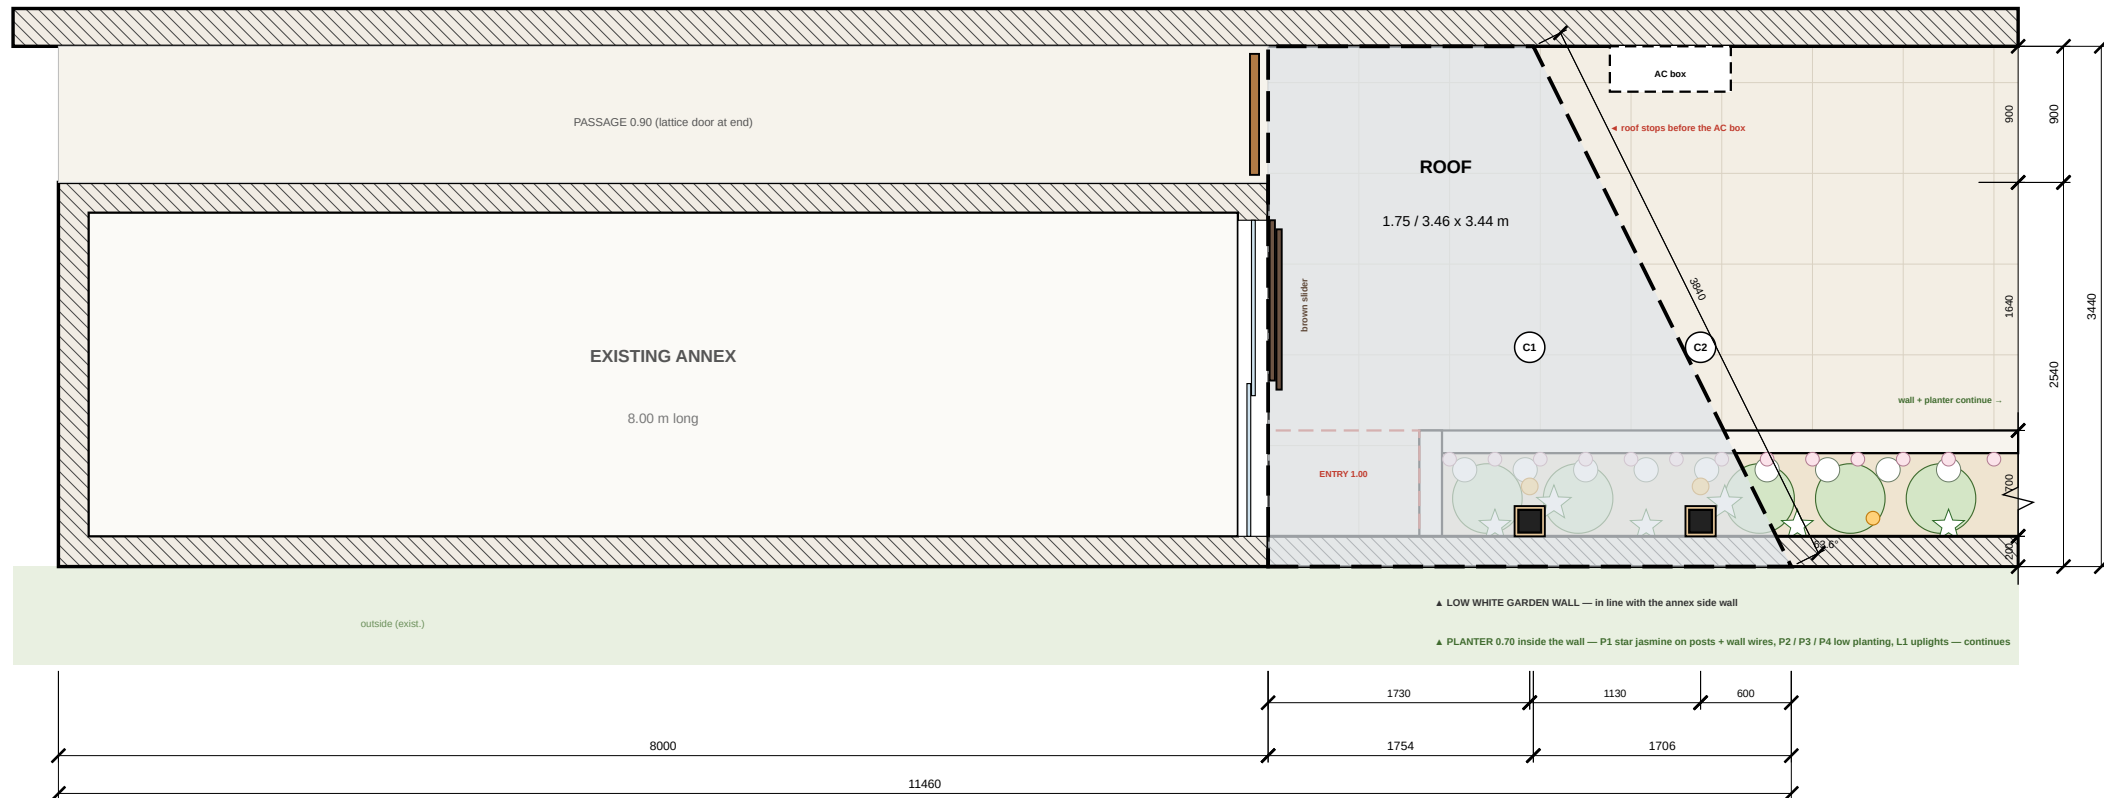

 TOP VIEW — ANNEX, GARDEN & ROOF

V1T-01 1:50 @ A3 — annex + garden wall in one line; planter 0.70 continues; entry 1.00 at the door

2/V1T-01 ROOF FRAMING PLAN — 1:30

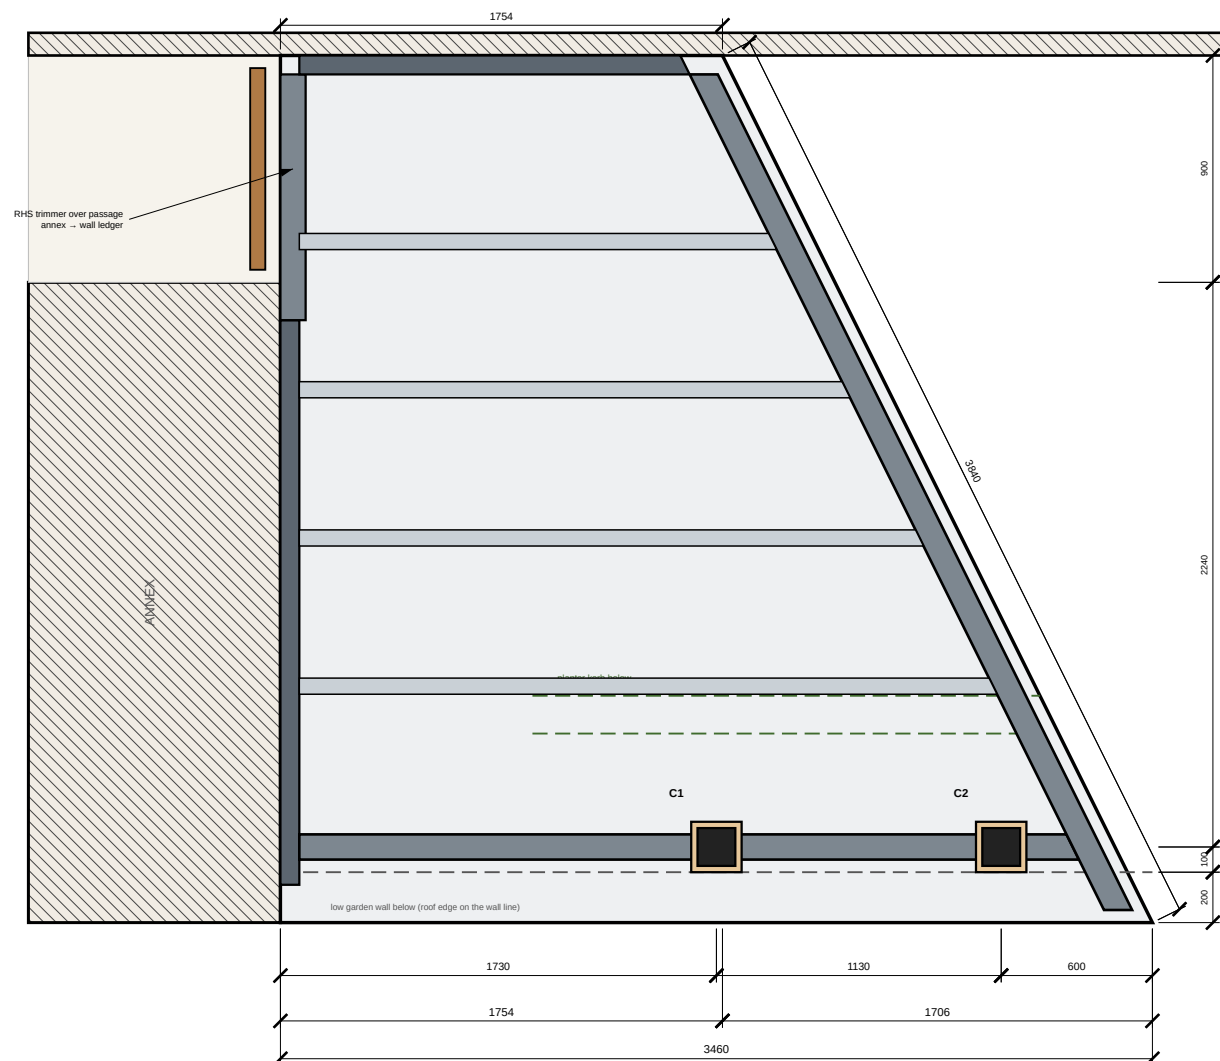

THIS VERSION

option A continued over the passage to tall wall, no void; plants edge 3.46, 2.20 at the annex line, 1.75 at the tall wall (same raked angle); bears on the annex ledger + a ledger on the tall wall; 2 columns against the garden wall.

Roof fixed to the annex end façade AND to the tall house wall (steel ledgers, resin anchors); covers the passage in front of the lattice door (RHS trimmer over the passage, annex – wall ledger).

Triangle continued to the tall wall on the SAME raked line as option A: plants edge 3.46 m, edge at the annex line 2.20 m, edge at the tall wall 1.75 m; raked edge 3.84 m at 63.6° to the plants edge.


C1 in the middle of the 3.46 edge (1.73 from the façade); C2 0.60 m from the tip (the tip cantilevers 0.60).

Joists run from the annex ledger to the raked edge beam (max. span ≈ 3.2 m); over the passage they bear on the RHS trimmer + wall ledger.

COMMON

Annex side wall and low white garden wall are ONE line; the roof's plants edge (fascia) is on it.
 0.70 inside the wall (soil + white kerb), continues along the wall; paved entry space 1.00 between the façade and the planter (walk in to the left glass door).
 Planter opening runs to the side wall (no pier).
 C1 / C2: SHS 150 clad 200x200 thermo-ash, against the garden wall, 2 SS brackets each into the wall; edge beam on the column line, roof cantilevers 0.30 to the fascia over the wall.
 Underside +2.36, fascia 0.43 (top +2.79); columns 0.13 above roof. Falls 1.70 to the box gutter on the raked edge; rainwater down C2.

3/V1T-01 3D — BIRD'S EYE (from outside, over the low garden wall)

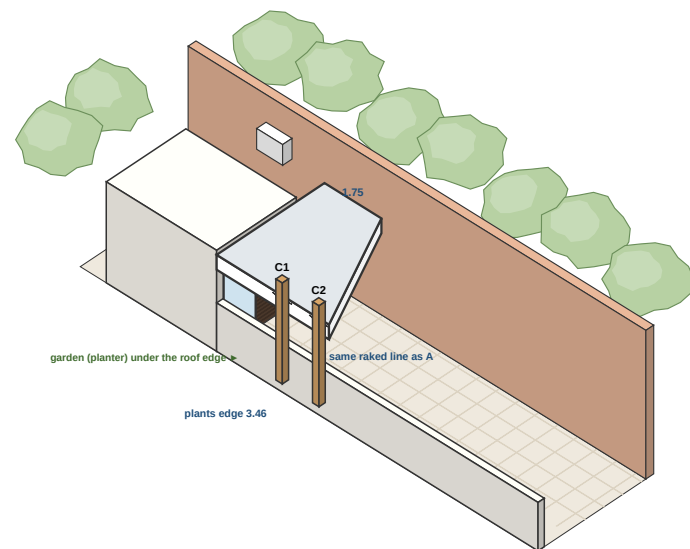

SCALE BAR 1:50 (top view)



COURTYARD ROOF — V1T

OPTION C — TRIANGLE TO THE WALL (no void): plants edge 3.46, same raked line: option A continued over the passage to the tall wall, no void: plants edge 3.46, 2.20 at the annex line, 1.75 at the tall wall (same raked angle); bears on the annex ledger + a ledger on the tall wall
2 columns against the garden wall
Client: Owner / Client
Design & drawings: Claude Code

DRAWING NOTES

1. All dimensions from this drawing. Use figured dimensions only.
2. All dimensions in millimetres; levels in metres relative to internal FFL ± 0.000 (datum to be tied to site survey).
3. Contractor to verify all dimensions, levels & existing structure on site before fabrication or ordering.
4. Read with all other architectural, structural & services drawings and the specification notes (A-001).
5. Structural members are preliminary: final design, connections & calculations by a licensed structural engineer to local code before construction.
6. Report any discrepancy to the designer before proceeding.

Rev	Date	Description
C16	08.10.2026	Roof supported by the tall wall, no void: C triangle / D rectangle 2.20
C15	08.10.2026	Void edge max 2.20 (before the AC box): A triangle same angle / B rectangle 2.20
C14	07.10.2026	Planting per client reference: jasmine, low shrubs, uplifts

FOR CLIENT CHECK — roof supported by the tall wall, no void at the door entrance: OPTION C / OPTION D

DRAWING TITLE

OPTION C — TRIANGLE TO WALL
top view & roof framing

SCALE @ A3 1:50 / 1:30	DATE 08.10.2026
DRAWN / CHECKED CC / —	SERIES ARCHITECTURAL

DRAWING No.


EV

C16-C

C16

OPTION D — RECTANGLE 2.20 TO THE WALL (2.20 x 3.44, no void)


TALL HOUSE WALL (exist., AC units)

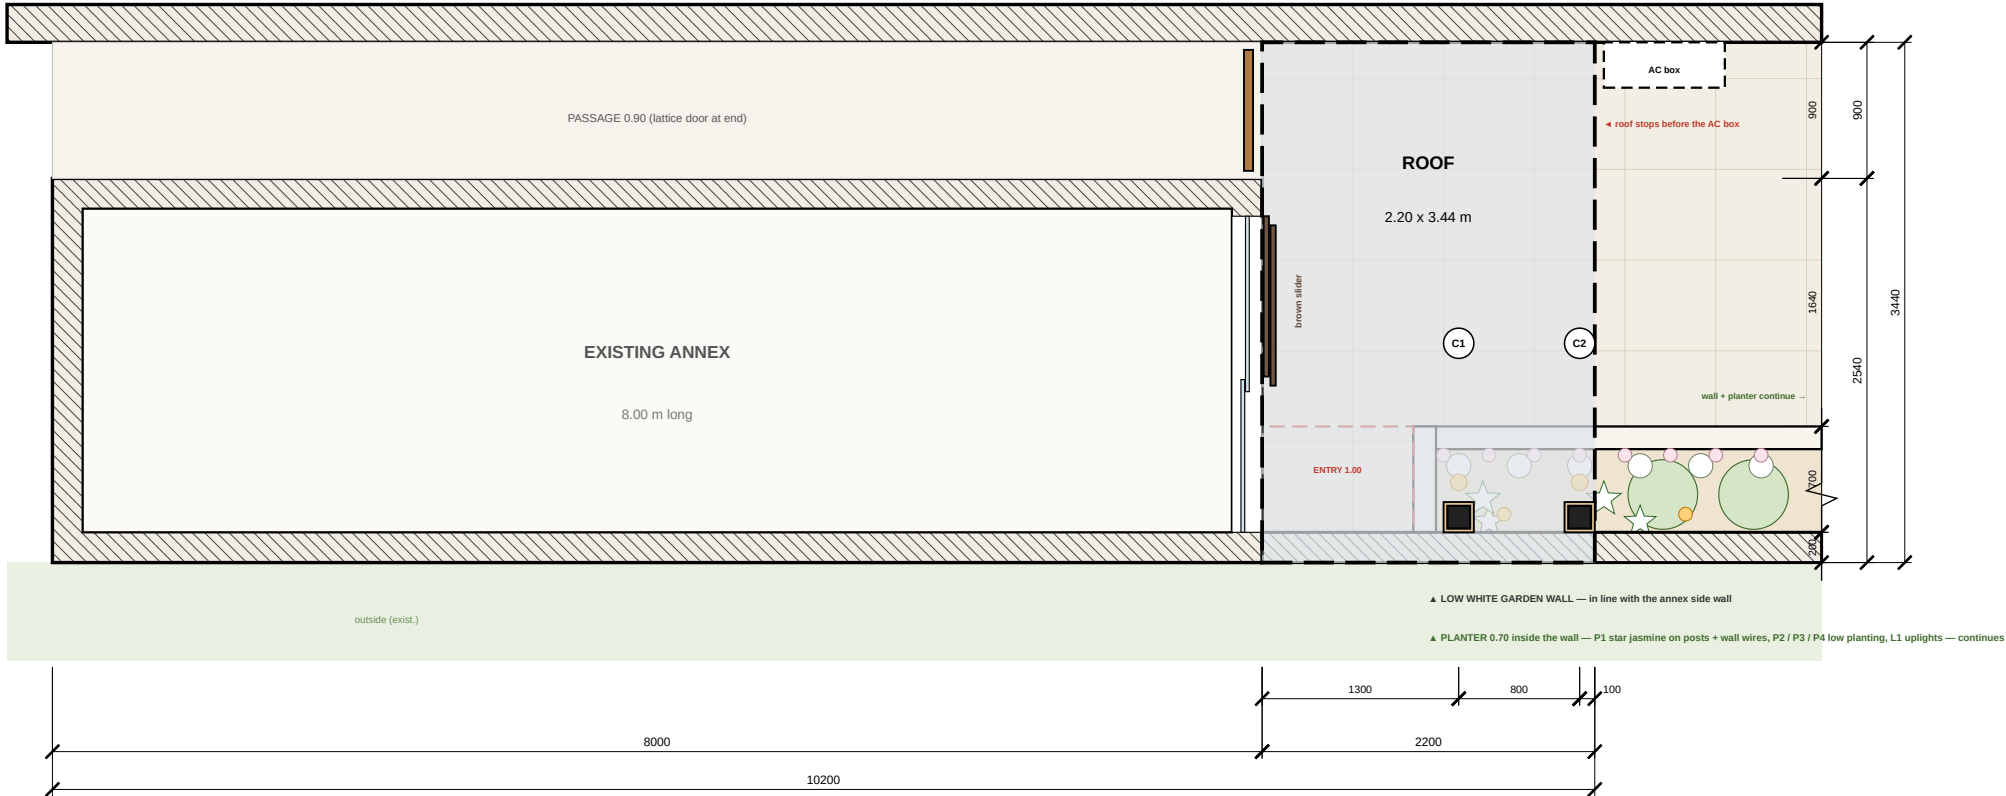

1 TOP VIEW — ANNEX, GARDEN & ROOF

V1-01 1:50 @ A3 — annex + garden wall in one line; planter 0.70 continues; entry 1.00 at the door

2/V1-01 ROOF FRAMING PLAN — 1:30

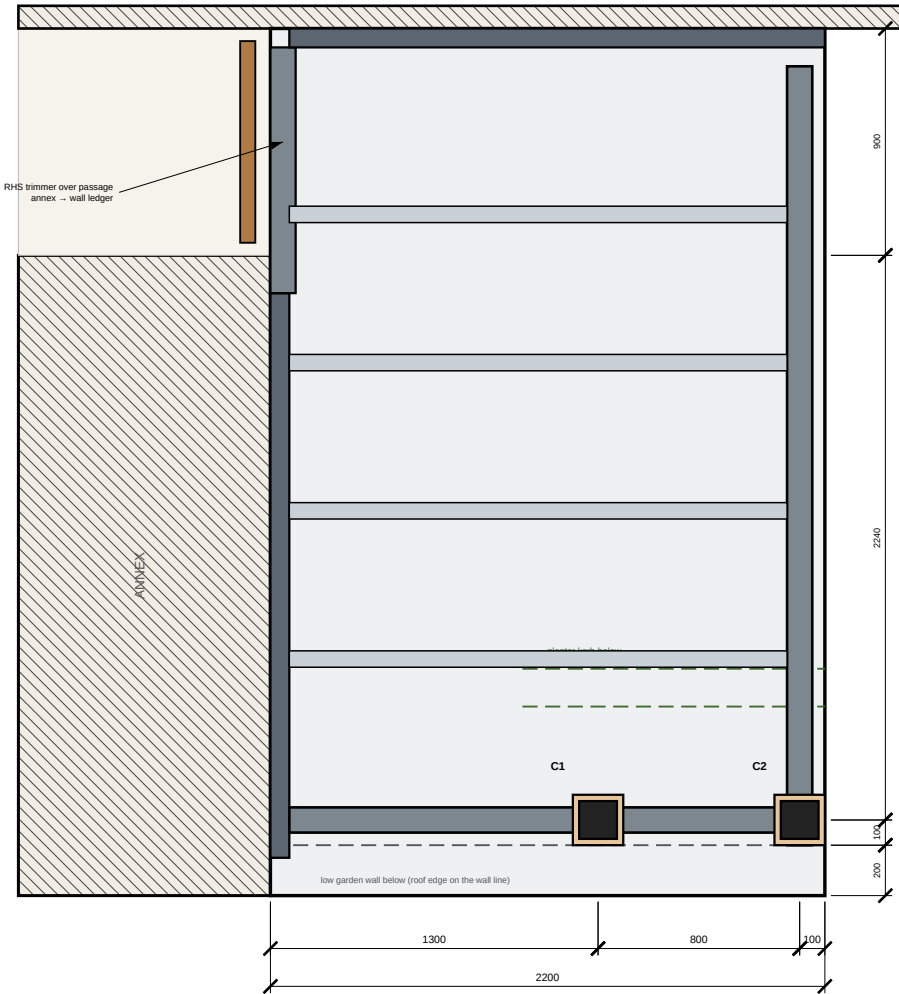

THIS VERSION

option B continued over the passage to the tall wall, no void: 2.20 x 3.44; bears on the annex ledger + a ledger on the tall wall; 2 columns against the garden wall. Roof fixed to the annex end façade AND to the tall house wall (steel ledgers, resin anchors); covers the passage in front of the lattice door (RHS trimmer over the passage, annex — wall ledger).

C1 just inside the planter (clear of the near-end kerb), C2 at the corner; roof 2.20 long along the tall wall — stops before the AC box.

COMMON


Annex side wall and low white garden wall are ONE line; the roof's plants edge (fascia) is on it.

Planter 0.70 inside the wall (soil + white kerb), continues along the wall; paved entry space 1.00 between the façade and the planter (walk in to the left glass door). Entrance opening runs to the side wall (no pier).

C1 / C2: SHS 150 clad 200x200 thermo-ash, against the garden wall, 2 SS brackets each into the wall; edge beam on the column line, roof cantilevers 0.30 to the fascia over the wall.

Underside +2.36, fascia 0.43 (top +2.79); columns 0.13 above roof. Falls 1:70 to the box gutter on the raked edge; rainwater down C2.

3/V1-01 3D — BIRD'S EYE (from outside, over the low garden wall)

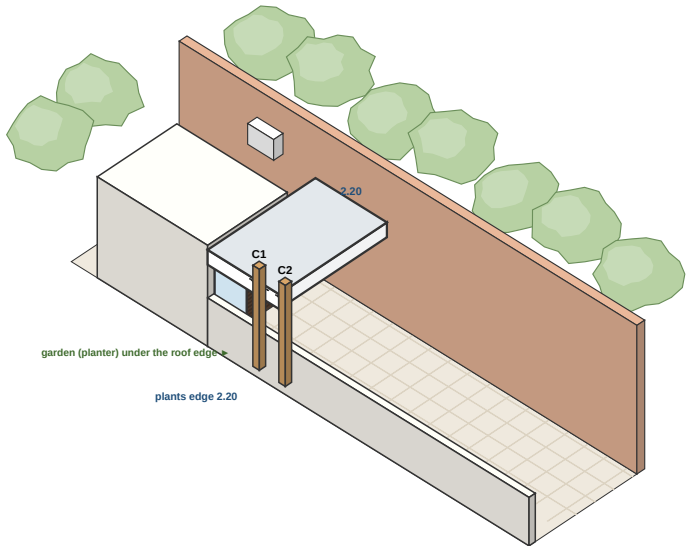

SCALE BAR 1:50 (top view)



COURTYARD ROOF — V1

OPTION D — RECTANGLE 2.20 TO THE WALL (2.20 x 3.44, no void): option B continued over the passage to the tall wall, no void: 2.20 x 3.44; bears on the annex ledger + a ledger on the tall wall; 2 columns against the garden wall
Client: Owner / Client
Design & drawings: Claude Code

DRAWING NOTES

- Do not scale from this drawing. Use figured dimensions only.
- All dimensions in millimetres; levels in metres relative to internal FFL ± 0.000 (datum to be tied to site survey).
- Contractor to verify all dimensions, levels & existing structure on site before fabrication or ordering.
- Read with all other architectural, structural & services drawings and the specification notes (A-001).
- Structural members are preliminary: final design, connections & calculations by a licensed structural engineer to local code before construction.
- Report any discrepancy to the designer before proceeding.

REVISIONS

Rev	Date	Description
C16	08.10.2026	Roof supported by the tall wall, no void: C triangle / D rectangle 2.20
C15	08.10.2026	Void edge max 2.20 (before the AC box): A triangle same angle / B rectangle 2.20
C14	07.10.2026	Planting per client reference: jasmine, low shrubs, uprights

FOR CLIENT CHECK — roof supported by the tall wall, no void at the door entrance: OPTION C / OPTION D

DRAWING TITLE

OPTION D — RECTANGLE TO WALL
top view & roof framing

SCALE @ A3

1:50 / 1:30

DRAWN / CHECKED

CC / —

DATE

08.10.2026

SERIES

ARCHITECTURAL

DRAWING No.

REV

C16-D

C16