



VERSION 2T — TRIANGLE, 0.90 m VOID + 2 RODS

1/V2T-02 VIEW TO ANNEX FAÇADE (as site photo) — 1:50

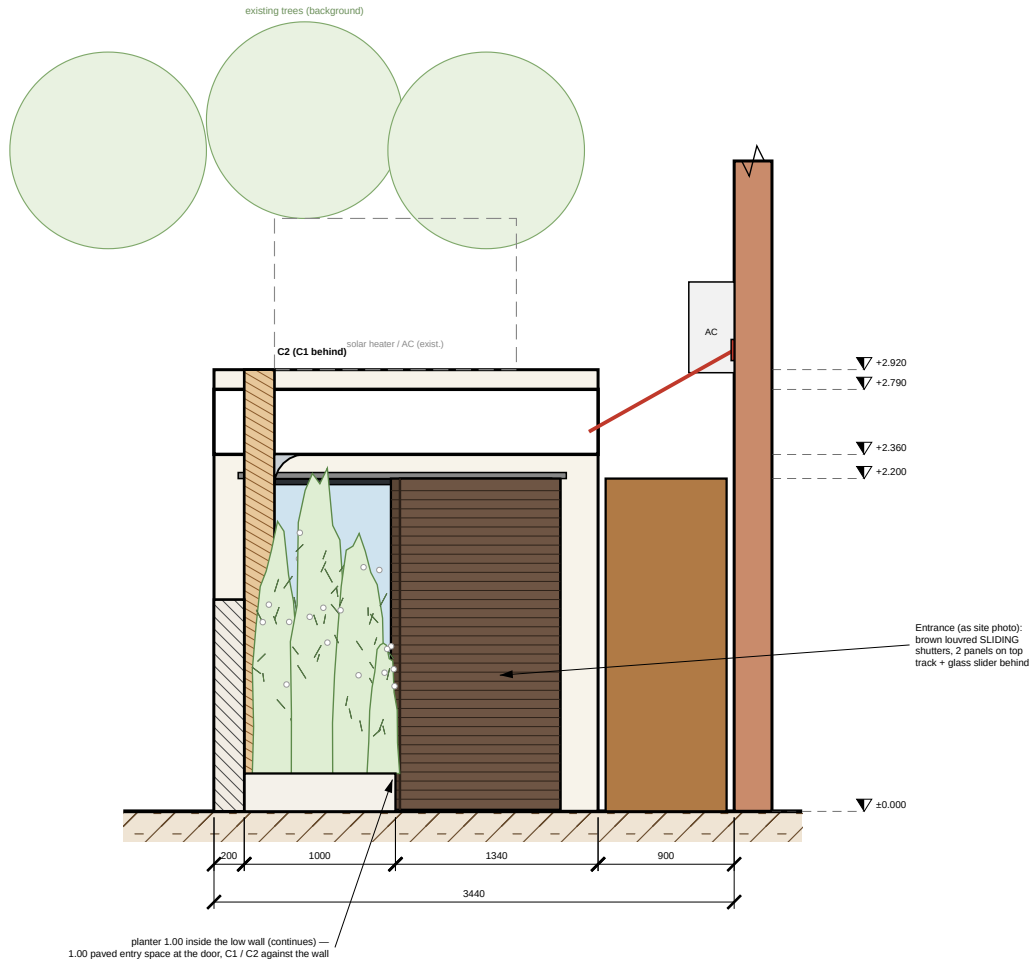


2/V2T-02 PLANTS-SIDE ELEVATION — C1 + C2 — 1:50 (plants edge 3.22 + 1.26 = 4.48)

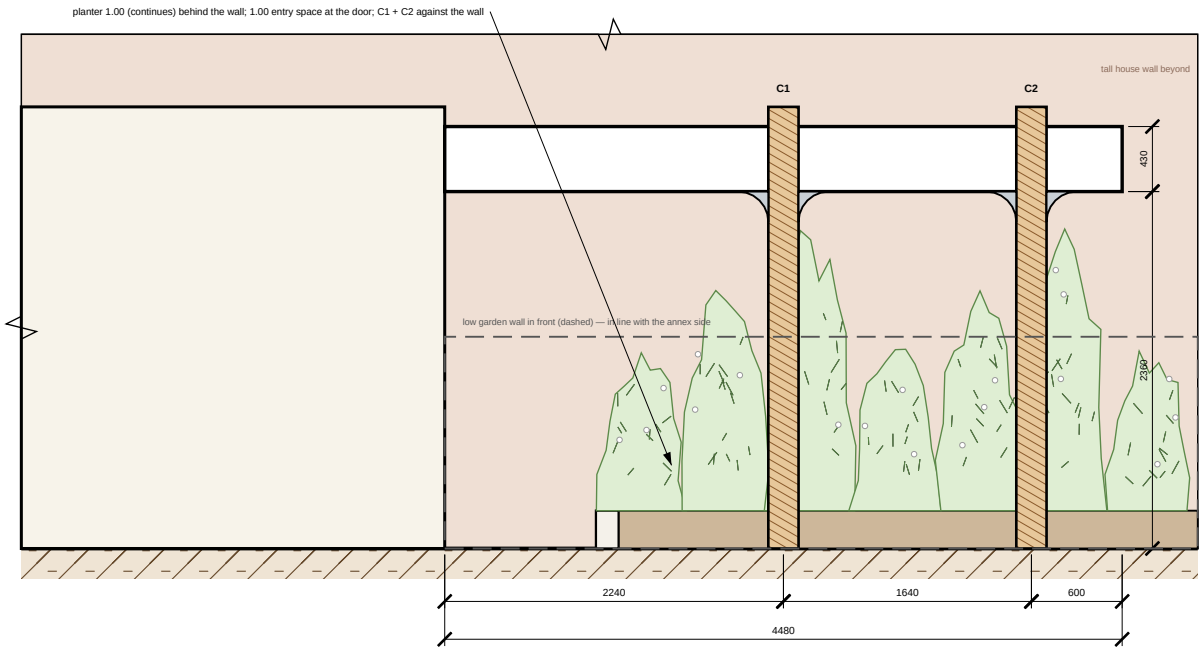


NOTES
triangular roof: plants edge 3.22 + 1.26 = 4.48, void edge 3.22, raked edge 2.84; 0.90 m void open, 2 slim Ø16 stainless hangers to the tall wall; 2 columns against the garden wall.
Underside +2.36, fascia 0.43 (top +2.79); columns 0.13 above roof.
Annex side wall + low garden wall in one line (roof edge on it). Planter 1.00 inside the wall, continues; 1.00 paved entry space at the door; C1 + C2 against the wall. Trees are existing, in the background.
Refined roof section & details: sheet V2T-03.

3/V2T-02 SECTION ACROSS AT C1 — 1:50 (refined: V2T-03)

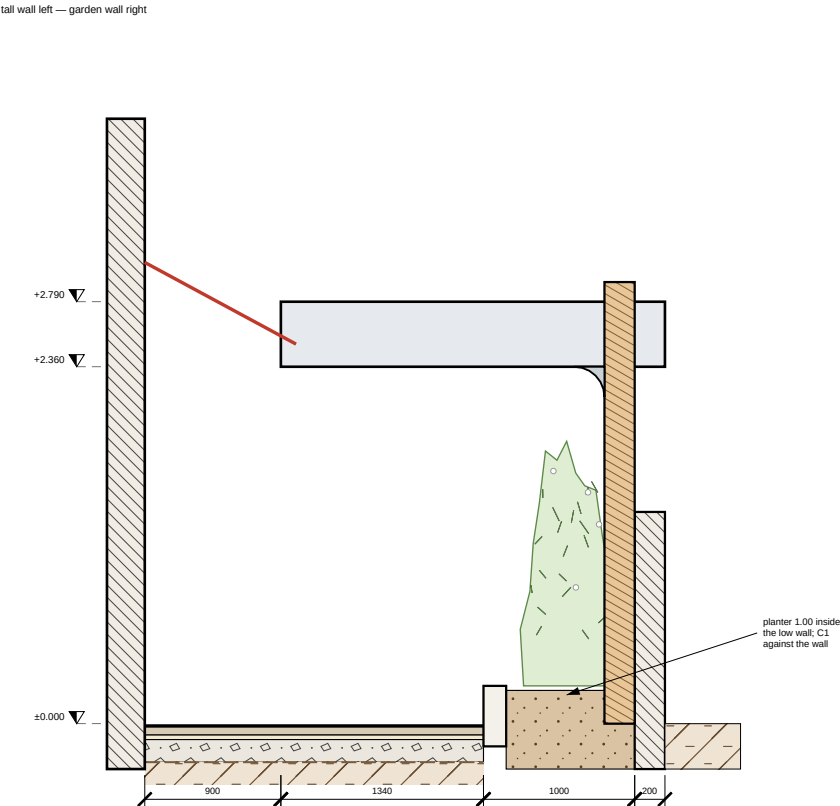

4/V2T-02 3D — EYE LEVEL, SAME DIRECTION AS THE SITE PHOTO

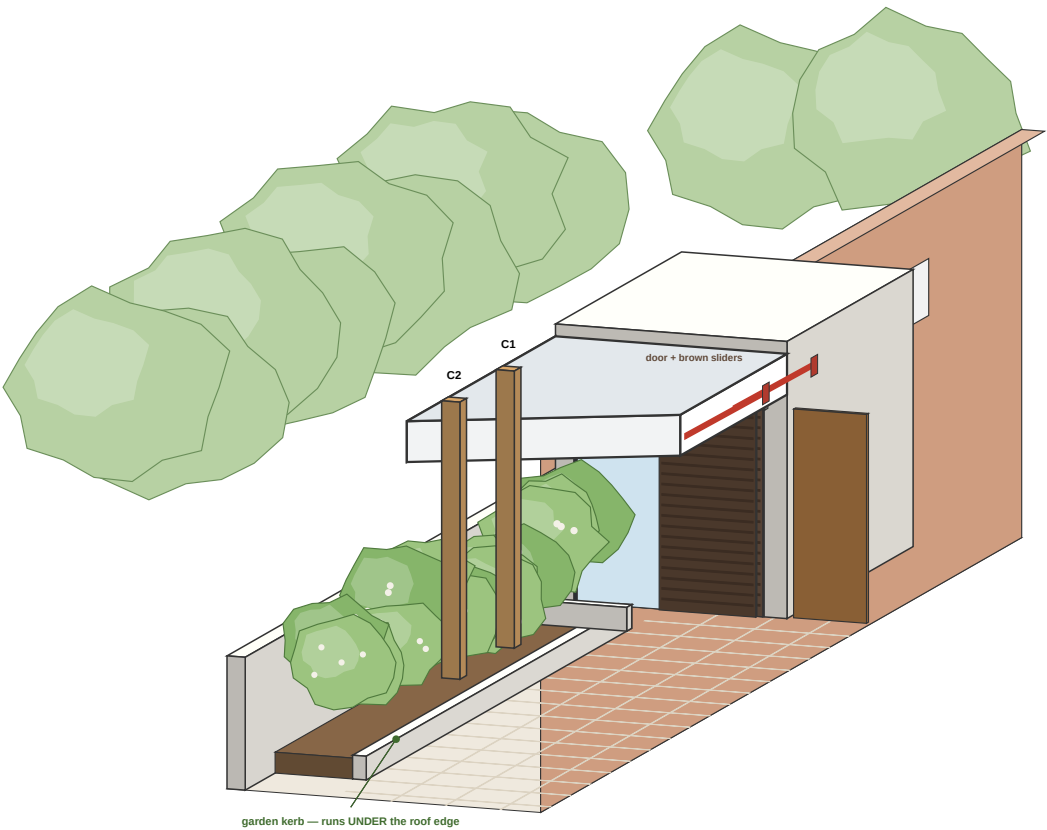

COURTYARD ROOF — V2T

VERSION 2T — TRIANGLE, 0.90 m VOID + 2 RODS: triangular roof: plants edge 3.22 + 1.26 = 4.48, void edge 3.22, raked edge 2.84; 0.90 m void open, 2 slim Ø16 stainless hangers to the tall wall; 2 columns against the garden wall
Client: Owner / Client
Design & drawings: Claude Code

DRAWING NOTES

- Do not scale from this drawing. Use figured dimensions only.
- All dimensions in millimetres; levels in metres relative to internal FFL ±0.000 (datum to be tied to site survey).
- Contractor to verify all dimensions, levels & existing structure on site before fabrication or ordering.
- Read with all other architectural, structural & services drawings and the specification notes (A-001).
- Structural members are preliminary: final design, connections & calculations by a licensed structural engineer to local code before construction.
- Report any discrepancy to the designer before proceeding.

REVISIONS

Rev	Date	Description
C12	07.10.2026	FINAL V2T set: walls in one line, planter 1.00 + entry 1.00, hangers
C11	07.10.2026	Annex side wall + garden wall in one line; roof as sketch
C08	07.10.2026	Planter 1.00; columns against + fixed to the low wall
C06	07.10.2026	Garden = planter in front of the façade, left of the door, partly under roof

FINAL DESIGN (V2T) — for engineer's calcs & tender; verify all dimensions on site

DRAWING TITLE

V2T TRIANGLE + RODS
views, section & 3D view

SCALE @ A3 1:50	DATE 07.10.2026
DRAWN / CHECKED CC / —	SERIES ARCHITECTURAL


DRAWING No. REV

V2T-02 C12

VERSION 2T — TRIANGLE, 0.90 m VOID + 2 RODS


1/V2T-03 ROOF SECTION ACROSS AT C1 — 1:25

(as client sketch B: roof stops, rods to the wall)

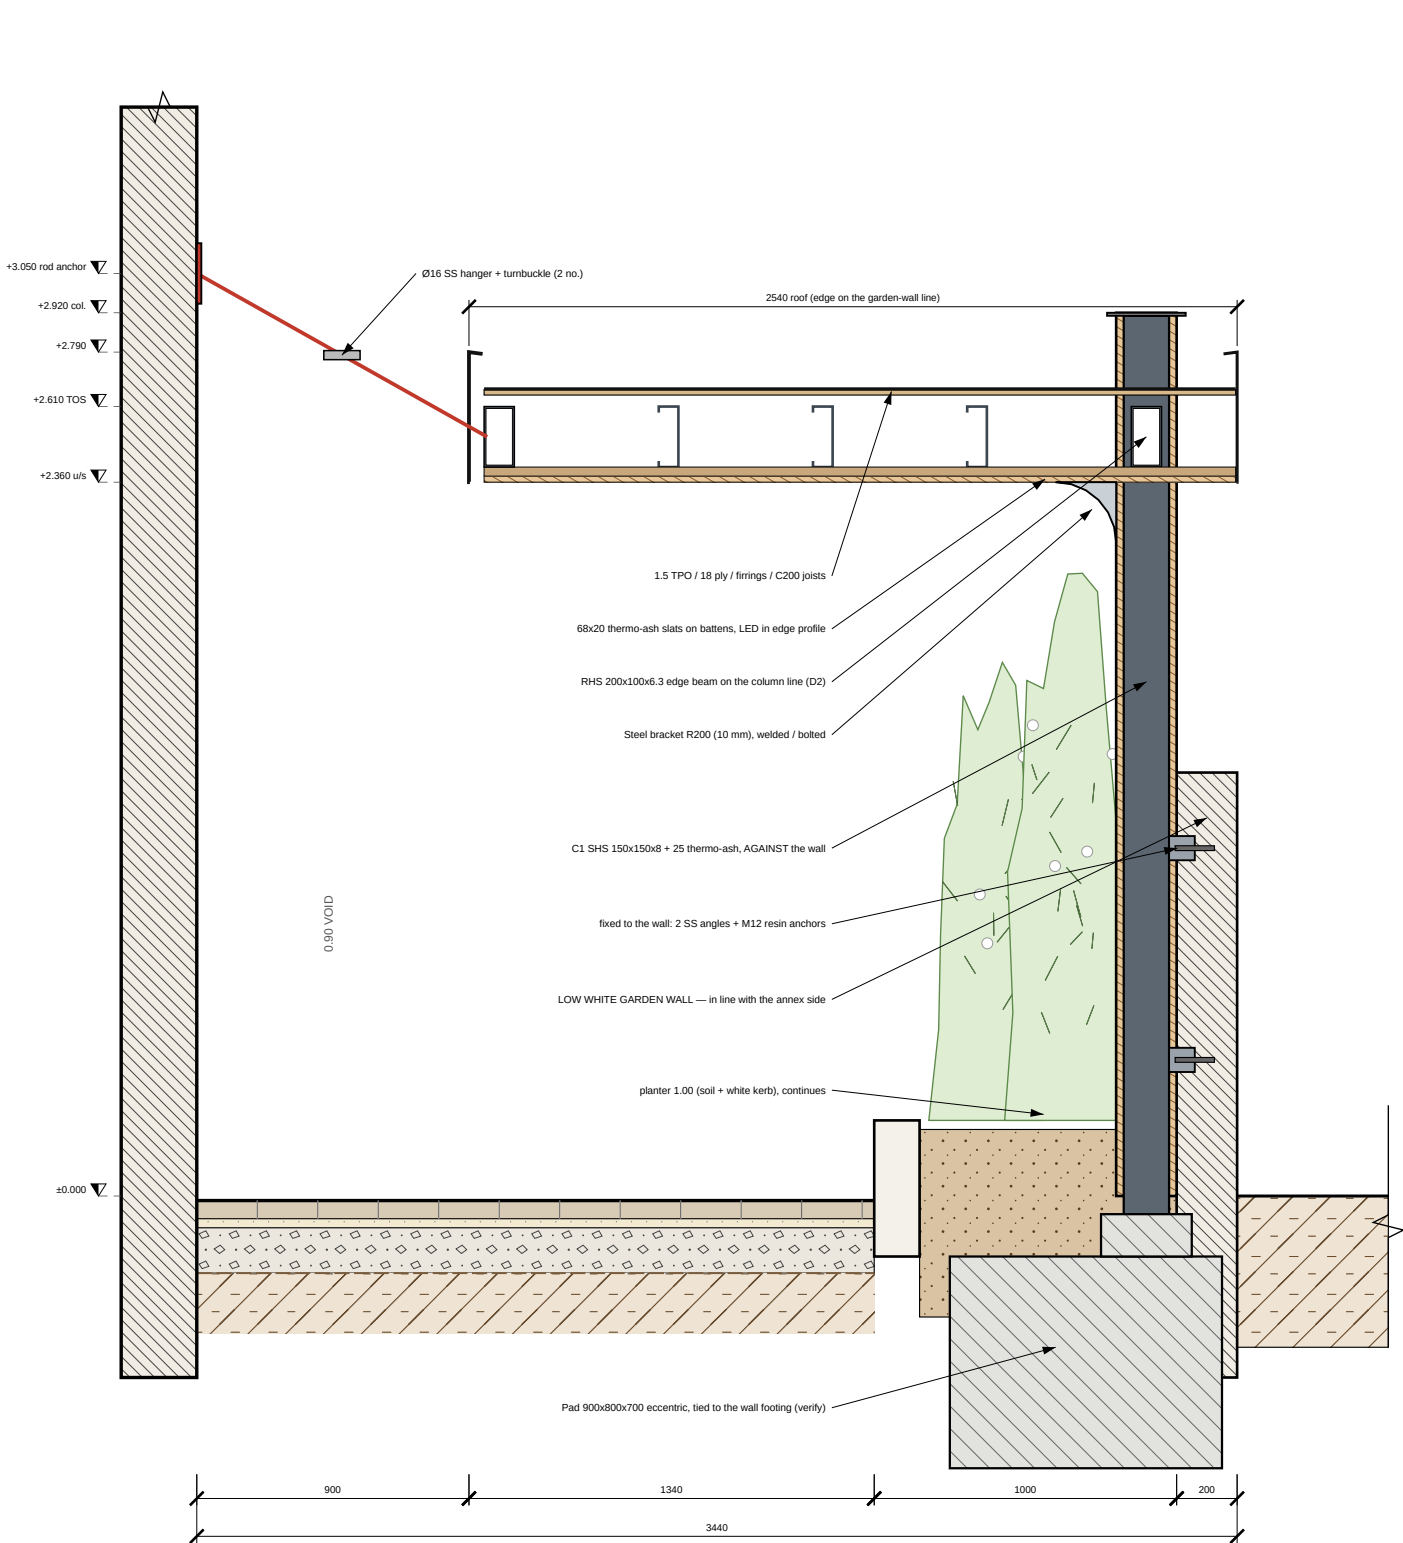


SPECIFICATION
Steel S355, hot-dip galvanised; columns & brackets powder-coated RAL 9010 or timber-clad (thermo-ash).
Roof: TPO 1.5 on 18 mm marine ply on tapered firings (fall 1:70 to the free-edge box gutter).
Soffit: thermo-ash 68x20 slats, LED 2700 K in perimeter profile. Fascia 3 mm aluminium RAL 9010, 0.43 m.
Rods: Ø16 stainless 316, fork ends, turnbuckle, = 30° rise; engineer to confirm wall anchors.


SCALE BAR 1:25 (section 1)

 


D1 ROD TO WALL (client sketch B) — 1:20

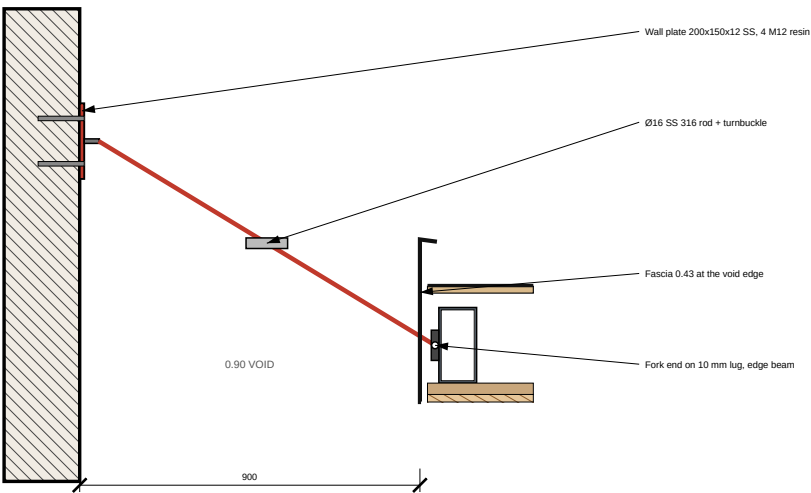

D2 COLUMN / ROOF JUNCTION (plants side) — 1:15

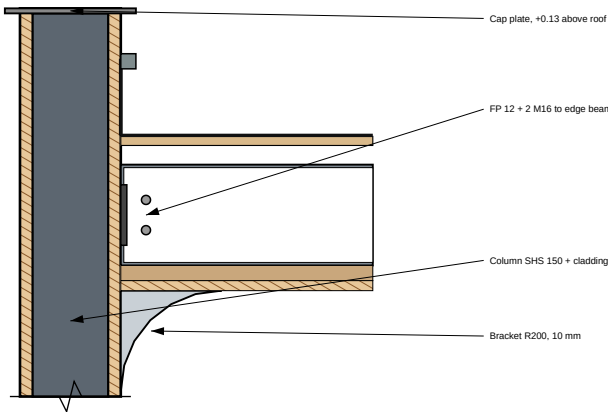

D3 TIP AT C2 (triangle) — PLAN 1:15

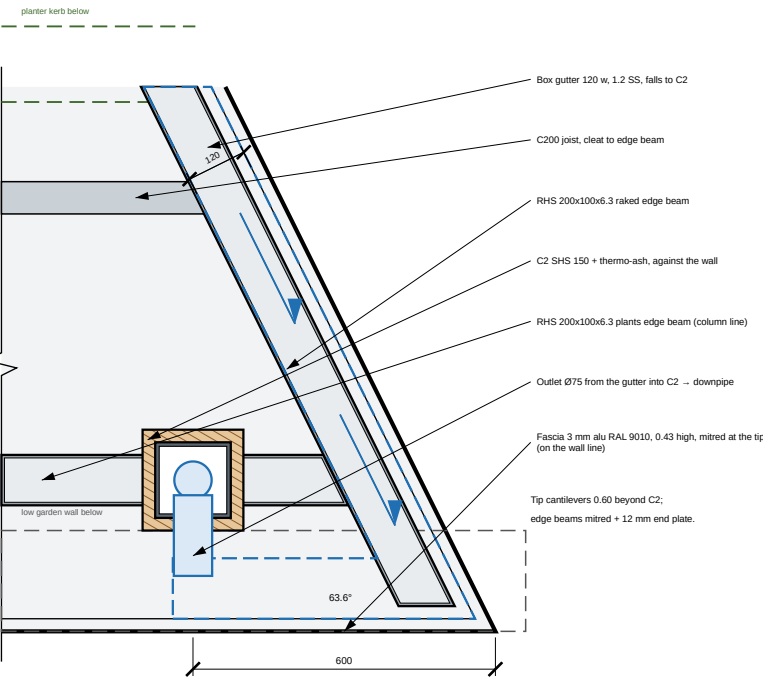

COURTYARD ROOF — V2T

VERSION 2T — TRIANGLE, 0.90 m VOID + 2 RODS: triangular roof: plants edge 3.22 + 1.26 = 4.48, void edge 3.22, raked edge 2.84; 0.90 m void open, 2 slim Ø16 stainless hangers to the tall wall; 2 columns against the garden wall
Client: Owner / Client
Design & drawings: Claude Code

DRAWING NOTES

- Do not scale from this drawing. Use figured dimensions only.
- All dimensions in millimetres; levels in metres relative to internal FFL ±0.000 (datum to be tied to site survey).
- Contractor to verify all dimensions, levels & existing structure on site before fabrication or ordering.
- Read with all other architectural, structural & services drawings and the specification notes (A-001).
- Structural members are preliminary: final design, connections & calculations by a licensed structural engineer to local code before construction.
- Report any discrepancy to the designer before proceeding.

REVISIONS

Rev	Date	Description
C12	07.10.2026	FINAL V2T set: walls in one line, planter 1.00 + entry 1.00, hangers
C11	07.10.2026	Annex side wall + garden wall in one line; roof as sketch
C08	07.10.2026	Planter 1.00; columns against + fixed to the low wall
C06	07.10.2026	Garden = planter in front of the façade, left of the door, partly under roof

FINAL DESIGN (V2T) — for engineer's calcs & tender; verify all dimensions on site

DRAWING TITLE

V2T TRIANGLE + RODS
roof section & details

SCALE @ A3

1:25 / 1:15 / 1:20

DRAWN / CHECKED

CC / —

DATE

07.10.2026

SERIES

ARCHITECTURAL

DRAWING No.

V2T-03

REV

C12