


VERSION 2T — TRIANGLE, 0.90 m VOID + 2 RODS


TALL HOUSE WALL (exist., AC units)

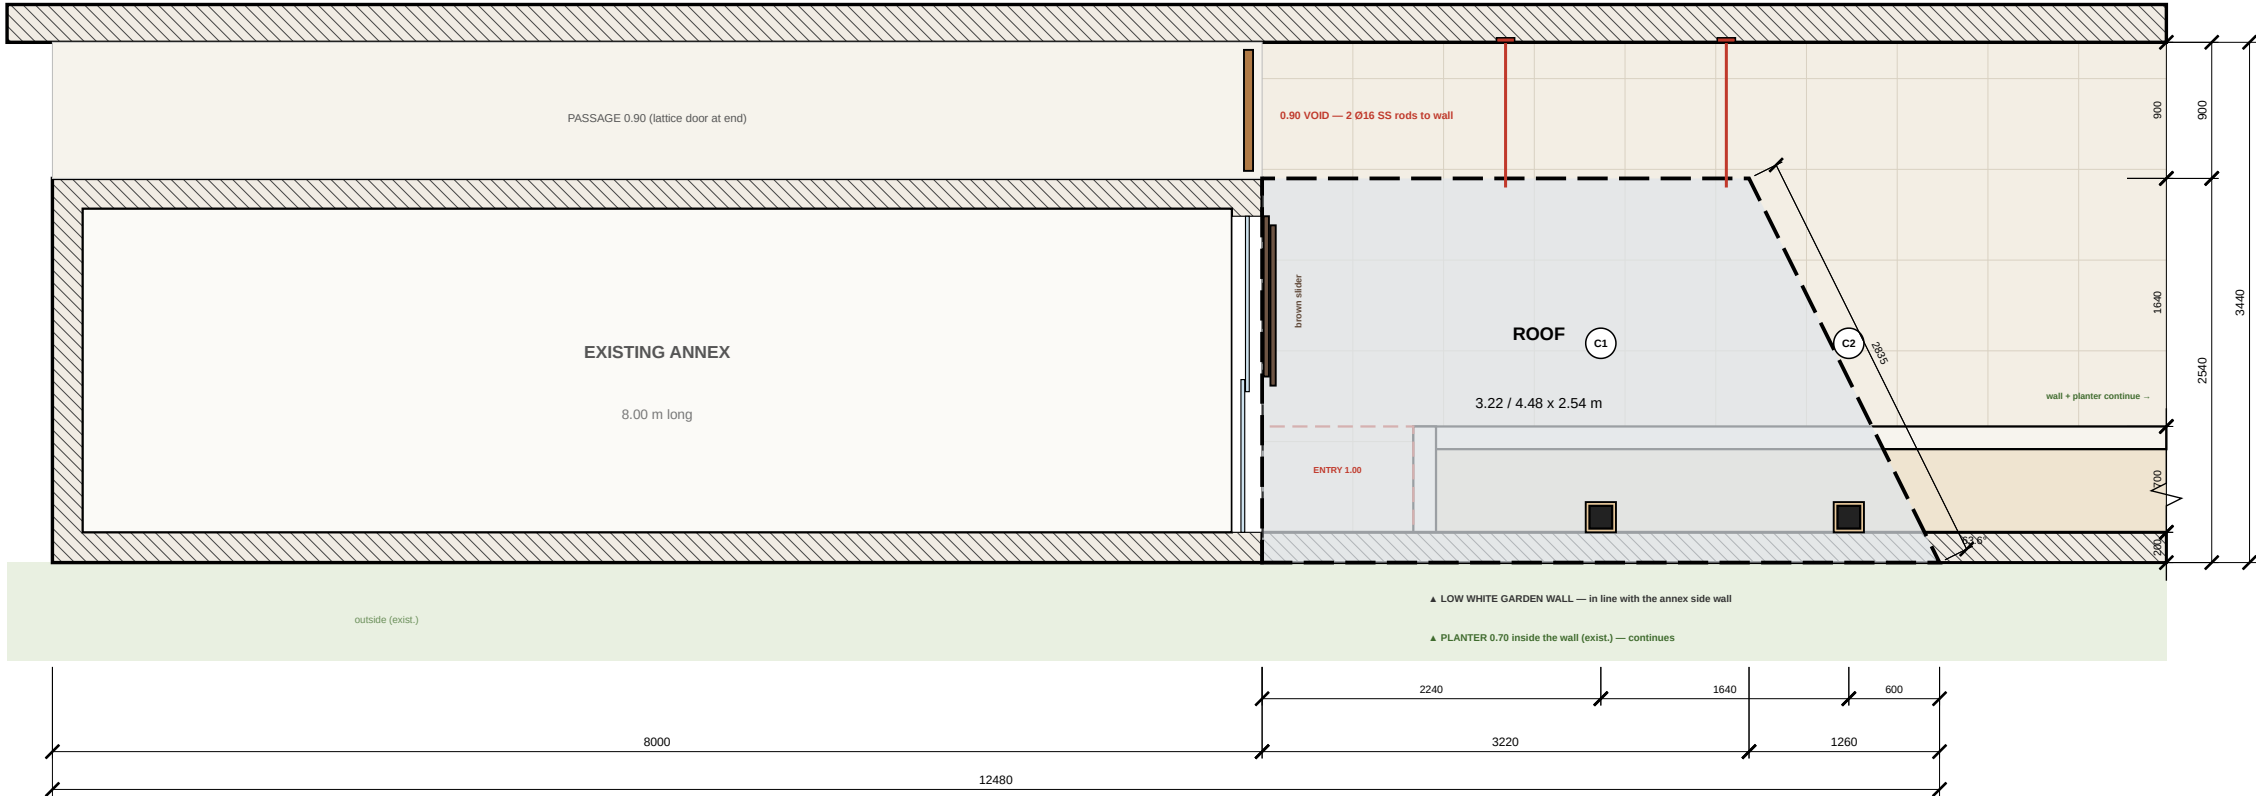

1 TOP VIEW — ANNEX, GARDEN & ROOF


V2T-01 1:50 @ A3 — annex + garden wall in one line; planter 0.70 continues; entry 1.00 at the door

2/V2T-01 ROOF FRAMING PLAN — 1:30

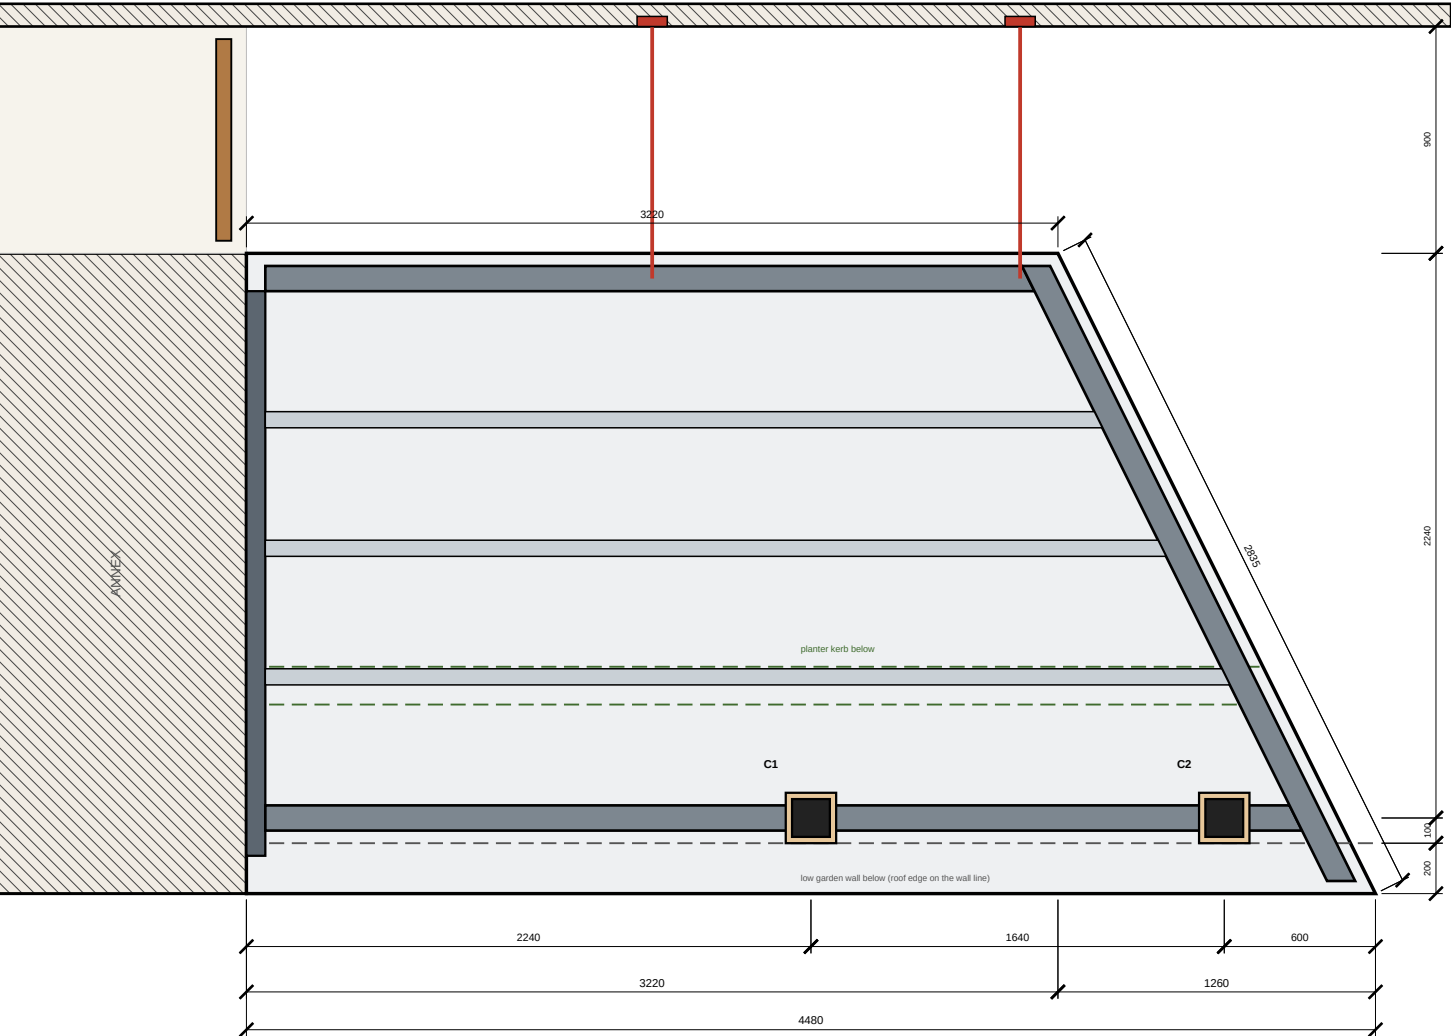

THIS VERSION
triangular roof: plants edge 3.22 + 1.26 = 4.48, void edge 3.22, raked edge 2.84; 0.90 m void open, 2 slim Ø16 stainless hangers to the tall wall; 2 columns against the garden wall.
Roof fixed to the annex end façade (ledger). The 0.90 m passage to the lattice door stays open.
Void edge hung from the tall house wall on 2 Ø16 stainless rods (lumbuckles, wall plates) — slim, almost invisible.
Triangle: plants edge 3.22 + 1.26 = 4.48 m, raked edge 2.84 m at 63.6° to the plants edge.
C1 in the middle of the 4.48 edge (2.24 from the façade); C2 0.60 m in from the tip (the tip cantilevers 0.60).
Joists run from the annex ledger to the raked edge beam (max. span = 4.2 m).
COMMON
Annex side wall and low white garden wall are ONE line; the roof's plants edge (fascia) is on it.
Planter 0.70 inside the wall (soil + white kerb), continues along the wall; paved entry space 1.00 between the façade and the planter (walk in to the left glass door).
Entrance opening runs to the side wall (no pier).
C1 / C2: SHS 150 clad 200x200 thermo-ash, against the garden wall, 2 SS brackets each into the wall; edge beam on the column line, roof cantilevers 0.30 to the fascia over the wall.
Underside +2.36, fascia 0.43 (top +2.79); columns 0.13 above roof. Falls 1.70 to the box gutter on the raked edge; rainwater down C2.

3/V2T-01 3D — BIRD'S EYE (from outside, over the low garden wall)

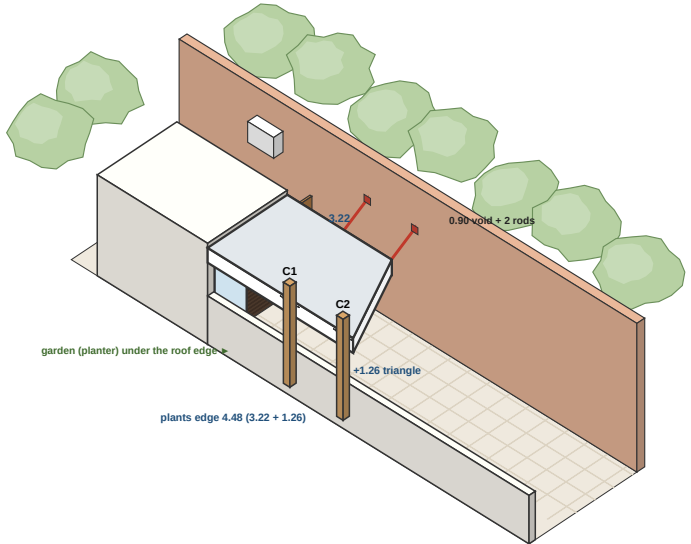

COURTYARD ROOF — V2T

VERSION 2T — TRIANGLE, 0.90 m VOID + 2 RODS: triangular roof: plants edge 3.22 + 1.26 = 4.48, void edge 3.22, raked edge 2.84; 0.90 m void open, 2 slim Ø16 stainless hangers to the tall wall; 2 columns against the garden wall
Client: Owner / Client
Design & drawings: Claude Code

DRAWING NOTES

- Do not scale from this drawing. Use figured dimensions only.
- All dimensions in millimetres; levels in metres relative to internal FFL ± 0.000 (datum to be tied to site survey).
- Contractor to verify all dimensions, levels & existing structure on site before fabrication or ordering.
- Read with all other architectural, structural & services drawings and the specification notes (A-001).
- Structural members are preliminary: final design, connections & calculations by a licensed structural engineer to local code before construction.
- Report any discrepancy to the designer before proceeding.

REVISIONS

Rev	Date	Description
C13	07.10.2026	Planter 0.70 (-30 %), soil only, no bushes; garden wall continues
C12	07.10.2026	FINAL V2T set: walls in one line, planter 1.00 + entry 1.00, hangers
C11	07.10.2026	Annex side wall + garden wall in one line; roof as sketch

FOR CLIENT CHECK (V2T) — planter 0.70, more paving under the roof; full technical set follows

DRAWING TITLE

V2T TRIANGLE + RODS
top view & roof framing

SCALE @ A3

1:50 / 1:30

DRAWN / CHECKED

CC / —

DATE

07.10.2026

SERIES

ARCHITECTURAL

DRAWING No.


V2T-01

REV


C13

VERSION 2T — TRIANGLE, 0.90 m VOID + 2 RODS

1/V2T-02 VIEW TO ANNEX FAÇADE (as site photo) — 1:50

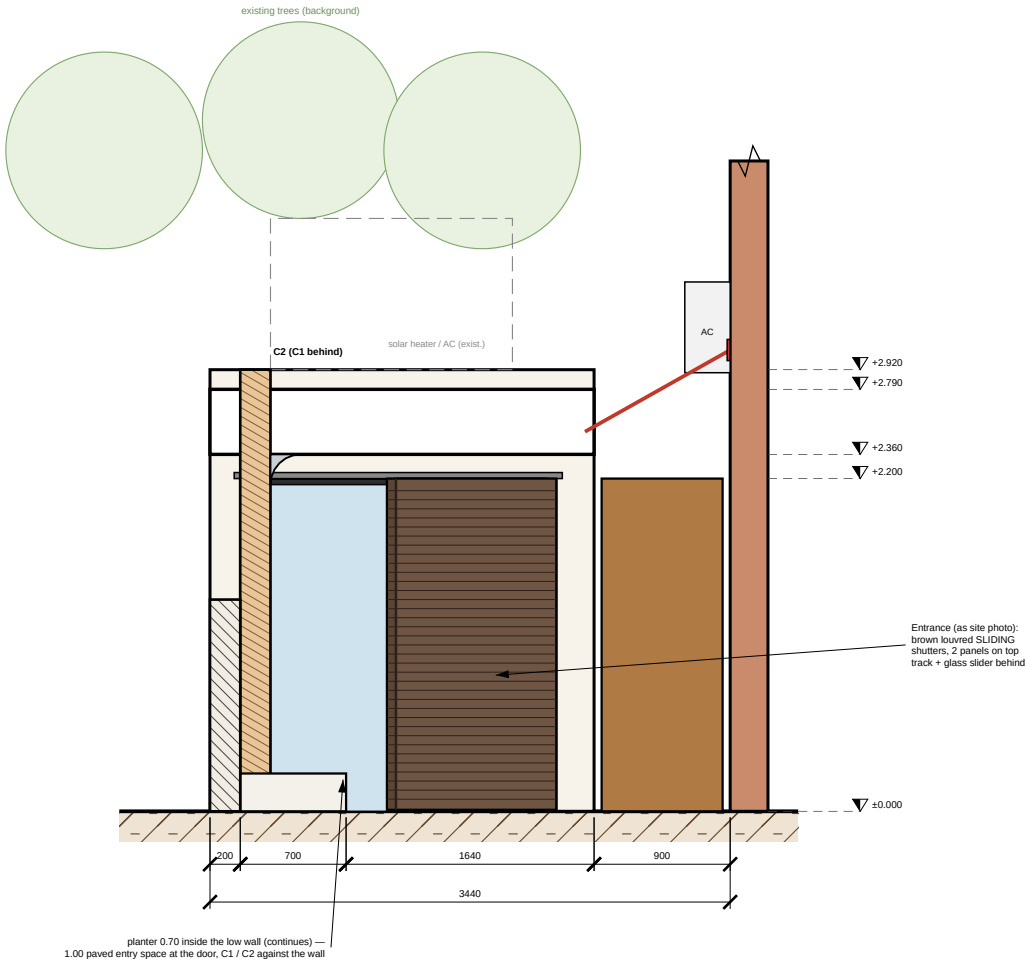


2/V2T-02 PLANTS-SIDE ELEVATION — C1 + C2 — 1:50 (plants edge 3.22 + 1.26 = 4.48)

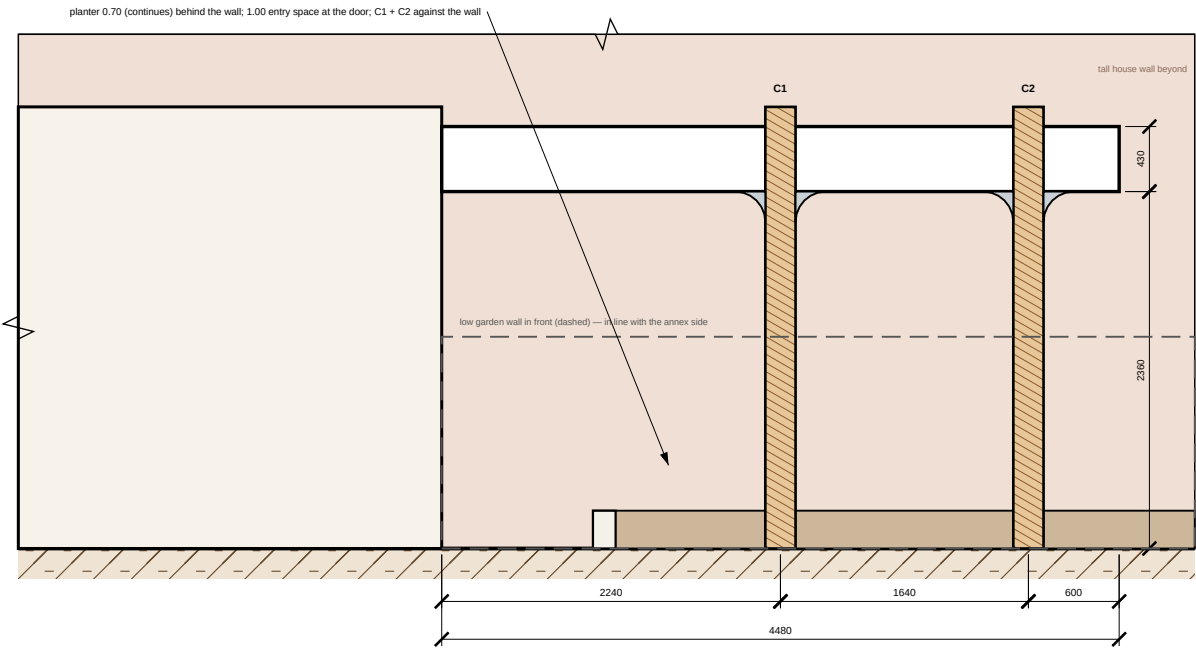


NOTES
triangular roof: plants edge 3.22 + 1.26 = 4.48, void edge 3.22, raked edge 2.84; 0.90 m void open, 2 slim Ø16 stainless hangers to the tall wall; 2 columns against the garden wall.
Underside +2.36, fascia 0.43 (top +2.79); columns 0.13 above roof.
Annex side wall + low garden wall in one line (roof edge on it). Planter 0.70 inside the wall, continues; 1.00 paved entry space at the door; C1 + C2 against the wall. Trees are existing, in the background.
Refined roof section & details: sheet V2T-03.

3/V2T-02 SECTION ACROSS AT C1 — 1:50 (refined: V2T-03)

tall wall left — garden wall right

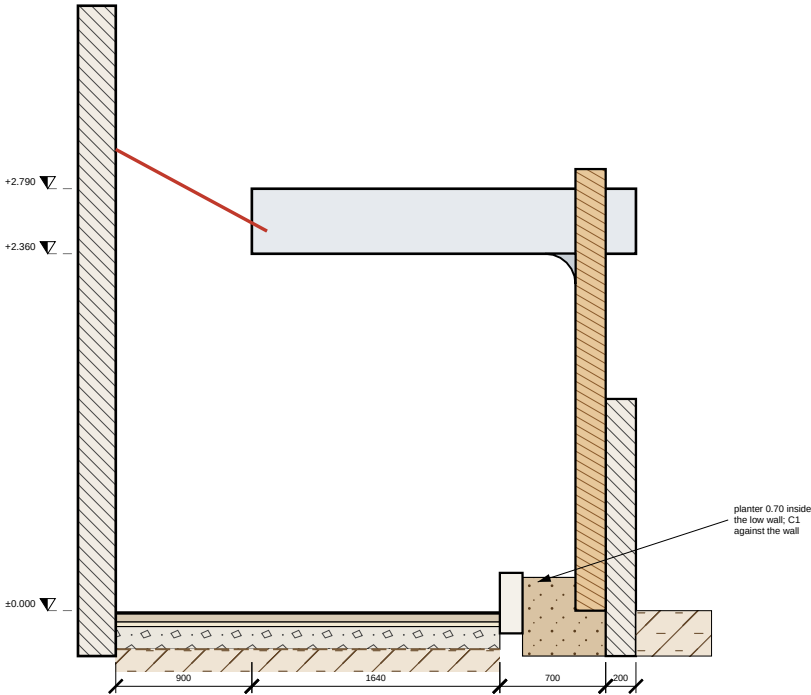

4/V2T-02 3D — EYE LEVEL, SAME DIRECTION AS THE SITE PHOTO

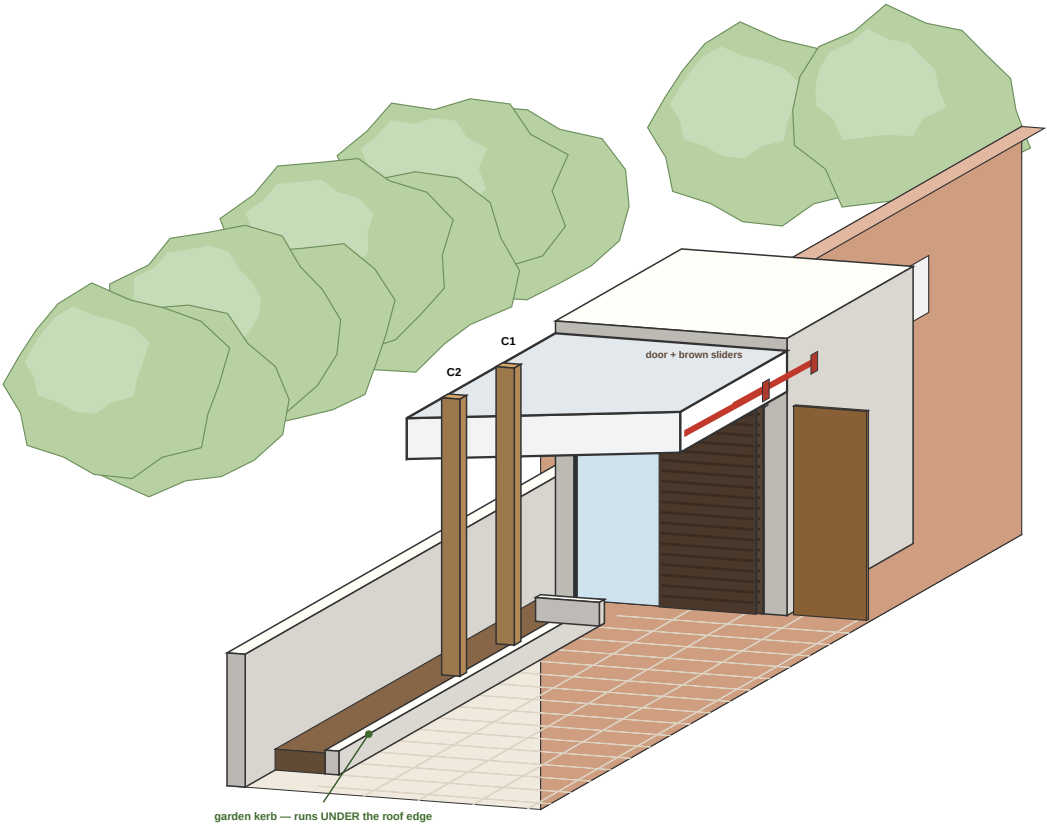

COURTYARD ROOF — V2T

VERSION 2T — TRIANGLE, 0.90 m VOID + 2 RODS: triangular roof: plants edge 3.22 + 1.26 = 4.48, void edge 3.22, raked edge 2.84; 0.90 m void open, 2 slim Ø16 stainless hangers to the tall wall; 2 columns against the garden wall
Client: Owner / Client
Design & drawings: Claude Code

- DRAWING NOTES**
- Do not scale from this drawing. Use figured dimensions only.
 - All dimensions in millimetres; levels in metres relative to internal FFL ±0.000 (datum to be tied to site survey).
 - Contractor to verify all dimensions, levels & existing structure on site before fabrication or ordering.
 - Read with all other architectural, structural & services drawings and the specification notes (A-001).
 - Structural members are preliminary: final design, connections & calculations by a licensed structural engineer to local code before construction.
 - Report any discrepancy to the designer before proceeding.

REVISIONS		
Rev	Date	Description
C13	07.10.2026	Planter 0.70 (-30 %), soil only, no bushes; garden wall continues
C12	07.10.2026	FINAL V2T set: walls in one line, planter 1.00 + entry 1.00, hangers
C11	07.10.2026	Annex side wall + garden wall in one line; roof as sketch

FOR CLIENT CHECK (V2T) — planter 0.70, more paving under the roof; full technical set follows

DRAWING TITLE	
V2T TRIANGLE + RODS views, section & 3D view	
SCALE @ A3 1:50	DATE 07.10.2026
DRAWN / CHECKED CC / —	SERIES ARCHITECTURAL


DRAWING No. REV

V2T-02 C13


VERSION 2T — TRIANGLE, 0.90 m VOID + 2 RODS

1/V2T-03 ROOF SECTION ACROSS AT C1 — 1:25


(as client sketch B: roof stops, rods to the wall)

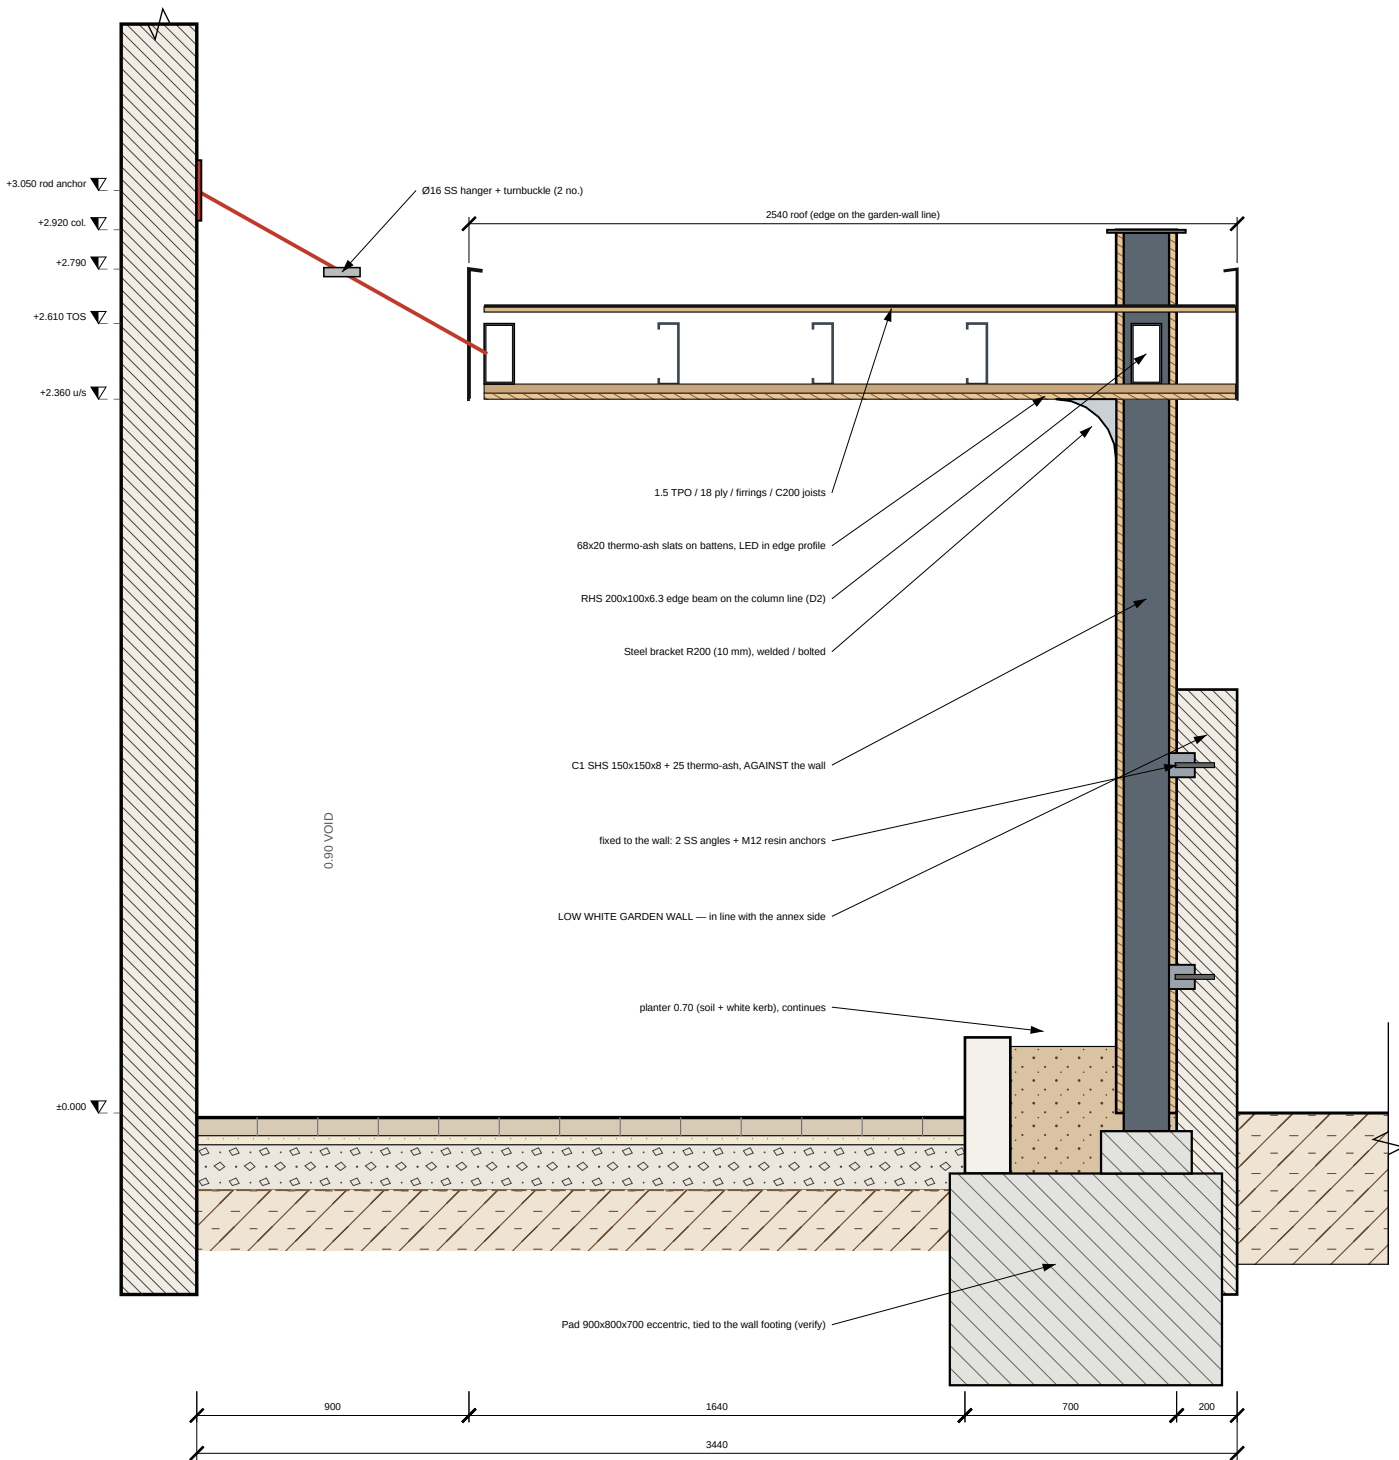


SPECIFICATION
Steel S355, hot-dip galvanised; columns & brackets powder-coated RAL 9010 or timber-clad (thermo-ash).
Roof: TPO 1.5 on 18 mm marine ply on tapered firings (fall 1:70 to the free-edge box gutter).
Soffit: thermo-ash 68x20 slats, LED 2700 K in perimeter profile. Fascia 3 mm aluminium RAL 9010, 0.43 m.
Rods: Ø16 stainless 316, fork ends, turnbuckle, = 30° rise; engineer to confirm wall anchors.

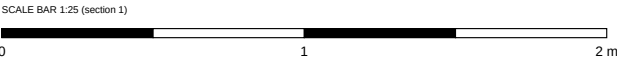


D1 ROD TO WALL (client sketch B) — 1:20

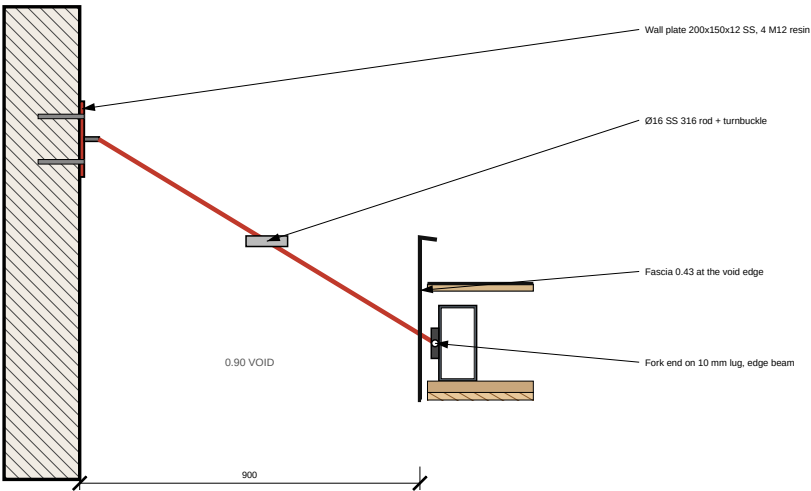

D2 COLUMN / ROOF JUNCTION (plants side) — 1:15

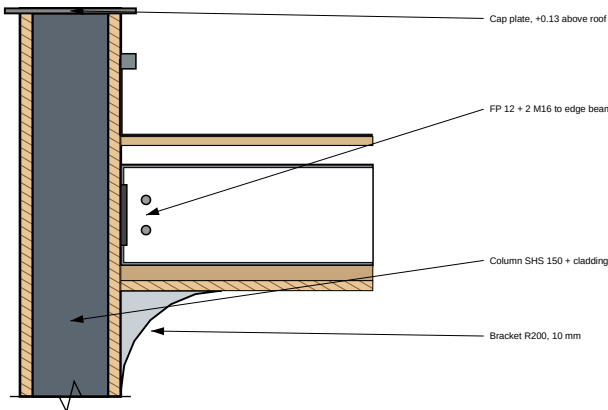

D3 TIP AT C2 (triangle) — PLAN 1:15

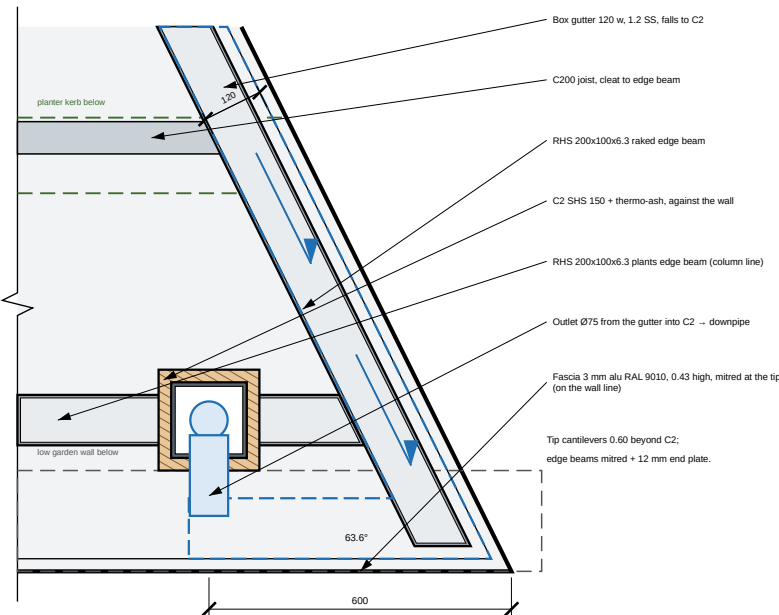

COURTYARD ROOF — V2T

VERSION 2T — TRIANGLE, 0.90 m VOID + 2 RODS: triangular roof: plants edge 3.22 + 1.26 = 4.48, void edge 3.22, raked edge 2.84; 0.90 m void open, 2 slim Ø16 stainless hangers to the tall wall; 2 columns against the garden wall
Client: Owner / Client
Design & drawings: Claude Code

DRAWING NOTES

- Do not scale from this drawing. Use figured dimensions only.
- All dimensions in millimetres; levels in metres relative to internal FFL ±0.000 (datum to be tied to site survey).
- Contractor to verify all dimensions, levels & existing structure on site before fabrication or ordering.
- Read with all other architectural, structural & services drawings and the specification notes (A-001).
- Structural members are preliminary: final design, connections & calculations by a licensed structural engineer to local code before construction.
- Report any discrepancy to the designer before proceeding.

REVISIONS

Rev	Date	Description
C13	07.10.2026	Planter 0.70 (-30 %), soil only, no bushes; garden wall continues
C12	07.10.2026	FINAL V2T set: walls in one line, planter 1.00 + entry 1.00, hangers
C11	07.10.2026	Annex side wall + garden wall in one line; roof as sketch

FOR CLIENT CHECK (V2T) — planter 0.70, more paving under the roof; full technical set follows

DRAWING TITLE

V2T TRIANGLE + RODS
roof section & details

SCALE @ A3

1:25 / 1:15 / 1:20

DRAWN / CHECKED

CC / —

DATE

07.10.2026

SERIES

ARCHITECTURAL

DRAWING No.

V2T-03

REV

C13