



GARDEN EDGE — CORRECTED SHAPE (2nd round)

1 SECTION ACROSS AT C1 — 1:25


tall house wall LEFT — garden RIGHT

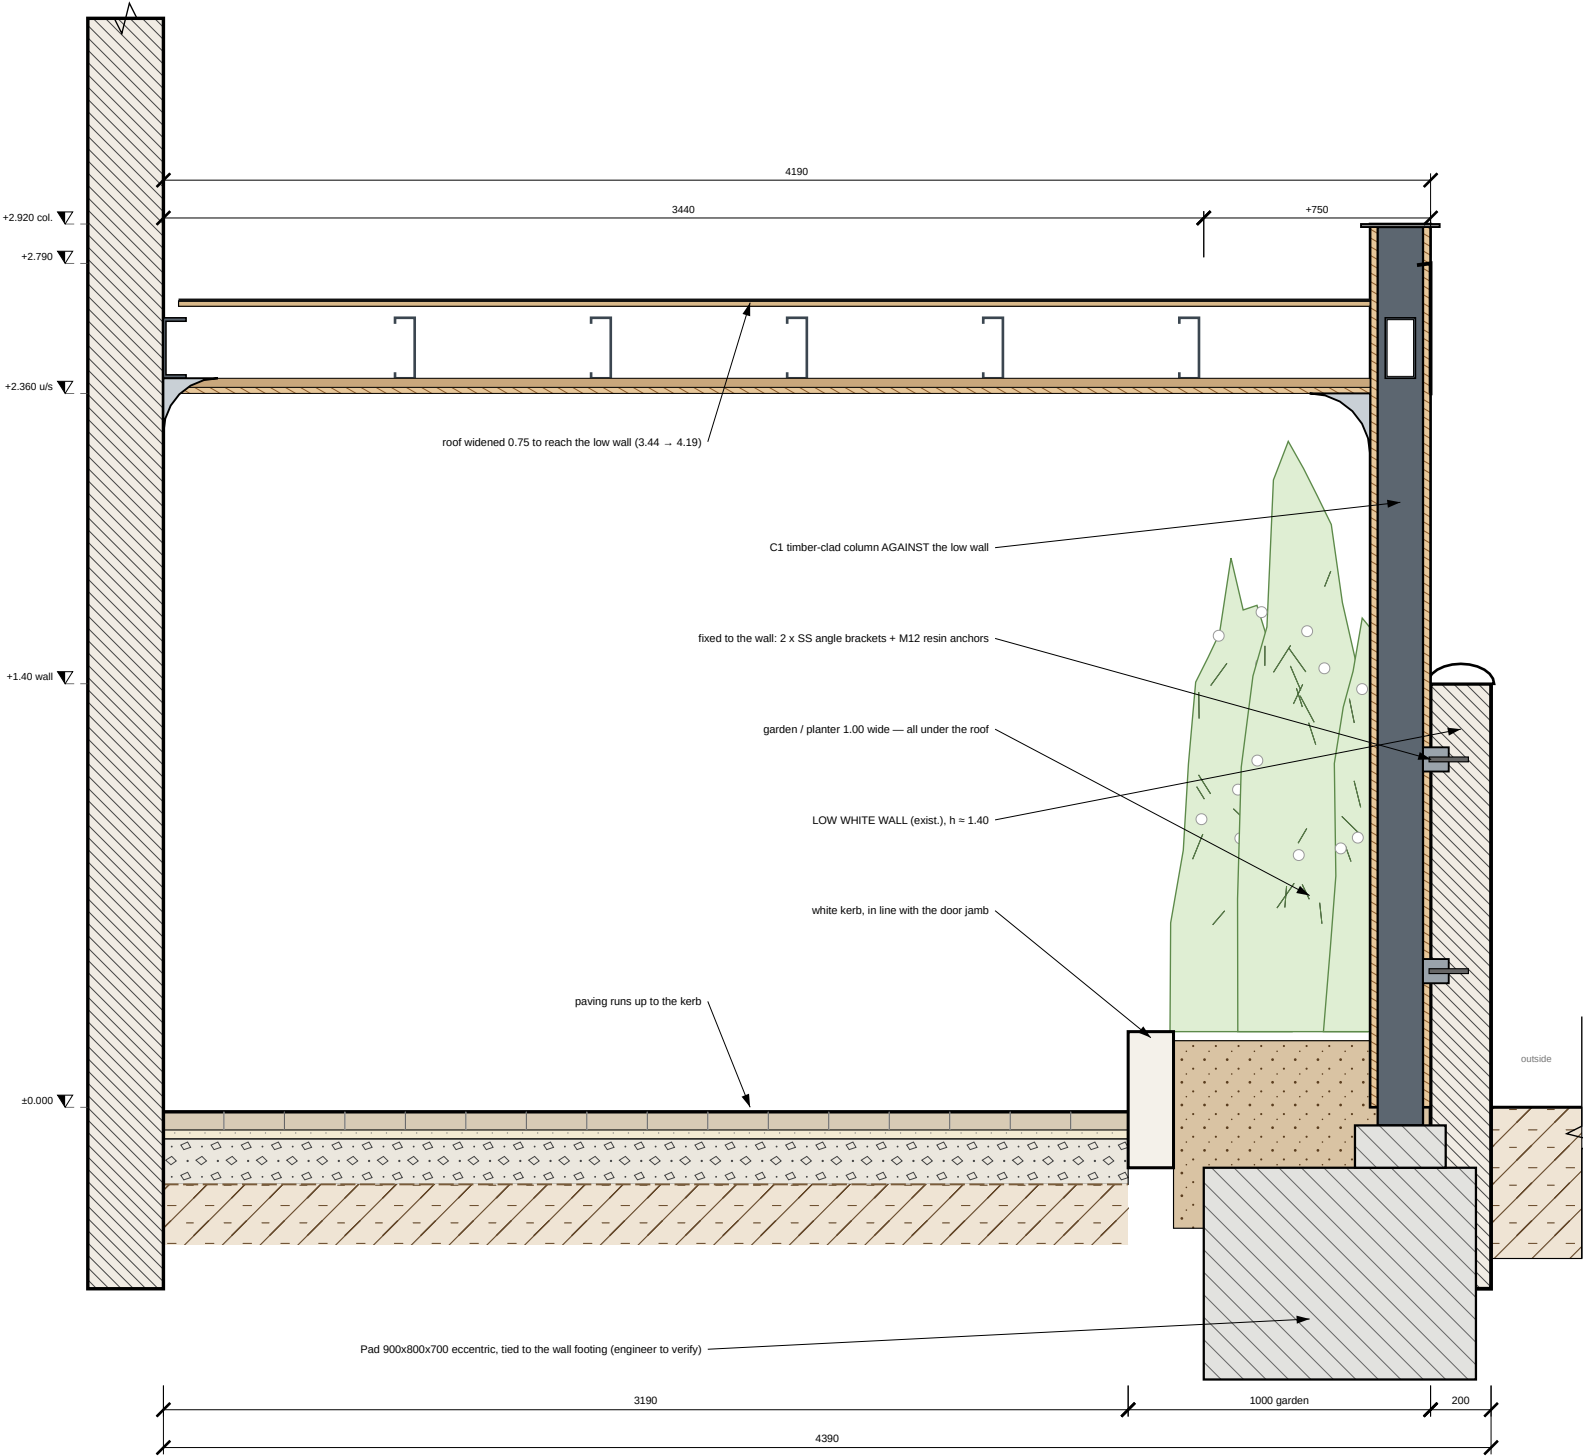

2 KEY PLAN — 1:100 (V1 shown; same edge for all)

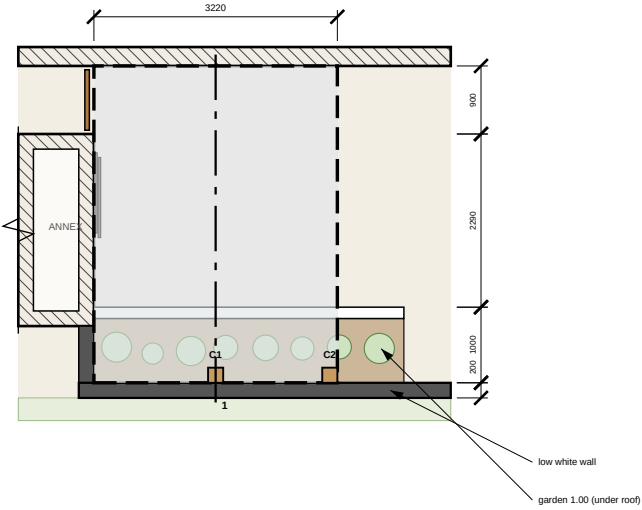

3 3D — SAME DIRECTION AS THE SITE PHOTO

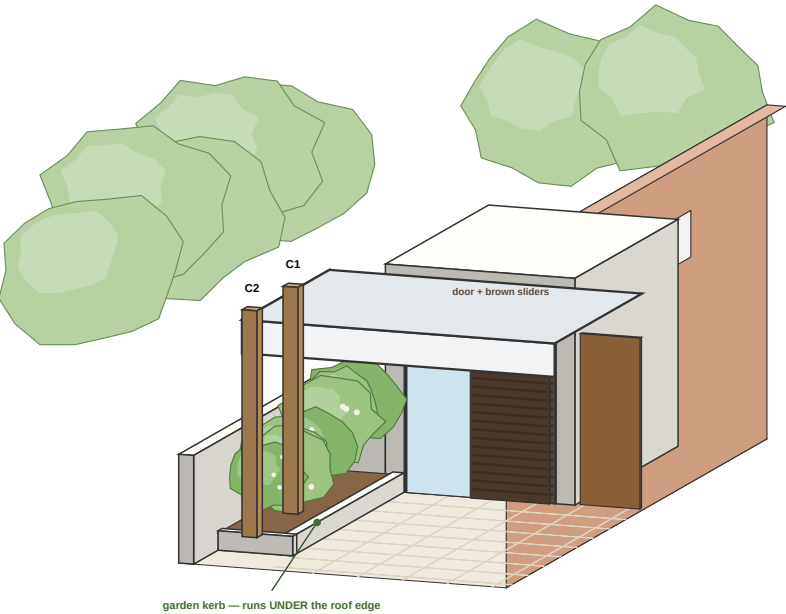

WHAT CHANGED (your comments on C07)
Garden / planter is double: 1.00 m from the kerb (door-jamb line) to the low white wall.
The timber-clad columns stand against the low wall and are fixed to it (2 SS brackets each).
So the roof edge comes out to the wall: +0.75 m (V1 3.44 to 4.19, V2 2.54 to 3.29); the whole planter is under the roof.
PLEASE CONFIRM
OK like this? Or should the roof stay 3.44 with only the columns at the wall? Then all 12 sheets follow.

COURTYARD ROOF — GARDEN EDGE

Kerb -> 1.00 m planter -> low white wall; timber-clad columns against the wall and fixed to it; roof edge out to the wall, whole planter under the roof.
Client: Owner / Client
Design & drawings: Claude Code

- DRAWING NOTES**
- Do not scale from this drawing. Use figured dimensions only.
 - All dimensions in millimetres; levels in metres relative to internal FFL ±0.000 (datum to be tied to site survey).
 - Contractor to verify all dimensions, levels & existing structure on site before fabrication or ordering.
 - Read with all other architectural, structural & services drawings and the specification notes (A-001).
 - Structural members are preliminary: final design, connections & calculations by a licensed structural engineer to local code before construction.
 - Report any discrepancy to the designer before proceeding.

REVISIONS		
Rev	Date	Description
C08	07.10.2026	Planter 1.00 wide; columns against + fixed to the low wall; roof to wall
C07	07.10.2026	Low white wall moved in, directly behind the planter
C06	07.10.2026	Garden = planter in front of the façade, left of the door, partly under roof
C05	07.10.2026	Triangular versions V1T/V2T; 3D views; details D3

FOR CLIENT CONFIRMATION — shape only; full set follows once confirmed

DRAWING TITLE
**GARDEN EDGE — corrected shape
section, key plan & 3D**

SCALE @ A3 1:25 / 1:100	DATE 07.10.2026
DRAWN / CHECKED CC / —	SERIES ARCHITECTURAL

DRAWING No. REV

C08-01 **C08**