


VERSION 2T — TRIANGLE, 0.90 m VOID + 2 RODS


TALL HOUSE WALL (exist., AC units)

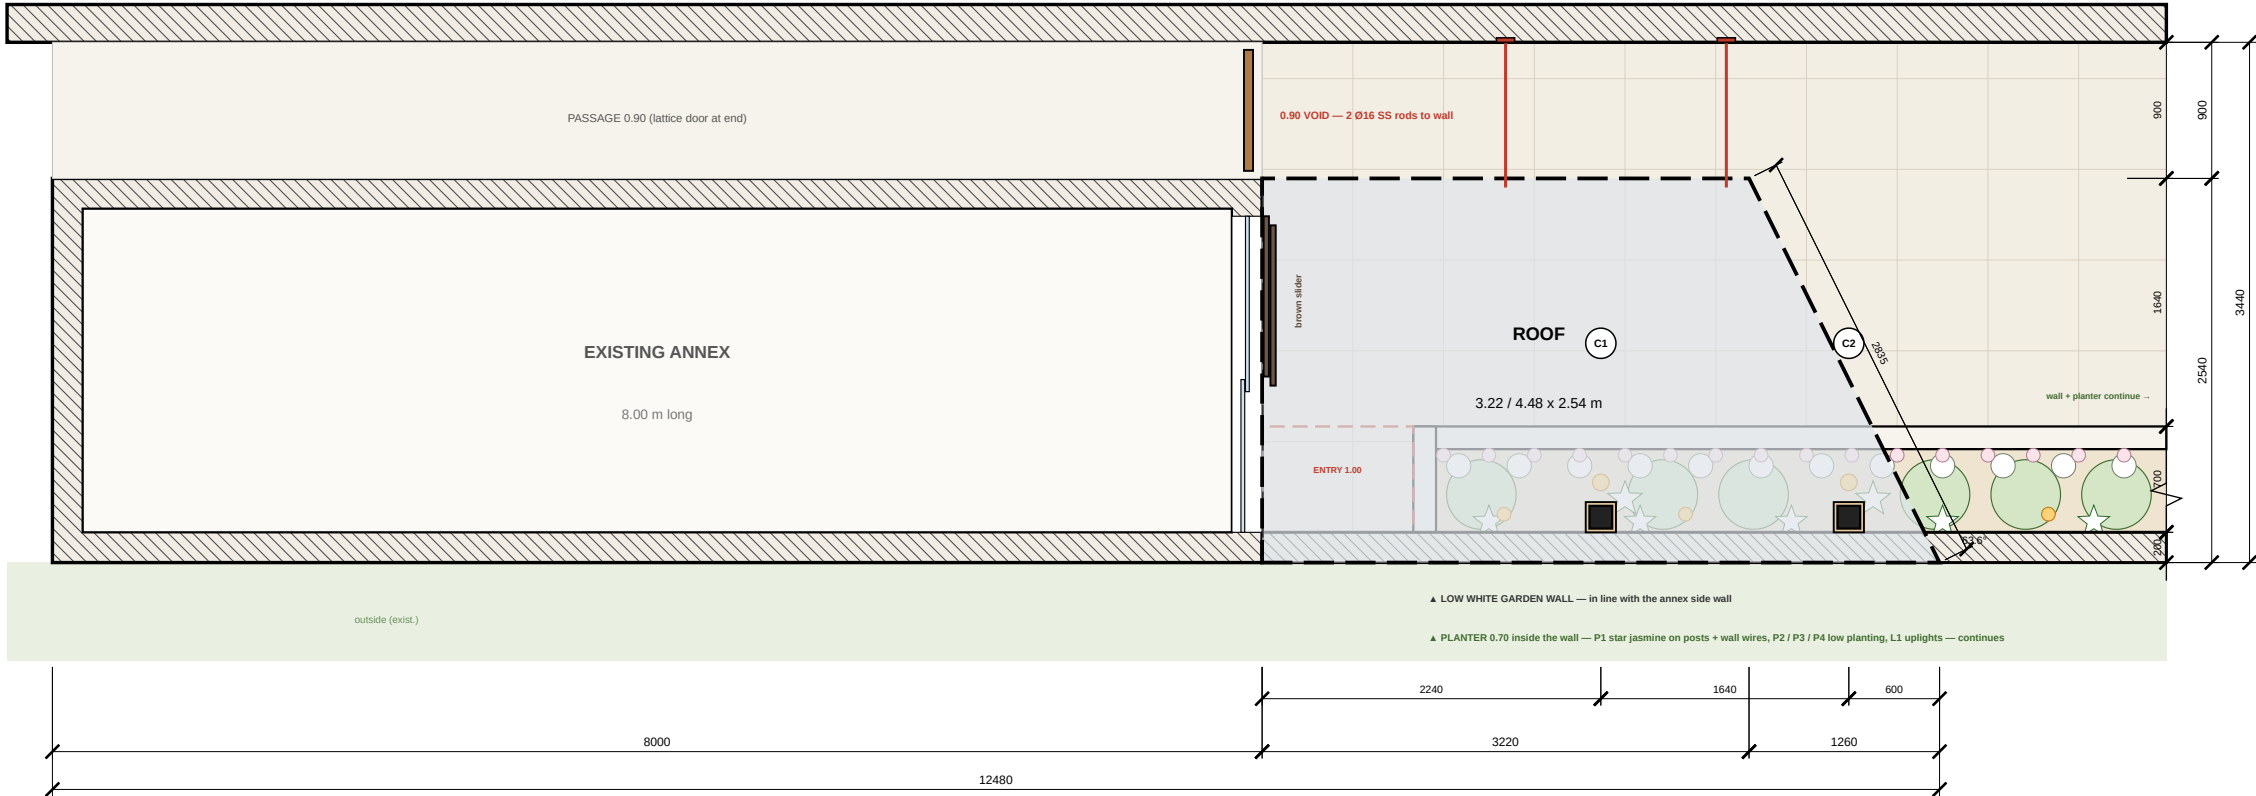

1 TOP VIEW — ANNEX, GARDEN & ROOF


V2T-01 1:50 @ A3 — annex + garden wall in one line; planter 0.70 continues; entry 1.00 at the door

2/V2T-01 ROOF FRAMING PLAN — 1:30

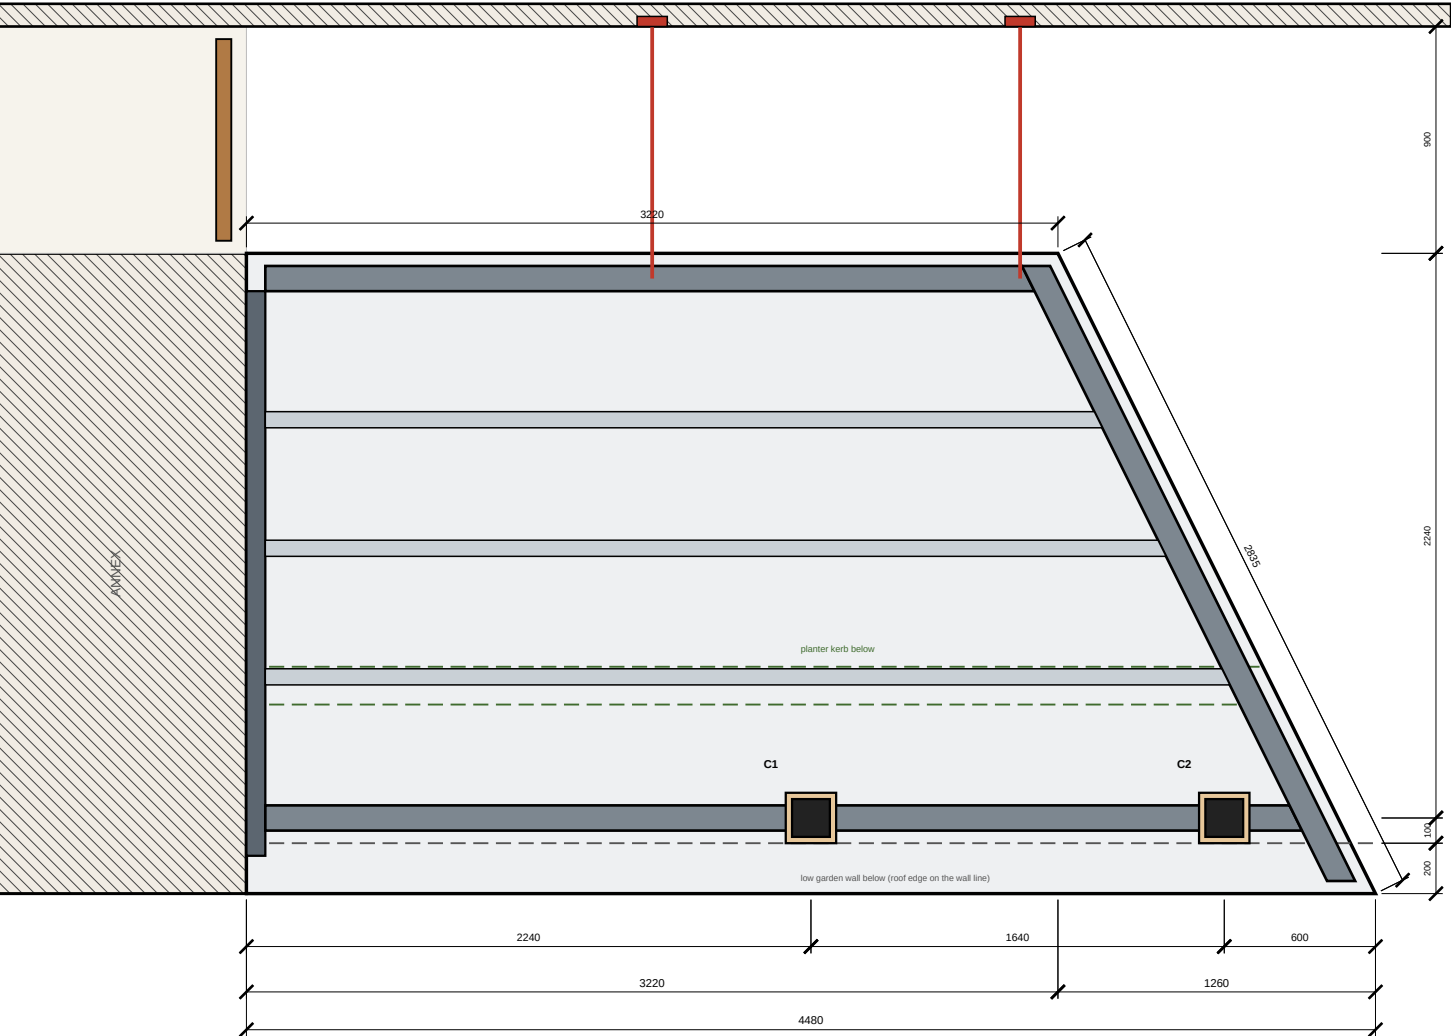

THIS VERSION
triangular roof: plants edge 3.22 + 1.26 = 4.48, void edge 3.22, raked edge 2.84; 0.90 m void open, 2 slim Ø16 stainless hangers to the tall wall; 2 columns against the garden wall.
Roof fixed to the annex end façade (ledger). The 0.90 m passage to the lattice door stays open.
Void edge hung from the tall house wall on 2 Ø16 stainless rods (lumbuckles, wall plates) — slim, almost invisible.
Triangle: plants edge 3.22 + 1.26 = 4.48 m; raked edge 2.84 m at 63.6° to the plants edge.
C1 in the middle of the 4.48 edge (2.24 from the façade); C2 0.60 m in from the tip (the tip cantilevers 0.60).
Joists run from the annex ledger to the raked edge beam (max. span = 4.2 m).
COMMON
Annex side wall and low white garden wall are ONE line; the roof's plants edge (fascia) is on it.
Planter 0.70 inside the wall (soil + white kerb), continues along the wall; paved entry space 1.00 between the façade and the planter (walk in to the left glass door).
Entrance opening runs to the side wall (no pier).
C1 / C2: SHS 150 clad 200x200 thermo-ash, against the garden wall, 2 SS brackets each into the wall; edge beam on the column line, roof cantilevers 0.30 to the fascia over the wall.
Underside +2.36, fascia 0.43 (top +2.79); columns 0.13 above roof. Falls 1:70 to the box gutter on the raked edge; rainwater down C2.

3/V2T-01 3D — BIRD'S EYE (from outside, over the low garden wall)

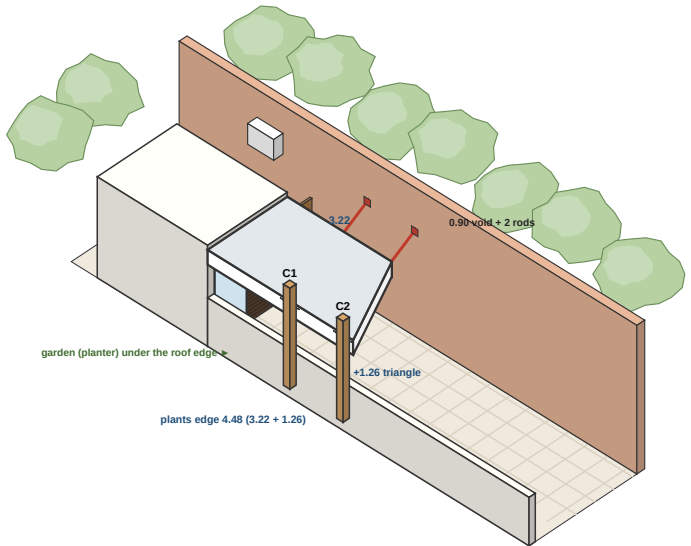

COURTYARD ROOF — V2T

VERSION 2T — TRIANGLE, 0.90 m VOID + 2 RODS: triangular roof: plants edge 3.22 + 1.26 = 4.48, void edge 3.22, raked edge 2.84; 0.90 m void open, 2 slim Ø16 stainless hangers to the tall wall; 2 columns against the garden wall
Client: Owner / Client
Design & drawings: Claude Code

DRAWING NOTES

- Do not scale from this drawing. Use figured dimensions only.
- All dimensions in millimetres; levels in metres relative to internal FFL ± 0.000 (datum to be tied to site survey).
- Contractor to verify all dimensions, levels & existing structure on site before fabrication or ordering.
- Read with all other architectural, structural & services drawings and the specification notes (A-001).
- Structural members are preliminary: final design, connections & calculations by a licensed structural engineer to local code before construction.
- Report any discrepancy to the designer before proceeding.

REVISIONS

Rev	Date	Description
T01	07.10.2026	FINAL technical design V2T (minimal set) — for tender & construction
C14	07.10.2026	Planting per client reference: jasmine, low shrubs, uprights
C13	07.10.2026	Planter 0.70, soil + low planting; garden wall continues

FINAL TECHNICAL DESIGN — for tender & construction. Structure subject to licensed engineer's sign-off; verify all dimensions on site

DRAWING TITLE

V2T TRIANGLE + RODS
top view & roof framing


SCALE @ A3 1:50 / 1:30	DATE 07.10.2026
DRAWN / CHECKED CC / —	SERIES ARCHITECTURAL

DRAWING No. REV


V2T-01 T01

VERSION 2T — TRIANGLE, 0.90 m VOID + 2 RODS

1/V2T-02 VIEW TO ANNEX FAÇADE (as site photo) — 1:50

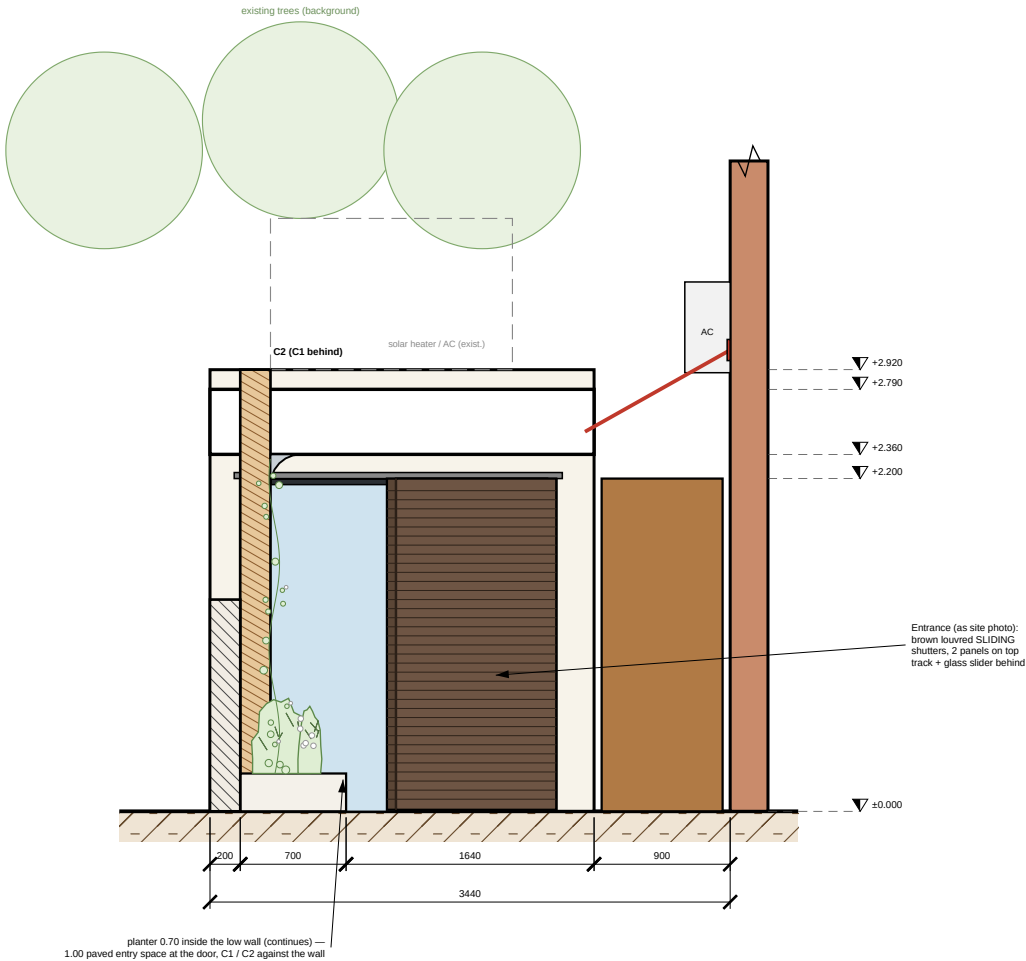


2/V2T-02 PLANTS-SIDE ELEVATION — C1 + C2 — 1:50 (plants edge 3.22 + 1.26 = 4.48)

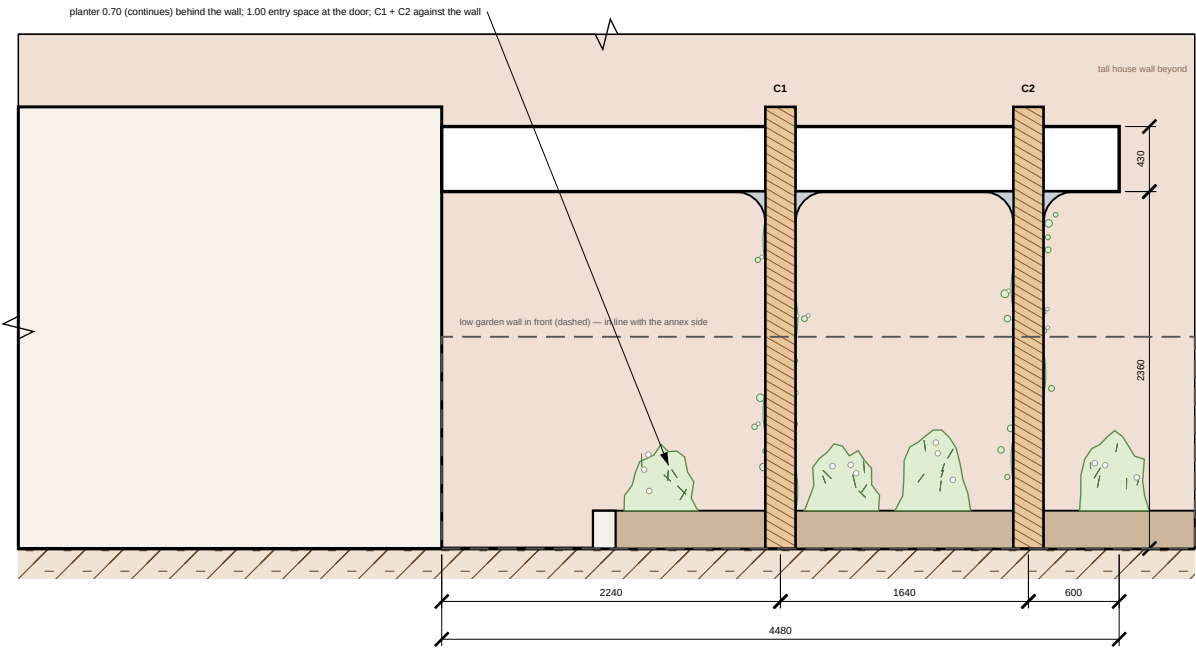


NOTES
triangular roof: plants edge 3.22 + 1.26 = 4.48, void edge 3.22, raked edge 2.84; 0.90 m void open, 2 slim Ø16 stainless hangers to the tall wall; 2 columns against the garden wall.
Underside +2.36, fascia 0.43 (top +2.79); columns 0.13 above roof.
Annex side wall + low garden wall in one line (roof edge on it). Planter 0.70 inside the wall, continues; 1.00 paved entry space at the door; C1 + C2 against the wall. Trees are existing, in the background.
Refined roof section & details: sheet V2T-03.

3/V2T-02 SECTION ACROSS AT C1 — 1:50 (refined: V2T-03)

tall wall left — garden wall right

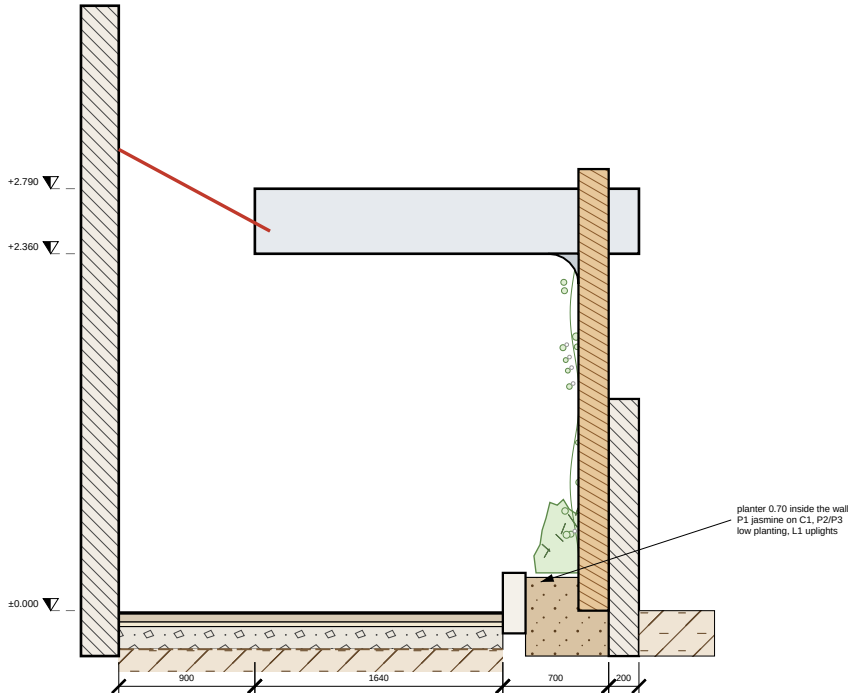

4/V2T-02 3D — EYE LEVEL, SAME DIRECTION AS THE SITE PHOTO

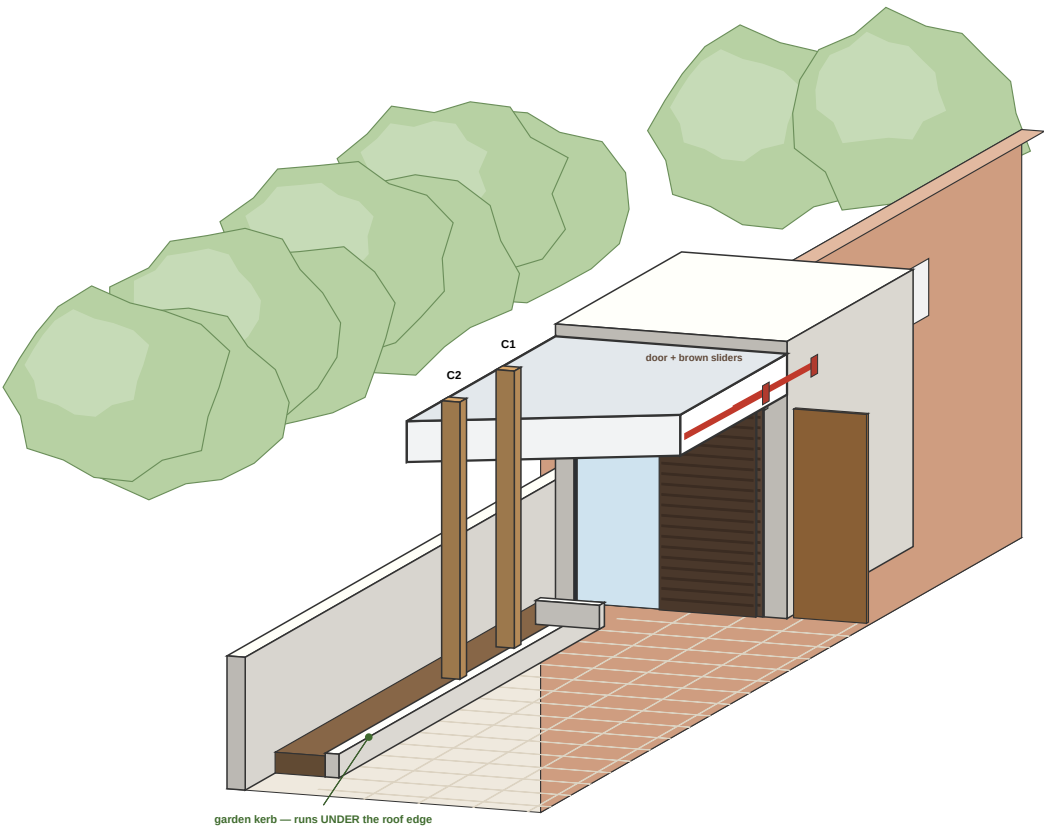

COURTYARD ROOF — V2T

VERSION 2T — TRIANGLE, 0.90 m VOID + 2 RODS: triangular roof: plants edge 3.22 + 1.26 = 4.48, void edge 3.22, raked edge 2.84; 0.90 m void open, 2 slim Ø16 stainless hangers to the tall wall; 2 columns against the garden wall
Client: Owner / Client
Design & drawings: Claude Code

DRAWING NOTES

- Do not scale from this drawing. Use figured dimensions only.
- All dimensions in millimetres; levels in metres relative to internal FFL ±0.000 (datum to be tied to site survey).
- Contractor to verify all dimensions, levels & existing structure on site before fabrication or ordering.
- Read with all other architectural, structural & services drawings and the specification notes (A-001).
- Structural members are preliminary: final design, connections & calculations by a licensed structural engineer to local code before construction.
- Report any discrepancy to the designer before proceeding.

REVISIONS

Rev	Date	Description
T01	07.10.2026	FINAL technical design V2T (minimal set) — for tender & construction
C14	07.10.2026	Planting per client reference: jasmine, low shrubs, uplights
C13	07.10.2026	Planter 0.70, soil + low planting; garden wall continues

FINAL TECHNICAL DESIGN — for tender & construction. Structure subject to licensed engineer's sign-off; verify all dimensions on site

DRAWING TITLE

V2T TRIANGLE + RODS
views, section & 3D view

SCALE @ A3 1:50	DATE 07.10.2026
DRAWN / CHECKED CC / —	SERIES ARCHITECTURAL


DRAWING No. REV

V2T-02 T01

VERSION 2T — TRIANGLE, 0.90 m VOID + 2 RODS

1/V2T-03 ROOF SECTION ACROSS AT C1 — 1:25

(as client sketch B: roof stops, rods to the wall)

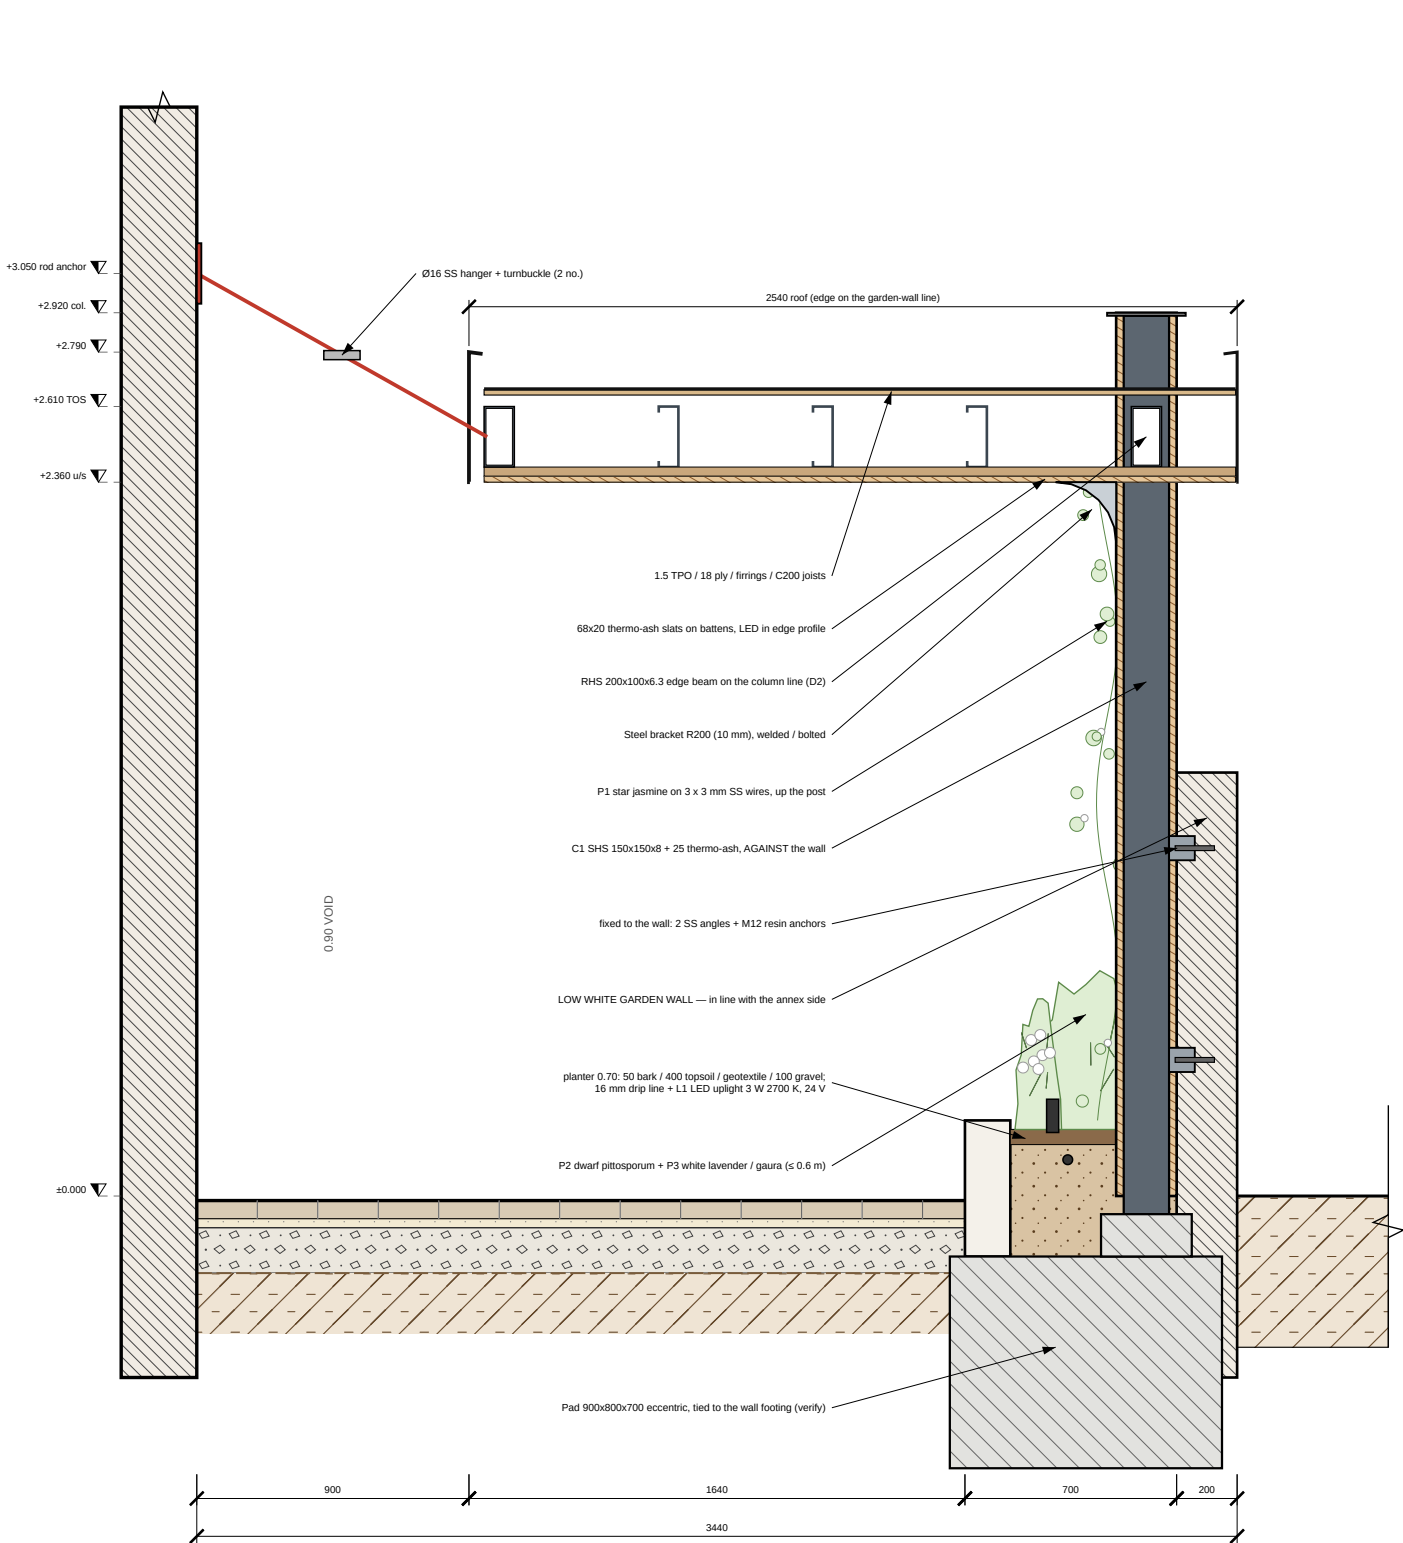


SPECIFICATION
Steel S355, hot-dip galvanised; columns & brackets powder-coated RAL 9010 or timber-clad (thermo-ash).
Roof: TPO 1.5 on 18 mm marine ply on tapered firings (fall 1:70 to the free-edge box gutter).
Soffit: thermo-ash 68x20 slats, LED 2700 K in perimeter profile. Fascia 3 mm aluminium RAL 9010, 0.43 m.
Rods: Ø16 stainless 316, fork ends, turnbuckle, = 30° rise; engineer to confirm wall anchors.


SCALE BAR 1:25 (section 1)




D1 ROD TO WALL (client sketch B) — 1:20

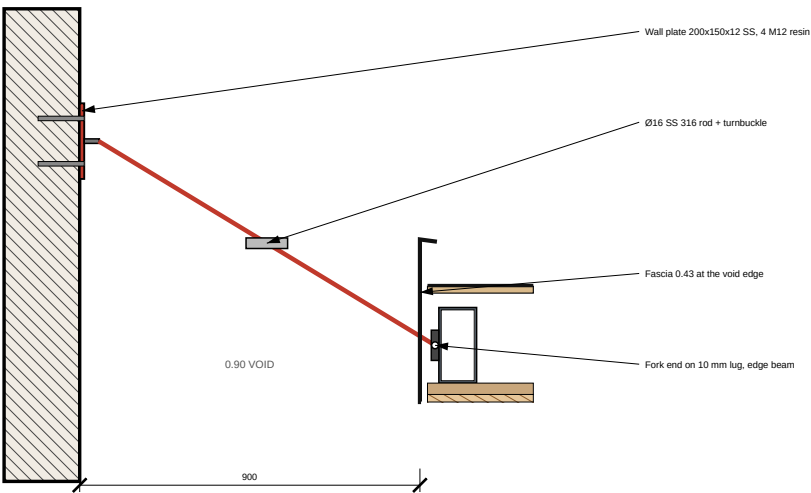

D2 COLUMN / ROOF JUNCTION (plants side) — 1:15

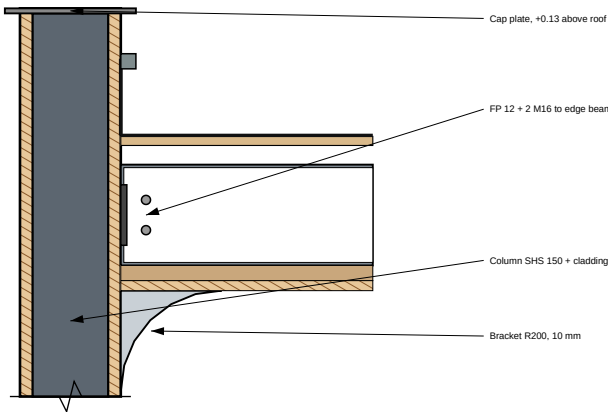

D3 TIP AT C2 (triangle) — PLAN 1:15

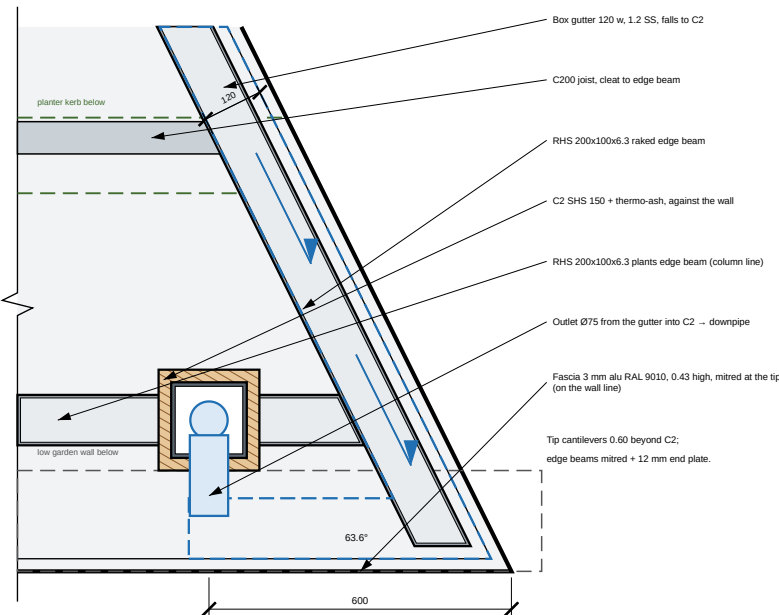

COURTYARD ROOF — V2T

VERSION 2T — TRIANGLE, 0.90 m VOID + 2 RODS: triangular roof: plants edge 3.22 + 1.26 = 4.48, void edge 3.22, raked edge 2.84; 0.90 m void open, 2 slim Ø16 stainless hangers to the tall wall; 2 columns against the garden wall
Client: Owner / Client
Design & drawings: Claude Code

DRAWING NOTES

- Do not scale from this drawing. Use figured dimensions only.
- All dimensions in millimetres; levels in metres relative to internal FFL ±0.000 (datum to be tied to site survey).
- Contractor to verify all dimensions, levels & existing structure on site before fabrication or ordering.
- Read with all other architectural, structural & services drawings and the specification notes (A-001).
- Structural members are preliminary: final design, connections & calculations by a licensed structural engineer to local code before construction.
- Report any discrepancy to the designer before proceeding.

REVISIONS

Rev	Date	Description
T01	07.10.2026	FINAL technical design V2T (minimal set) — for tender & construction
C14	07.10.2026	Planting per client reference: jasmine, low shrubs, uplights
C13	07.10.2026	Planter 0.70, soil + low planting; garden wall continues

FINAL TECHNICAL DESIGN — for tender & construction. Structure subject to licensed engineer's sign-off; verify all dimensions on site

DRAWING TITLE

V2T TRIANGLE + RODS
roof section & details

SCALE @ A3

1:25 / 1:15 / 1:20

DRAWN / CHECKED

CC / —

DRAWING No.

V2T-03

DATE

07.10.2026

SERIES

ARCHITECTURAL

REV

T01



1 EVENING — LED soffit + uplights (as client reference)



2 DAY — same view as the site photo

STEEL & MEMBER SCHEDULE

Mark	Member	Section	Material / finish	Length · qty	Connection
B1	Ledger on annex end facade	UPN 200	S275JR HDG	2240 · 1 no.	V2T-03 sect. 1 — M12 A4 resin @ 400
B2	Plants-edge beam on C1 / C2	RHS 200x100x6.3	S355J2H HDG + PPC	= 4090 · 1 no.	V2T-03 D2 — FP 12 + 2 M16
B3	Void-edge beam (hung from H1/H2)	RHS 200x100x6.3	S355J2H HDG + PPC	= 3030 · 1 no.	V2T-03 D1 — 10 mm fork lugs
B4	Raked-edge beam (gutter side)	RHS 200x100x6.3	S355J2H HDG + PPC	= 2720 · 1 no.	V2T-03 D3 — mitred, 12 mm end plate
J1-J3	Roof joists, ledger -> raked beam	C200x65x1.8 lipped	S350GD+Z275	3.30 / 3.56 / 3.81 m	cleats, 2 M12 each end
C1, C2	Columns against the garden wall	SHS 150x150x8	S355J2H HDG + PPC	2920 · 2 no.	V2T-03 sect. 1 + D2
BR	Curved knee brackets R200	PL 10, R 200	S355 HDG + PPC	3 no.	V2T-03 D2 — welded / 2 M16
H1, H2	Hangers to the tall wall	Ø16 rod + fork ends + turnbuckle	stainless 1.4401 (316)	= 1140 @ 28" · 2 no.	V2T-03 D1
WP	Hanger wall plates	PL 200x150x12	stainless 1.4401	2 no.	V2T-03 D1 — 4 M12 A4 resin each
WA	Column-to-wall angles	L 100x100x8 x 150	stainless 1.4401	4 no.	V2T-03 sect. 1 — 2 M12 A4 resin
BP	Column base plates	PL 250x250x15	S355 HDG	2 no.	4 M16 HD anchors into F1/F2
F1, F2	Pad footings (eccentric)	900x800x700	C25/30, XC2, B500C mesh	2 no.	V2T-03 sect. 1 (verify wall footing)

FINISHES

Item	Specification
Fascia	3 mm aluminium, PPC RAL 9010 satin, 430 high, concealed fixings, mitred at the tip
Steel (visible)	HDG + polyester PPC RAL 9010 satin; touch-up zinc-rich + PPC repair
Column cladding	25 mm thermo-ash vertical boards, concealed SS clips, oiled, 200x200 overall
Soffit	68x20 thermo-ash slats @ 90 mm, oiled, on 25x50 battens; black fleece
Roof	TPO 1.5 mm RAL 7035; aluminium PPC capping and flashings
Hangers	stainless 1.4401 satin, fork ends + turnbuckle + lock nuts
LED	24 V strip 2700 K, 10 W/m, CRI 90, IP65, in recessed aluminium profile, dimmable
Uplights L1	3 W 2700 K IP67 spike spots, 24 V, anthracite

ROOF BUILD-UP (top → bottom)

- 1.5 mm TPO membrane, light grey RAL 7035, fully adhered, welded seams
- 18 mm WBP marine plywood deck, screwed @ 150 / 300
- tapered timber firrings C24 (fall 1:70 to the box gutter)
- C200x65x1.8 galvanised joists @ = 510 between edge beams
- 25x50 battens + 68x20 thermo-ash soffit slats @ 90 (22 open joint), black fleece behind

PLANTING & LIGHTING SCHEDULE (planter 0.70: 50 bark mulch / 400 topsoil / geotextile / 100 gravel drainage; drip line 16 mm, 2 L/h @ 0.30)

Code	Botanical name	Common name	Size	Spacing	Mature h	Notes
P1	Trachelospermum jasminoides	star jasmine	3 L, 1.0-1.2 m	1 / column + 1.00 m on wall	climber	on 3 mm SS wires (posts: 3 vertical; wall: +0.60 / +1.00 / +1.35)
P2	Pittosporum tobira 'Nana'	dwarf pittosporum	5 L	0.60 m	0.5-0.6 m	middle row
P3	Lavandula ang. 'Edelweiss' / Gaura lindh. white	white lavender / gaura	2 L	0.40 m	0.4-0.5 m	front row, alternating
P4	Erigeron karvinskianus	Mexican daisy	1 L	0.30 m	0.2-0.3 m	kerb edge, trailing
L1	LED spike uplight 3 W 2700 K IP67	uplight	—	1 / column + 1.20 m	—	24 V, driver in annex

Key data: roof 9.78 m² — plants edge 3.22 + 1.26 = 4.48, void edge 3.22, raked edge 2.84 (63.6°), depth 2.54 (edges in line with the annex walls); 0.90 m void open to the tall wall; hangers H1/H2 Ø16 SS = 1.14 m @ 28"; underside +2.36, fascia 0.43 (top +2.79); falls 1:70 to the box gutter on the raked edge, outlet into C2.
Design basis (preliminary, engineer to verify): G 0.50 kN/m² + fascia 0.10 kN/m; Q 0.40 kN/m² (roof not accessible); snow 0.32 kN/m²; wind uplift = 0.7 kN/m² net — hangers act in tension only, under uplift the frame spans unaided (rods slack); seismic: light roof, check anchors.

COURTYARD ROOF — V2T

VERSION 2T — TRIANGLE, 0.90 m VOID + 2 RODS: triangular roof: plants edge 3.22 + 1.26 = 4.48, void edge 3.22, raked edge 2.84; 0.90 m void open, 2 slim Ø16 stainless hangers to the tall wall; 2 columns against the garden wall
Client: Owner / Client
Design & drawings: Claude Code

DRAWING NOTES

- Do not scale from this drawing. Use figured dimensions only.
- All dimensions in millimetres; levels in metres relative to internal FFL ±0.000 (datum to be tied to site survey).
- Contractor to verify all dimensions, levels & existing structure on site before fabrication or ordering.
- Read with all other architectural, structural & services drawings and the specification notes (A-001).
- Structural members are preliminary: final design, connections & calculations by a licensed structural engineer to local code before construction.
- Report any discrepancy to the designer before proceeding.

REVISIONS

Rev	Date	Description
T01	07.10.2026	FINAL technical design V2T (minimal set) — for tender & construction
C14	07.10.2026	Planting per client reference: jasmine, low shrubs, uplights
C13	07.10.2026	Planter 0.70, soil + low planting; garden wall continues

FINAL TECHNICAL DESIGN — for tender & construction. Structure subject to licensed engineer's sign-off; verify all dimensions on site

DRAWING TITLE

V2T TRIANGLE + RODS
3D views & schedules

SCALE @ A3	DATE
NTS	07.10.2026
DRAWN / CHECKED	SERIES
CC / —	ARCHITECTURAL

DRAWING No. REV

V2T-04 T01