


PROPOSAL C — TIMBER GARDEN ROOM & OUTDOOR KITCHEN

Glulam garden room with a glass roof for dining, plus an open-air outdoor kitchen along the house wall and tumbled travertine paving.

AXONOMETRIC FROM SOUTH-EAST (east wall cut away at 1.0 m) — NTS

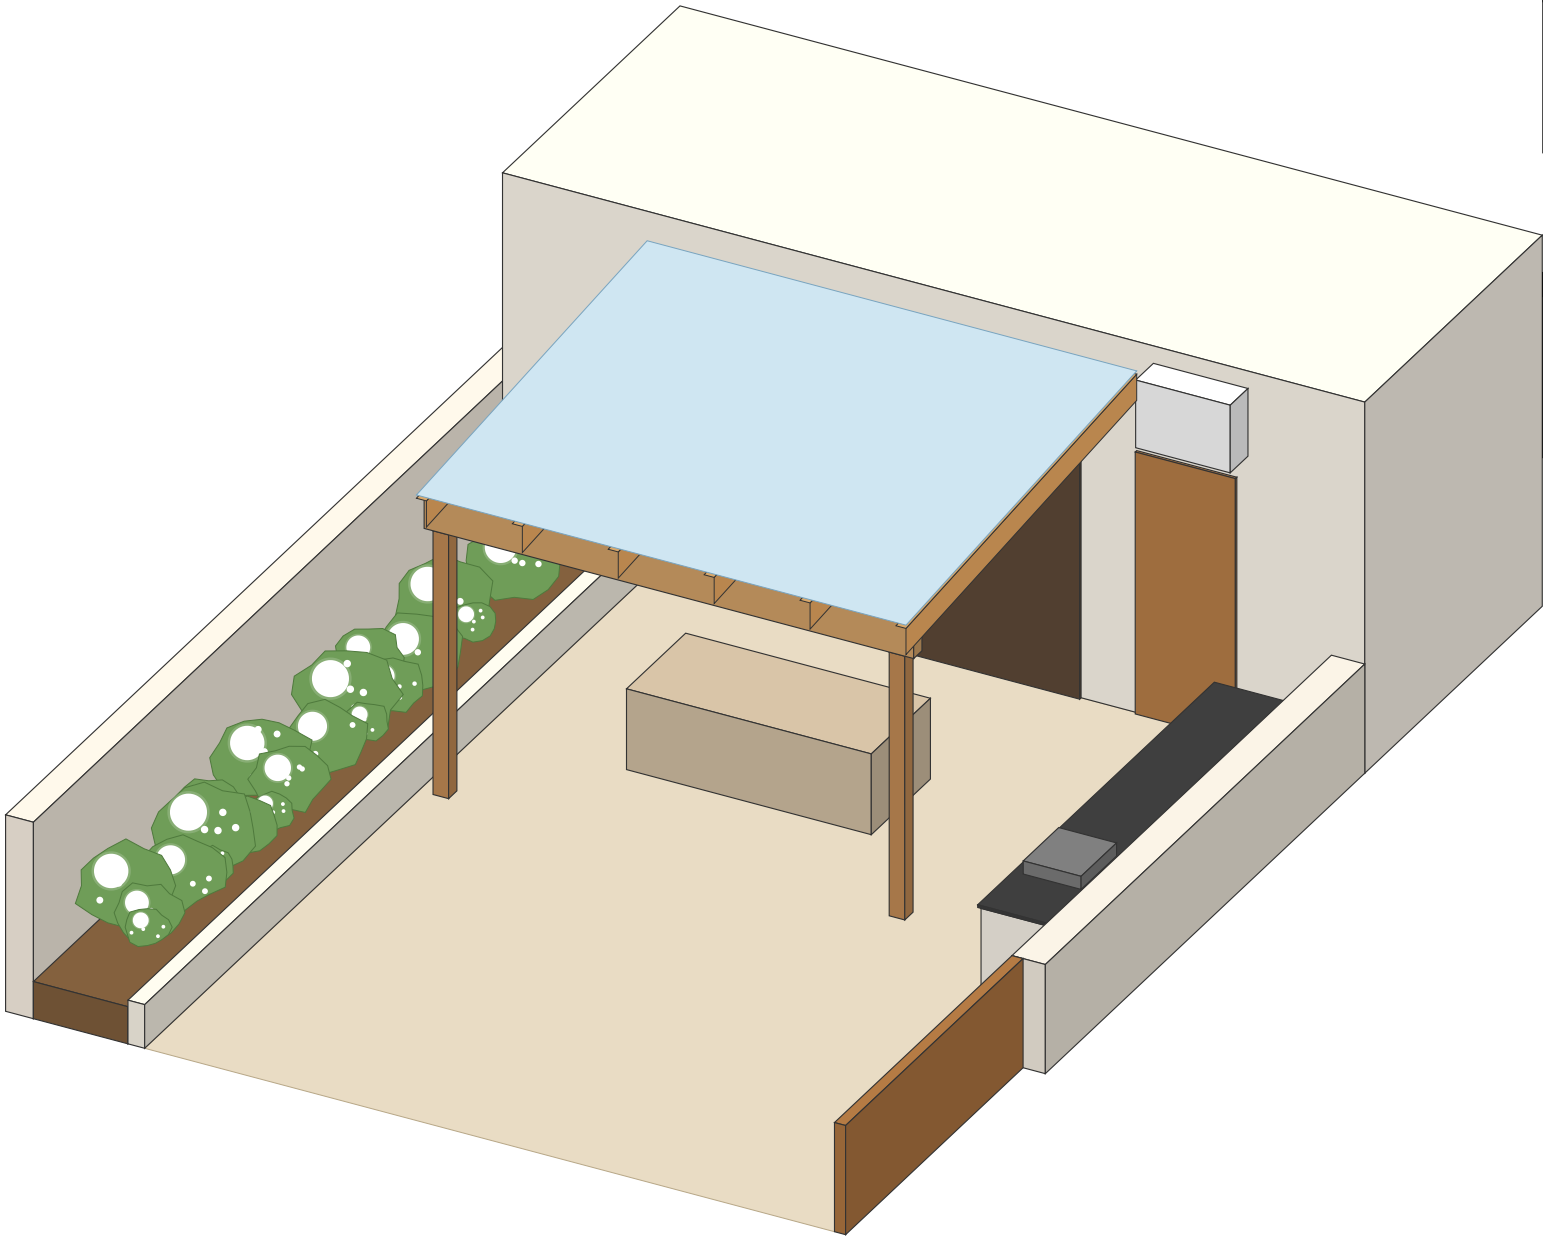

CONCEPT

Warm timber structure with a 5" glass roof keeps the doors and hall bright while giving all-weather dining for 8. Cooking happens in the open air beside it: a 4 m built-in kitchen with grill, sink and fridge along the east wall, with services next to the existing utility room.

KEY FEATURES

- GL24h larch glulam, 6 rafters @ 862, front beam on 2 posts (no post mid-span).
- 8+8 laminated solar-control glass, optional motorised shade.
- Outdoor kitchen: grill outside the roof, sink & fridge, sintered-stone top.
- Tumbled travertine in French pattern; planter & jasmine retained.

DRAWING REGISTER

No.	Title
C-000	Cover, concept & register
C-100	General arrangement plan 1:50
C-101	Roof & structure plan 1:25
C-200	Elevation A 1:25
C-300	Section A-A (N-S) 1:20
C-500	Details 1:2 / 1:5 / 1:10
C-600	Schedules & BOQ

COMPARISON WITH DESIGN A

Criterion	Design A	Prop. C
Roof	Opaque membrane	Glass (bright)
Material	Steel + timber	Glulam timber
Cooking	—	Outdoor kitchen 4 m
Load on façade	Ledger	Ledger (lighter)
Paving	Concrete pavers	Travertine
Cost class	€€	€€€
Daylight to doors	Reduced	Maintained
Maintenance	Oil timber	Clean glass, oil

COURTYARD — PROPOSAL C

Timber garden room & outdoor kitchen — alternative to Design A (same courtyard, existing doors retained)
Client: Owner / Client
Design & drawings: Claude Code

DRAWING NOTES

1. Do not scale from this drawing. Use figured dimensions only.
2. All dimensions in millimetres; levels in metres relative to internal FFL ± 0.000 (datum to be tied to site survey).
3. Contractor to verify all dimensions, levels & existing structure on site before fabrication or ordering.
4. Read with all other architectural, structural & services drawings and the specification notes (A-001).
5. Structural members are preliminary: final design, connections & calculations by a licensed structural engineer to local code before construction.
6. Report any discrepancy to the designer before proceeding.

REVISIONS

Rev	Date	Description
C01	06.10.2026	Issued for construction / tender
P01	05.10.2026	Concept (client renders)

DESIGN PROPOSAL — developed design, buildable; confirm by survey & engineer before construction

DRAWING TITLE


Proposal C — cover, concept & drawing register

SCALE @ A3	DATE
NTS	06.10.2026
DRAWN / CHECKED	SERIES
CC / —	ARCHITECTURAL

DRAWING No. REV


C-000

C01

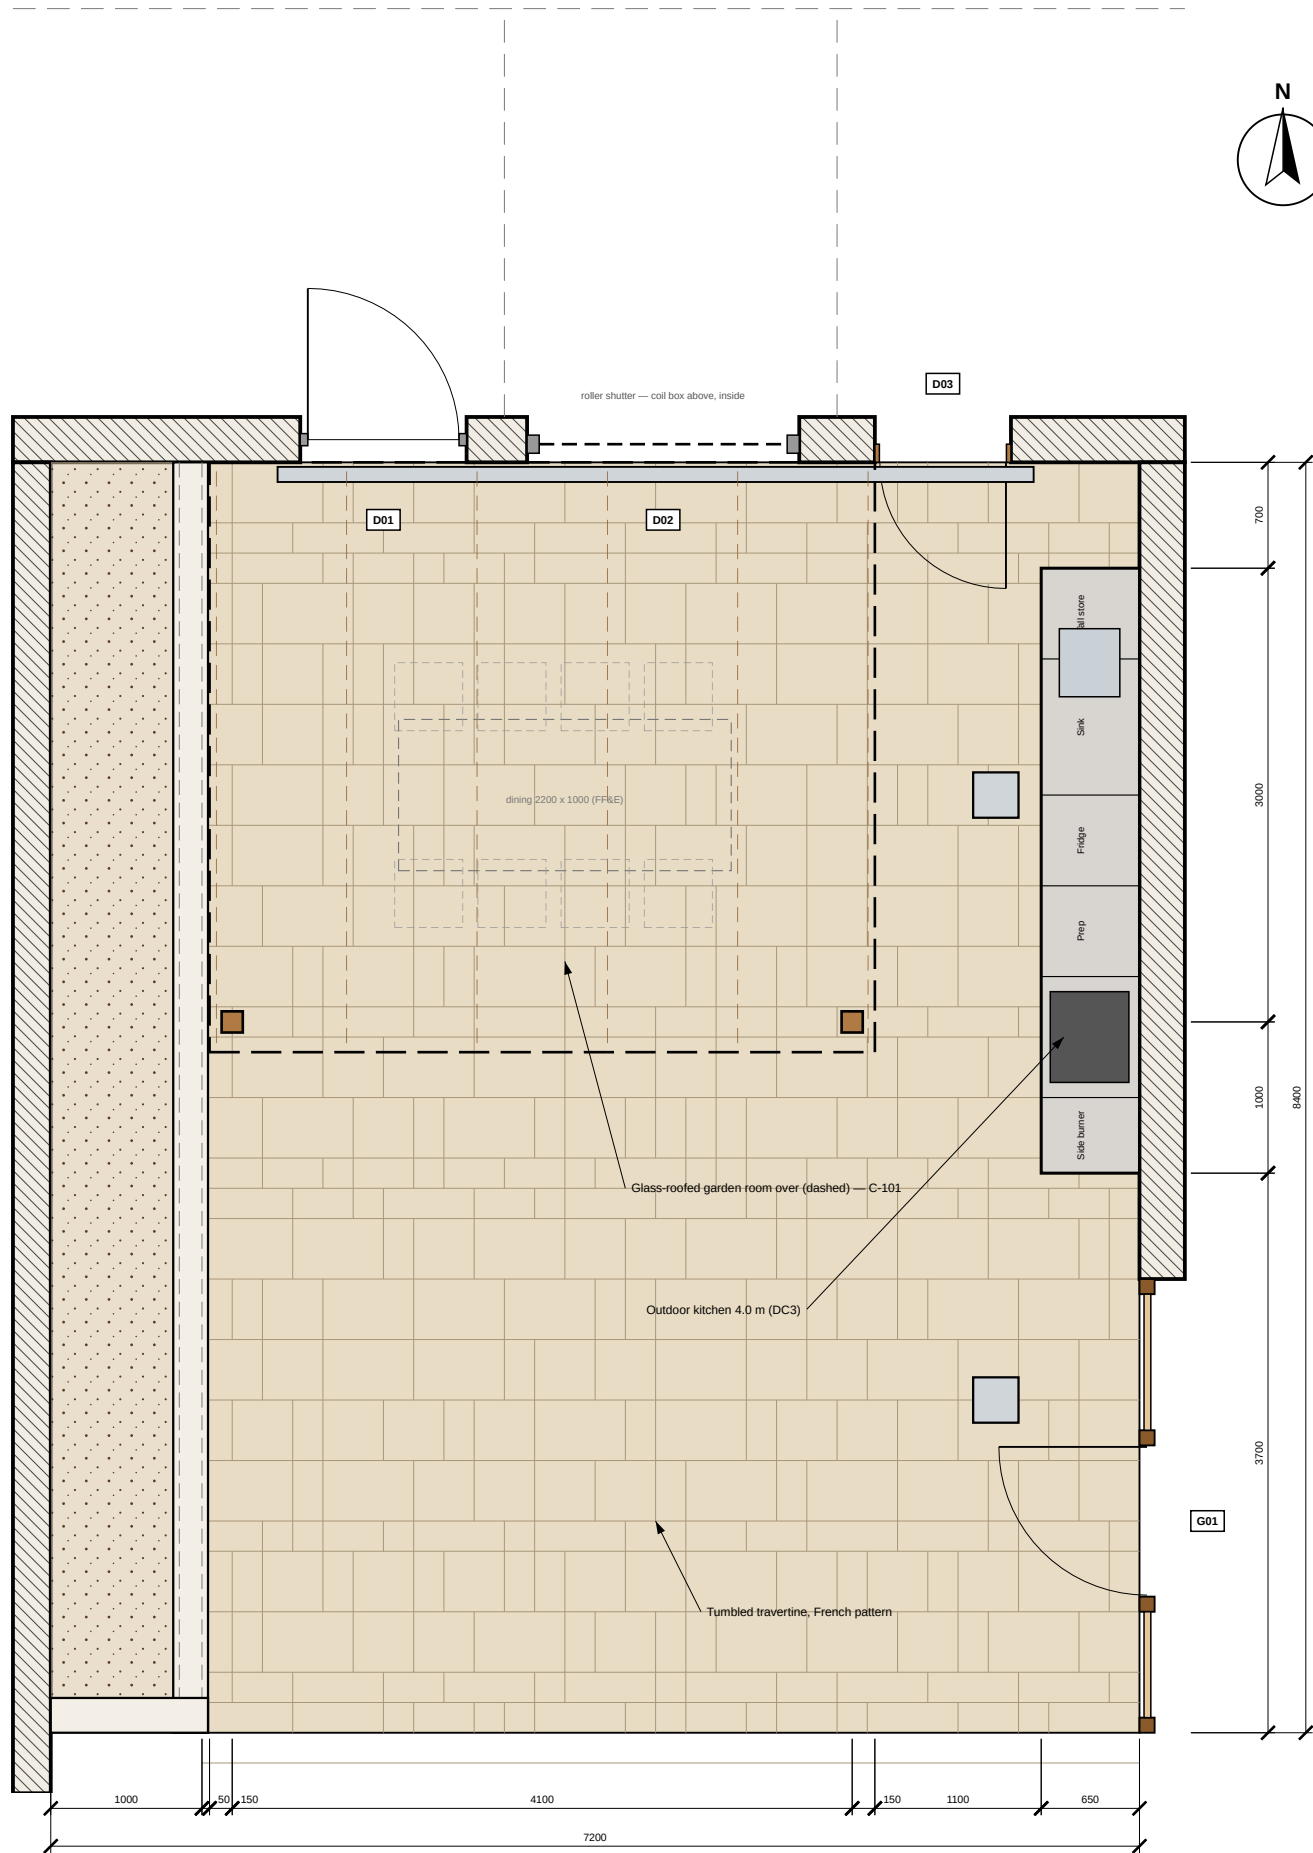

- NOTES**
- Roof stops at X = 5450 so AC1 above D03 stays in the open (no relocation needed).
 - Gullies G1/G2 move west to X = 6250 (clear of kitchen); falls 1:80 to them, kitchen side 1:60.
 - Kitchen waste connects to G1 via trap; water from utility; LPG cupboard ventilated.
 - Travertine: 30 mm tumbled, filled, frost-resistant; laid on 30 mortar bed on 100 slab.
 - Planter & planting as A-104; add herbs (thyme, oregano, sage) at S end.

1
C-100
GENERAL ARRANGEMENT PLAN
1:50 @ A3

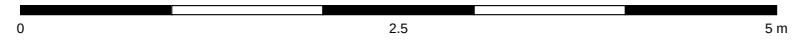

COURTYARD — PROPOSAL C

Timber garden room & outdoor kitchen — alternative to Design A (same courtyard, existing doors retained)
Client: Owner / Client
Design & drawings: Claude Code

- DRAWING NOTES**
- Do not scale from this drawing. Use figured dimensions only.
 - All dimensions in millimetres; levels in metres relative to internal FFL ± 0.000 (datum to be tied to site survey).
 - Contractor to verify all dimensions, levels & existing structure on site before fabrication or ordering.
 - Read with all other architectural, structural & services drawings and the specification notes (A-001).
 - Structural members are preliminary: final design, connections & calculations by a licensed structural engineer to local code before construction.
 - Report any discrepancy to the designer before proceeding.

REVISIONS		
Rev	Date	Description
C01	06.10.2026	Issued for construction / tender
P01	05.10.2026	Concept (client renders)

DESIGN PROPOSAL — developed design, buildable; confirm by survey & engineer before construction

DRAWING TITLE
Proposal C — general arrangement plan

SCALE @ A3 1:50	DATE 06.10.2026
DRAWN / CHECKED CC / —	SERIES ARCHITECTURAL

DRAWING No. **C-100** REV **C01**

COURTYARD — PROPOSAL C

Timber garden room & outdoor kitchen — alternative to Design A (same courtyard, existing doors retained)
Client: Owner / Client
Design & drawings: Claude Code

- DRAWING NOTES
- Do not scale from this drawing. Use figured dimensions only.
 - All dimensions in millimetres; levels in metres relative to internal FFL ± 0.000 (datum to be tied to site survey).
 - Contractor to verify all dimensions, levels & existing structure on site before fabrication or ordering.
 - Read with all other architectural, structural & services drawings and the specification notes (A-001).
 - Structural members are preliminary: final design, connections & calculations by a licensed structural engineer to local code before construction.
 - Report any discrepancy to the designer before proceeding.

REVISIONS		
Rev	Date	Description
C01	06.10.2026	Issued for construction / tender
P01	05.10.2026	Concept (client renders)



DESIGN PROPOSAL — developed design, buildable; confirm by survey & engineer before construction

DRAWING TITLE
Proposal C — roof & structure plan

SCALE @ A3 1:25	DATE 06.10.2026
DRAWN / CHECKED CC / —	SERIES ARCHITECTURAL

DRAWING No. REV

C-101 C01

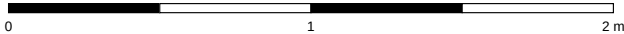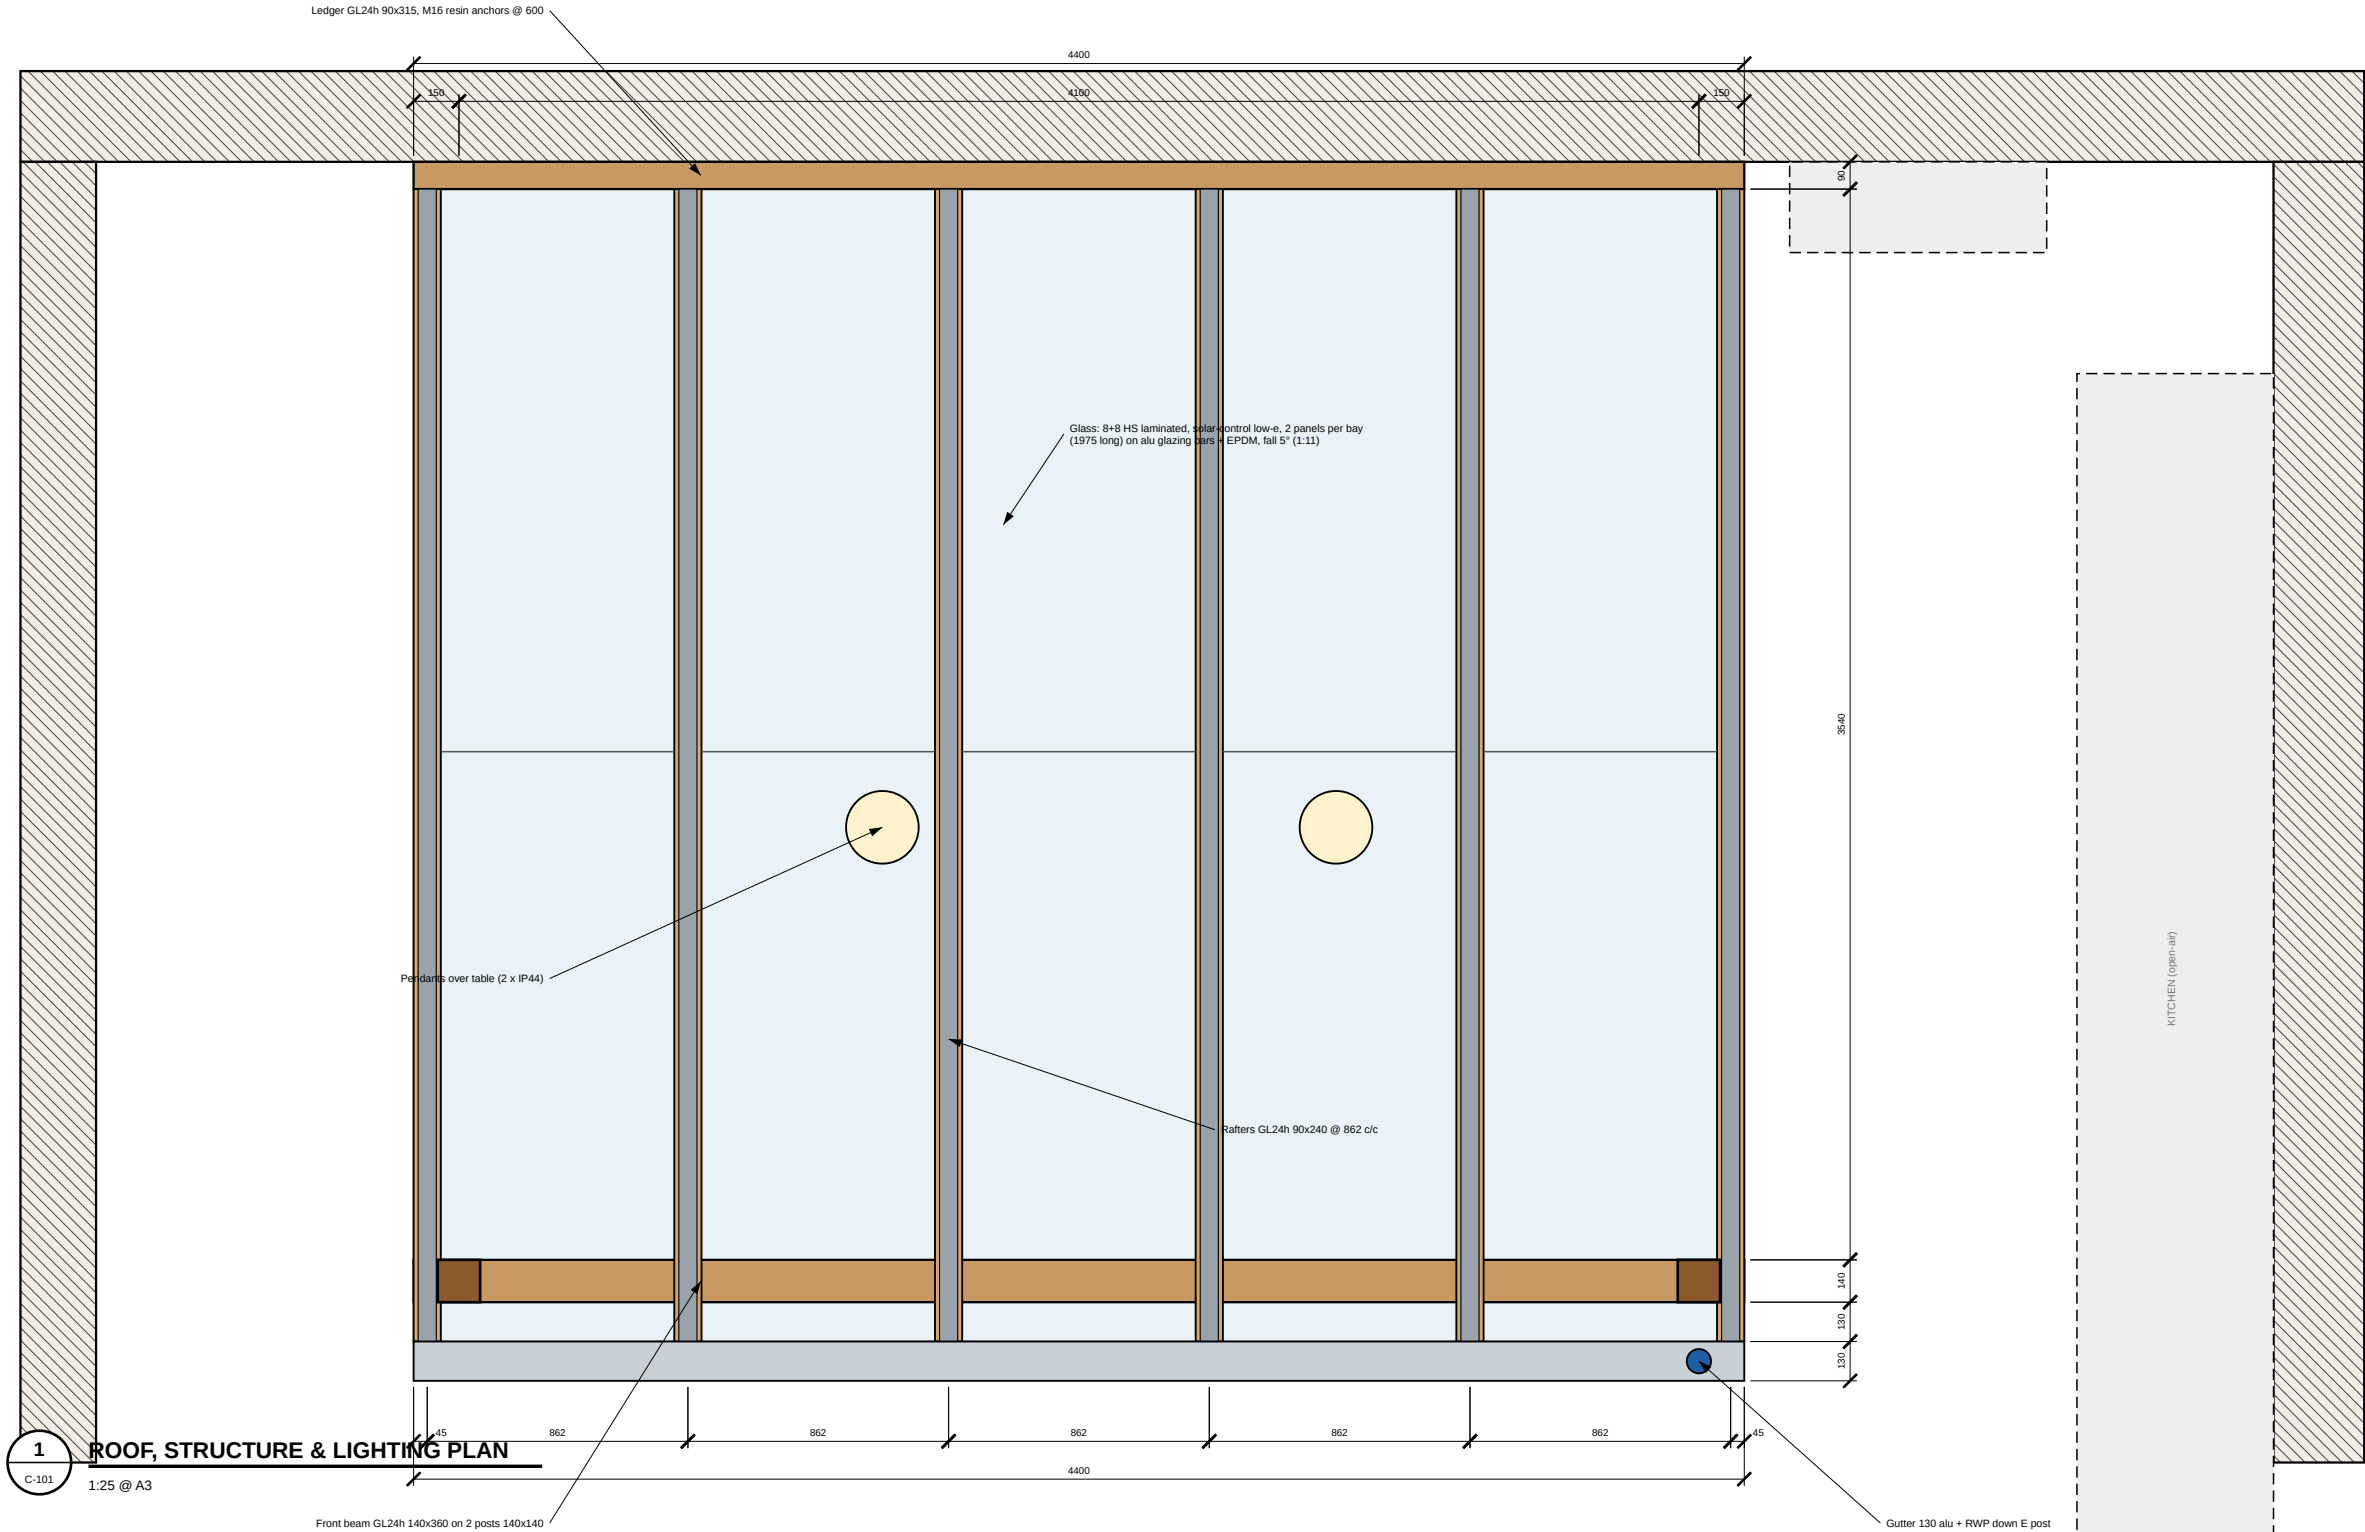

COURTYARD — PROPOSAL C

Timber garden room & outdoor kitchen — alternative to Design A (same courtyard, existing doors retained)
Client: Owner / Client
Design & drawings: Claude Code

- DRAWING NOTES
- Do not scale from this drawing. Use figured dimensions only.
 - All dimensions in millimetres; levels in metres relative to internal FFL ± 0.000 (datum to be tied to site survey).
 - Contractor to verify all dimensions, levels & existing structure on site before fabrication or ordering.
 - Read with all other architectural, structural & services drawings and the specification notes (A-001).
 - Structural members are preliminary: final design, connections & calculations by a licensed structural engineer to local code before construction.
 - Report any discrepancy to the designer before proceeding.

REVISIONS		
Rev	Date	Description
C01	06.10.2026	Issued for construction / tender
P01	05.10.2026	Concept (client renders)

DESIGN PROPOSAL — developed design, buildable; confirm by survey & engineer before construction


DRAWING TITLE

Proposal C — elevation A (looking north)


SCALE @ A3	DATE
1:25	06.10.2026
DRAWN / CHECKED	SERIES
CC / —	ARCHITECTURAL

DRAWING No. REV

C-200 C01

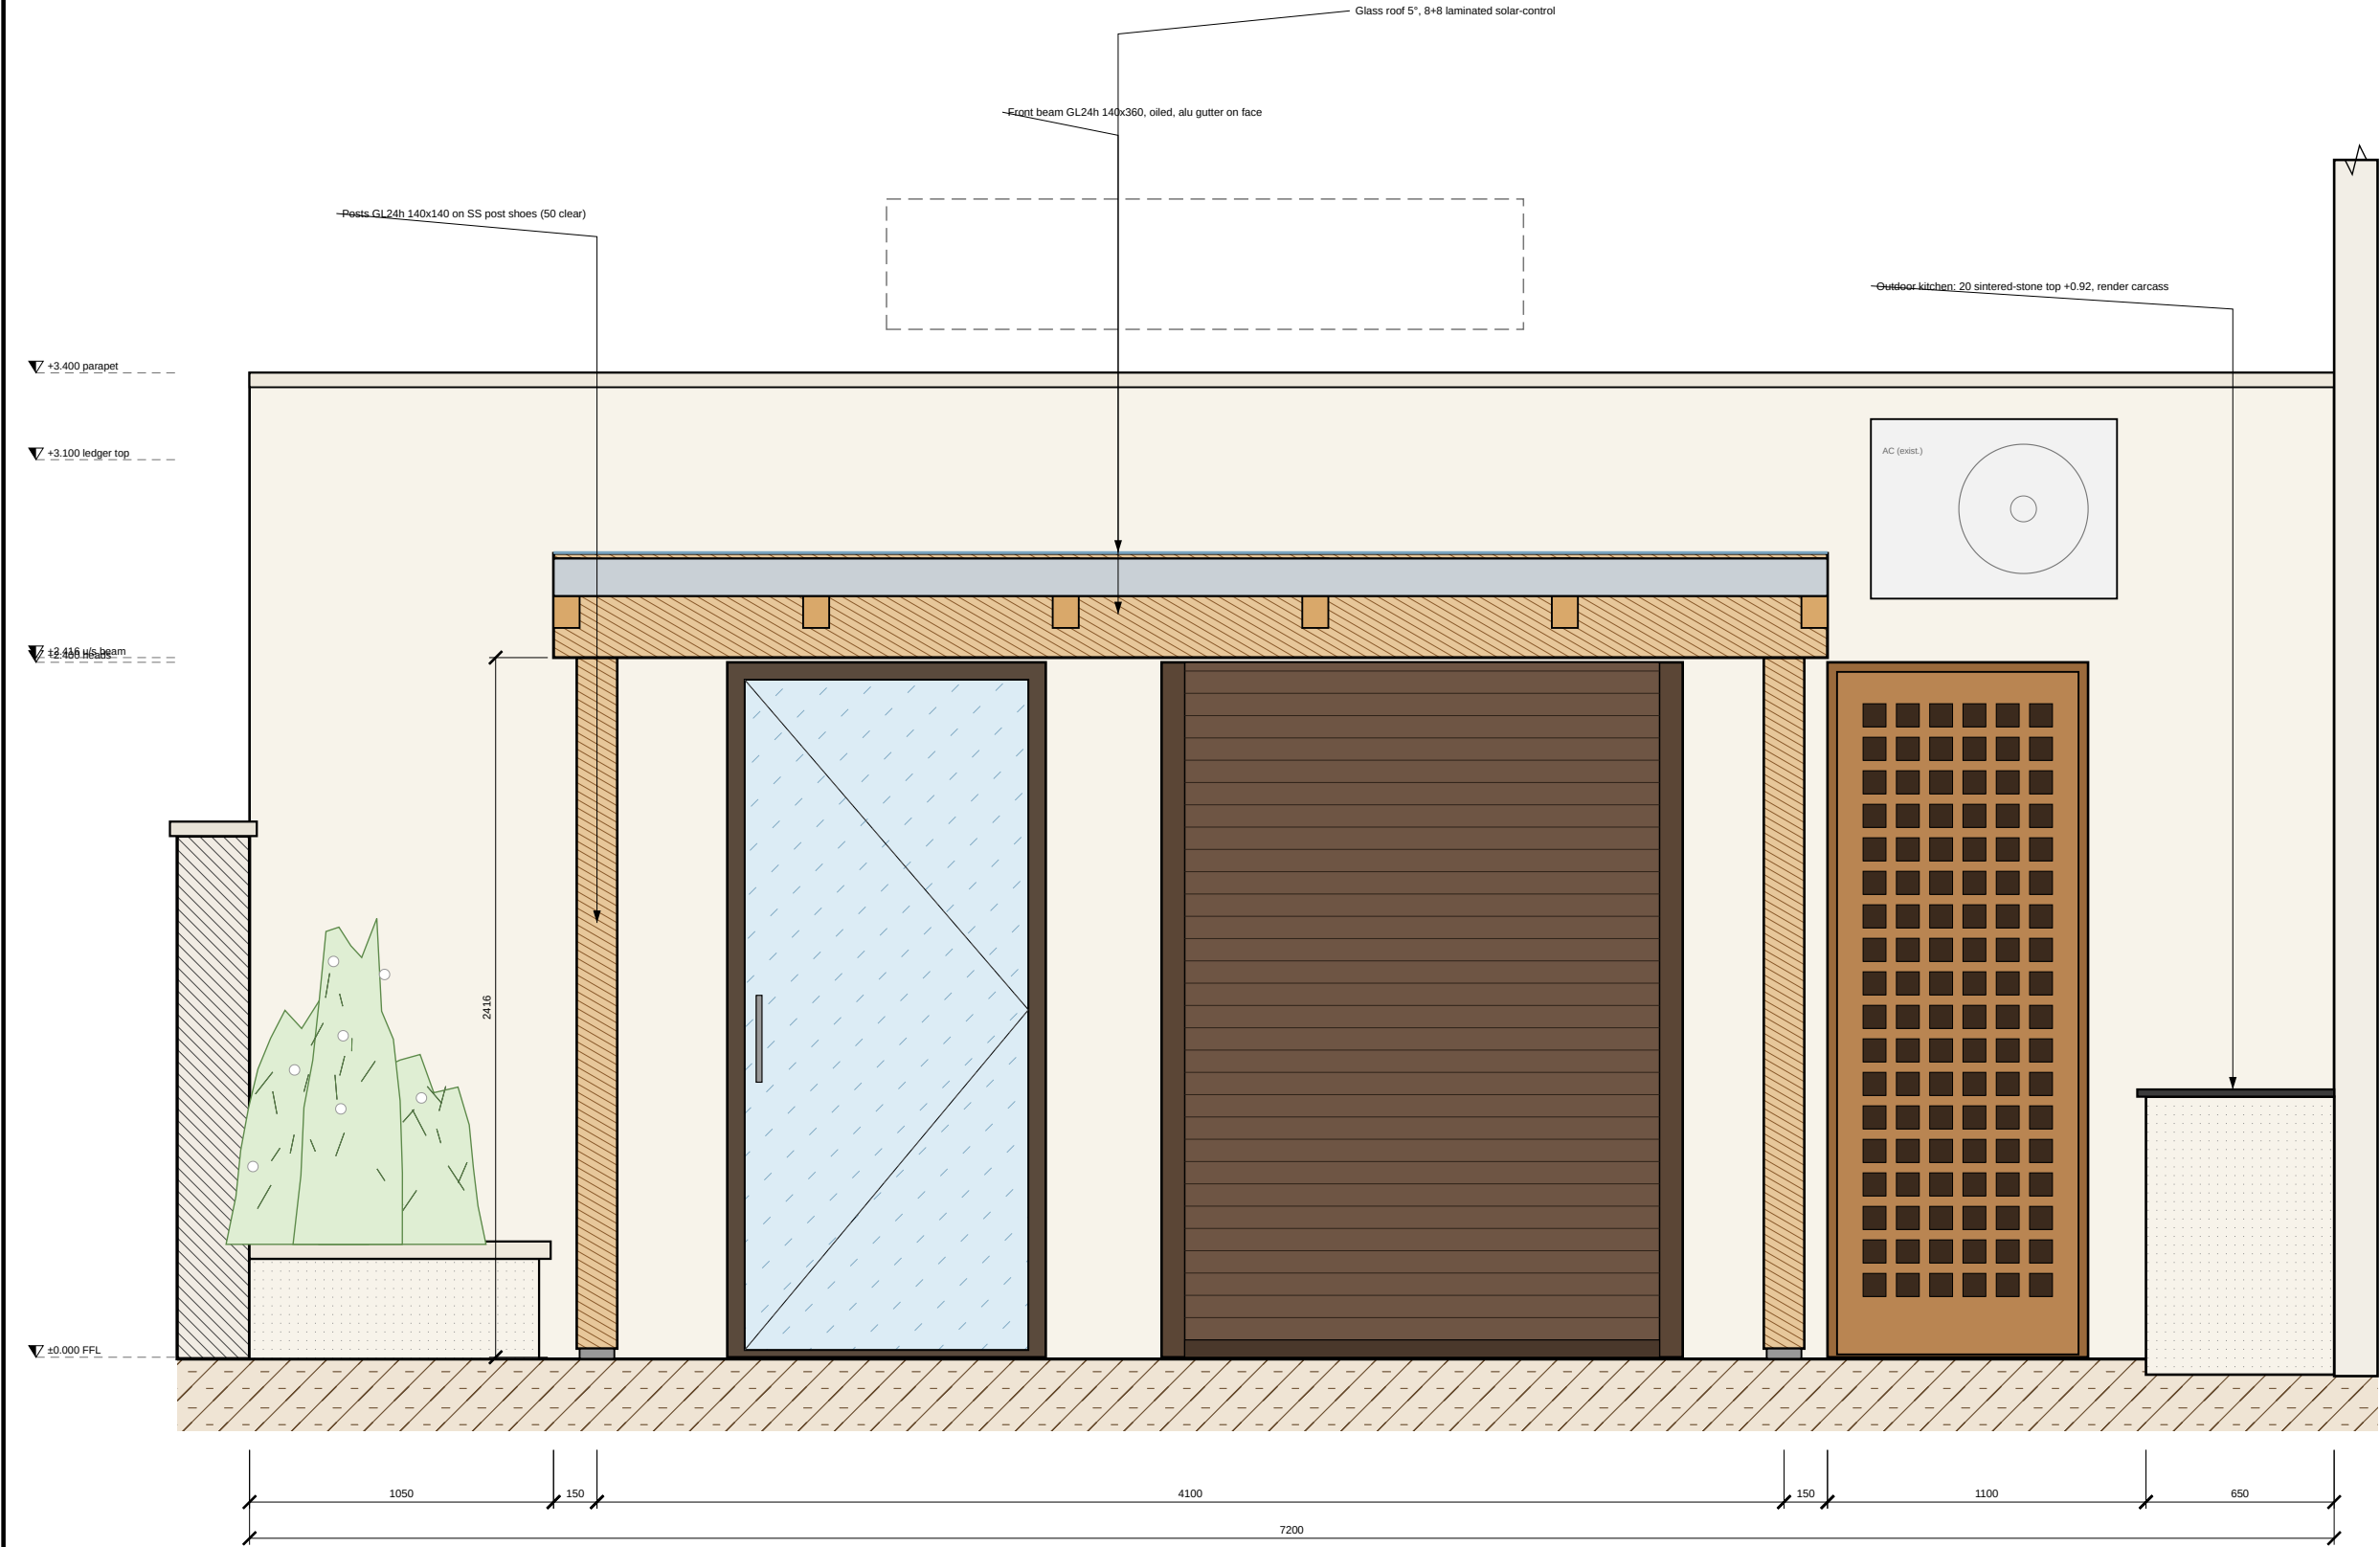

1 ELEVATION A — GARDEN ROOM & KITCHEN (looking north)
C-200 1:25 @ A3

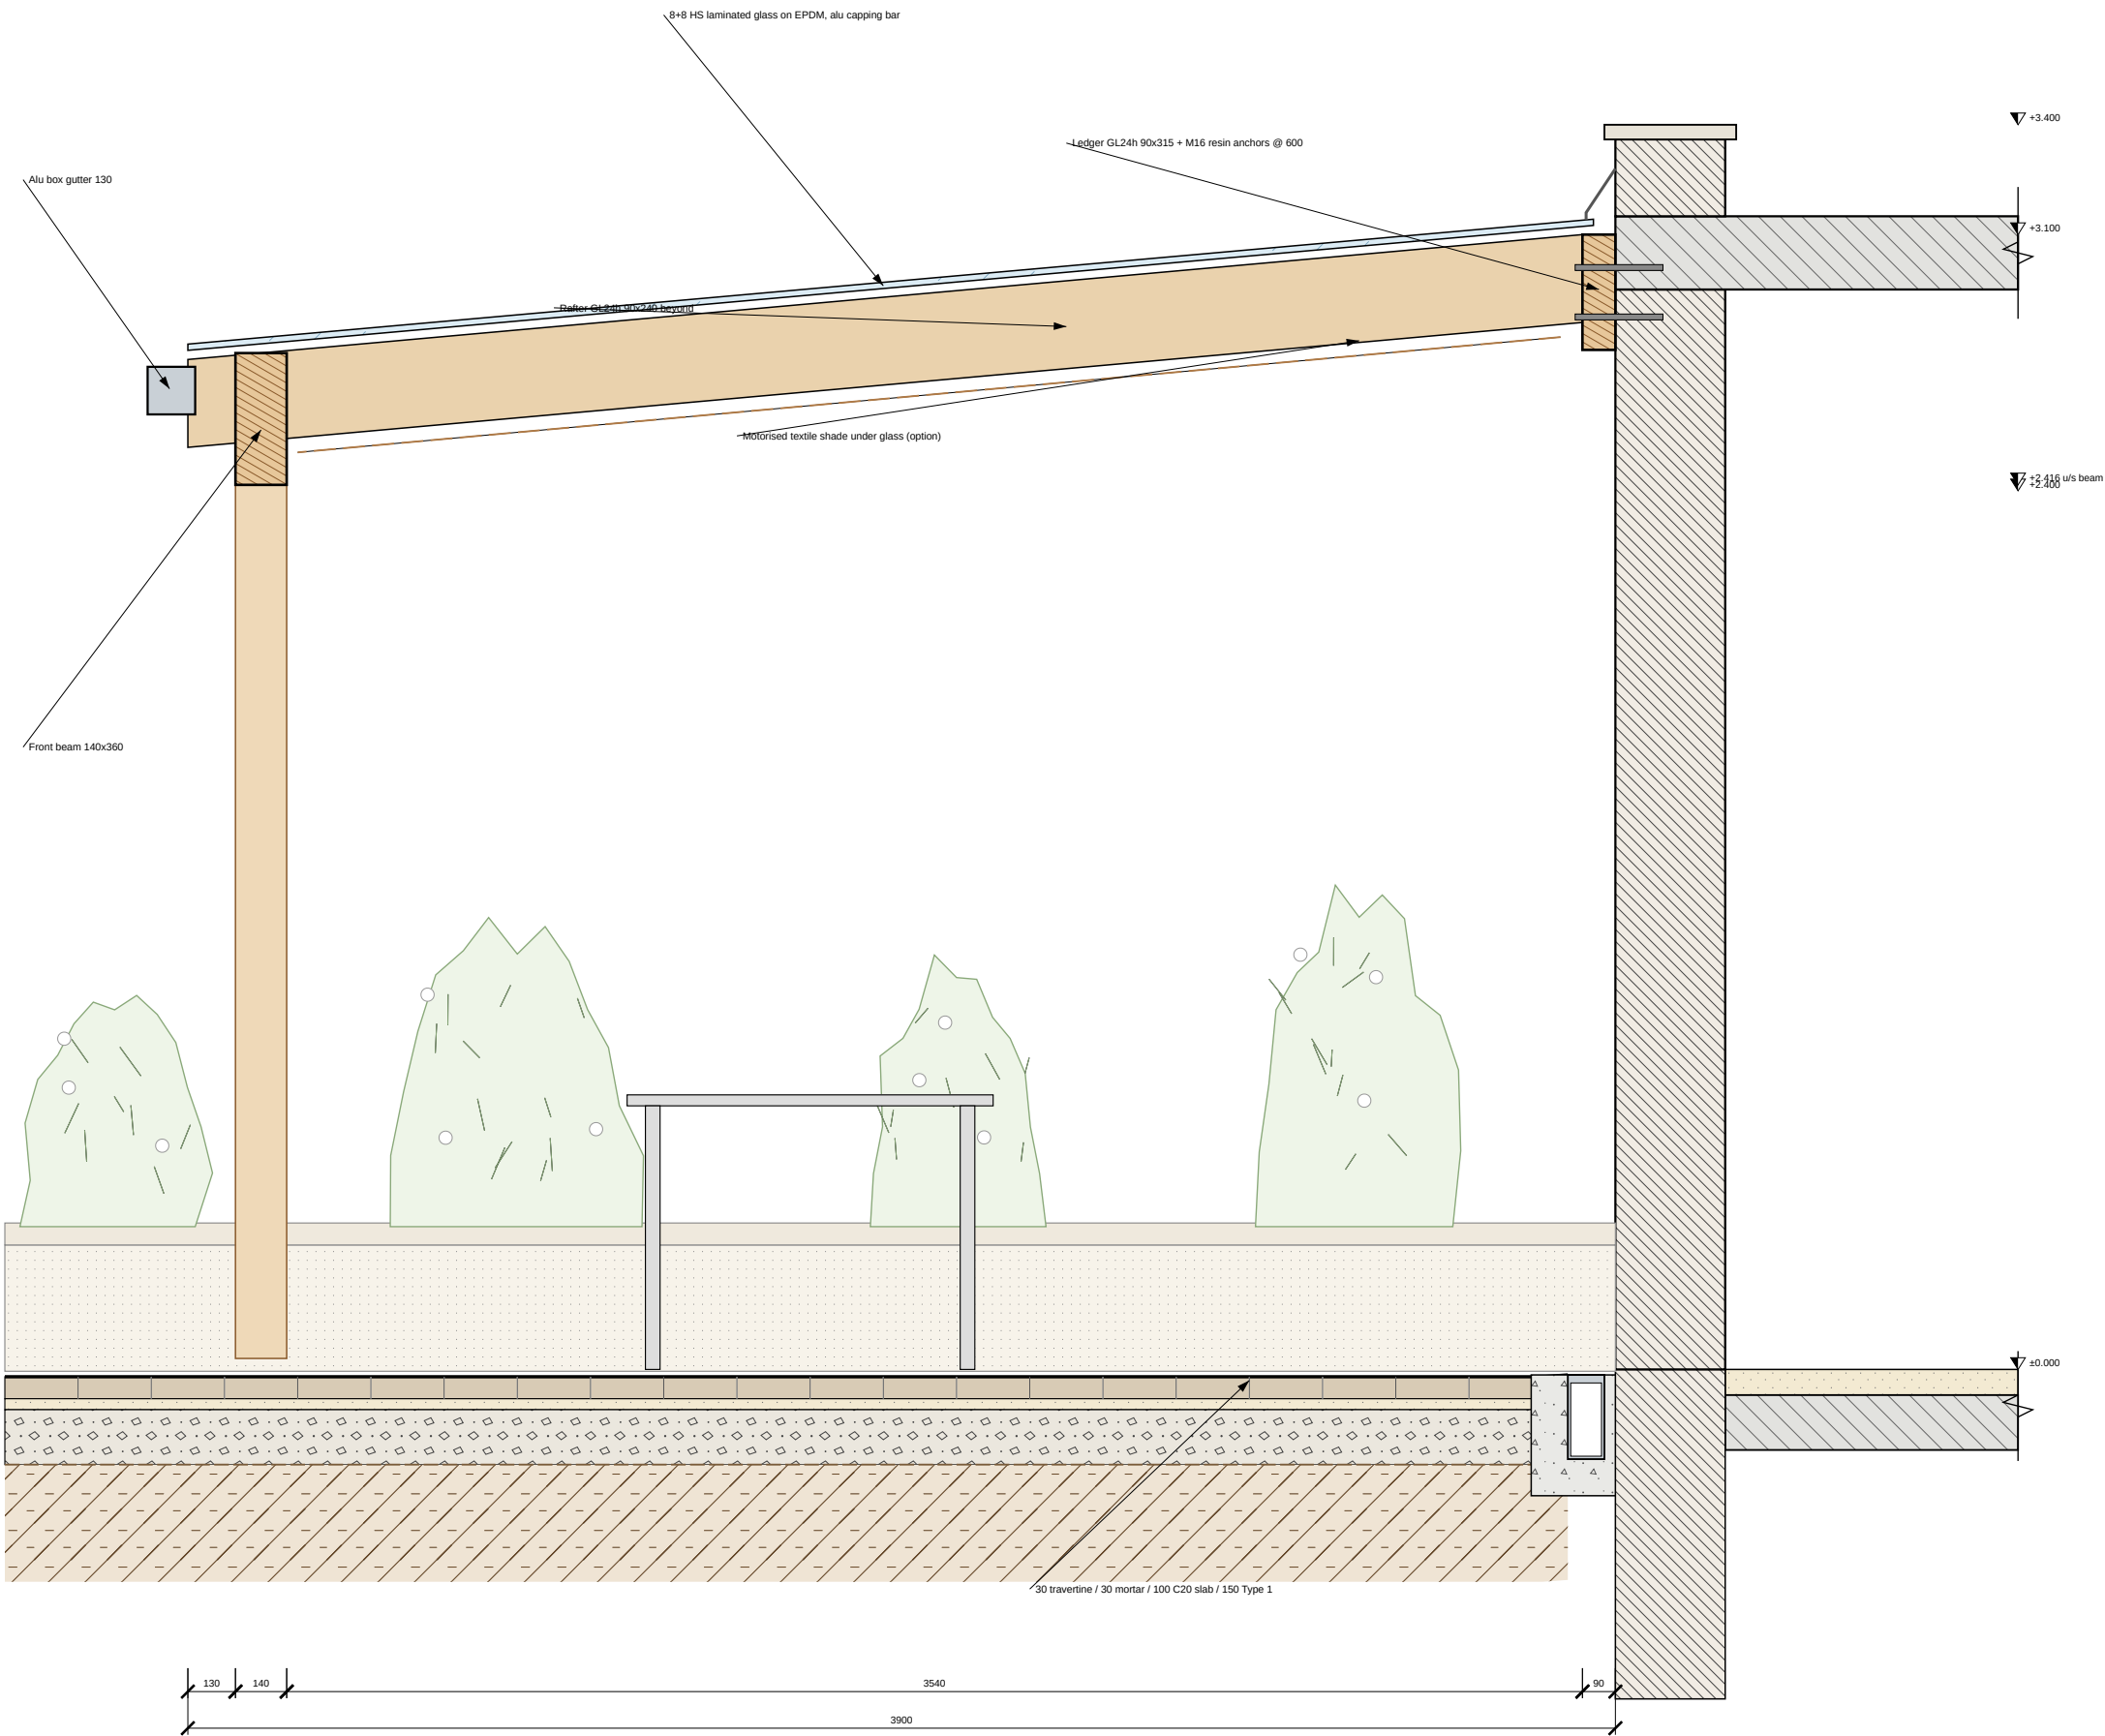

1 SECTION A-A
C-300 1:20 @ A3 through ledger, glass roof & front beam, looking west



COURTYARD — PROPOSAL C

Timber garden room & outdoor kitchen — alternative to Design A (same courtyard, existing doors retained)
Client: Owner / Client
Design & drawings: Claude Code

- DRAWING NOTES**
- Do not scale from this drawing. Use figured dimensions only.
 - All dimensions in millimetres; levels in metres relative to internal FFL ± 0.000 (datum to be tied to site survey).
 - Contractor to verify all dimensions, levels & existing structure on site before fabrication or ordering.
 - Read with all other architectural, structural & services drawings and the specification notes (A-001).
 - Structural members are preliminary: final design, connections & calculations by a licensed structural engineer to local code before construction.
 - Report any discrepancy to the designer before proceeding.

REVISIONS		
Rev	Date	Description
C01	06.10.2026	Issued for construction / tender
P01	05.10.2026	Concept (client renders)

DESIGN PROPOSAL — developed design, buildable; confirm by survey & engineer before construction


DRAWING TITLE
Proposal C — section A-A (N-S at X = 3000)

SCALE @ A3 1:20	DATE 06.10.2026
DRAWN / CHECKED CC / —	SERIES ARCHITECTURAL


DRAWING No. REV

C-300 **C01**


DC1 GLAZING BAR ON RAFTER — 1:2

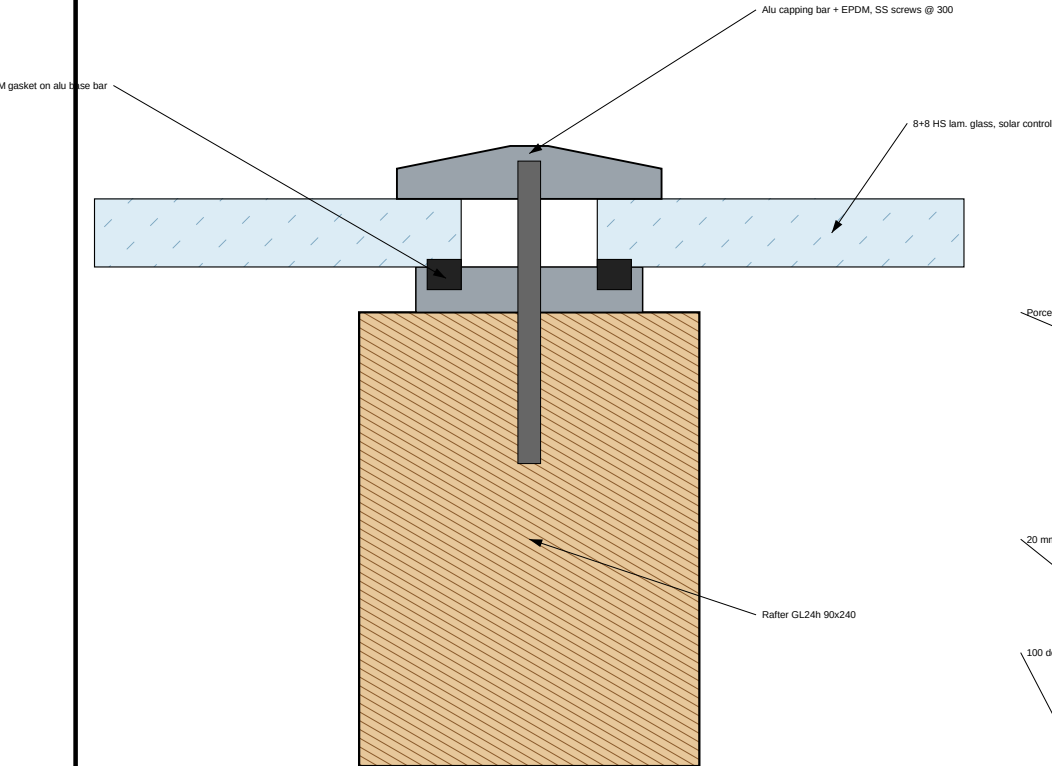

DC2 POST SHOE — 1:10

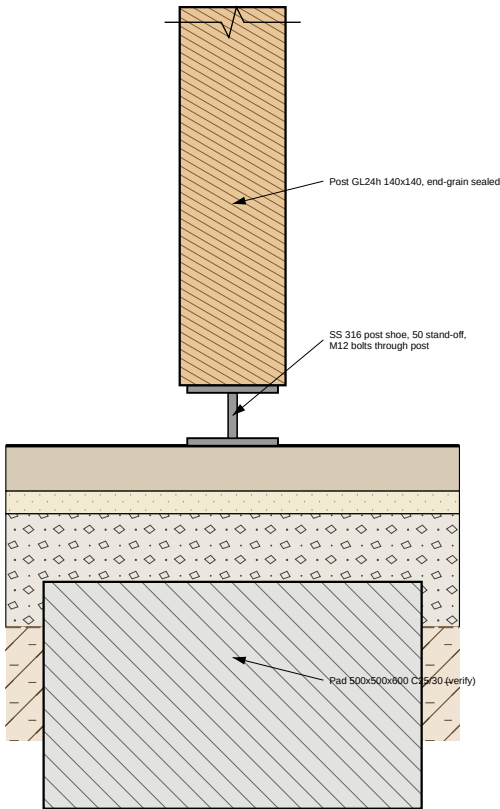

DC3 OUTDOOR KITCHEN COUNTER — 1:10

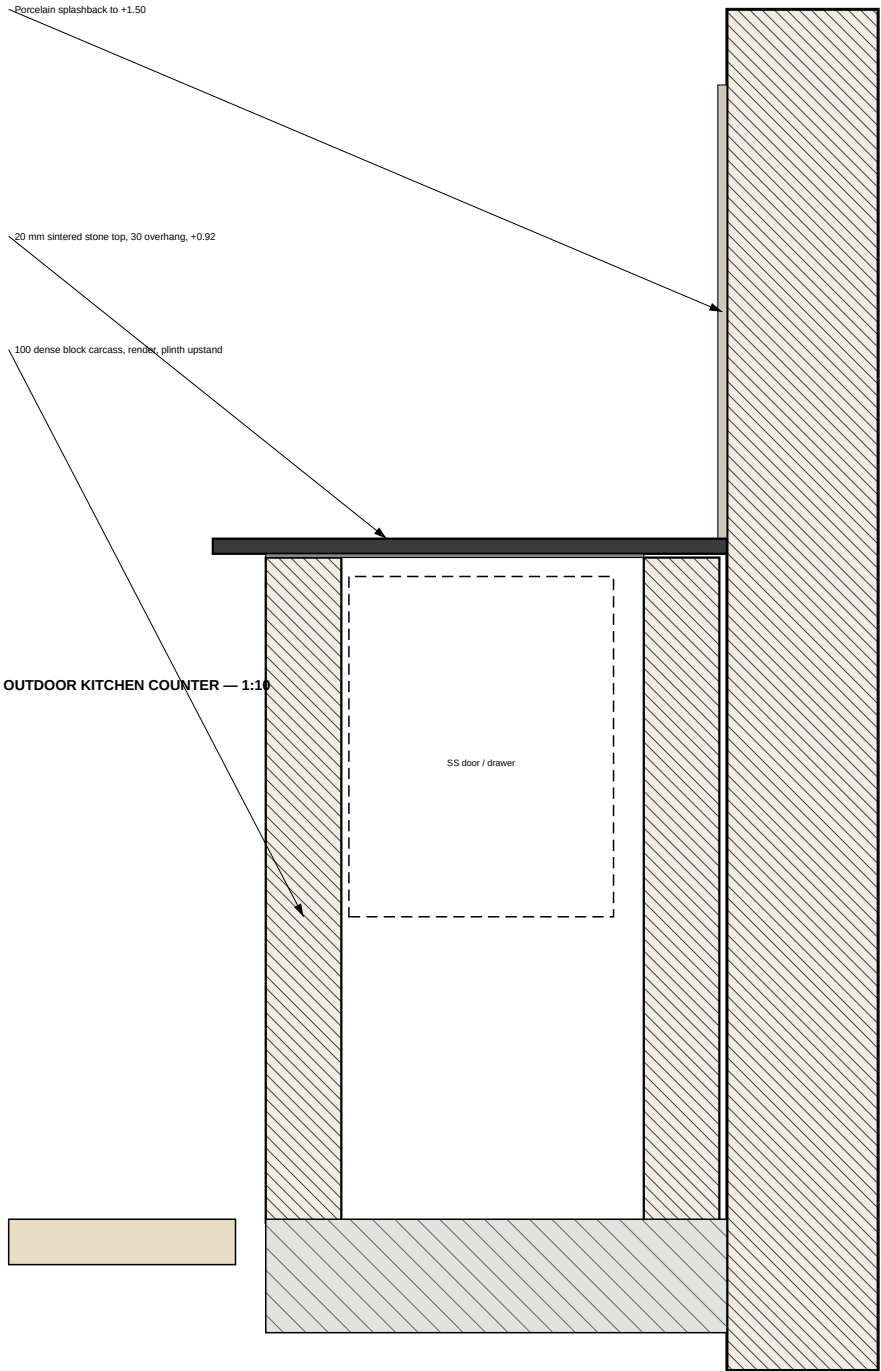

STRUCTURE (preliminary)

- Glulam GL24h (EN 14080), service class 3 — use durable-species lamellas (larch/Douglas) or treated; oil finish; tops of beams capped with alu flashing.
- Front beam 140x360 span 4.1 m: $M = 9 \text{ kNm}$, $\sigma = 3 \text{ MPa}$ $\ll 17 \text{ MPa}$.
- Rafter 90x240 @ 862 span 3.7 m: $\delta = 3 \text{ mm}$ (L/1400).
- Ledger 90x315: 2 M16 resin anchors @ 600 into RC ring beam (survey!).
- Loads: glass 0.45, timber 0.15, snow 1.0 kN/m² (assumed).
- Bracing: knee braces in façade plane not needed — ledger + 2 posts + glass/bars diaphragm; add SS diagonal tie-rods in roof plane if engineer requires.

KITCHEN SERVICES

- Cold water 15 mm from utility (frost drain-down valve), sink waste 40 mm — trap —, gully G1 (relocated to X = 6250).
- LPG 2 x 11 kg in ventilated cupboard (low-level vents), regulator, hose $\leq 1.5 \text{ m}$; or natural gas by Gas Safe/licensed fitter.
- Power: 16 A RCBO, 2 twin IP66 sockets + fridge spur; LED strip under top.
- Grill sits OUTSIDE the glass roof (smoke & heat) — keep 1.0 m clear of AC2.

COURTYARD — PROPOSAL C

Timber garden room & outdoor kitchen — alternative to Design A (same courtyard, existing doors retained)

Client: Owner / Client

Design & drawings: Claude Code

DRAWING NOTES

1. Do not scale from this drawing. Use figured dimensions only.
2. All dimensions in millimetres; levels in metres relative to internal FFL ± 0.000 (datum to be tied to site survey).
3. Contractor to verify all dimensions, levels & existing structure on site before fabrication or ordering.
4. Read with all other architectural, structural & services drawings and the specification notes (A-001).
5. Structural members are preliminary: final design, connections & calculations by a licensed structural engineer to local code before construction.
6. Report any discrepancy to the designer before proceeding.

REVISIONS

Rev	Date	Description
C01	06.10.2026	Issued for construction / tender
P01	05.10.2026	Concept (client renders)

DESIGN PROPOSAL — developed design, buildable; confirm by survey & engineer before construction

DRAWING TITLE

Proposal C — details

SCALE @ A3

1:2 / 1:5 / 1:10

DRAWN / CHECKED

CC / —

DATE

06.10.2026

SERIES

ARCHITECTURAL

DRAWING No.

C-500

REV

C01

Item	Description	Unit	Qty	Rate
1	PRELIMINARIES & SURVEY			
1.1	Survey incl. ring-beam check for ledger	item	1	
2	GROUNDWORKS & DRAINAGE			
2.1	Strip & excavate	m³	15.6	
2.2	Post pads 500x500x600	no	2	
2.3	Gullies relocated to X = 6250, Ø110 drains	item	1	
2.4	C20 slab 100 under travertine + mesh	m²	52.1	
3	GLULAM STRUCTURE			
3.1	Ledger GL24h 90x315	m	4.4	
3.2	Front beam GL24h 140x360	m	4.4	
3.3	Rafters GL24h 90x240	m	23.7	
3.4	Posts GL24h 140x140 + SS shoes	no	2	
3.5	Resin anchors M16, hangers, bolts	item	1	
4	GLAZED ROOF			
4.1	8+8 HS laminated solar-control glass	m²	17.4	

Item	Description	Unit	Qty	Rate
4.2	Alu glazing bars, cappings, flashings	m	32	
4.3	Alu box gutter + RWP	m	4.4	
4.4	Motorised under-glass textile shade (option)	m²	15.8	
5	OUTDOOR KITCHEN			
5.1	Block carcass + render, 4.0 m	m	4.0	
5.2	Sintered stone worktop 20 mm	m	4.0	
5.3	Built-in gas grill 800, side burner, sink + tap	item	1	
5.4	Outdoor fridge 600, SS doors & drawers	item	1	
5.5	Water, waste, gas & power services	item	1	
6	PAVING			
6.1	Tumbled travertine 30 mm French pattern on mortar	m²	52.1	
7	LIGHTING & POWER			
7.1	Pendants x2, under-counter LED, uplights	item	1	
8	PLANTER (as Design A) + herbs	m	8.4	
9	CONTINGENCY	%	10	

COURTYARD — PROPOSAL C

Timber garden room & outdoor kitchen — alternative to Design A (same courtyard, existing doors retained)
Client: Owner / Client
Design & drawings: Claude Code

- DRAWING NOTES
- Do not scale from this drawing. Use figured dimensions only.
 - All dimensions in millimetres; levels in metres relative to internal FFL ±0.000 (datum to be tied to site survey).
 - Contractor to verify all dimensions, levels & existing structure on site before fabrication or ordering.
 - Read with all other architectural, structural & services drawings and the specification notes (A-001).
 - Structural members are preliminary: final design, connections & calculations by a licensed structural engineer to local code before construction.
 - Report any discrepancy to the designer before proceeding.

REVISIONS		
Rev	Date	Description
C01	06.10.2026	Issued for construction / tender
P01	05.10.2026	Concept (client renders)

DESIGN PROPOSAL — developed design, buildable; confirm by survey & engineer before construction

DRAWING TITLE	
Proposal C — schedules & bill of quantities	
SCALE @ A3	DATE
NTS	06.10.2026
DRAWN / CHECKED	SERIES
CC / —	QUANTITIES

Glass supplier to confirm panel build-up, heat-soak and fixings; kitchen appliances to client selection (allow cut-outs per manufacturer).

DRAWING No. REV

C-600C01