

PROPOSAL D — GREEN CANOPY, WATER & LIVING WALL

Sedum-roofed bronze canopy, raised reflecting pool fed by rain chains, a living wall and permeable paving that harvests rainwater for irrigation.

AXONOMETRIC FROM SOUTH-EAST (east wall cut away at 1.0 m) — NTS



CONCEPT
A sustainable, cooling courtyard: every drop of rain is either stored (2000 L tank), reused (living wall, planter, pool top-up) or infiltrated through permeable paving. The canopy carries an extensive sedum roof seen from the house above; rain chains turn storms into a feature.

KEY FEATURES

- 4.3 x 3.6 m canopy, 3 slim bronze posts, sedum roof, white soffit with downlights.
- Raised reflecting pool 600 x 3600 with seat-height coping and weir.
- Living wall beside D01; drip-fed from harvested rain.
- Permeable herringbone paving (no gullies), fire bowl lounge.

DRAWING REGISTER

No.	Title
D-000	Cover, concept & register
D-100	General arrangement plan 1:50
D-101	Green roof & structure plan 1:25
D-200	Elevation A 1:25
D-300	Section A-A (N-S) 1:25
D-500	Details 1:10
D-600	Schedules & BOQ

COMPARISON WITH DESIGN A

Criterion	Design A	Prop. D
Roof	Membrane	Sedum green roof
Water	Gullies to drain	SuDS + 2000 L reuse
Biodiversity	Planter	Roof + wall + pool
Cooling	Shade	Shade + evap.
Posts	2 timber-clad	3 slim CHS
Cost class	€€	€€€
Maintenance	Low	Medium (pump, wall)
Load on façade	Ledger	Ledger

COURTYARD — PROPOSAL D

Green canopy, water & living wall — alternative to Design A (same courtyard, existing doors retained)
Client: Owner / Client
Design & drawings: Claude Code

DRAWING NOTES

1. Do not scale from this drawing. Use figured dimensions only.
2. All dimensions in millimetres; levels in metres relative to internal FFL ±0.000 (datum to be tied to site survey).
3. Contractor to verify all dimensions, levels & existing structure on site before fabrication or ordering.
4. Read with all other architectural, structural & services drawings and the specification notes (A-001).
5. Structural members are preliminary: final design, connections & calculations by a licensed structural engineer to local code before construction.
6. Report any discrepancy to the designer before proceeding.

REVISIONS

Rev	Date	Description
C01	06.10.2026	Issued for construction / tender
P01	05.10.2026	Concept (client renders)

DESIGN PROPOSAL — developed design, buildable; confirm by survey & engineer before construction



DRAWING TITLE

Proposal D — cover, concept & drawing register

SCALE @ A3	DATE
NTS	06.10.2026
DRAWN / CHECKED	SERIES
CC / —	ARCHITECTURAL

DRAWING No. REV

D-000 C01

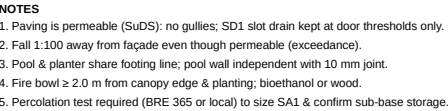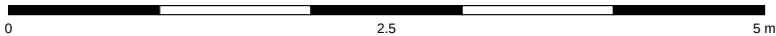

Green canopy, water & living wall — alternative to Design A (same courtyard, existing doors retained)
Client: Owner / Client
Design & drawings: Claude Code

1. Do not scale from this drawing. Use figured dimensions only.
2. All dimensions in millimetres; levels in metres relative to internal FFL ± 0.000 (datum to be tied to site survey).
3. Contractor to verify all dimensions, levels & existing structure on site before fabrication or ordering.
4. Read with all other architectural, structural & services drawings and the specification notes (A-001).
5. Structural members are preliminary: final design, connections & calculations by a licensed structural engineer to local code before construction.
6. Report any discrepancy to the designer before proceeding.

Rev	Date	Description
C01	06.10.2026	Issued for construction / tender
P01	05.10.2026	Concept (client renders)

DESIGN PROPOSAL — developed design, buildable; confirm by survey & engineer before construction

Proposal D — general arrangement plan


DRAWING No. REV

C01

1
D-100

GENERAL ARRANGEMENT PLAN

1:50 @ A3

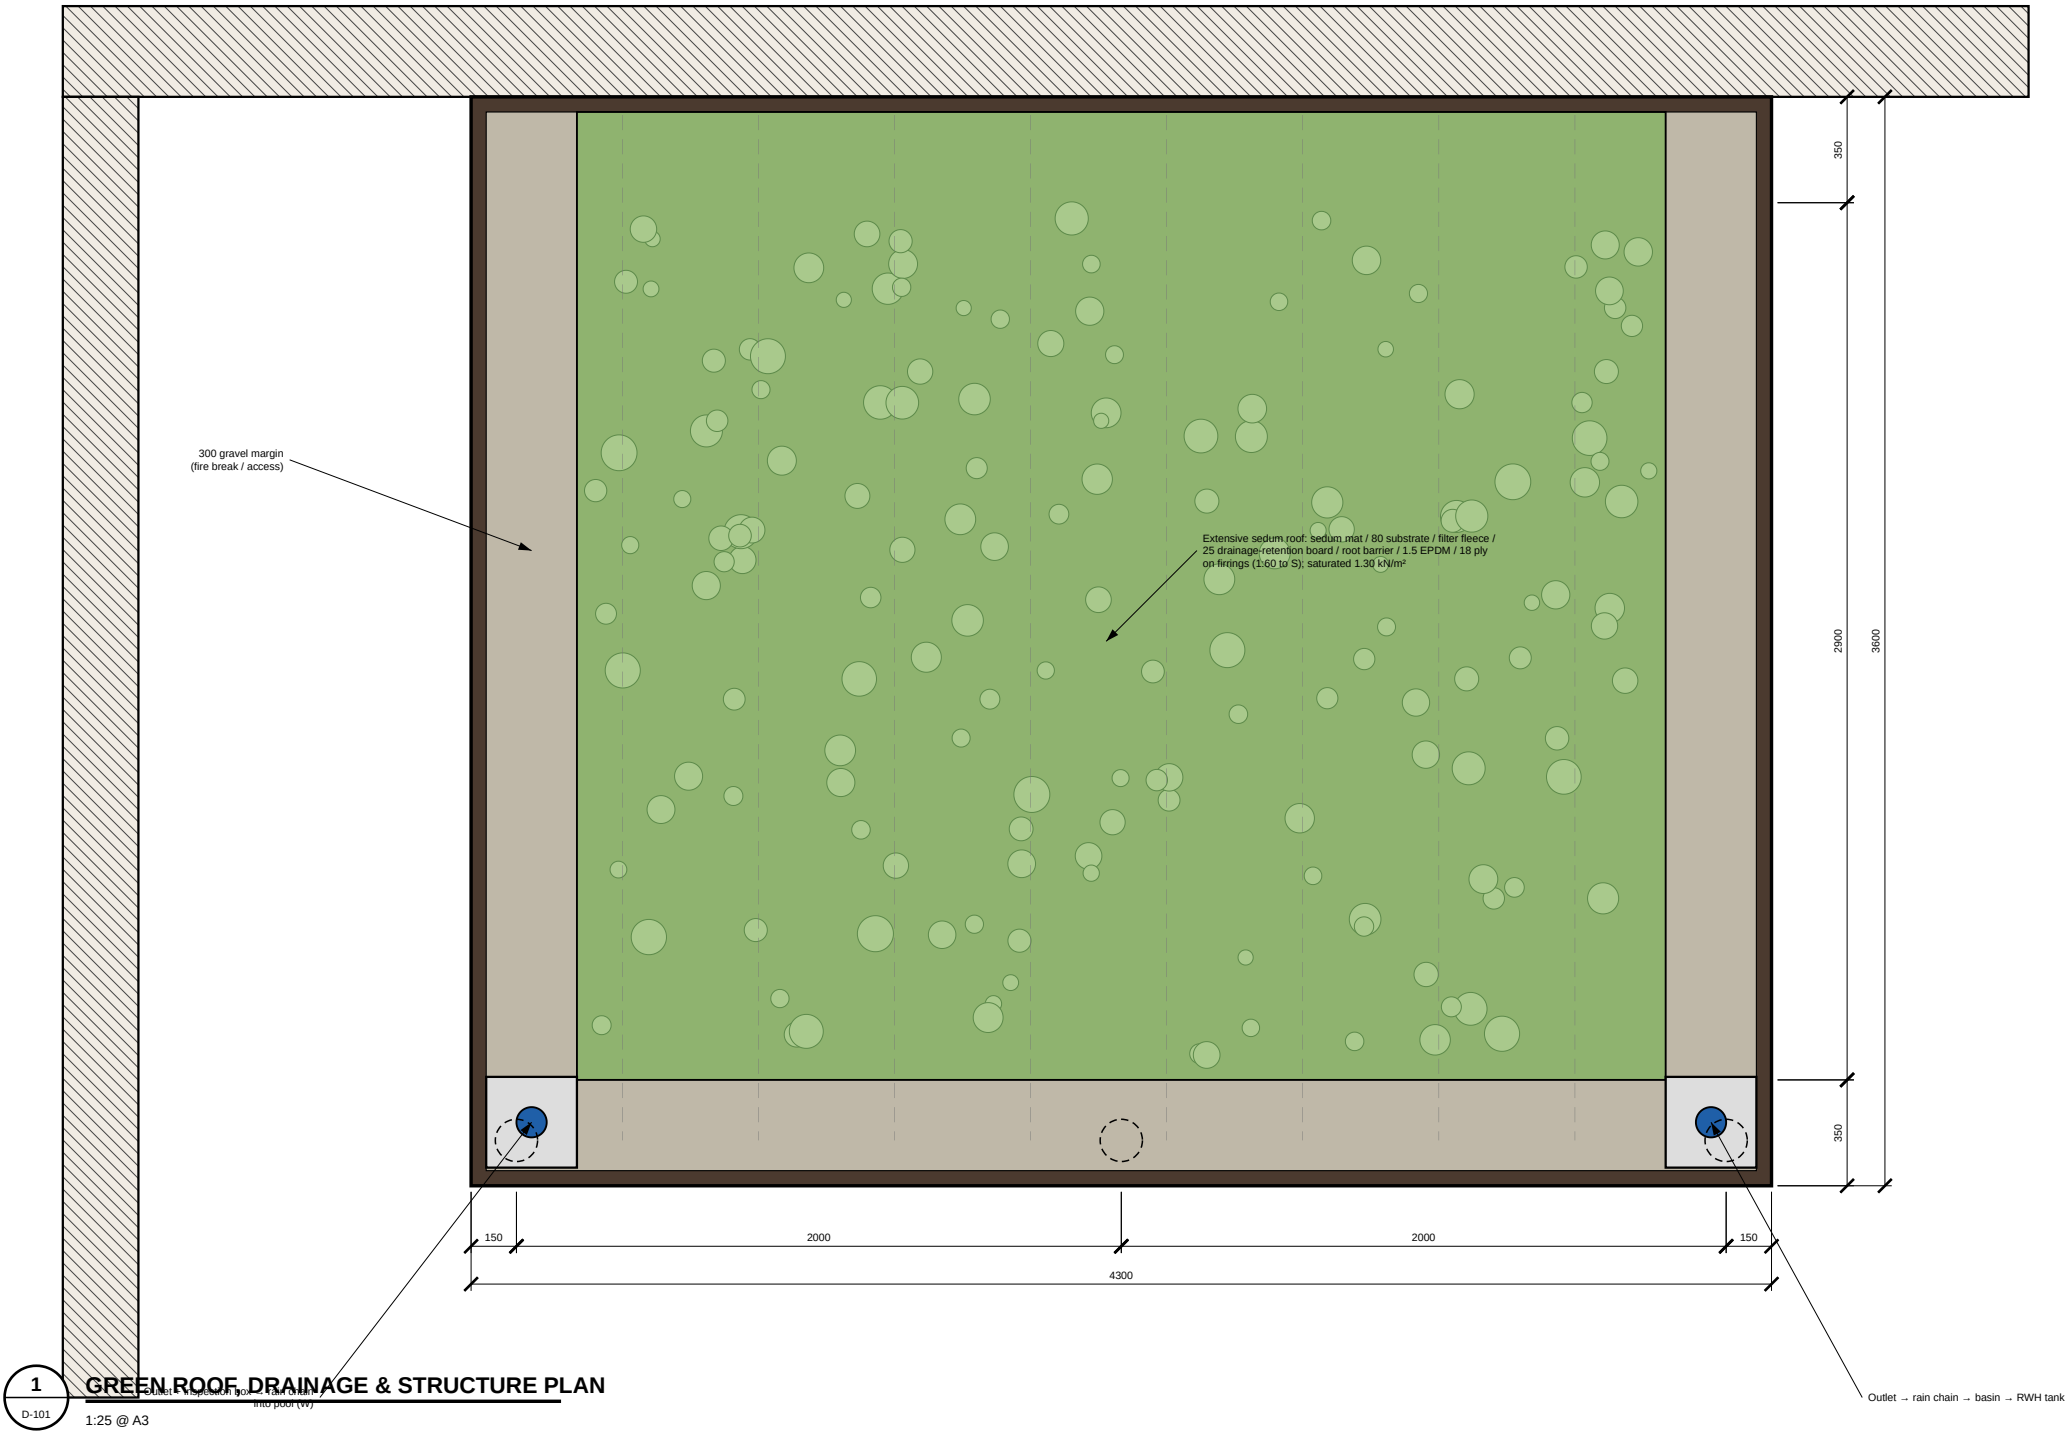

COURTYARD — PROPOSAL D

Green canopy, water & living wall — alternative to Design A (same courtyard, existing doors retained)
Client: Owner / Client
Design & drawings: Claude Code

- DRAWING NOTES**
- Do not scale from this drawing. Use figured dimensions only.
 - All dimensions in millimetres; levels in metres relative to internal FFL ± 0.000 (datum to be tied to site survey).
 - Contractor to verify all dimensions, levels & existing structure on site before fabrication or ordering.
 - Read with all other architectural, structural & services drawings and the specification notes (A-001).
 - Structural members are preliminary: final design, connections & calculations by a licensed structural engineer to local code before construction.
 - Report any discrepancy to the designer before proceeding.

REVISIONS		
Rev	Date	Description
C01	06.10.2026	Issued for construction / tender
P01	05.10.2026	Concept (client renders)

DESIGN PROPOSAL — developed design, buildable; confirm by survey & engineer before construction

DRAWING TITLE
Proposal D — green roof & structure plan

SCALE @ A3 1:25	DATE 06.10.2026
DRAWN / CHECKED CC / —	SERIES ARCHITECTURAL

DRAWING No. REV

D-101 **C01**

COURTYARD — PROPOSAL D

Green canopy, water & living wall — alternative to Design A (same courtyard, existing doors retained)
Client: Owner / Client
Design & drawings: Claude Code

- DRAWING NOTES
- Do not scale from this drawing. Use figured dimensions only.
 - All dimensions in millimetres; levels in metres relative to internal FFL ± 0.000 (datum to be tied to site survey).
 - Contractor to verify all dimensions, levels & existing structure on site before fabrication or ordering.
 - Read with all other architectural, structural & services drawings and the specification notes (A-001).
 - Structural members are preliminary: final design, connections & calculations by a licensed structural engineer to local code before construction.
 - Report any discrepancy to the designer before proceeding.

REVISIONS		
Rev	Date	Description
C01	06.10.2026	Issued for construction / tender
P01	05.10.2026	Concept (client renders)

DESIGN PROPOSAL — developed design, buildable; confirm by survey & engineer before construction


DRAWING TITLE

Proposal D — elevation A (looking north)


SCALE @ A3	DATE
1:25	06.10.2026
DRAWN / CHECKED	SERIES
CC / —	ARCHITECTURAL

DRAWING No. REV

D-200 C01

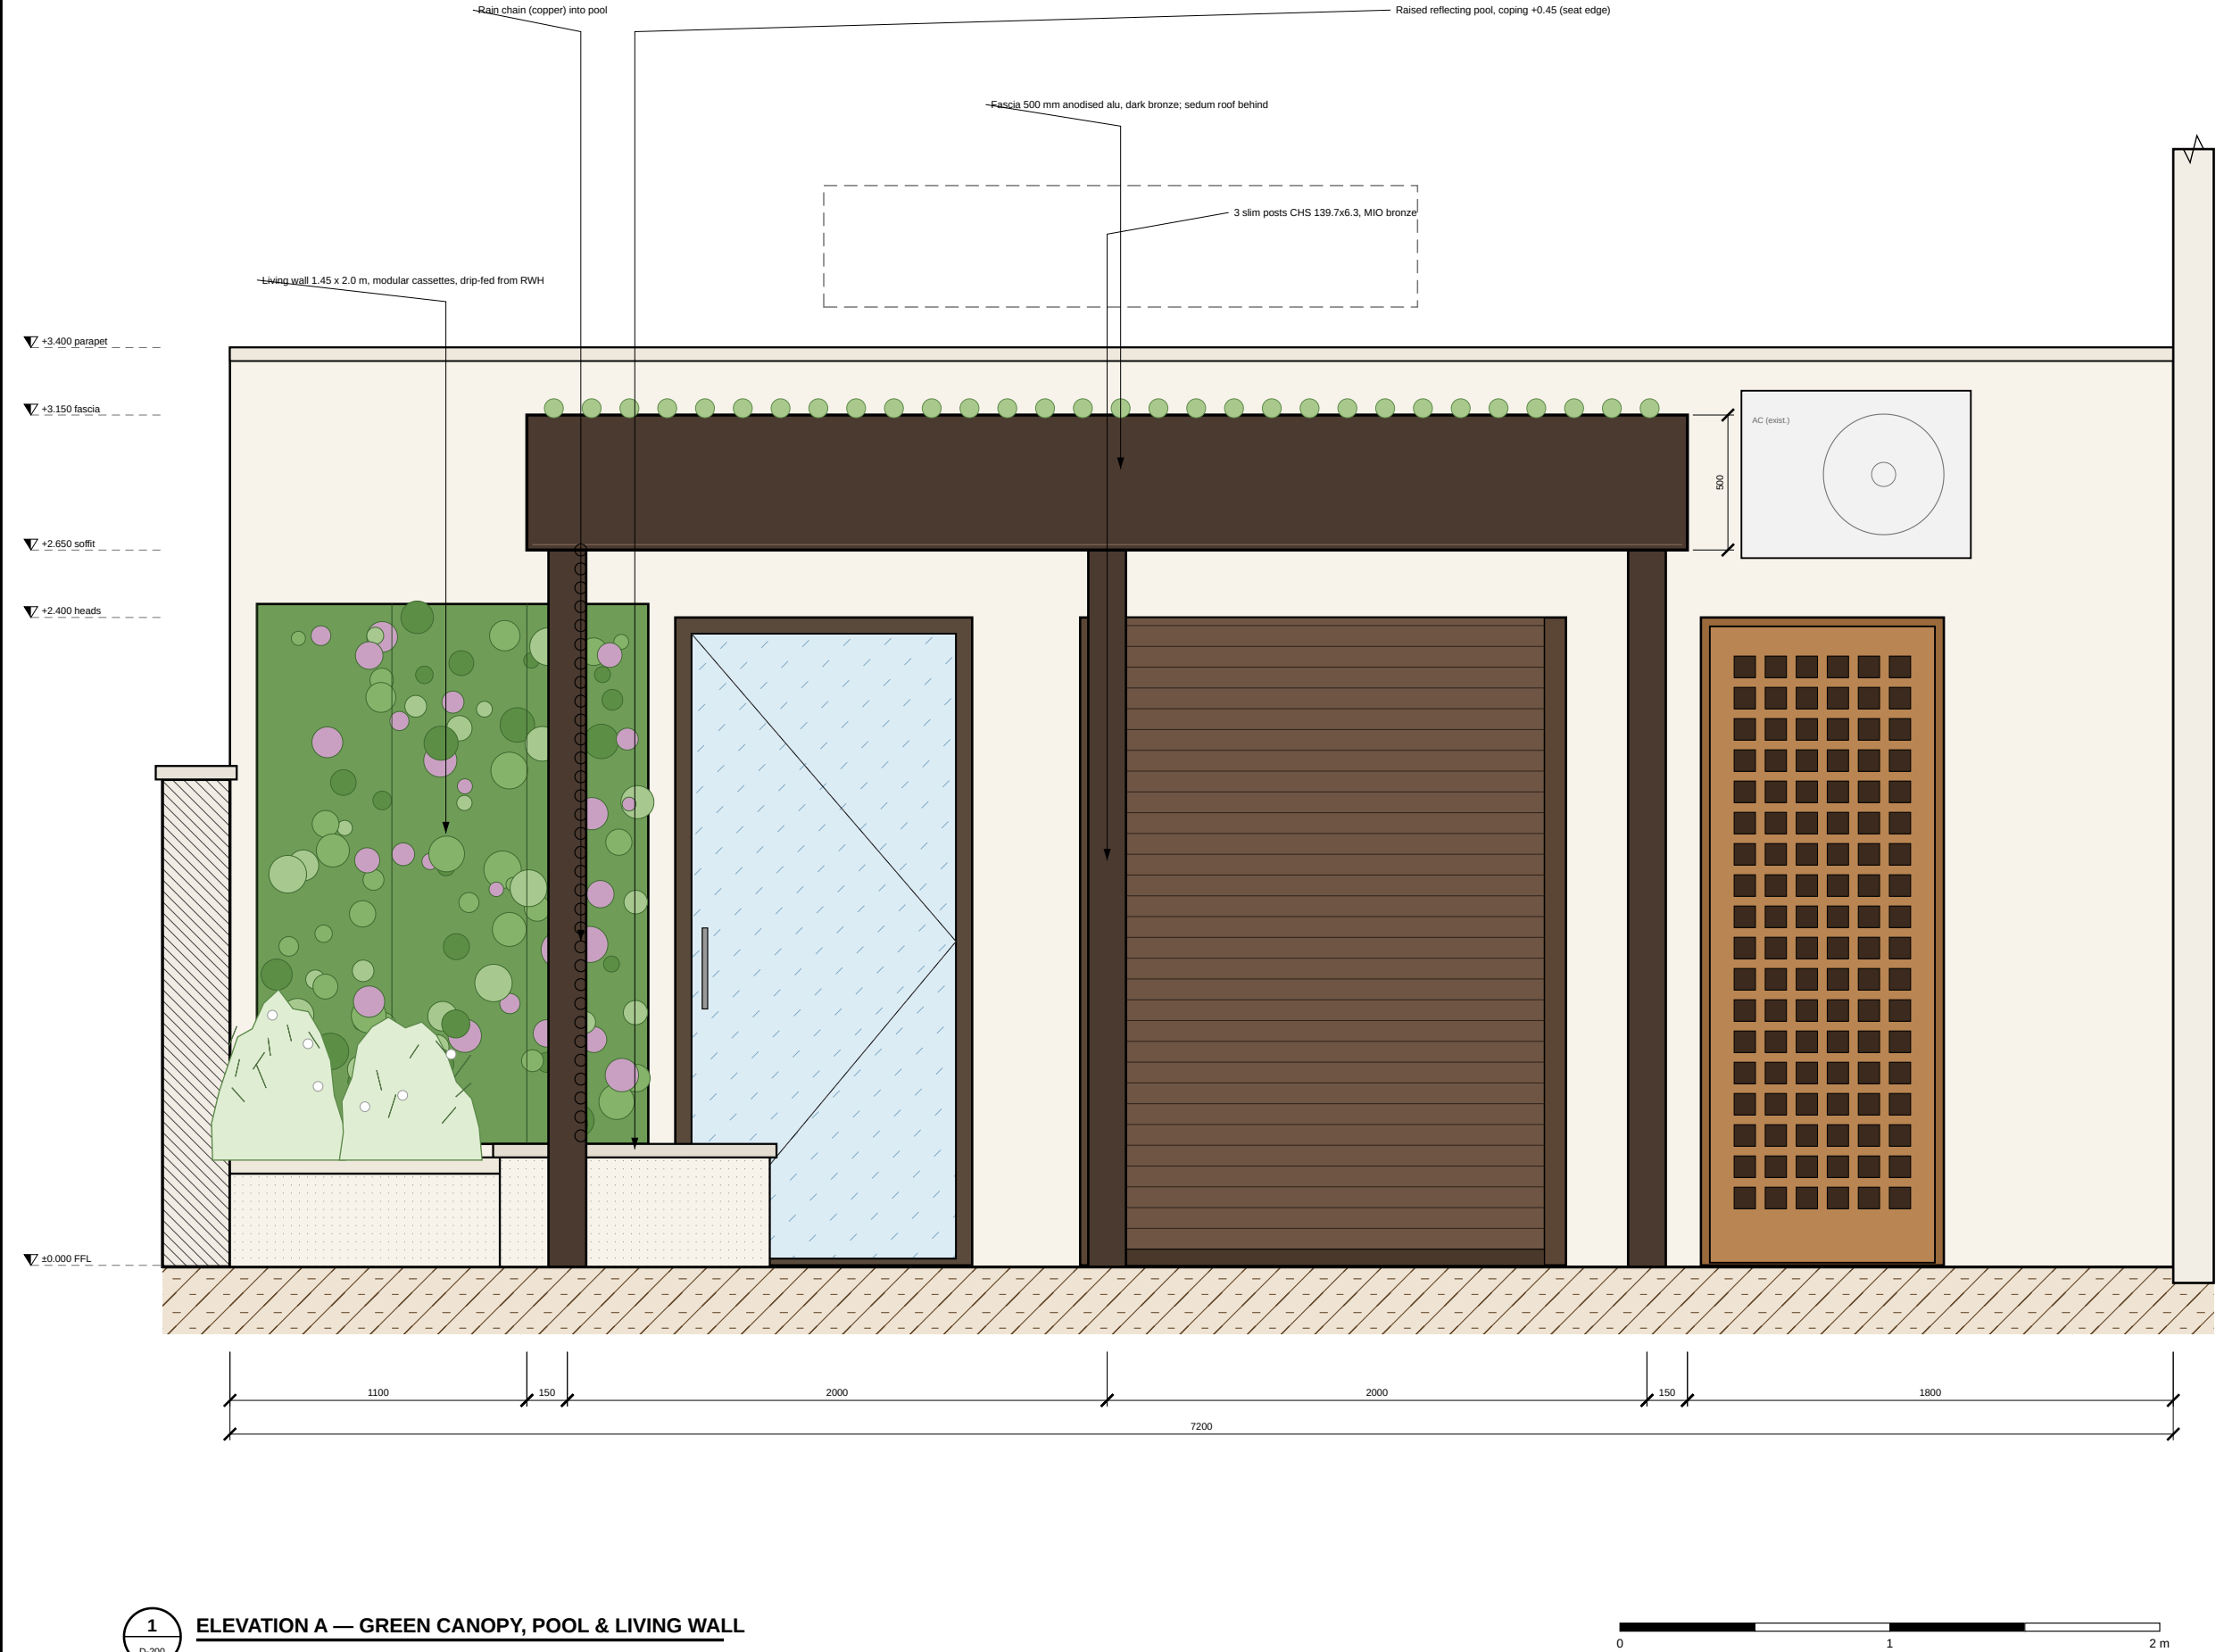

1 ELEVATION A — GREEN CANOPY, POOL & LIVING WALL
D-200 1:25 @ A3

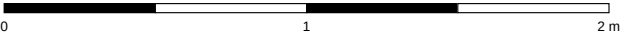

COURTYARD — PROPOSAL D

Green canopy, water & living wall — alternative to Design A (same courtyard, existing doors retained)
Client: Owner / Client
Design & drawings: Claude Code

- DRAWING NOTES
- Do not scale from this drawing. Use figured dimensions only.
 - All dimensions in millimetres; levels in metres relative to internal FFL ± 0.000 (datum to be tied to site survey).
 - Contractor to verify all dimensions, levels & existing structure on site before fabrication or ordering.
 - Read with all other architectural, structural & services drawings and the specification notes (A-001).
 - Structural members are preliminary: final design, connections & calculations by a licensed structural engineer to local code before construction.
 - Report any discrepancy to the designer before proceeding.

REVISIONS		
Rev	Date	Description
C01	06.10.2026	Issued for construction / tender
P01	05.10.2026	Concept (client renders)


DESIGN PROPOSAL — developed design, buildable; confirm by survey & engineer before construction

DRAWING TITLE
Proposal D — section A-A (N-S at X = 1500)


SCALE @ A3 1:25	DATE 06.10.2026
DRAWN / CHECKED CC / —	SERIES ARCHITECTURAL

DRAWING No. REV

D-300 C01

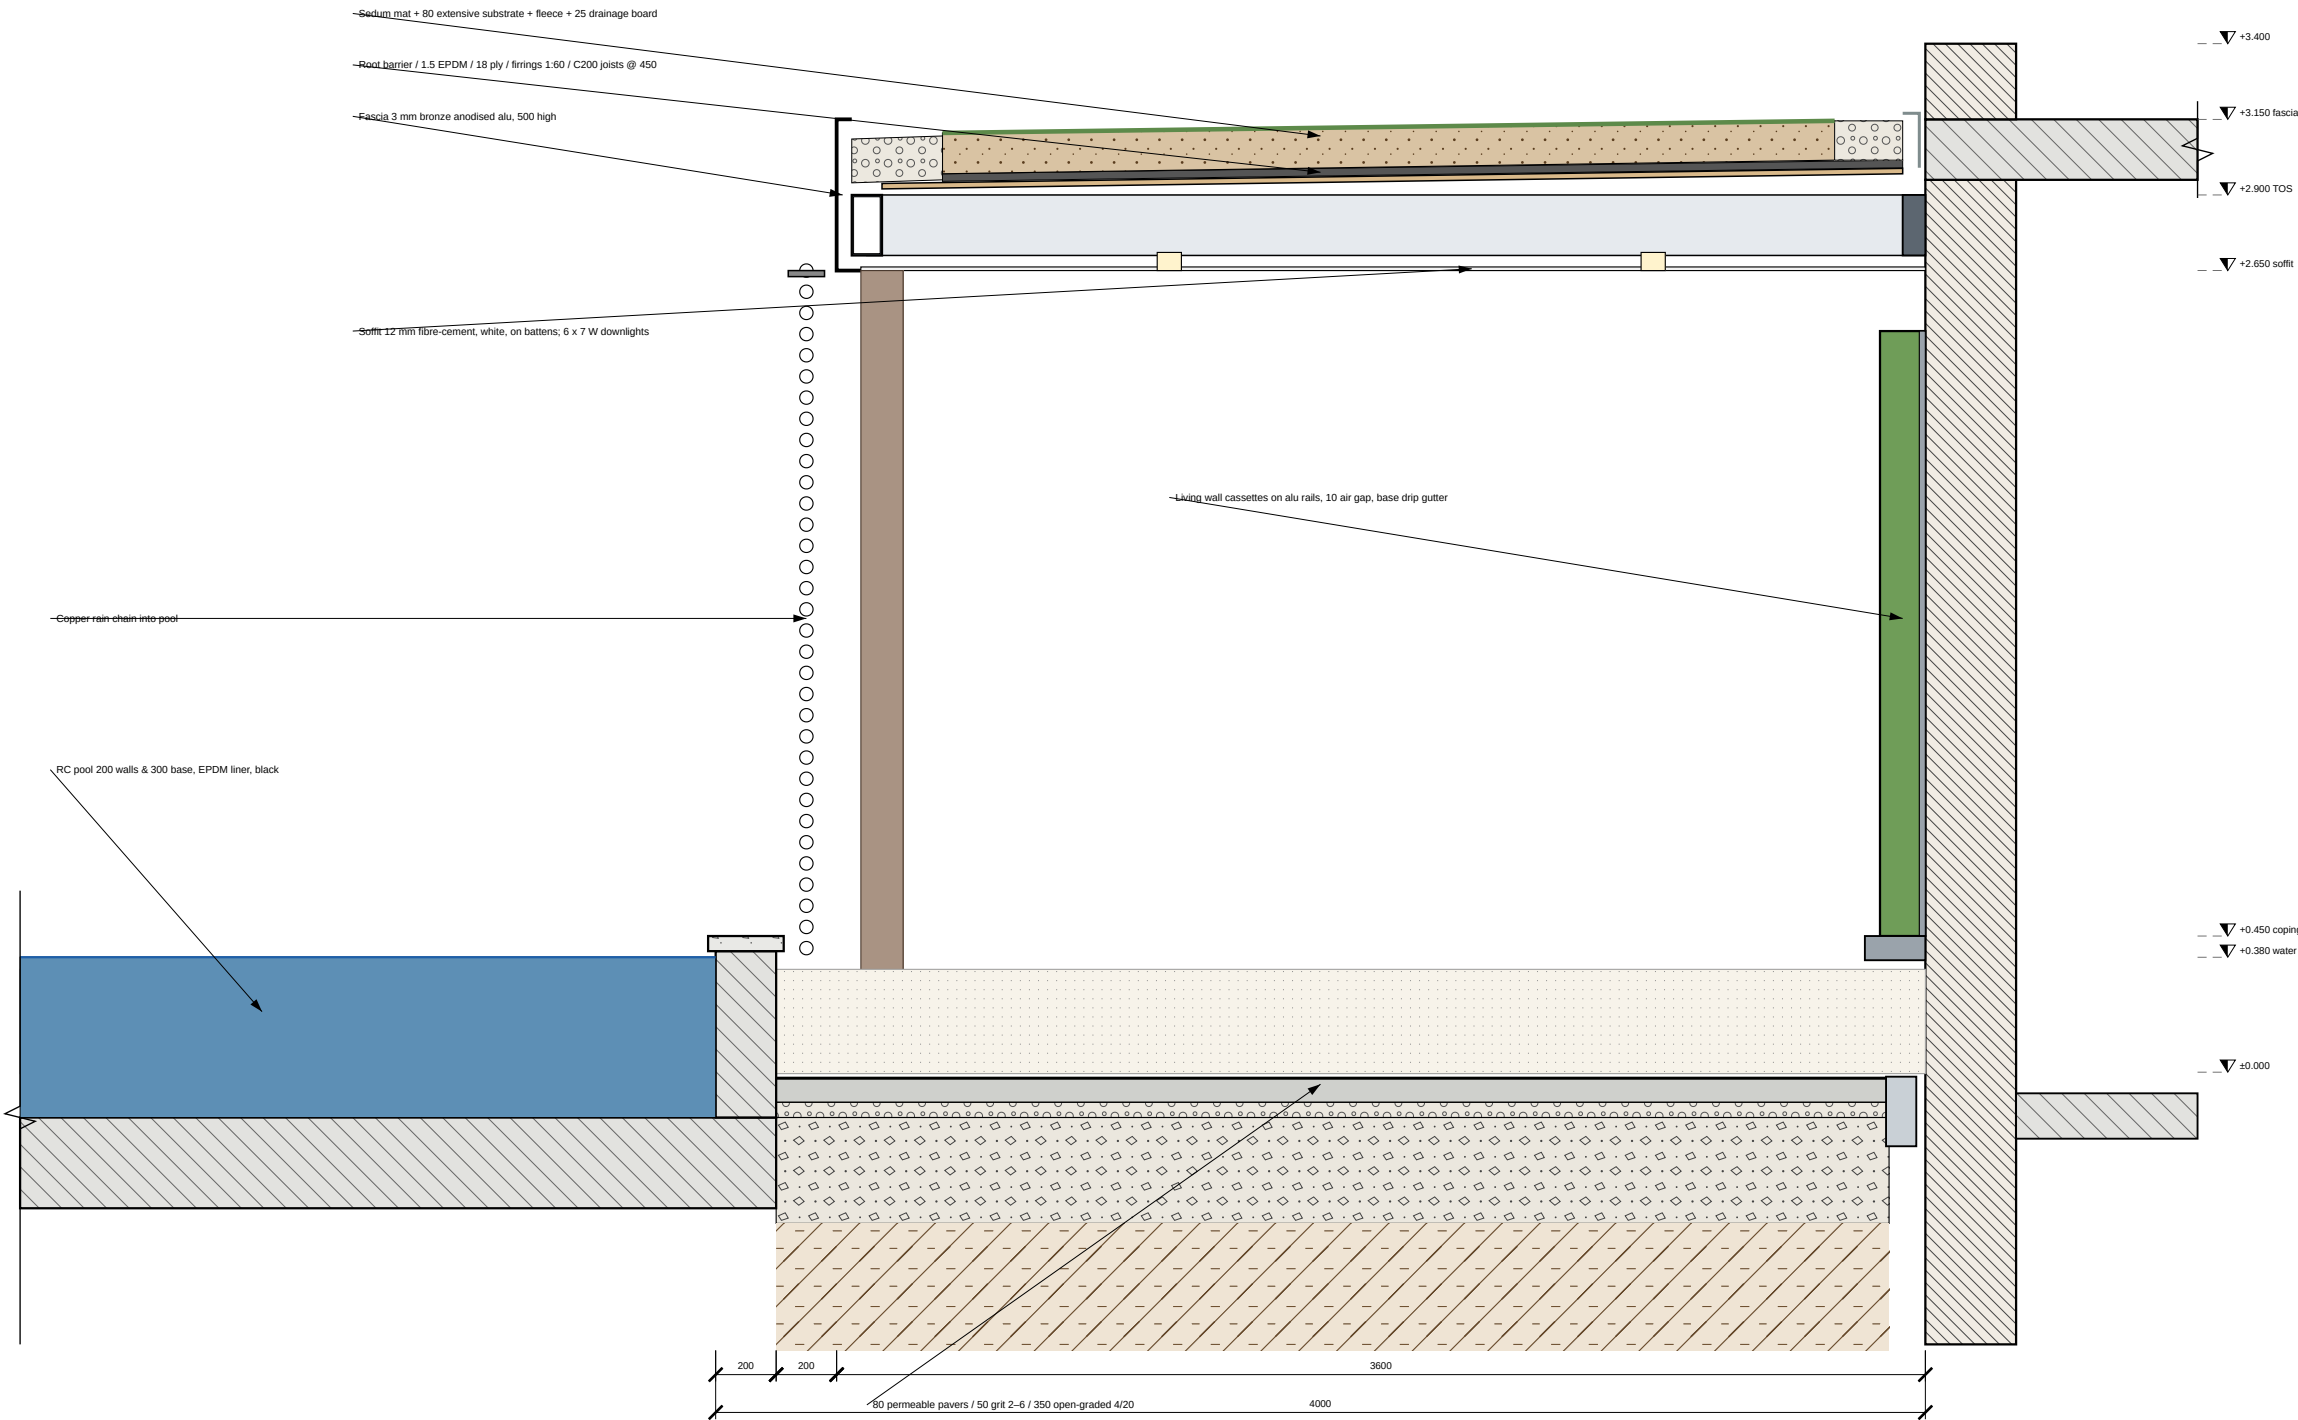

1 SECTION A-A
D-300 1:25 @ A3 through living wall, green roof & pool, looking west

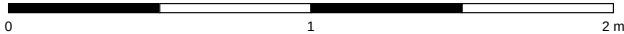

Planter kerb (existing design)

Precast coping 250x50, 25 drip both sides

1.0 EPDM liner on 300 g underlay, black

200 RC wall C35/45 XC4, Ø10 @ 200 EF

300 RC base on 50 blinding + 150 Type 1

80 permeable concrete pavers, 8 mm joints with 2-6 grit

50 bedding grit 2-6.3

350 open-graded sub-base 4/20 (storage 30% voids)

Geotextile; infiltration $\geq 1e-5$ m/s (test)

Waterproof backing: 2 coats tanking slurry

Alu rails 40 + 10 air gap, SS anchors

500x500 planted cassettes, drip line per row

Drip gutter → planter

D-500 C01

Item	Description	Unit	Qty	Rate
1	PRELIMINARIES & SURVEY			
1.1	Survey, percolation test, set-up	item	1	
2	GROUNDWORKS			
2.1	Excavate for permeable build-up (0.5 m)	m³	26.0	
2.2	RWH tank 2000 L excavation & install	item	1	
2.3	Post pads 600x600x700	no	3	
3	CANOPY STRUCTURE			
3.1	Steel frame HDG (ledger, beams, C200 @ 450)	t	0.75	
3.2	CHS 139.7x6.3 posts, MIO bronze	no	3	
3.3	Ply deck, firings, EPDM, flashings	m²	15.5	
3.4	Green roof system (sedum, substrate, layers)	m²	11.1	
3.5	Bronze fascia 500 mm	m	11.5	
3.6	Fibre-cement soffit + 6 downlights	m²	15.5	

Green roof & living wall by specialist (design & install, 2-year maintenance). Pool pump/UV sized by supplier.

Item	Description	Unit	Qty	Rate
3.7	Outlets, inspection boxes, 2 copper rain chains	item	1	
4	WATER FEATURE			
4.1	RC raised pool incl. liner, coping	item	1	
4.2	Pump, UV, weir, skimmer, lighting 2 x 12 V	item	1	
5	LIVING WALL			
5.1	Modular living wall 1.45 x 2.0 incl. plants	m²	2.9	
5.2	Irrigation controller & dosing	item	1	
6	PAVING			
6.1	Permeable pavers 80 herringbone + border	m²	52.1	
6.2	Open-graded sub-base 350 + grit 50 + geotextile	m²	52.1	
7	PLANTER (as A) & FIRE BOWL (FF&E)	item	1	
8	ELECTRICAL	item	1	
9	CONTINGENCY	%	10	

COURTYARD — PROPOSAL D

Green canopy, water & living wall — alternative to Design A (same courtyard, existing doors retained)
Client: Owner / Client
Design & drawings: Claude Code

- DRAWING NOTES
- Do not scale from this drawing. Use figured dimensions only.
 - All dimensions in millimetres; levels in metres relative to internal FFL ±0.000 (datum to be tied to site survey).
 - Contractor to verify all dimensions, levels & existing structure on site before fabrication or ordering.
 - Read with all other architectural, structural & services drawings and the specification notes (A-001).
 - Structural members are preliminary: final design, connections & calculations by a licensed structural engineer to local code before construction.
 - Report any discrepancy to the designer before proceeding.

REVISIONS		
Rev	Date	Description
C01	06.10.2026	Issued for construction / tender
P01	05.10.2026	Concept (client renders)

DESIGN PROPOSAL — developed design, buildable; confirm by survey & engineer before construction

DRAWING TITLE	
Proposal D — schedules & bill of quantities	
SCALE @ A3	DATE
NTS	06.10.2026
DRAWN / CHECKED	SERIES
CC / —	QUANTITIES

DRAWING No.

REV

D-600C01