



VERSION 1 — ROOF TO THE WALL

TALL HOUSE WALL (exist., AC units)

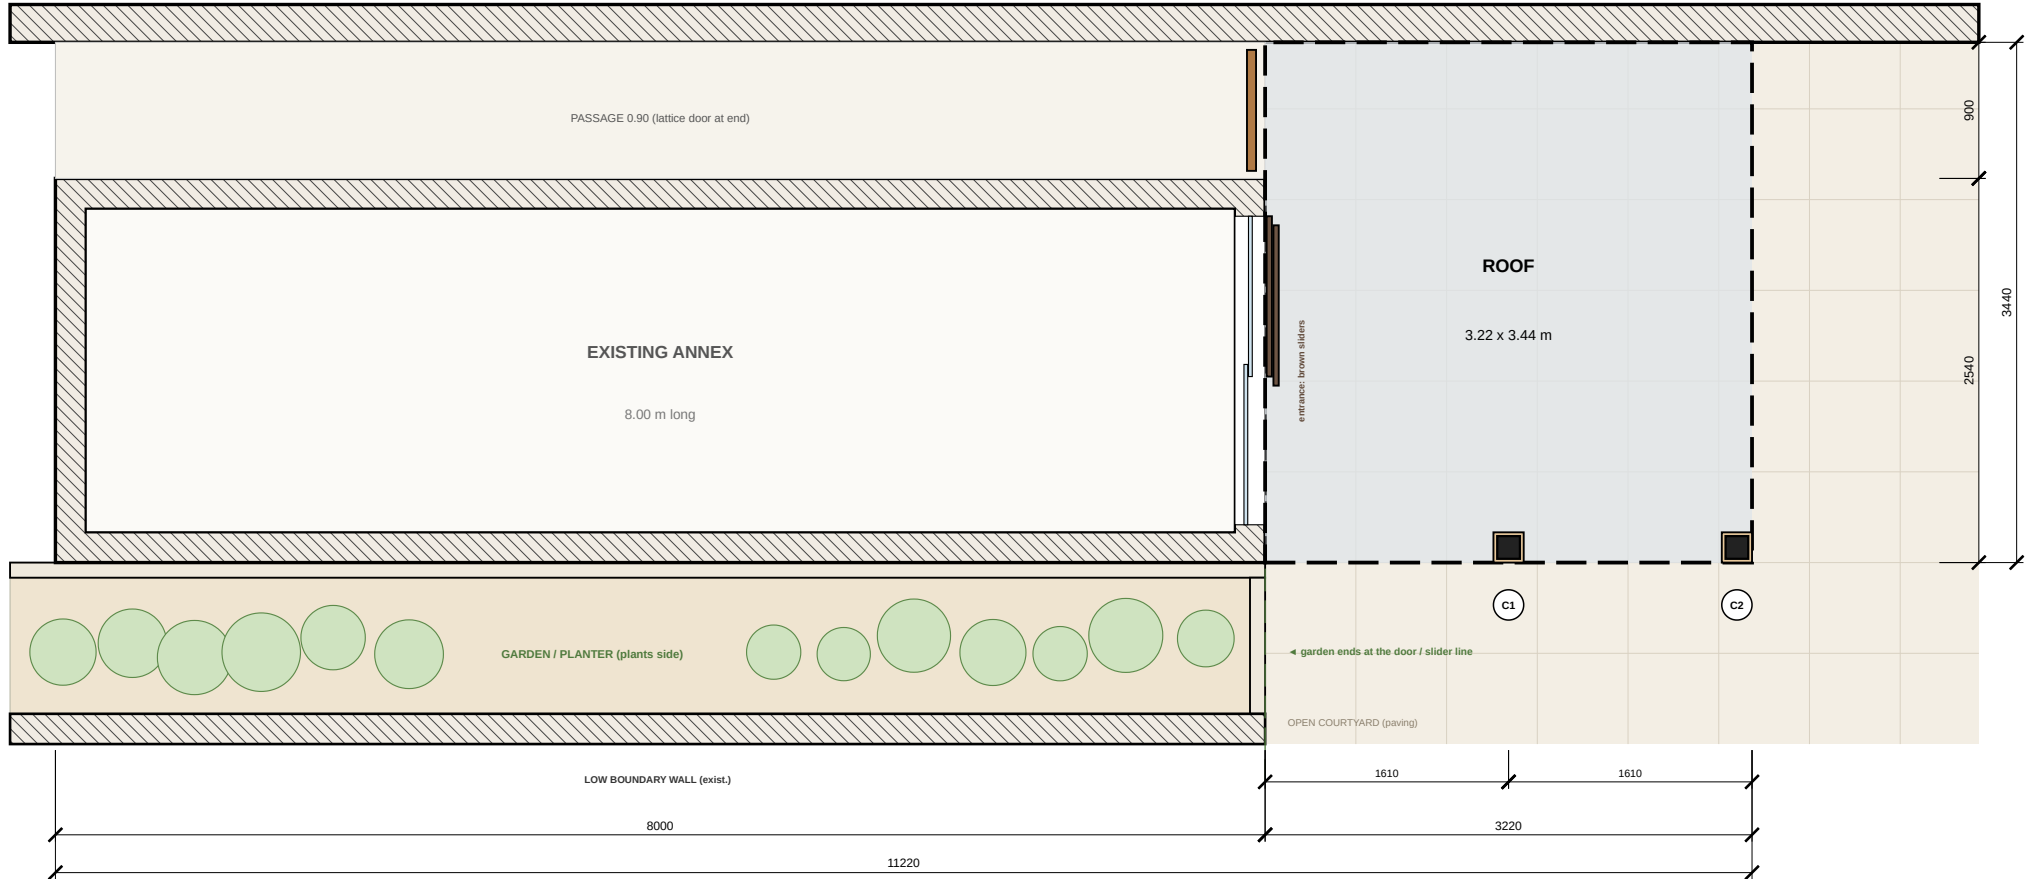

1 TOP VIEW — ANNEX, GARDEN & ROOF
V1-01 1:50 @ A3 — garden ends at the door line; trees = background

2/V1-01 ROOF FRAMING PLAN — 1:30

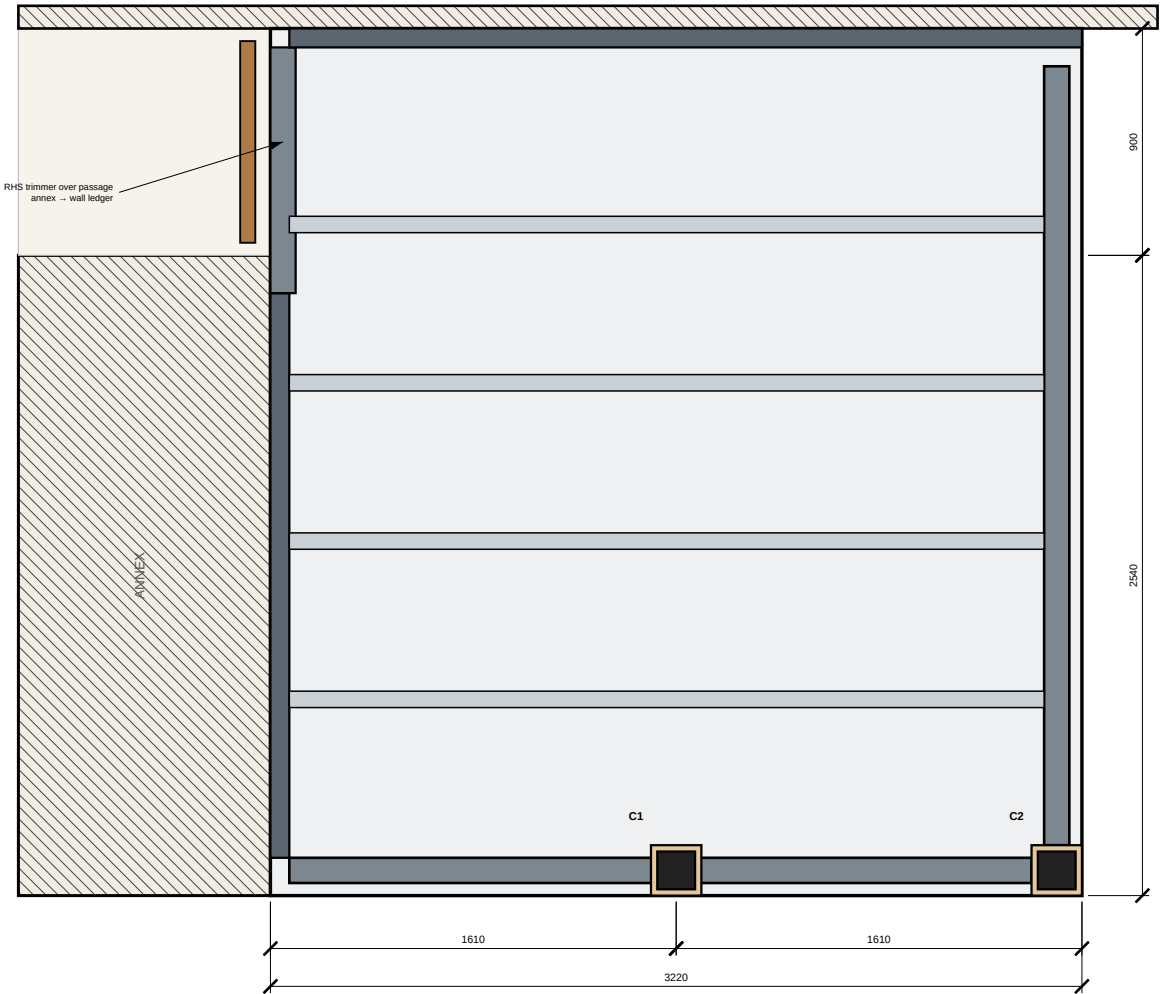

THIS VERSION
roof 3.22 x 3.44 up to the tall wall (bears on wall ledger + curved brackets); 2 columns on the plants side.
Roof fixed to the annex end façade AND to the tall house wall (steel ledgers, resin anchors); covers the passage in front of the lattice door (RHS trimmer over the passage, annex - wall ledger).
C1 in the middle of the plants edge, C2 at the corner.
COMMON
Roof 3.22 m from the annex façade along the top edge. Underside +2.36, fascia 0.43 (top +2.79); columns 200x200, 0.13 above roof, curved bracket under the junction (client section).
Garden & low wall stop at the annex end façade (door / slider line); beyond it open paving.
Falls 1:70 to the concealed gutter at the free edge; rainwater down C2.



COURTYARD ROOF — V1

VERSION 1 — ROOF TO THE WALL: roof 3.22 x 3.44 up to the tall wall (bears on wall ledger + curved brackets); 2 columns on the plants side
Client: Owner / Client
Design & drawings: Claude Code

- DRAWING NOTES**
- Do not scale from this drawing. Use figured dimensions only.
 - All dimensions in millimetres; levels in metres relative to internal FFL ±0.000 (datum to be tied to site survey).
 - Contractor to verify all dimensions, levels & existing structure on site before fabrication or ordering.
 - Read with all other architectural, structural & services drawings and the specification notes (A-001).
 - Structural members are preliminary: final design, connections & calculations by a licensed structural engineer to local code before construction.
 - Report any discrepancy to the designer before proceeding.

REVISIONS		
Rev	Date	Description
C05	07.10.2026	Garden ends at door/slider line; triangular versions V1/V2; 3D views
C04	07.10.2026	Two versions V1/V2 per client sections & site photo
C02	07.10.2026	Canopy to client sketch: 8.00 house, roof 3.22, u/s 2.36, fascia 0.43


PREVIEW FOR CLIENT REVIEW — per client sketch, mark-ups & site photo; not for construction

DRAWING TITLE	
V1 ROOF TO WALL top view & roof framing	
SCALE @ A3 1:50 / 1:30	DATE 07.10.2026
DRAWN / CHECKED CC / —	SERIES ARCHITECTURAL


DRAWING No.	REV
V1-01	C05

VERSION 1 — ROOF TO THE WALL

1/V1-02 VIEW TO ANNEX FAÇADE (as site photo) — 1:50

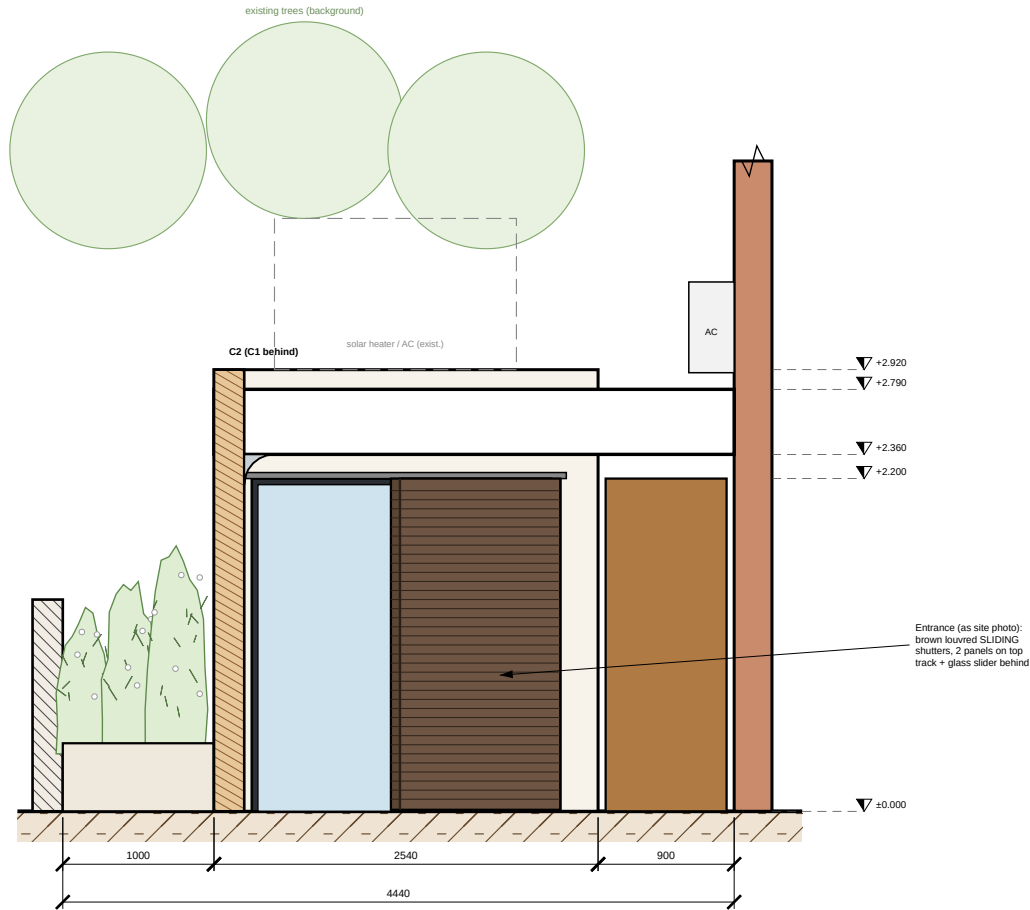


2/V1-02 PLANTS-SIDE ELEVATION — C1 + C2 — 1:50

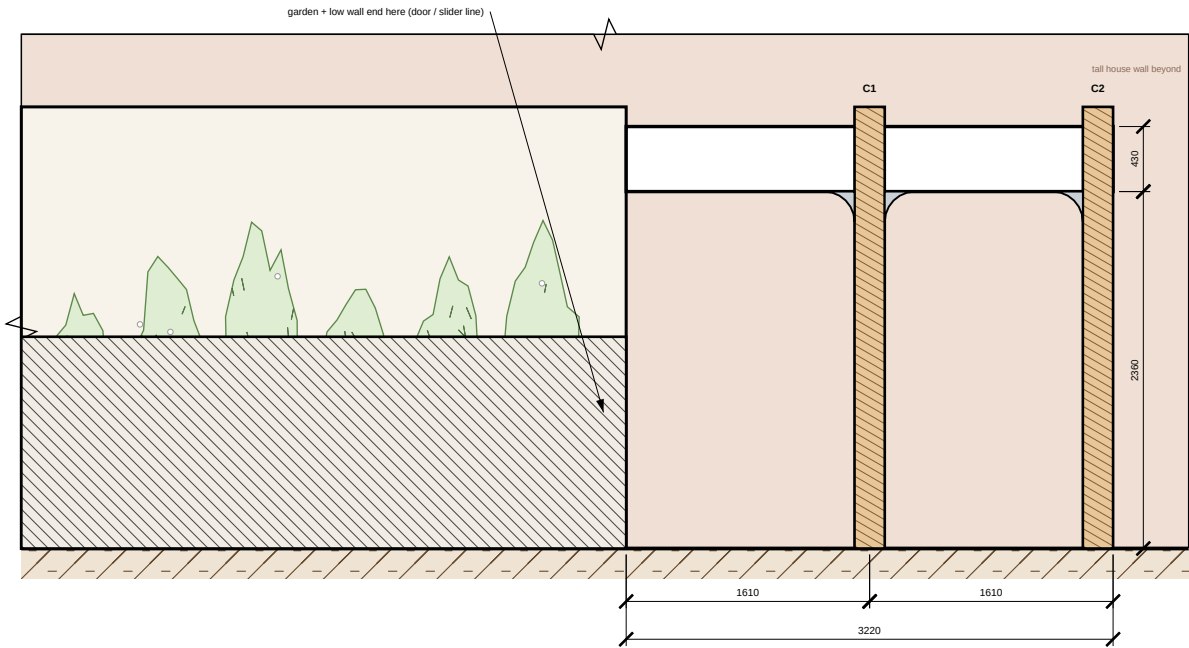


NOTES
roof 3.22 x 3.44 up to the tall wall (bears on wall ledger + curved brackets); 2 columns on the plants side.
Underside +2.36, fascia 0.43 (top +2.79); columns 0.13 above roof.
Garden + low wall end at the annex end façade (door / slider line). Trees are existing, in the background.
Refined roof section & details: sheet V1-03.

3/V1-02 SECTION ACROSS AT C1 — 1:50 (refined: V1-03)

tall wall left — plants side right

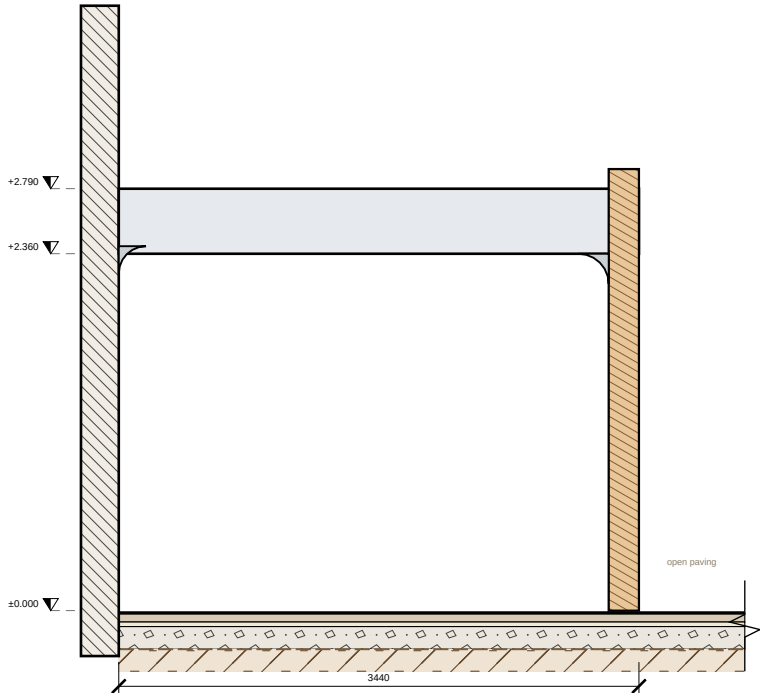

4/V1-02 3D VIEW — from the plants side (courtyard)

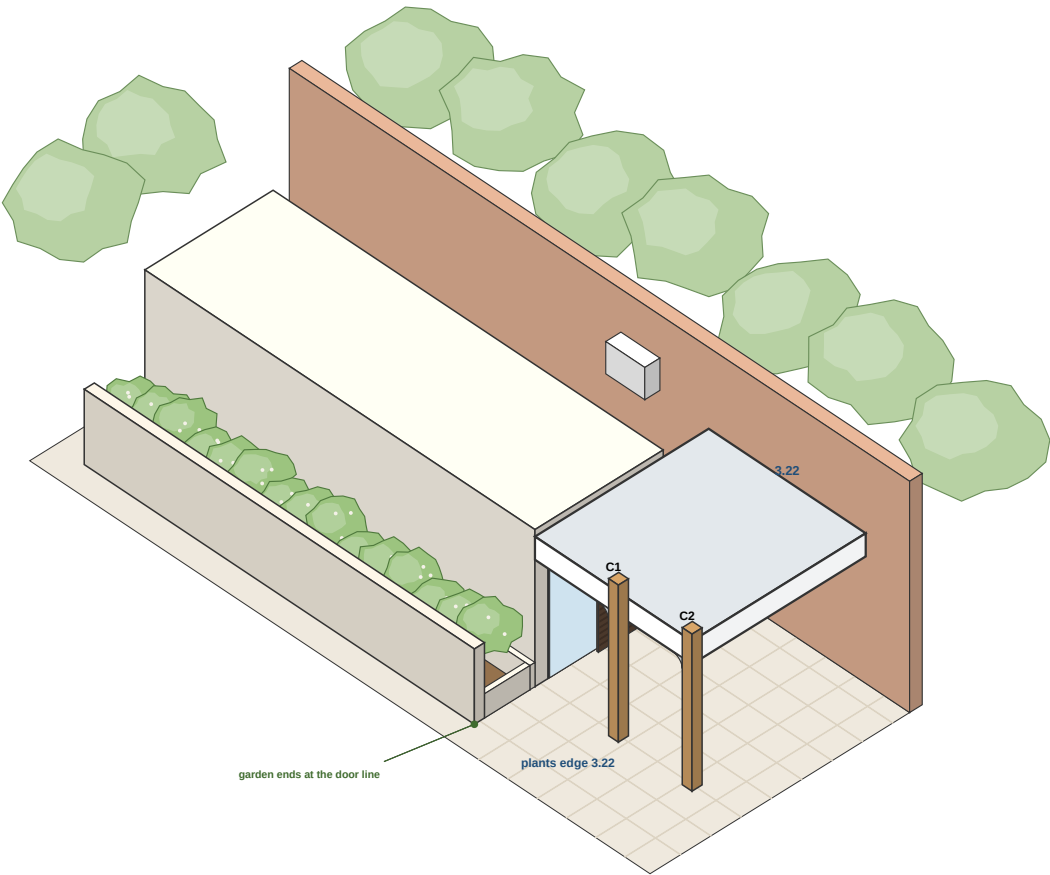

COURTYARD ROOF — V1

VERSION 1 — ROOF TO THE WALL: roof 3.22 x 3.44 up to the tall wall (bears on wall ledger + curved brackets); 2 columns on the plants side
Client: Owner / Client
Design & drawings: Claude Code

- DRAWING NOTES**
- Do not scale from this drawing. Use figured dimensions only.
 - All dimensions in millimetres; levels in metres relative to internal FFL ±0.000 (datum to be tied to site survey).
 - Contractor to verify all dimensions, levels & existing structure on site before fabrication or ordering.
 - Read with all other architectural, structural & services drawings and the specification notes (A-001).
 - Structural members are preliminary: final design, connections & calculations by a licensed structural engineer to local code before construction.
 - Report any discrepancy to the designer before proceeding.

REVISIONS		
Rev	Date	Description
C05	07.10.2026	Garden ends at door/slider line; triangular versions V1/V2; 3D views
C04	07.10.2026	Two versions V1/V2 per client sections & site photo
C02	07.10.2026	Canopy to client sketch: 8.00 house, roof 3.22, u/s 2.36, fascia 0.43

PREVIEW FOR CLIENT REVIEW — per client sketch, mark-ups & site photo; not for construction

DRAWING TITLE	
V1 ROOF TO WALL views, section & 3D view	
SCALE @ A3	DATE
1:50	07.10.2026
DRAWN / CHECKED	SERIES
CC / —	ARCHITECTURAL


DRAWING No. REV

V1-02 C05


VERSION 1 — ROOF TO THE WALL

1/V1-03 ROOF SECTION ACROSS AT C1 — 1:25


(as client sketch A: roof runs to the wall)

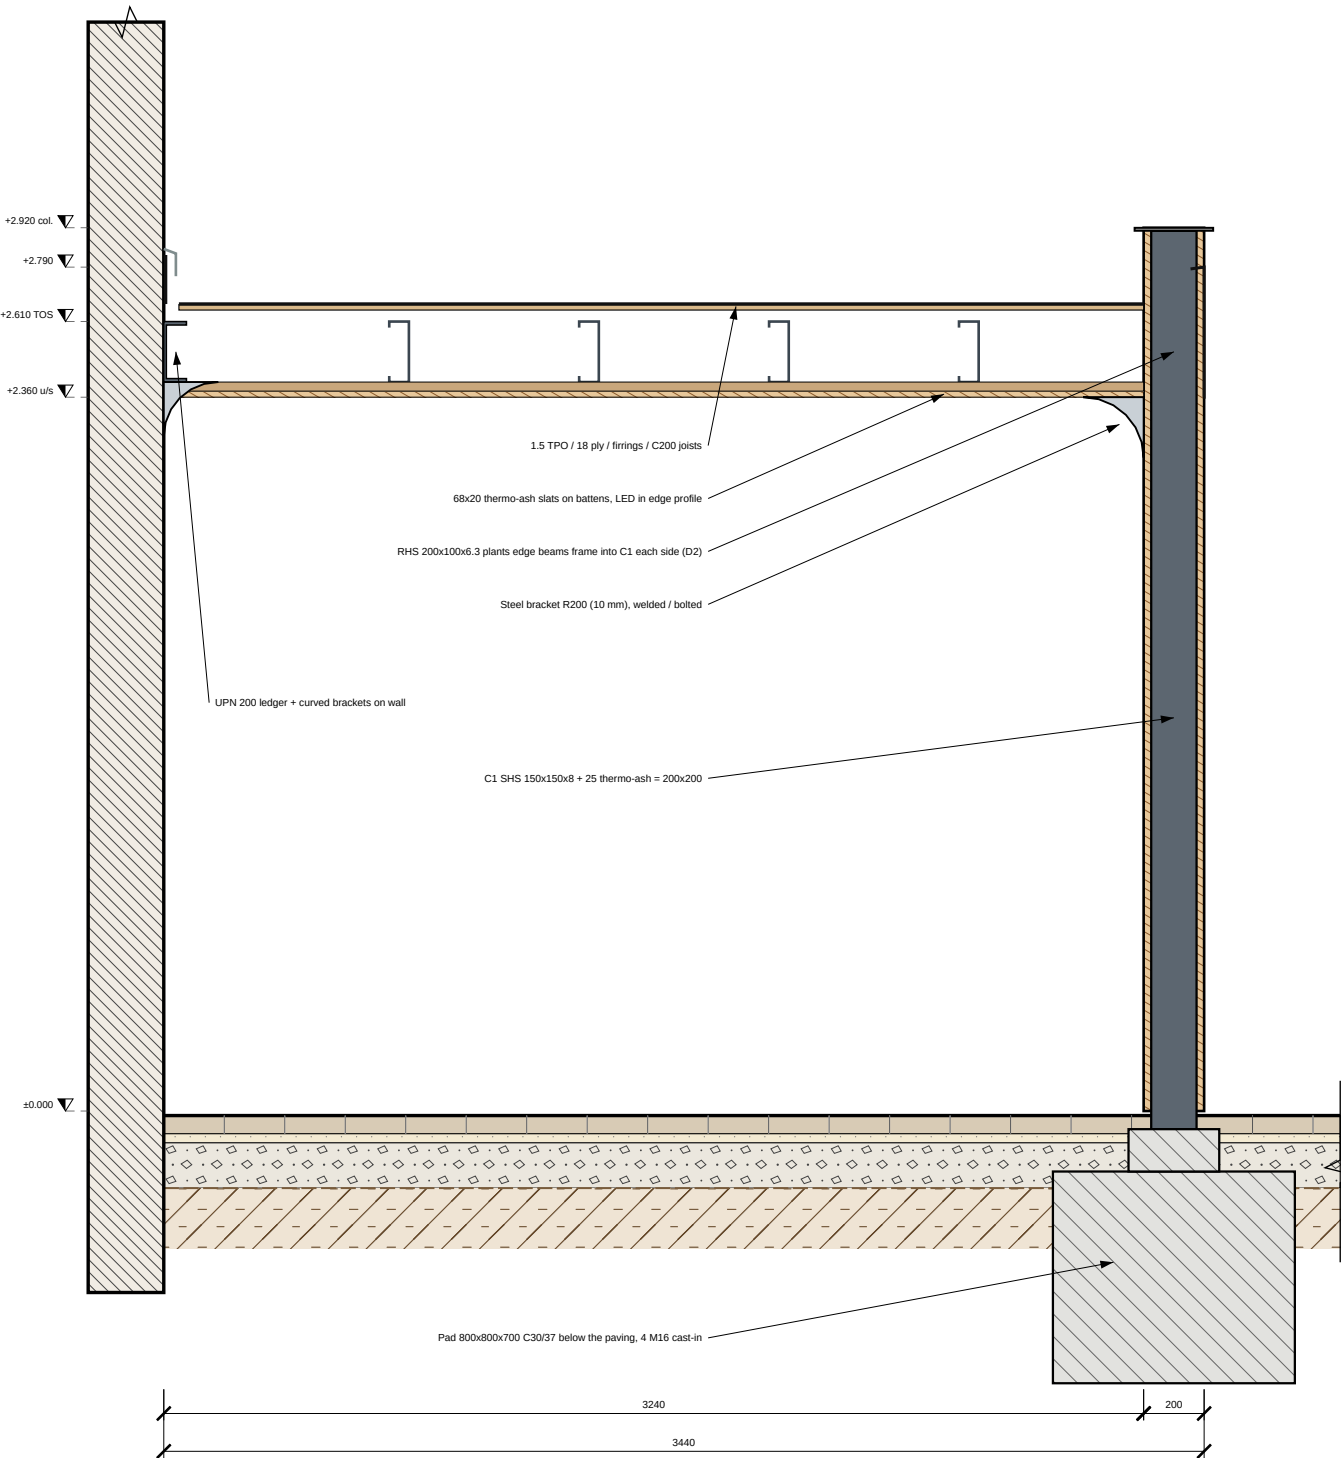


SPECIFICATION
Steel S355, hot-dip galvanised; columns & brackets powder-coated RAL 9010 or timber-clad (thermo-ash).
Roof: TPO 1.5 on 18 mm marine ply on tapered firrings (fall 1:70 to the free-edge box gutter).
Soffit: thermo-ash 68x20 slats, LED 2700 K in perimeter profile. Fascia 3 mm aluminium RAL 9010, 0.43 m.
Wall ledger & brackets into sound masonry/RC — engineer to confirm anchors.

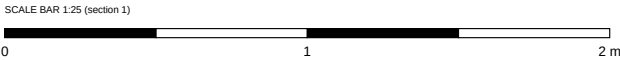


D1 ROOF TO WALL (client sketch A) — 1:15

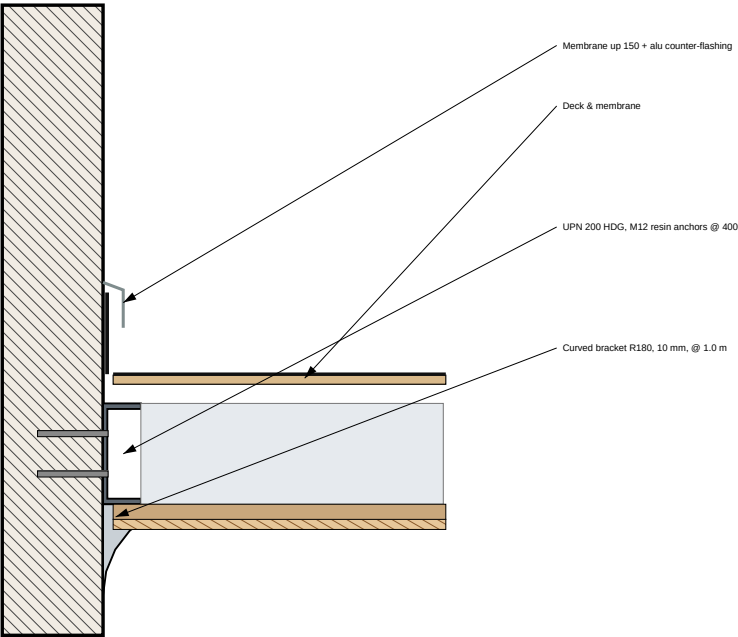

D2 COLUMN / ROOF JUNCTION (plants side) — 1:15

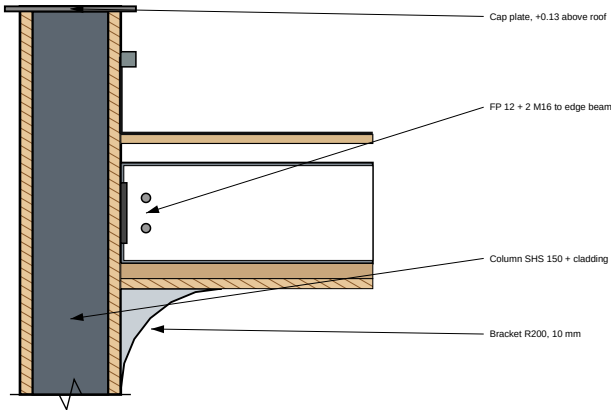

D3 CORNER AT C2 — PLAN 1:15

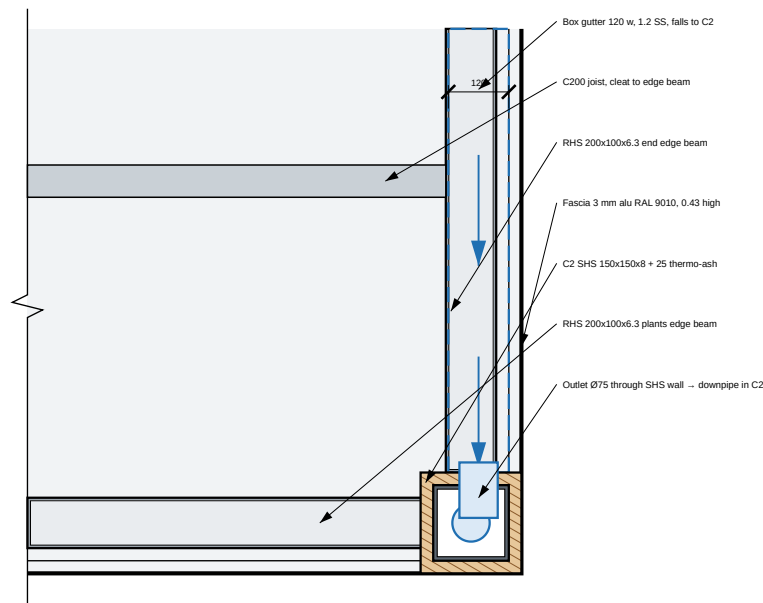

COURTYARD ROOF — V1

VERSION 1 — ROOF TO THE WALL: roof 3.22 x 3.44 up to the tall wall (bears on wall ledger + curved brackets); 2 columns on the plants side
Client: Owner / Client
Design & drawings: Claude Code

- DRAWING NOTES**
- Do not scale from this drawing. Use figured dimensions only.
 - All dimensions in millimetres; levels in metres relative to internal FFL ±0.000 (datum to be tied to site survey).
 - Contractor to verify all dimensions, levels & existing structure on site before fabrication or ordering.
 - Read with all other architectural, structural & services drawings and the specification notes (A-001).
 - Structural members are preliminary: final design, connections & calculations by a licensed structural engineer to local code before construction.
 - Report any discrepancy to the designer before proceeding.

REVISIONS		
Rev	Date	Description
C05	07.10.2026	Garden ends at door/slider line; triangular versions V1/V2; 3D views
C04	07.10.2026	Two versions V1/V2 per client sections & site photo
C02	07.10.2026	Canopy to client sketch: 8.00 house, roof 3.22, u/s 2.36, fascia 0.43


PREVIEW FOR CLIENT REVIEW — per client sketch, mark-ups & site photo; not for construction

DRAWING TITLE	
V1 ROOF TO WALL roof section & details	
SCALE @ A3 1:25 / 1:15 / 1:20	DATE 07.10.2026
DRAWN / CHECKED CC / —	SERIES ARCHITECTURAL

DRAWING No. **V1-03** REV **C05**

VERSION 2 — 0.90 m VOID + 2 STEEL RODS

TALL HOUSE WALL (exist., AC units)

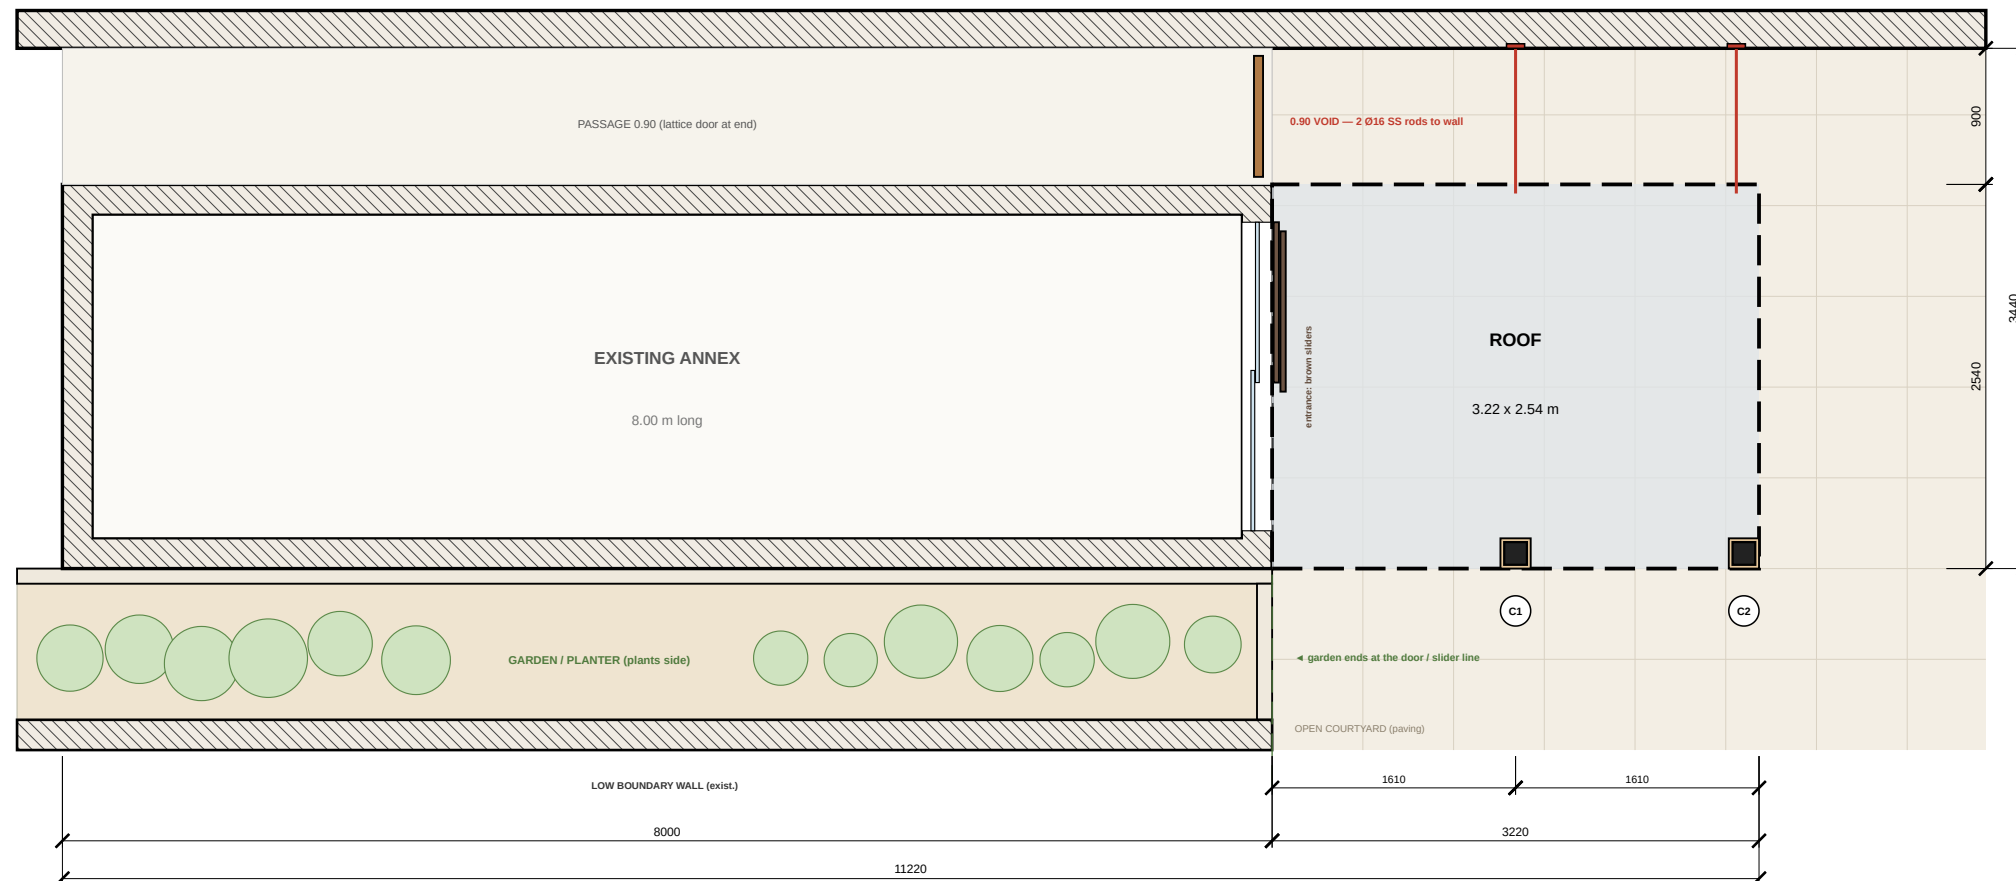

COURTYARD ROOF — V2

VERSION 2 — 0.90 m VOID + 2 STEEL RODS: roof 3.22 x 2.54; 0.90 m void
left open; void edge tied to the tall wall with 2 slim Ø16 stainless
rods (rising ≈ 30°); 2 columns on the plants side
Client: Owner / Client
Design & drawings: Claude Code


DRAWING NOTES

1. Do not scale from this drawing. Use figured dimensions only.
2. All dimensions in millimetres; levels in metres relative to internal FFL ± 0.000 (datum to be tied to site survey).
3. Contractor to verify all dimensions, levels & existing structure on site before fabrication or ordering.
4. Read with all other architectural, structural & services drawings and the specification notes (A-001).
5. Structural members are preliminary: final design, connections & calculations by a licensed structural engineer to local code before construction.
6. Report any discrepancy to the designer before proceeding.

1 TOP VIEW — ANNEX, GARDEN & ROOF

V2-01 1:50 @ A3 — garden ends at the door line; trees = background

2/V2-01 ROOF FRAMING PLAN — 1:30

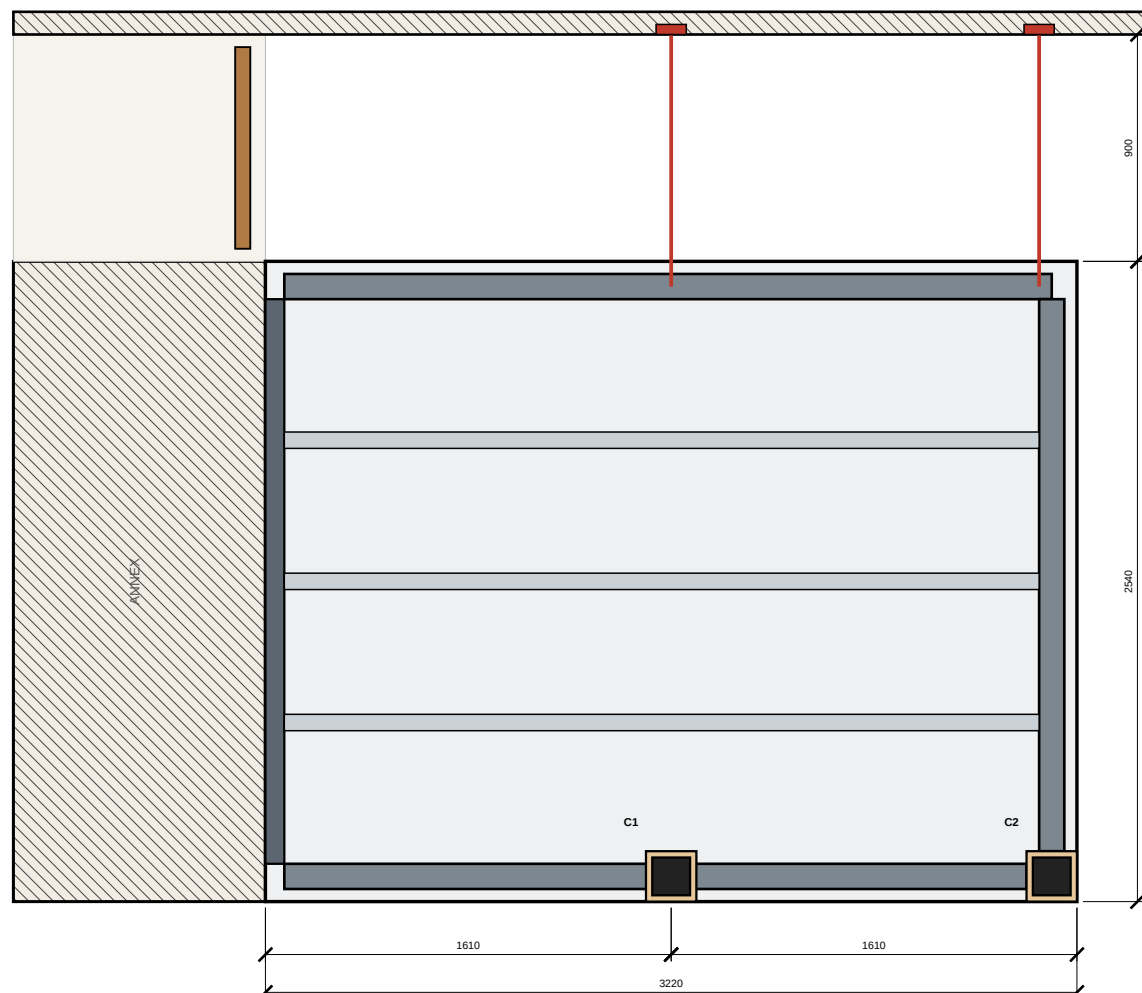

THIS VERSION

roof 3.22 x 2.54; 0.90 m void left open; void edge tied to the tall wall with 2 slim Ø16 stainless rods (rising $\approx 30^\circ$); 2 columns on the plants side. Roof fixed to the annex end facade (ledge). The 0.90 m passage to the lattice door stays open.


Void edge hung from the tall house wall on 2 Ø16 stainless rods (turnbuckles, wall plates) — slim, almost invisible. C1 in the middle of the plants edge. C2 at the corner.

COMMON

Roof 3.22 m from the annex façade along the top edge. Underside +2.36, fascia 0.43 (top +2.79); columns 200x200, 0.13 above roof, curved bracket under the junction (client section).

Garden & low wall stop at the annex end façade (door / slider line); beyond it open paving.
Falls 1:70 to the concealed gutter at the free edge; rainwater down C2.

SCALE BAR 1:50 (top view)

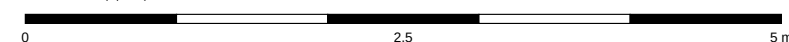

REVISIONS

Rev	Date	Description
C05	07.10.2026	Garden ends at door/slider line; triangular versions V1TV2T; 3D views
C04	07.10.2026	Two versions V1/V2 per client sections & site photo
C02	07.10.2026	Canopy to client sketch: 8.00 house, roof 3.22, u/s 2.36, fascia 0.43

PREVIEW FOR CLIENT REVIEW — per client sketch, mark-ups & site photo; not for construction

DRAWING TITLE

V2 VOID + RODS
top view & roof framing

SCALE @ A3 1:50 / 1:30	DATE 07.10.2026
DRAWN / CHECKED CC / —	SERIES ARCHITECTURAL

DRAWING No.


REV

V2-01


C05

VERSION 2 — 0.90 m VOID + 2 STEEL RODS

1/V2-02 VIEW TO ANNEX FAÇADE (as site photo) — 1:50

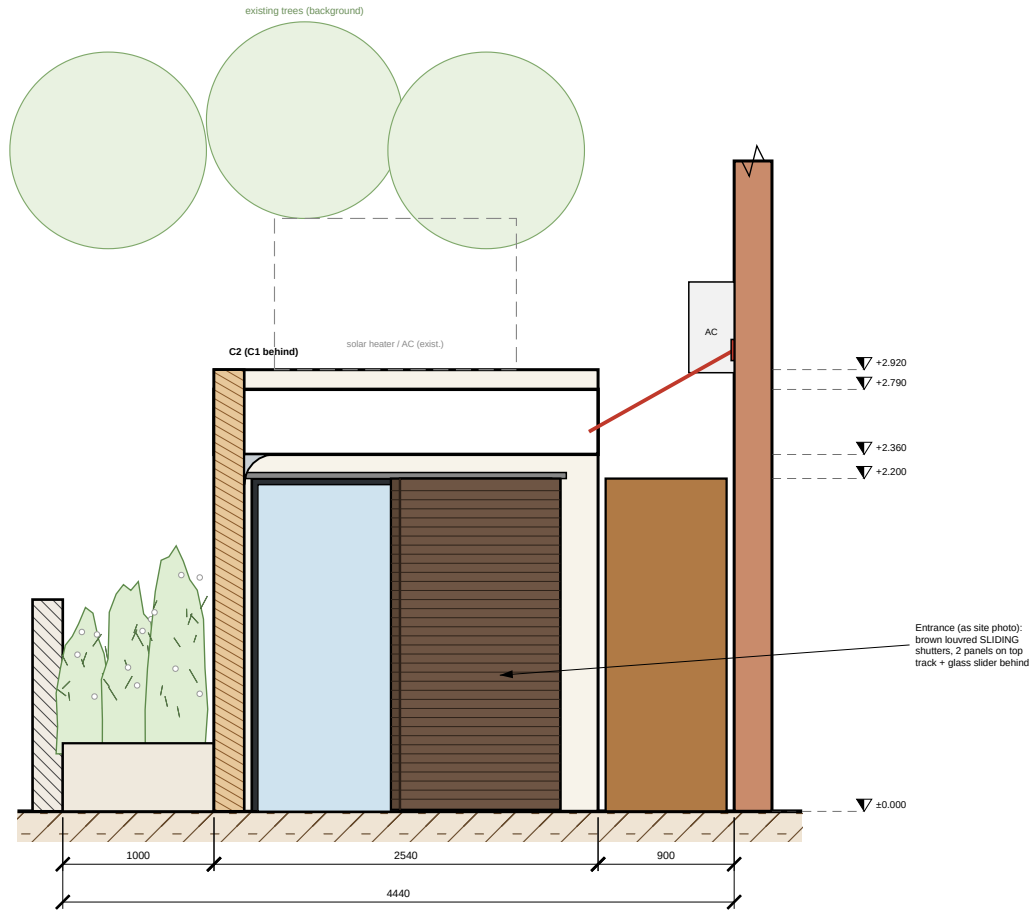


2/V2-02 PLANTS-SIDE ELEVATION — C1 + C2 — 1:50

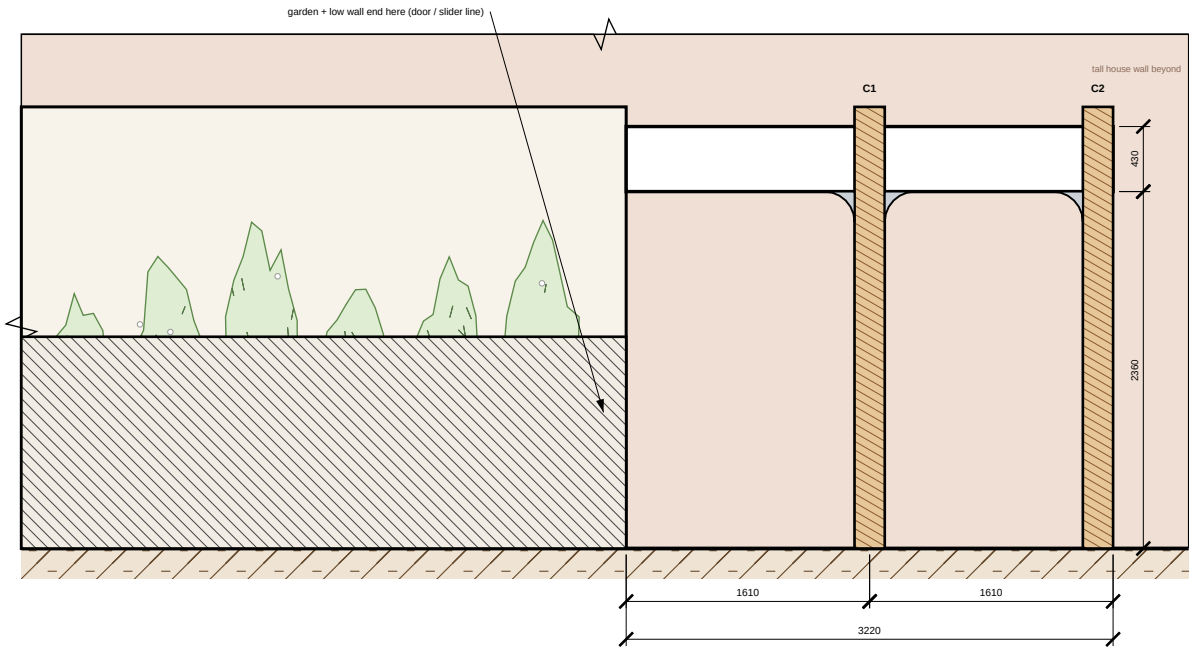


NOTES
roof 3.22 x 2.54; 0.90 m void left open; void edge tied to the tall wall with 2 slim Ø16 stainless rods (rising = 30°); 2 columns on the plants side.
Underside +2.36; fascia 0.43 (top +2.79); columns 0.13 above roof.
Garden + low wall end at the annex end façade (door / slider line). Trees are existing, in the background.
Refined roof section & details: sheet V2-03.

3/V2-02 SECTION ACROSS AT C1 — 1:50 (refined: V2-03)

tall wall left — plants side right

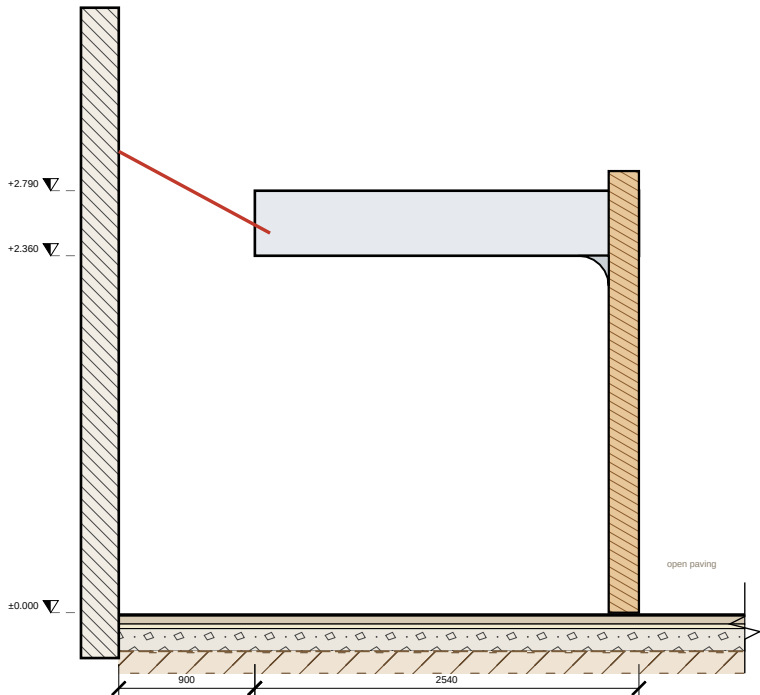

4/V2-02 3D VIEW — from the plants side (courtyard)

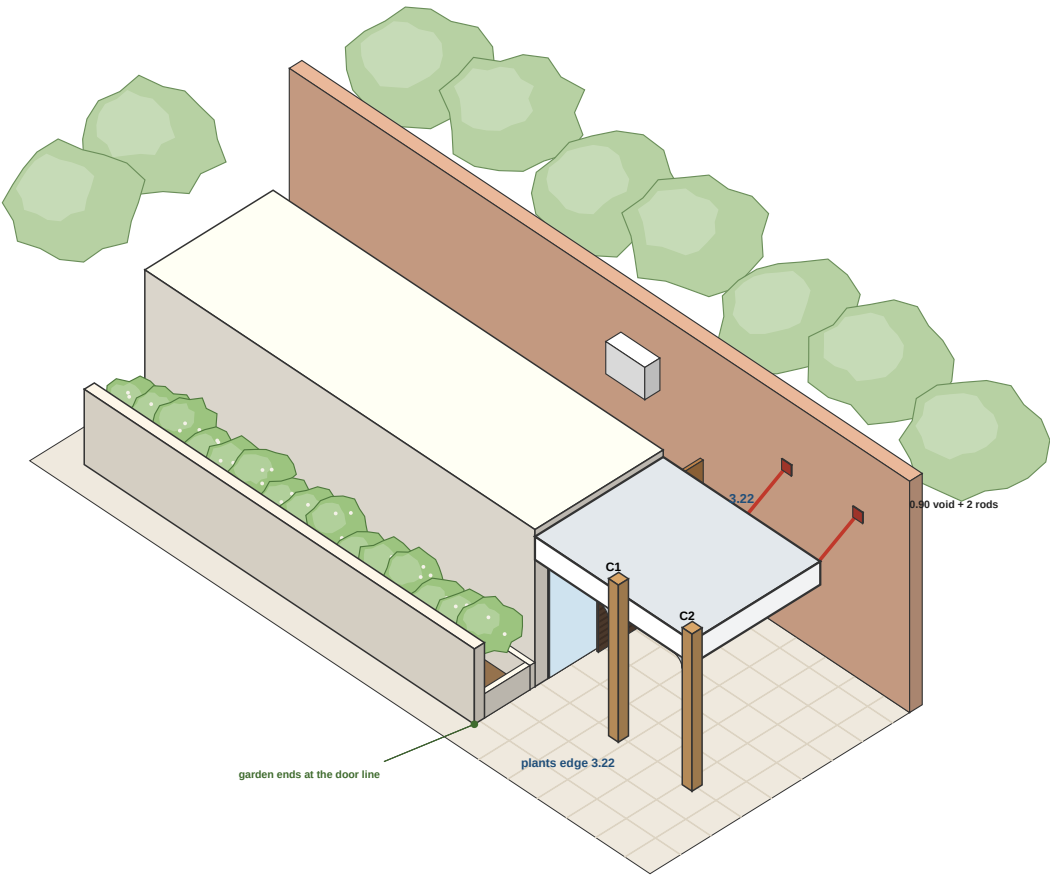

COURTYARD ROOF — V2

VERSION 2 — 0.90 m VOID + 2 STEEL RODS: roof 3.22 x 2.54; 0.90 m void left open; void edge tied to the tall wall with 2 slim Ø16 stainless rods (rising = 30°); 2 columns on the plants side
Client: Owner / Client
Design & drawings: Claude Code

DRAWING NOTES

- Do not scale from this drawing. Use figured dimensions only.
- All dimensions in millimetres; levels in metres relative to internal FFL ±0.000 (datum to be tied to site survey).
- Contractor to verify all dimensions, levels & existing structure on site before fabrication or ordering.
- Read with all other architectural, structural & services drawings and the specification notes (A-001).
- Structural members are preliminary: final design, connections & calculations by a licensed structural engineer to local code before construction.
- Report any discrepancy to the designer before proceeding.

REVISIONS

Rev	Date	Description
C05	07.10.2026	Garden ends at door/slider line; triangular versions V1/V2; 3D views
C04	07.10.2026	Two versions V1/V2 per client sections & site photo
C02	07.10.2026	Canopy to client sketch: 8.00 house, roof 3.22, u/s 2.36, fascia 0.43

PREVIEW FOR CLIENT REVIEW — per client sketch, mark-ups & site photo; not for construction

DRAWING TITLE

V2 VOID + RODS
views, section & 3D view

SCALE @ A3

1:50

DRAWN / CHECKED

CC / —

DATE

07.10.2026

SERIES

ARCHITECTURAL

DRAWING No.

REV


V2-02

C05

VERSION 2 — 0.90 m VOID + 2 STEEL RODS

1/V2-03 ROOF SECTION ACROSS AT C1 — 1:25

(as client sketch B: roof stops, rods to the wall)

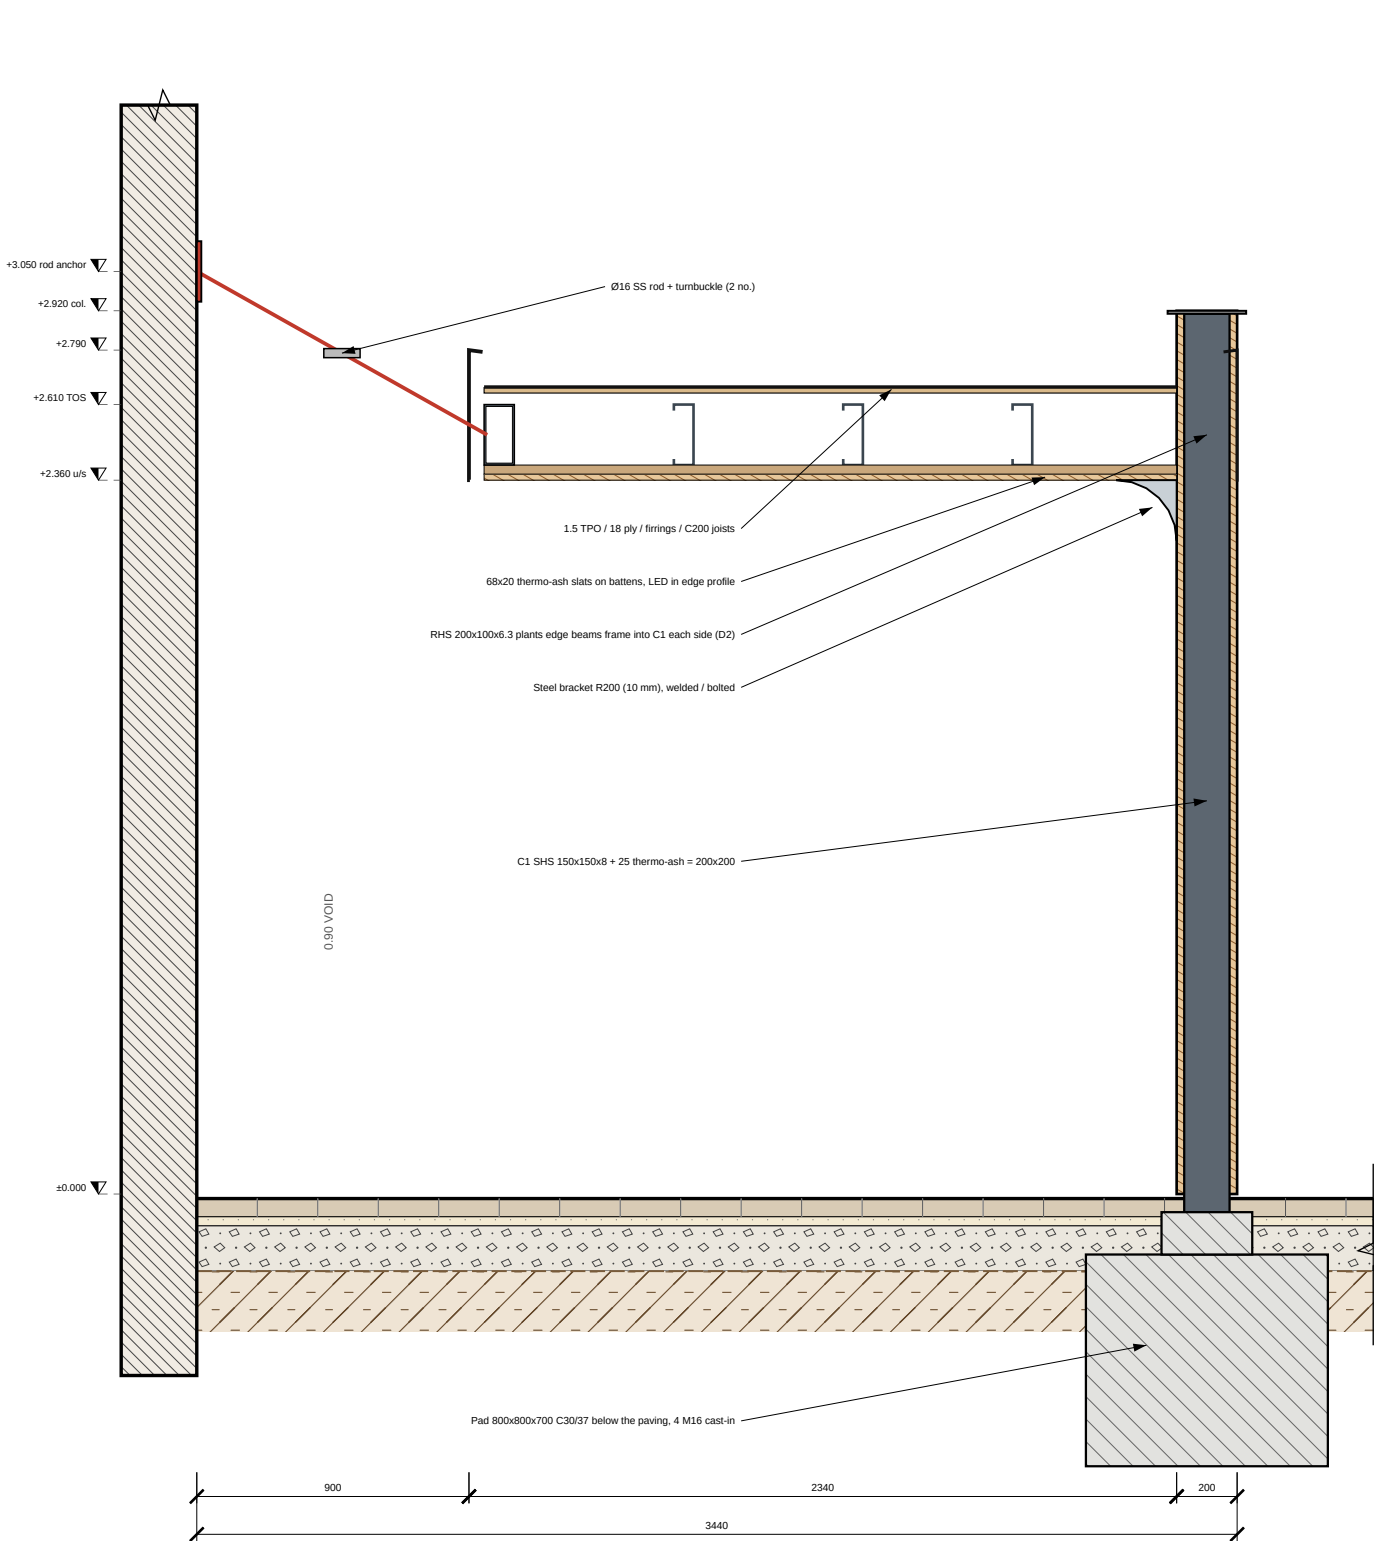


SPECIFICATION
Steel S355, hot-dip galvanised; columns & brackets powder-coated RAL 9010 or timber-clad (thermo-ash).
Roof: TPO 1.5 on 18 mm marine ply on tapered firrings (fall 1:70 to the free-edge box gutter).
Soffit: thermo-ash 68x20 slats, LED 2700 K in perimeter profile. Fascia 3 mm aluminium RAL 9010, 0.43 m.
Rods: Ø16 stainless 316, fork ends, turnbuckle, = 30° rise; engineer to confirm wall anchors.


SCALE BAR 1:25 (section 1)




D1 ROD TO WALL (client sketch B) — 1:20

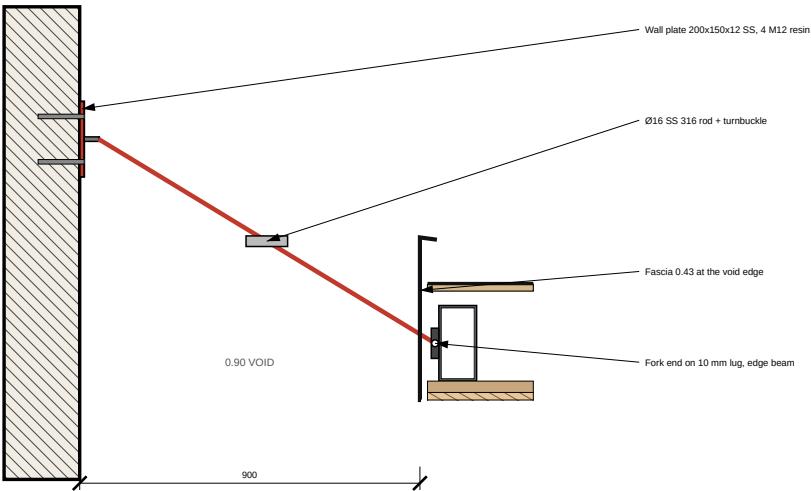

D2 COLUMN / ROOF JUNCTION (plants side) — 1:15

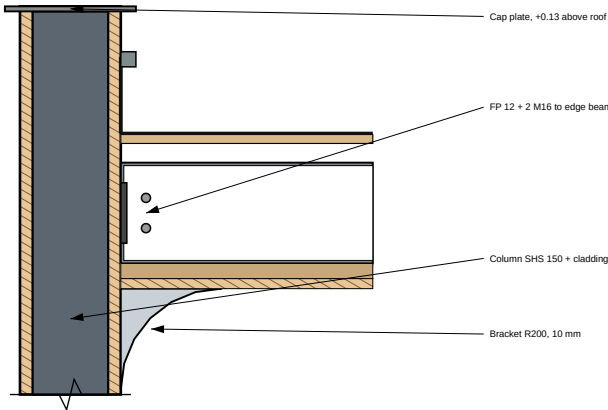

D3 CORNER AT C2 — PLAN 1:15

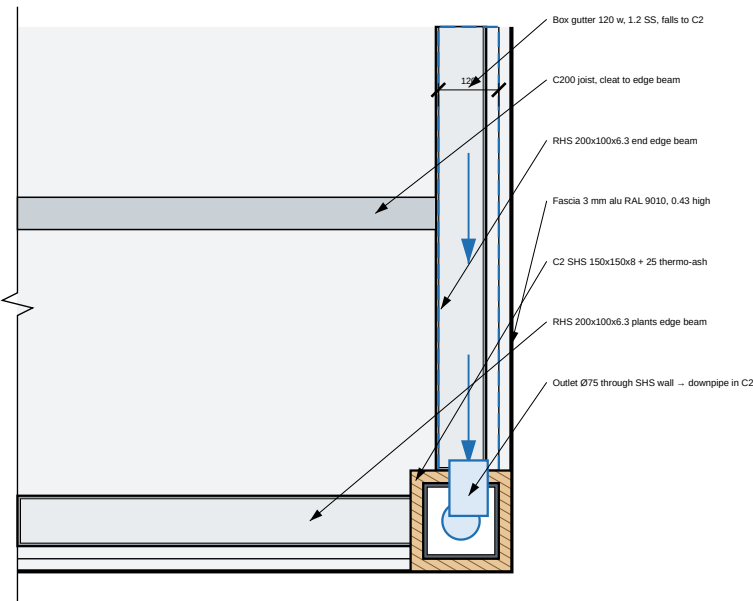

COURTYARD ROOF — V2

VERSION 2 — 0.90 m VOID + 2 STEEL RODS: roof 3.22 x 2.54; 0.90 m void left open; void edge tied to the tall wall with 2 slim Ø16 stainless rods (rising ≈ 30°); 2 columns on the plants side
Client: Owner / Client
Design & drawings: Claude Code

DRAWING NOTES

- Do not scale from this drawing. Use figured dimensions only.
- All dimensions in millimetres; levels in metres relative to internal FFL ±0.000 (datum to be tied to site survey).
- Contractor to verify all dimensions, levels & existing structure on site before fabrication or ordering.
- Read with all other architectural, structural & services drawings and the specification notes (A-001).
- Structural members are preliminary: final design, connections & calculations by a licensed structural engineer to local code before construction.
- Report any discrepancy to the designer before proceeding.

REVISIONS

Rev	Date	Description
C05	07.10.2026	Garden ends at door/slider line; triangular versions V1/V2; 3D views
C04	07.10.2026	Two versions V1/V2 per client sections & site photo
C02	07.10.2026	Canopy to client sketch: 8.00 house, roof 3.22, u/s 2.36, fascia 0.43

PREVIEW FOR CLIENT REVIEW — per client sketch, mark-ups & site photo; not for construction

DRAWING TITLE
V2 VOID + RODS
roof section & details


SCALE @ A3 1:25 / 1:15 / 1:20	DATE 07.10.2026
DRAWN / CHECKED CC / —	SERIES ARCHITECTURAL

DRAWING No. REV

V2-03 **C05**


VERSION 1T — TRIANGLE, ROOF TO THE WALL

TALL HOUSE WALL (exist., AC units)

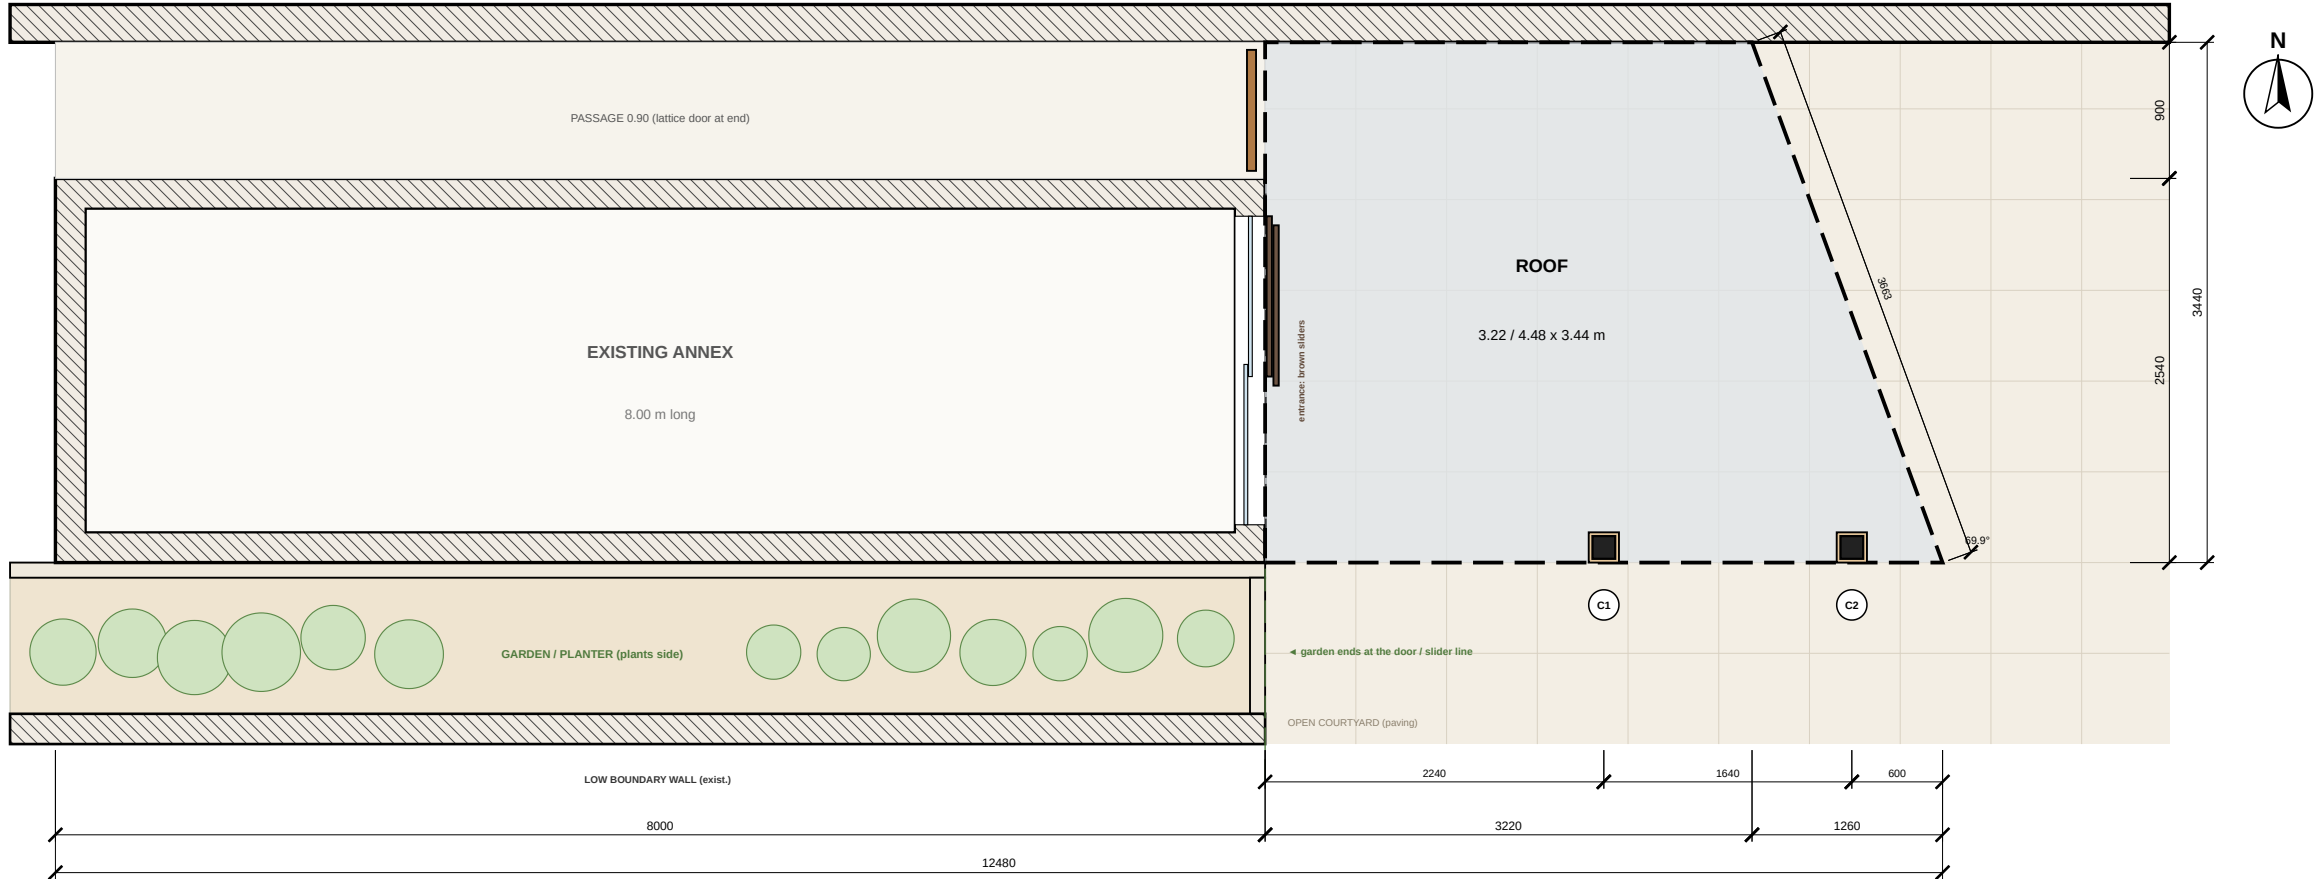

1 TOP VIEW — ANNEX, GARDEN & ROOF
V1T-01
1:50 @ A3 — garden ends at the door line; trees = background

2/V1T-01 ROOF FRAMING PLAN — 1:30

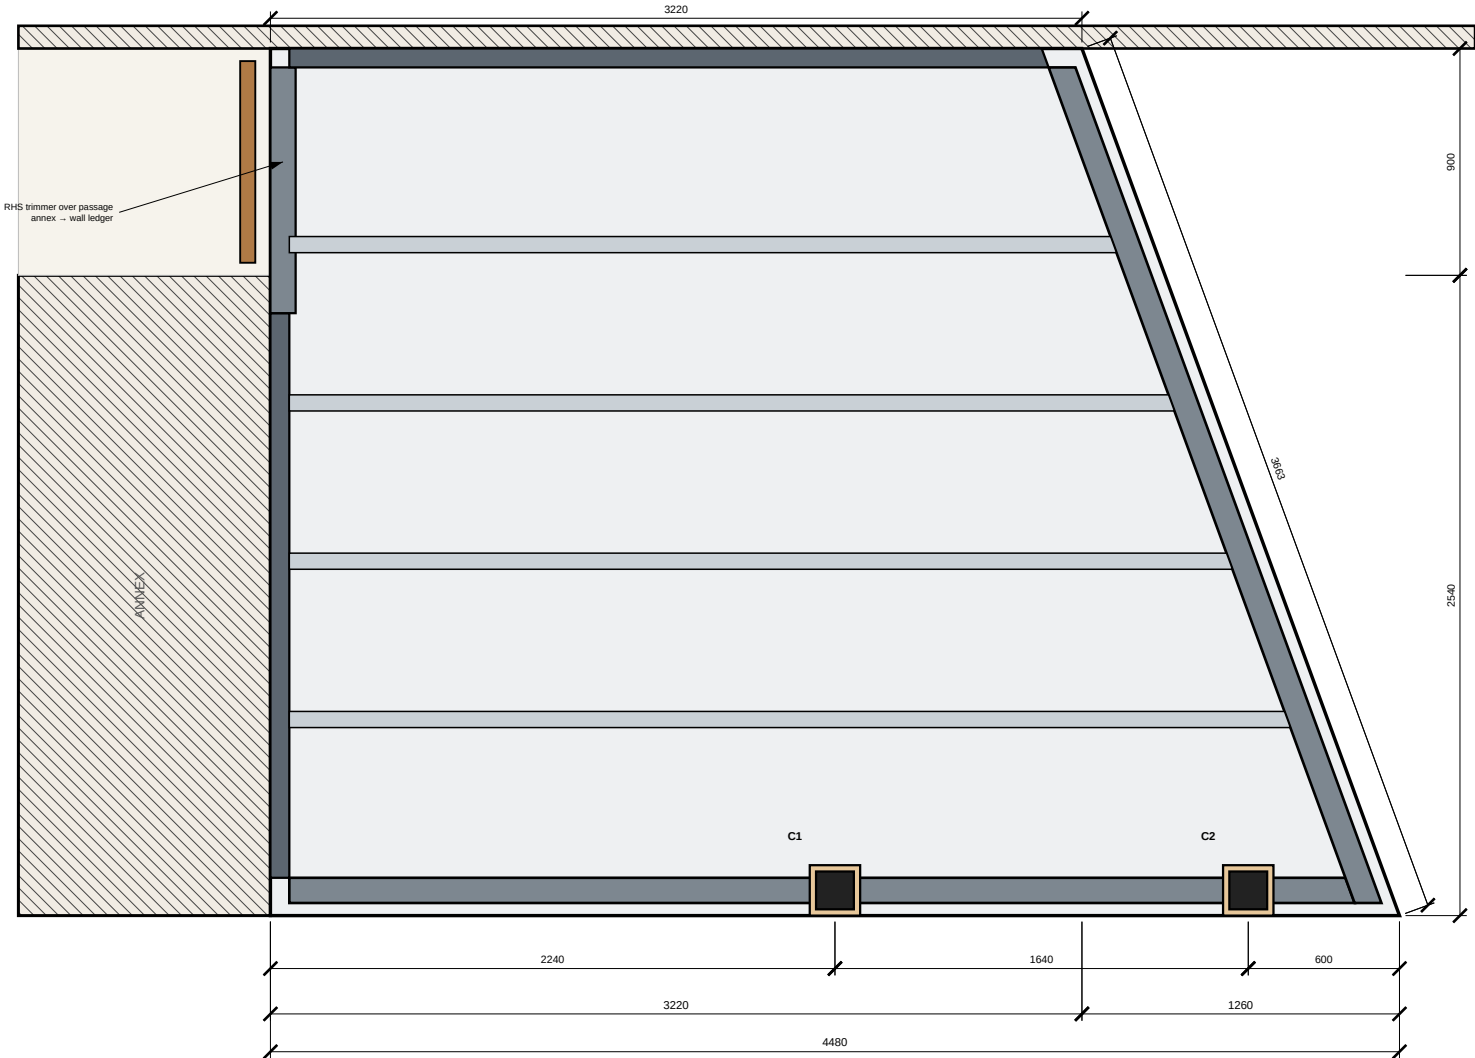

THIS VERSION
triangular roof: plants edge 3.22 + 1.26 = 4.48, wall edge 3.22, raked edge 3.66; runs to the tall wall (ledger + brackets); 2 columns on the plants side.
Roof fixed to the annex end façade AND to the tall house wall (steel ledgers, resin anchors); covers the passage in front of the lattice door (RHS trimmer over the passage, annex → wall ledger).
Triangle: plants edge 3.22 + 1.26 = 4.48 m; raked edge 3.66 m at 69.9° to the plants edge.
C1 in the middle of the 4.48 edge (2.24 from the façade); C2 0.60 m in from the tip (the tip cantilevers 0.60).
Joists run from the annex ledger to the raked edge beam (max. span = 4.2 m).
COMMON
Roof 3.22 m from the annex façade along the top edge. Underside +2.36, fascia 0.43 (top +2.79); columns 200x200, 0.13 above roof, curved bracket under the junction (client section).
Garden & low wall stop at the annex end façade (door / slider line); beyond it open paving.
Falls 1:70 to the concealed gutter at the free edge; rainwater down C2.



COURTYARD ROOF — V1T

VERSION 1T — TRIANGLE, ROOF TO THE WALL: triangular roof: plants edge 3.22 + 1.26 = 4.48, wall edge 3.22, raked edge 3.66; runs to the tall wall (ledger + brackets); 2 columns on the plants side
Client: Owner / Client
Design & drawings: Claude Code

- DRAWING NOTES**
- Do not scale from this drawing. Use figured dimensions only.
 - All dimensions in millimetres; levels in metres relative to internal FFL ±0.000 (datum to be tied to site survey).
 - Contractor to verify all dimensions, levels & existing structure on site before fabrication or ordering.
 - Read with all other architectural, structural & services drawings and the specification notes (A-001).
 - Structural members are preliminary: final design, connections & calculations by a licensed structural engineer to local code before construction.
 - Report any discrepancy to the designer before proceeding.

REVISIONS		
Rev	Date	Description
C05	07.10.2026	Garden ends at door/slider line; triangular versions V1T/V2T; 3D views
C04	07.10.2026	Two versions V1/V2 per client sections & site photo
C02	07.10.2026	Canopy to client sketch: 8.00 house, roof 3.22, u/s 2.36, fascia 0.43


PREVIEW FOR CLIENT REVIEW — per client sketch, mark-ups & site photo; not for construction

DRAWING TITLE	
V1T TRIANGLE TO WALL top view & roof framing	
SCALE @ A3 1:50 / 1:30	DATE 07.10.2026
DRAWN / CHECKED CC / —	SERIES ARCHITECTURAL
DRAWING No.	REV


V1T-01 C05

VERSION 1T — TRIANGLE, ROOF TO THE WALL

1/V1T-02 VIEW TO ANNEX FAÇADE (as site photo) — 1:50

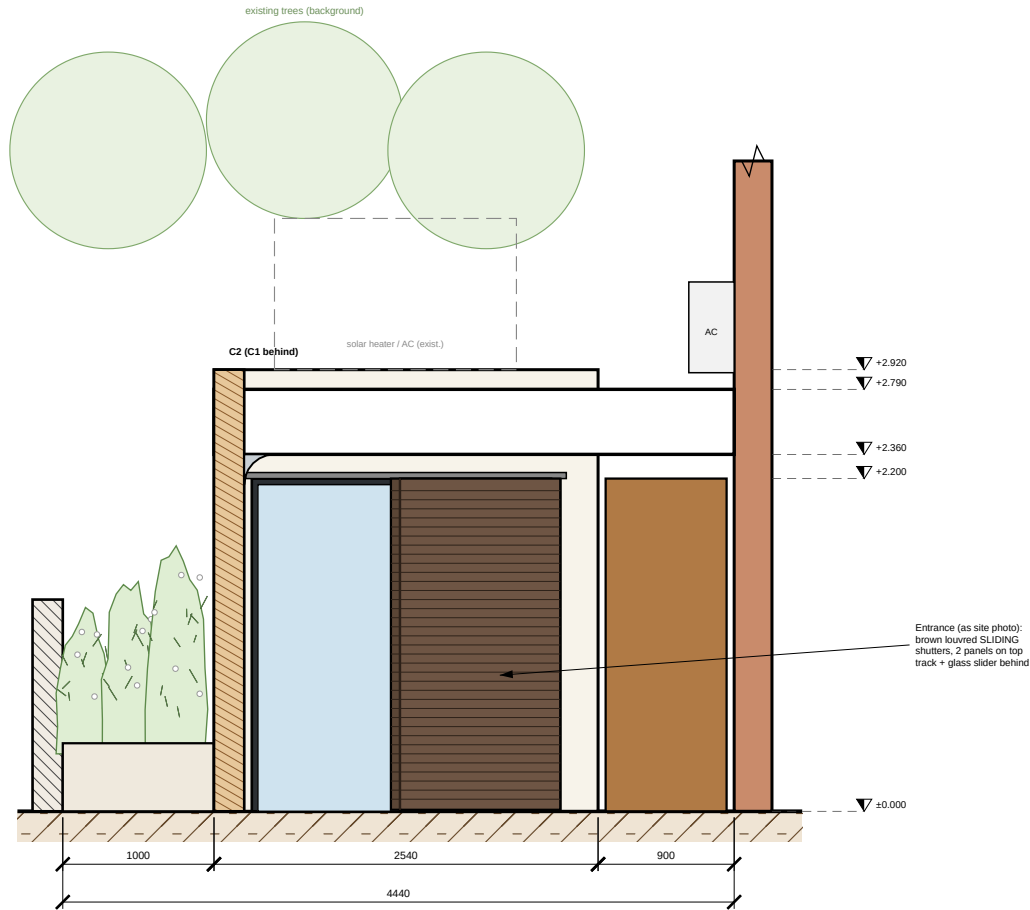


2/V1T-02 PLANTS-SIDE ELEVATION — C1 + C2 — 1:50 (plants edge 3.22 + 1.26 = 4.48)

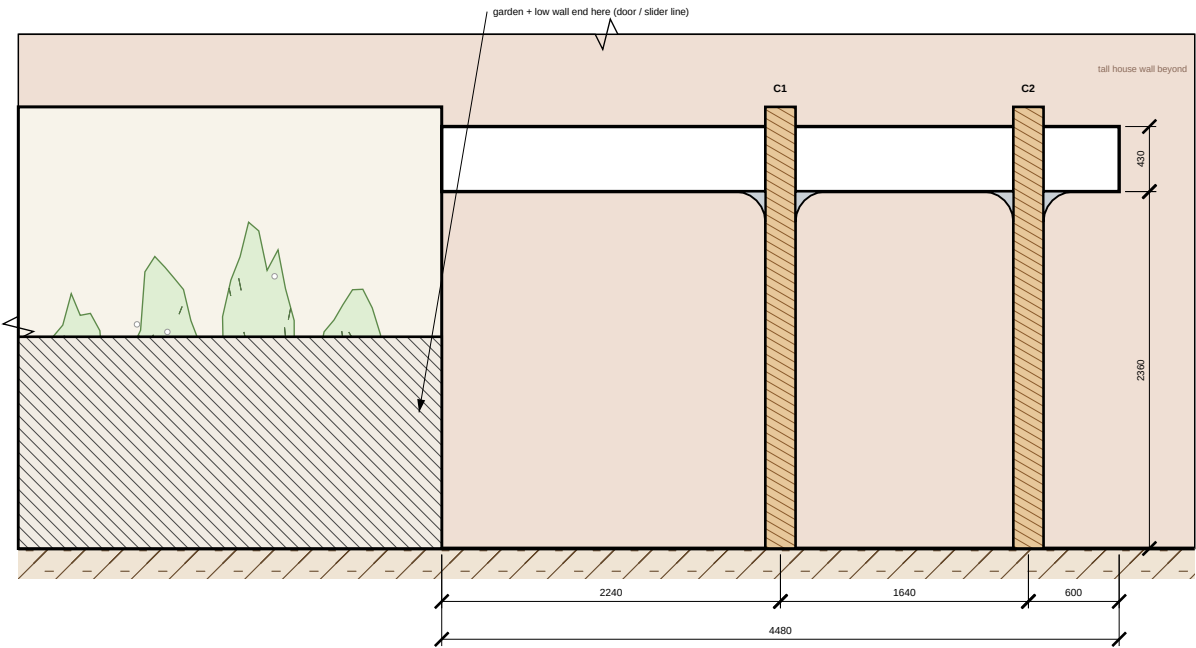


NOTES
triangular roof: plants edge 3.22 + 1.26 = 4.48, wall edge 3.22, raked edge 3.66; runs to the tall wall (ledger + brackets); 2 columns on the plants side.
Underside +2.36, fascia 0.43 (top +2.79); columns 0.13 above roof.
Garden + low wall end at the annex end façade (door / slider line). Trees are existing, in the background.
Refined roof section & details: sheet V1T-03.

3/V1T-02 SECTION ACROSS AT C1 — 1:50 (refined: V1T-03)

tall wall left — plants side right

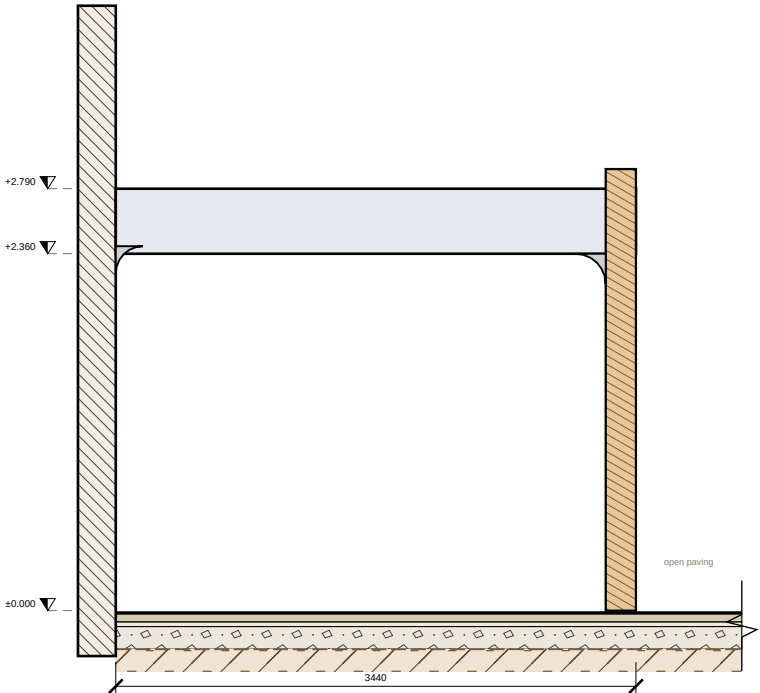

4/V1T-02 3D VIEW — from the plants side (courtyard)

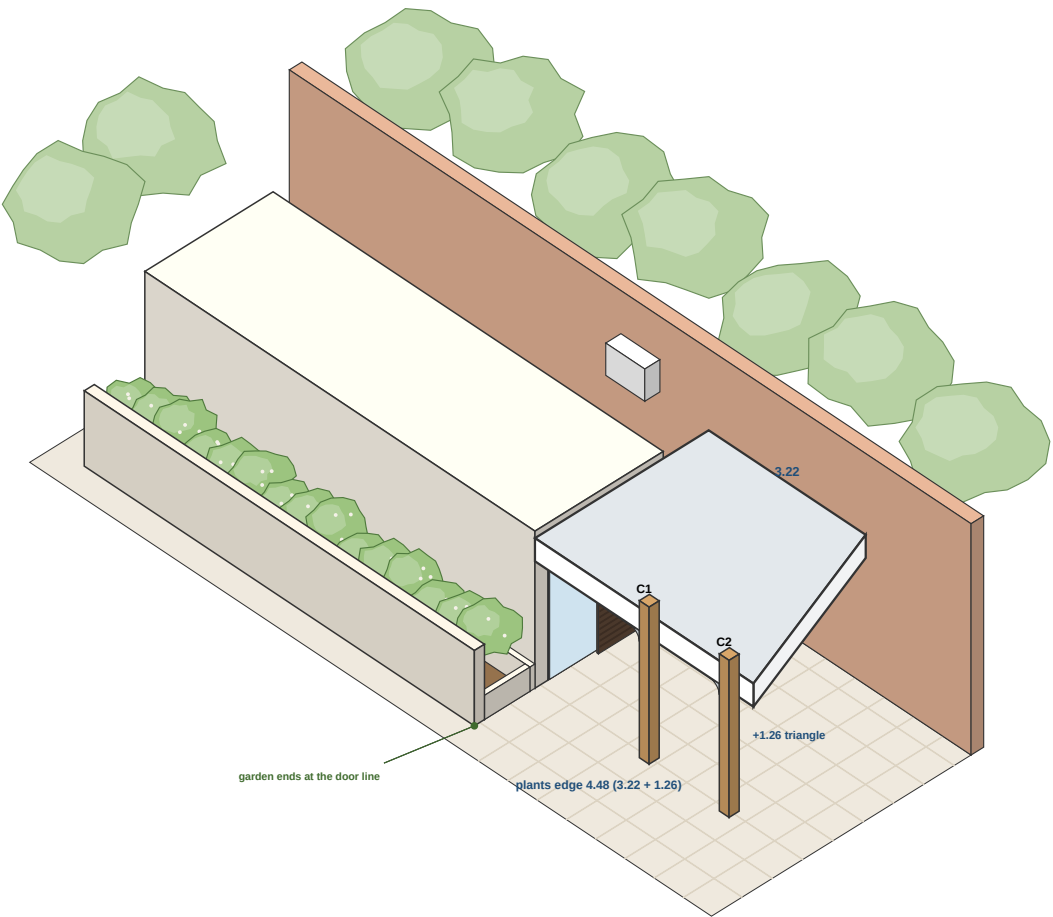

COURTYARD ROOF — V1T

VERSION 1T — TRIANGLE, ROOF TO THE WALL: triangular roof: plants edge 3.22 + 1.26 = 4.48, wall edge 3.22, raked edge 3.66; runs to the tall wall (ledger + brackets); 2 columns on the plants side
Client: Owner / Client
Design & drawings: Claude Code

DRAWING NOTES

- Do not scale from this drawing. Use figured dimensions only.
- All dimensions in millimetres; levels in metres relative to internal FFL ±0.000 (datum to be tied to site survey).
- Contractor to verify all dimensions, levels & existing structure on site before fabrication or ordering.
- Read with all other architectural, structural & services drawings and the specification notes (A-001).
- Structural members are preliminary: final design, connections & calculations by a licensed structural engineer to local code before construction.
- Report any discrepancy to the designer before proceeding.

REVISIONS

Rev	Date	Description
C05	07.10.2026	Garden ends at door/slider line; triangular versions V1T/V2T; 3D views
C04	07.10.2026	Two versions V1/V2 per client sections & site photo
C02	07.10.2026	Canopy to client sketch: 8.00 house, roof 3.22, u/s 2.36, fascia 0.43

PREVIEW FOR CLIENT REVIEW — per client sketch, mark-ups & site photo; not for construction

DRAWING TITLE

V1T TRIANGLE TO WALL
views, section & 3D view

SCALE @ A3 1:50	DATE 07.10.2026
DRAWN / CHECKED CC / —	SERIES ARCHITECTURAL

DRAWING No. REV


V1T-02

C05

VERSION 1T — TRIANGLE, ROOF TO THE WALL

1/V1T-03 ROOF SECTION ACROSS AT C1 — 1:25

(as client sketch A: roof runs to the wall)

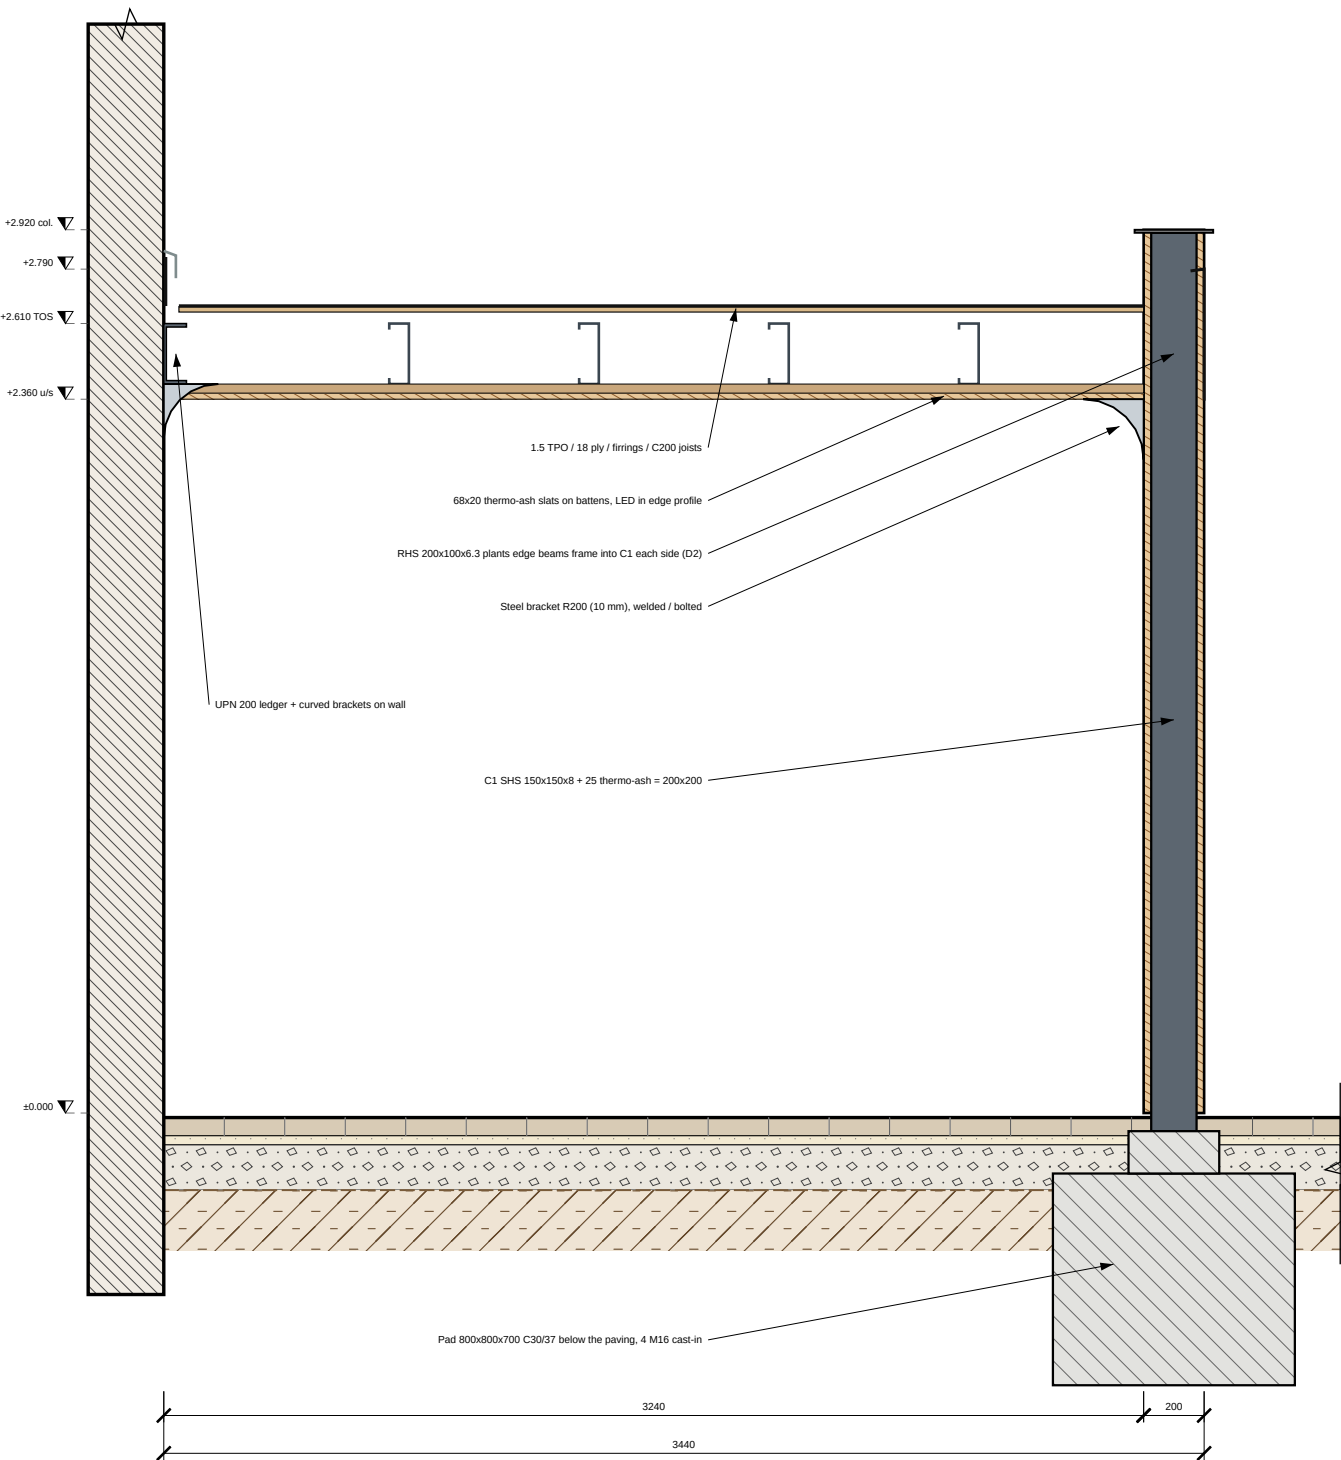


SPECIFICATION
Steel S355, hot-dip galvanised; columns & brackets powder-coated RAL 9010 or timber-clad (thermo-ash).
Roof: TPO 1.5 on 18 mm marine ply on tapered firrings (fall 1:70 to the free-edge box gutter).
Soffit: thermo-ash 68x20 slats, LED 2700 K in perimeter profile. Fascia 3 mm aluminium RAL 9010, 0.43 m.
Wall ledger & brackets into sound masonry/RC — engineer to confirm anchors.


SCALE BAR 1:25 (section 1)




D1 ROOF TO WALL (client sketch A) — 1:15

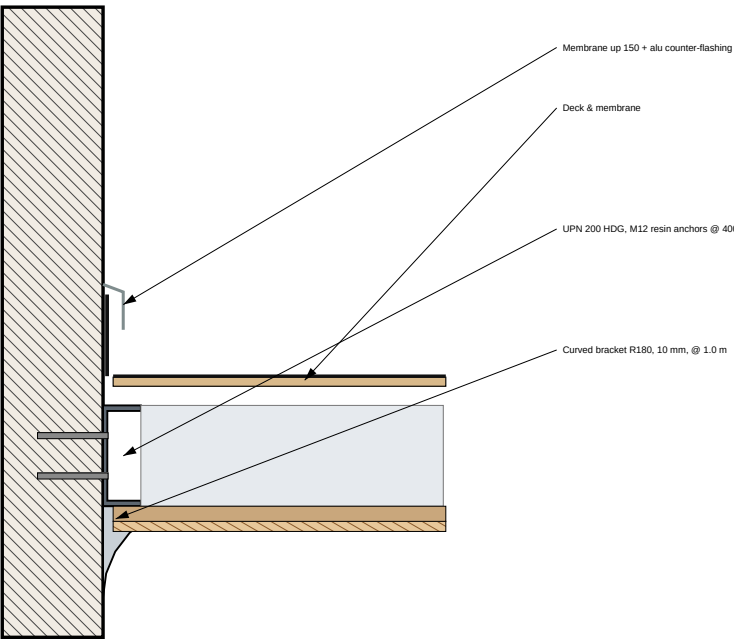

D2 COLUMN / ROOF JUNCTION (plants side) — 1:15

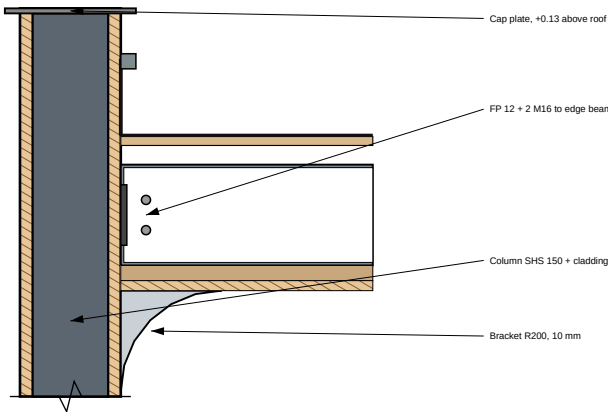

D3 TIP AT C2 (triangle) — PLAN 1:15

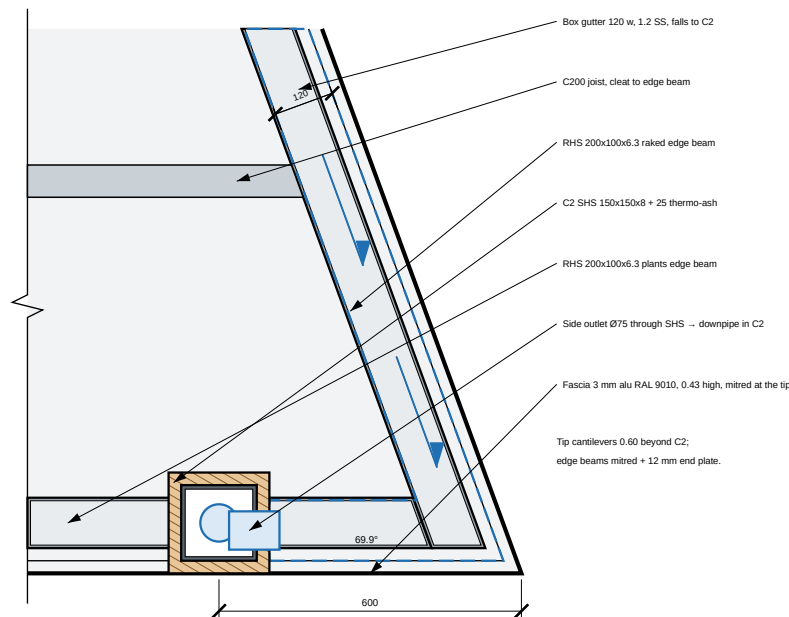

COURTYARD ROOF — V1T

VERSION 1T — TRIANGLE, ROOF TO THE WALL: triangular roof; plants edge 3.22 + 1.26 = 4.48, wall edge 3.22, raked edge 3.66; runs to the tall wall (ledger + brackets); 2 columns on the plants side
Client: Owner / Client
Design & drawings: Claude Code

DRAWING NOTES

- Do not scale from this drawing. Use figured dimensions only.
- All dimensions in millimetres; levels in metres relative to internal FFL ±0.000 (datum to be tied to site survey).
- Contractor to verify all dimensions, levels & existing structure on site before fabrication or ordering.
- Read with all other architectural, structural & services drawings and the specification notes (A-001).
- Structural members are preliminary: final design, connections & calculations by a licensed structural engineer to local code before construction.
- Report any discrepancy to the designer before proceeding.

REVISIONS

Rev	Date	Description
C05	07.10.2026	Garden ends at door/slider line; triangular versions V1T/V2T; 3D views
C04	07.10.2026	Two versions V1/V2 per client sections & site photo
C02	07.10.2026	Canopy to client sketch: 8.00 house, roof 3.22, u/s 2.36, fascia 0.43

PREVIEW FOR CLIENT REVIEW — per client sketch, mark-ups & site photo; not for construction

DRAWING TITLE

V1T TRIANGLE TO WALL
roof section & details

SCALE @ A3

1:25 / 1:15 / 1:20

DRAWN / CHECKED

CC / —

DATE

07.10.2026

SERIES

ARCHITECTURAL

DRAWING No.


V1T-03

REV

C05


VERSION 2T — TRIANGLE, 0.90 m VOID + 2 RODS

TALL HOUSE WALL (exist., AC units)

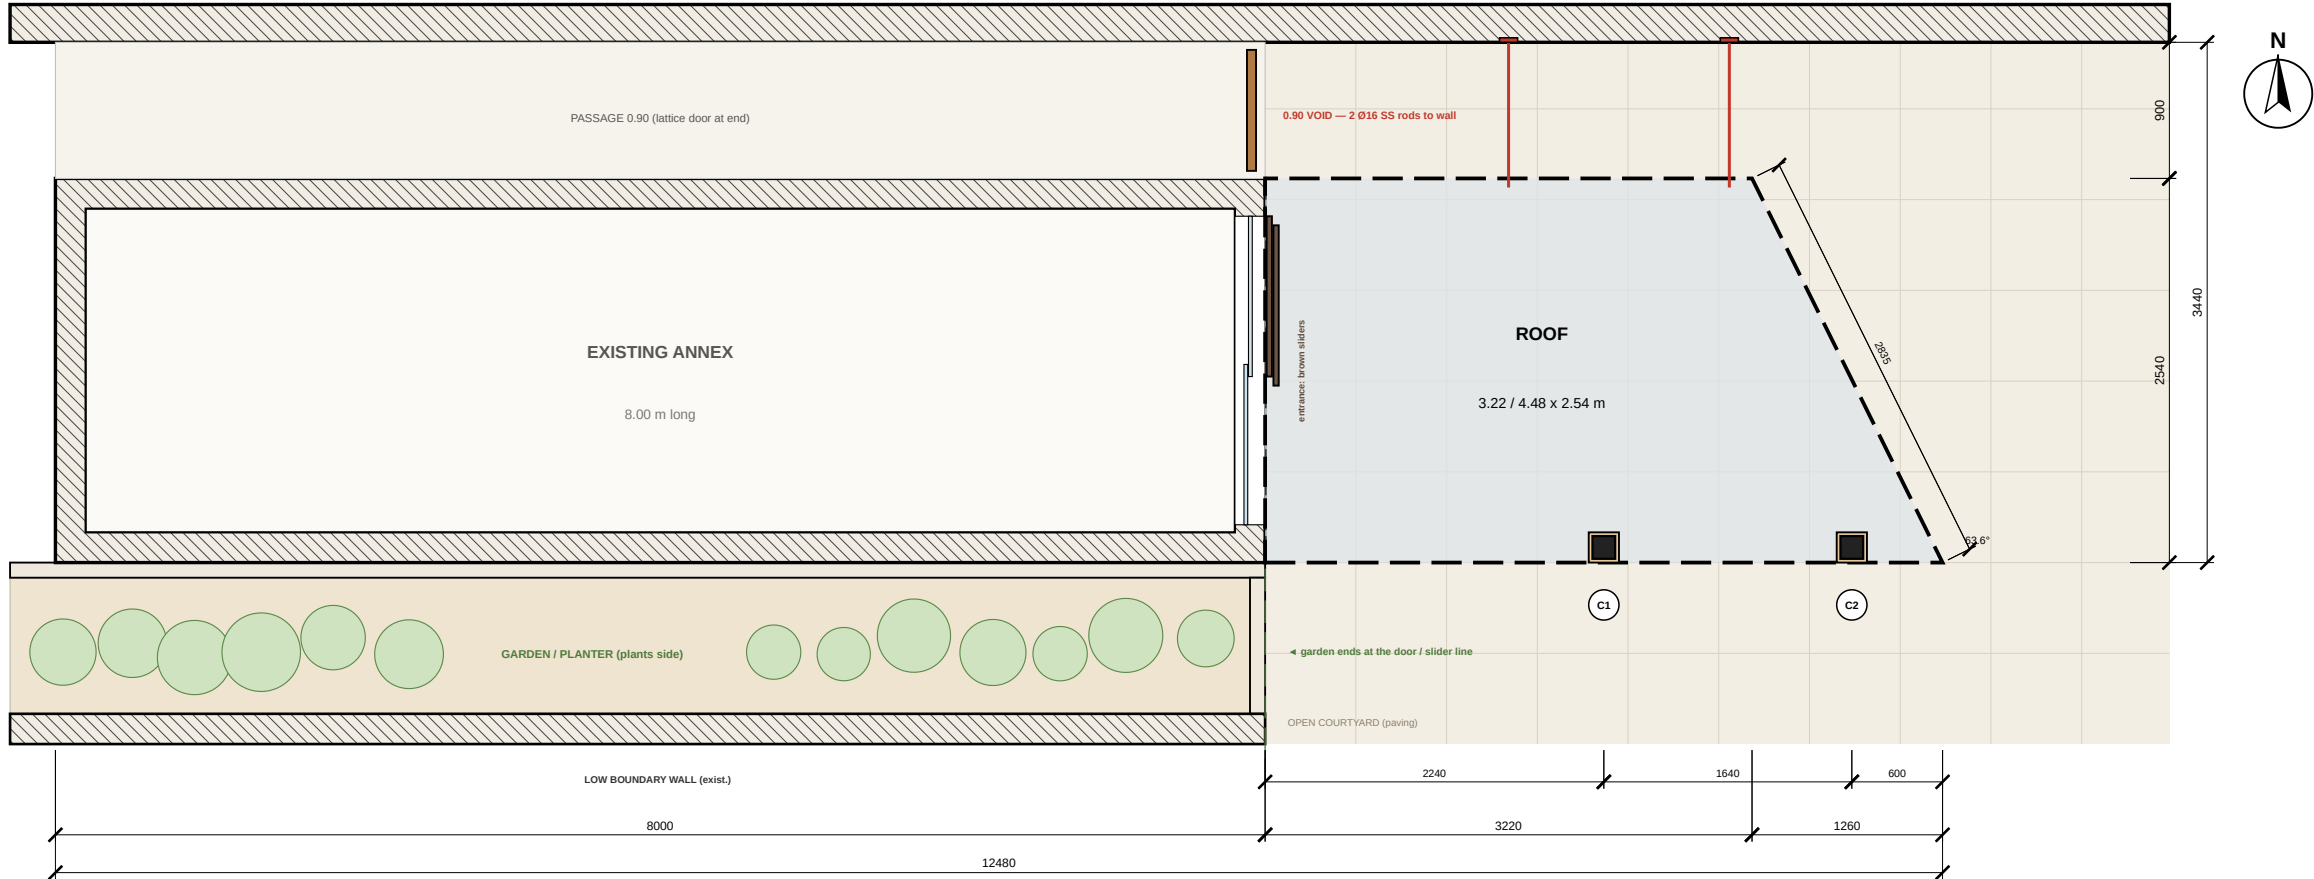

1 TOP VIEW — ANNEX, GARDEN & ROOF
V2T-01
1:50 @ A3 — garden ends at the door line; trees = background

2/V2T-01 ROOF FRAMING PLAN — 1:30

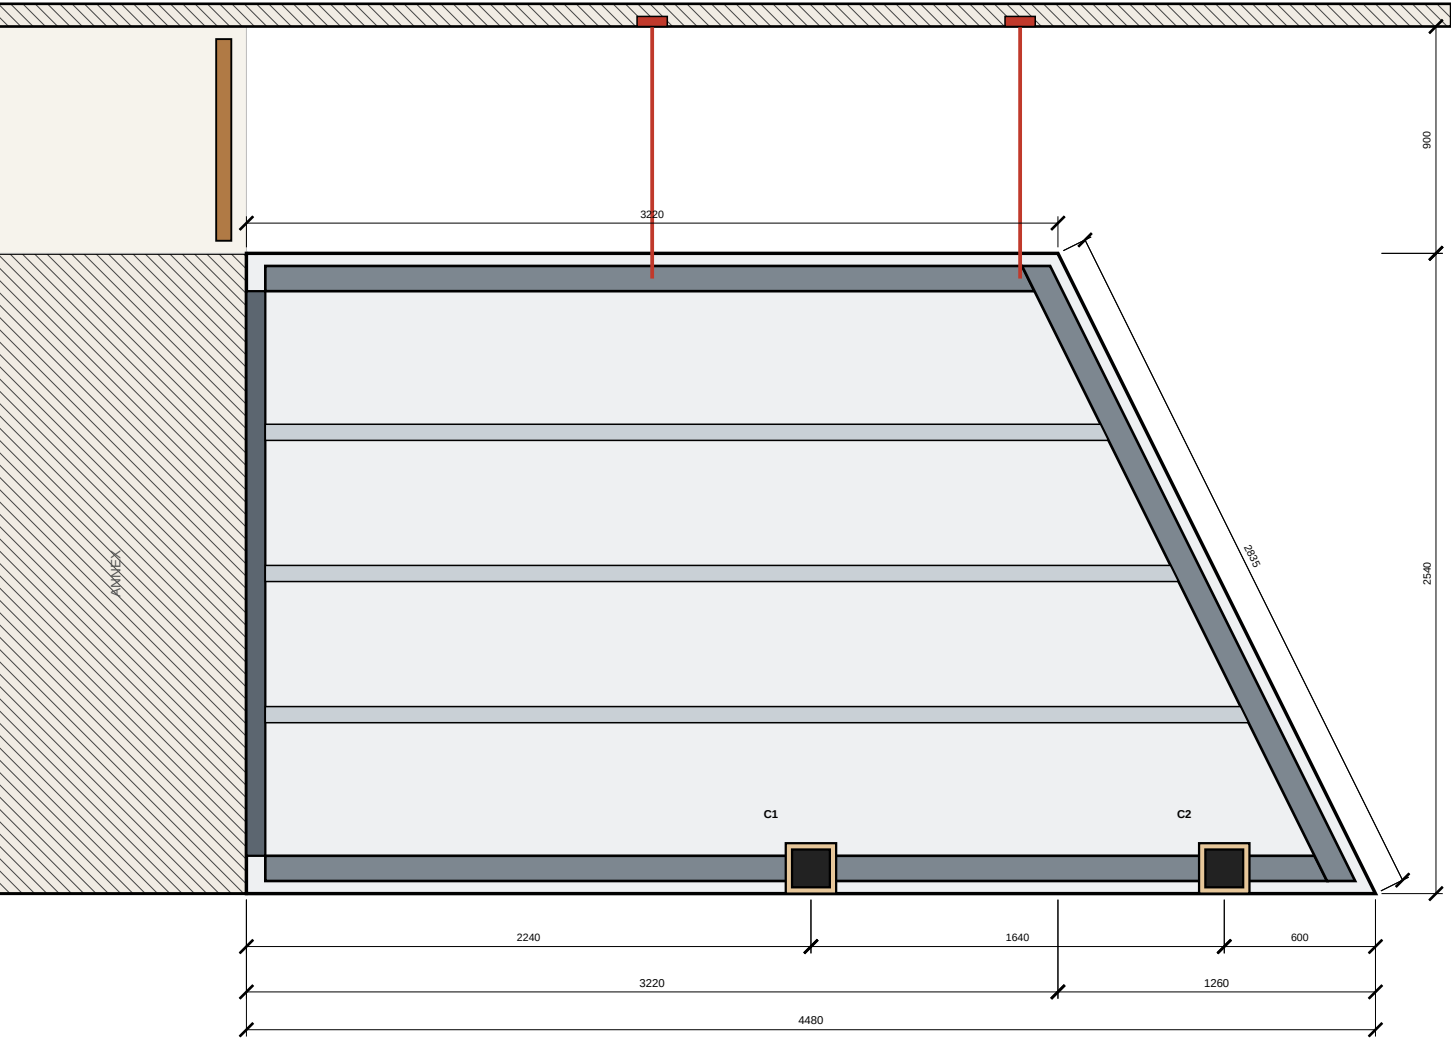

THIS VERSION
triangular roof: plants edge 3.22 + 1.26 = 4.48, void edge 3.22, raked edge 2.84; 0.90 m void open, 2 Ø16 stainless rods to the wall; 2 columns on the plants side.
Roof fixed to the annex end façade (ledger). The 0.90 m passage to the lattice door stays open.
Void edge hung from the tall house wall on 2 Ø16 stainless rods (turnbuckles, wall plates) — slim, almost invisible.
Triangle: plants edge 3.22 + 1.26 = 4.48 m; raked edge 2.84 m at 63.6° to the plants edge.
C1 in the middle of the 4.48 edge (2.24 from the façade); C2 0.60 m in from the tip (the tip cantilevers 0.60).
Joists run from the annex ledger to the raked edge beam (max. span = 4.2 m).
COMMON
Roof 3.22 m from the annex façade along the top edge. Underside +2.36, fascia 0.43 (top +2.79); columns 200x200, 0.13 above roof, curved bracket under the junction (client section).
Garden & low wall stop at the annex end façade (door / slider line); beyond it open paving.
Falls 1:70 to the concealed gutter at the free edge; rainwater down C2.



COURTYARD ROOF — V2T

VERSION 2T — TRIANGLE, 0.90 m VOID + 2 RODS: triangular roof: plants edge 3.22 + 1.26 = 4.48, void edge 3.22, raked edge 2.84; 0.90 m void open, 2 Ø16 stainless rods to the wall; 2 columns on the plants side
Client: Owner / Client
Design & drawings: Claude Code

- DRAWING NOTES**
- Do not scale from this drawing. Use figured dimensions only.
 - All dimensions in millimetres; levels in metres relative to internal FFL ±0.000 (datum to be tied to site survey).
 - Contractor to verify all dimensions, levels & existing structure on site before fabrication or ordering.
 - Read with all other architectural, structural & services drawings and the specification notes (A-001).
 - Structural members are preliminary: final design, connections & calculations by a licensed structural engineer to local code before construction.
 - Report any discrepancy to the designer before proceeding.

REVISIONS		
Rev	Date	Description
C05	07.10.2026	Garden ends at door/slider line; triangular versions V1T/V2T; 3D views
C04	07.10.2026	Two versions V1/V2 per client sections & site photo
C02	07.10.2026	Canopy to client sketch: 8.00 house, roof 3.22, u/s 2.36, fascia 0.43

PREVIEW FOR CLIENT REVIEW — per client sketch, mark-ups & site photo; not for construction


DRAWING TITLE
V2T TRIANGLE + RODS
top view & roof framing

SCALE @ A3 1:50 / 1:30	DATE 07.10.2026
DRAWN / CHECKED CC / —	SERIES ARCHITECTURAL


DRAWING No. **V2T-01** REV **C05**

VERSION 2T — TRIANGLE, 0.90 m VOID + 2 RODS

1/V2T-02 VIEW TO ANNEX FAÇADE (as site photo) — 1:50

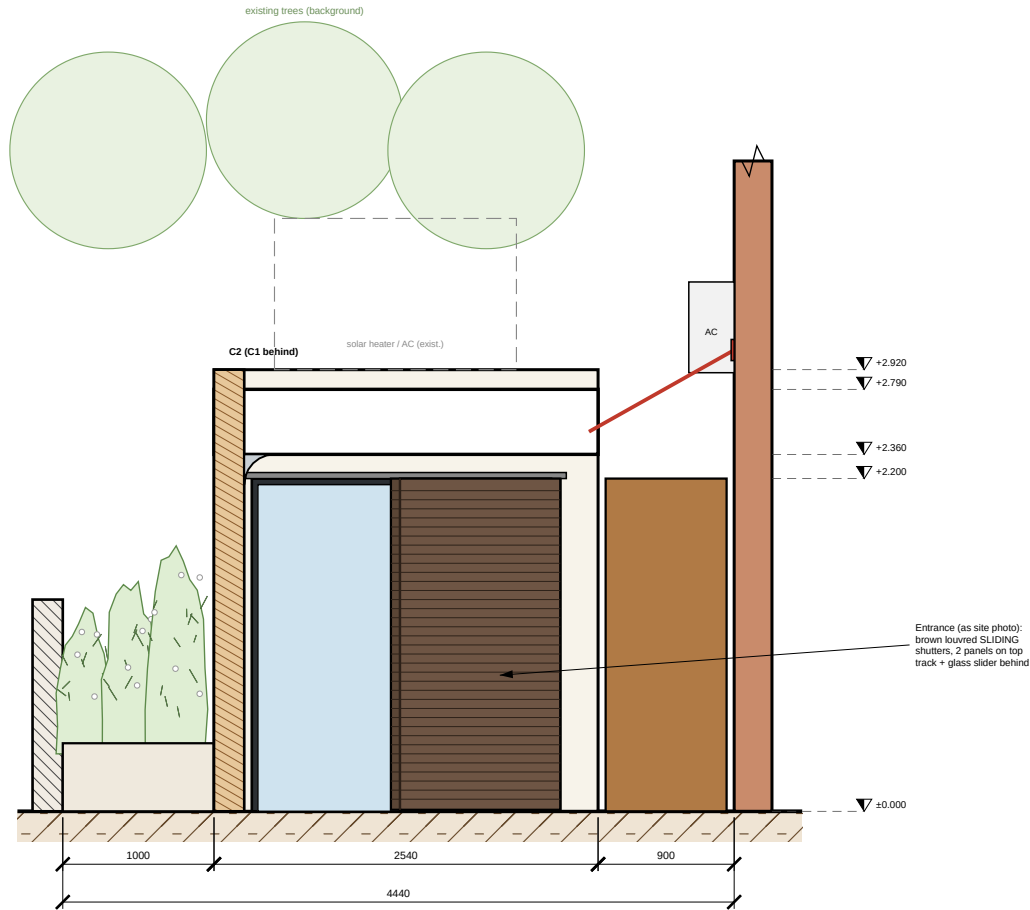


2/V2T-02 PLANTS-SIDE ELEVATION — C1 + C2 — 1:50 (plants edge 3.22 + 1.26 = 4.48)

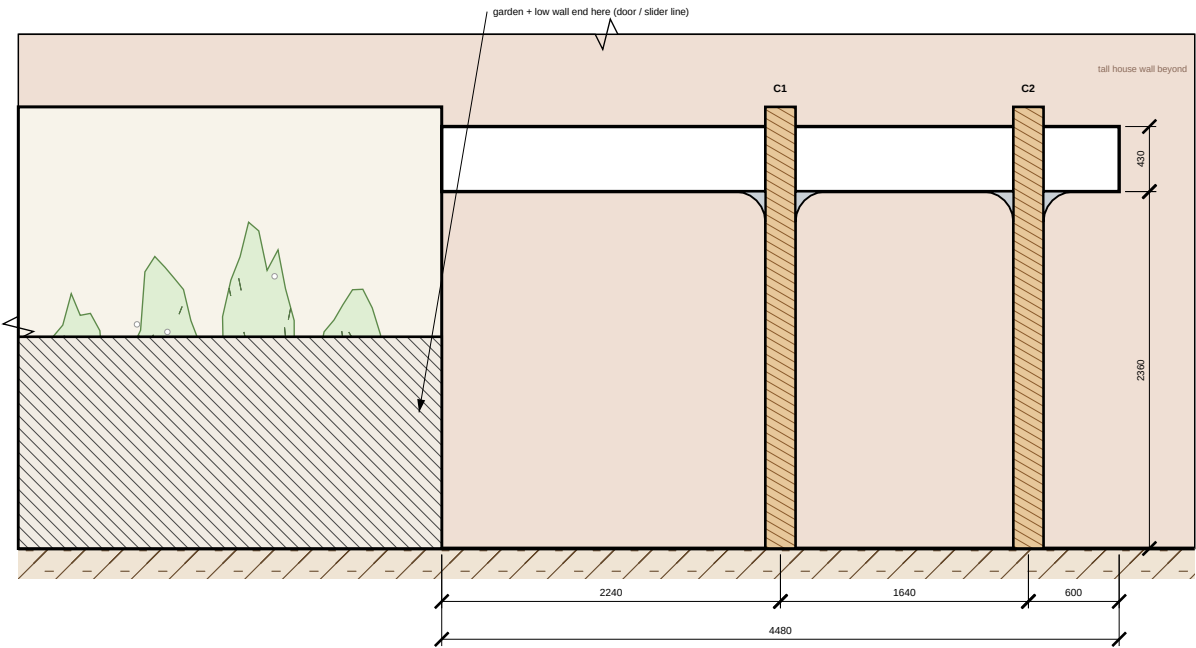


NOTES
triangular roof: plants edge 3.22 + 1.26 = 4.48, void edge 3.22, raked edge 2.84; 0.90 m void open, 2 Ø16 stainless rods to the wall; 2 columns on the plants side.
Underside +2.36, fascia 0.43 (top +2.79); columns 0.13 above roof.
Garden + low wall end at the annex end façade (door / slider line). Trees are existing, in the background.
Refined roof section & details: sheet V2T-03.

3/V2T-02 SECTION ACROSS AT C1 — 1:50 (refined: V2T-03)

tall wall left — plants side right

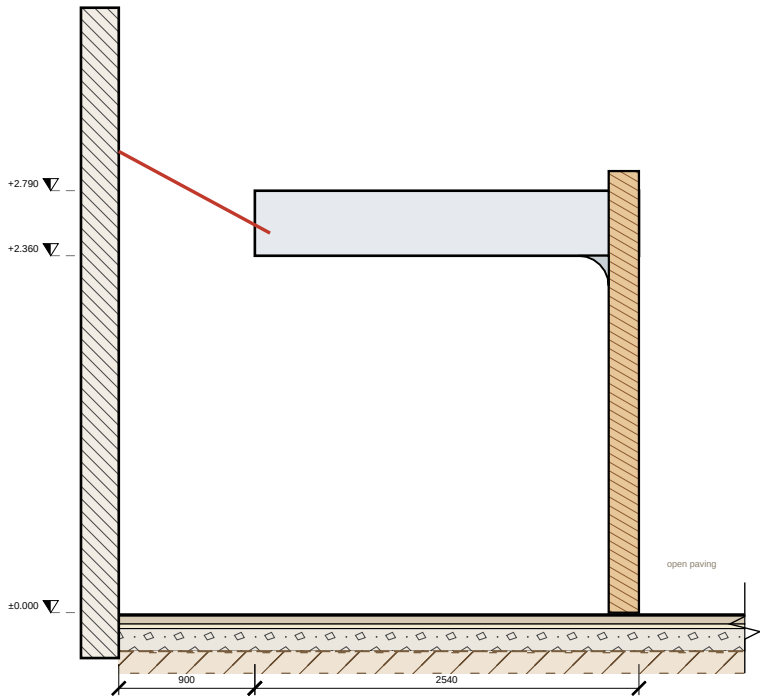

4/V2T-02 3D VIEW — from the plants side (courtyard)

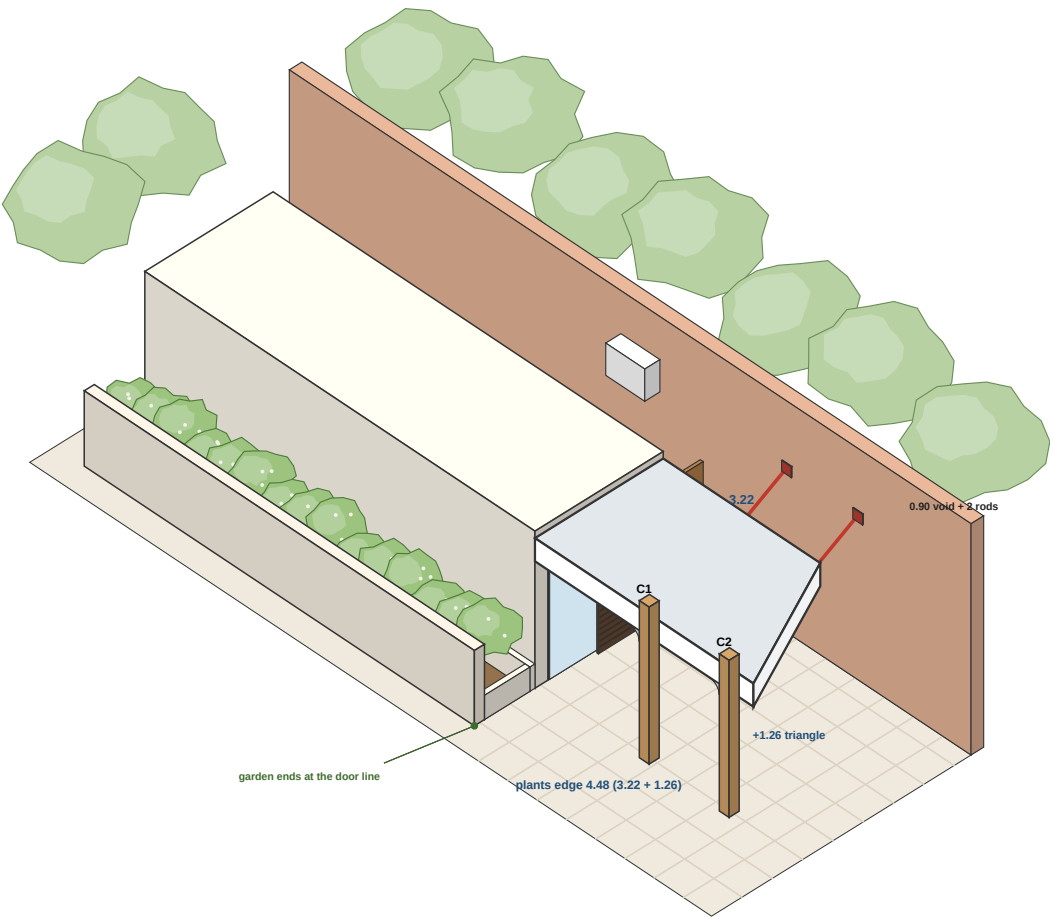

COURTYARD ROOF — V2T

VERSION 2T — TRIANGLE, 0.90 m VOID + 2 RODS: triangular roof: plants edge 3.22 + 1.26 = 4.48, void edge 3.22, raked edge 2.84; 0.90 m void open, 2 Ø16 stainless rods to the wall; 2 columns on the plants side
Client: Owner / Client
Design & drawings: Claude Code

DRAWING NOTES

- Do not scale from this drawing. Use figured dimensions only.
- All dimensions in millimetres; levels in metres relative to internal FFL ±0.000 (datum to be tied to site survey).
- Contractor to verify all dimensions, levels & existing structure on site before fabrication or ordering.
- Read with all other architectural, structural & services drawings and the specification notes (A-001).
- Structural members are preliminary: final design, connections & calculations by a licensed structural engineer to local code before construction.
- Report any discrepancy to the designer before proceeding.

REVISIONS

Rev	Date	Description
C05	07.10.2026	Garden ends at door/slider line; triangular versions V1T/V2T; 3D views
C04	07.10.2026	Two versions V1/V2 per client sections & site photo
C02	07.10.2026	Canopy to client sketch: 8.00 house, roof 3.22, u/s 2.36, fascia 0.43

PREVIEW FOR CLIENT REVIEW — per client sketch, mark-ups & site photo; not for construction

DRAWING TITLE

V2T TRIANGLE + RODS
views, section & 3D view

SCALE @ A3

1:50

DRAWN / CHECKED

CC / —

DATE

07.10.2026

SERIES

ARCHITECTURAL

DRAWING No.

V2T-02


REV

C05

VERSION 2T — TRIANGLE, 0.90 m VOID + 2 RODS

1/V2T-03 ROOF SECTION ACROSS AT C1 — 1:25

(as client sketch B: roof stops, rods to the wall)

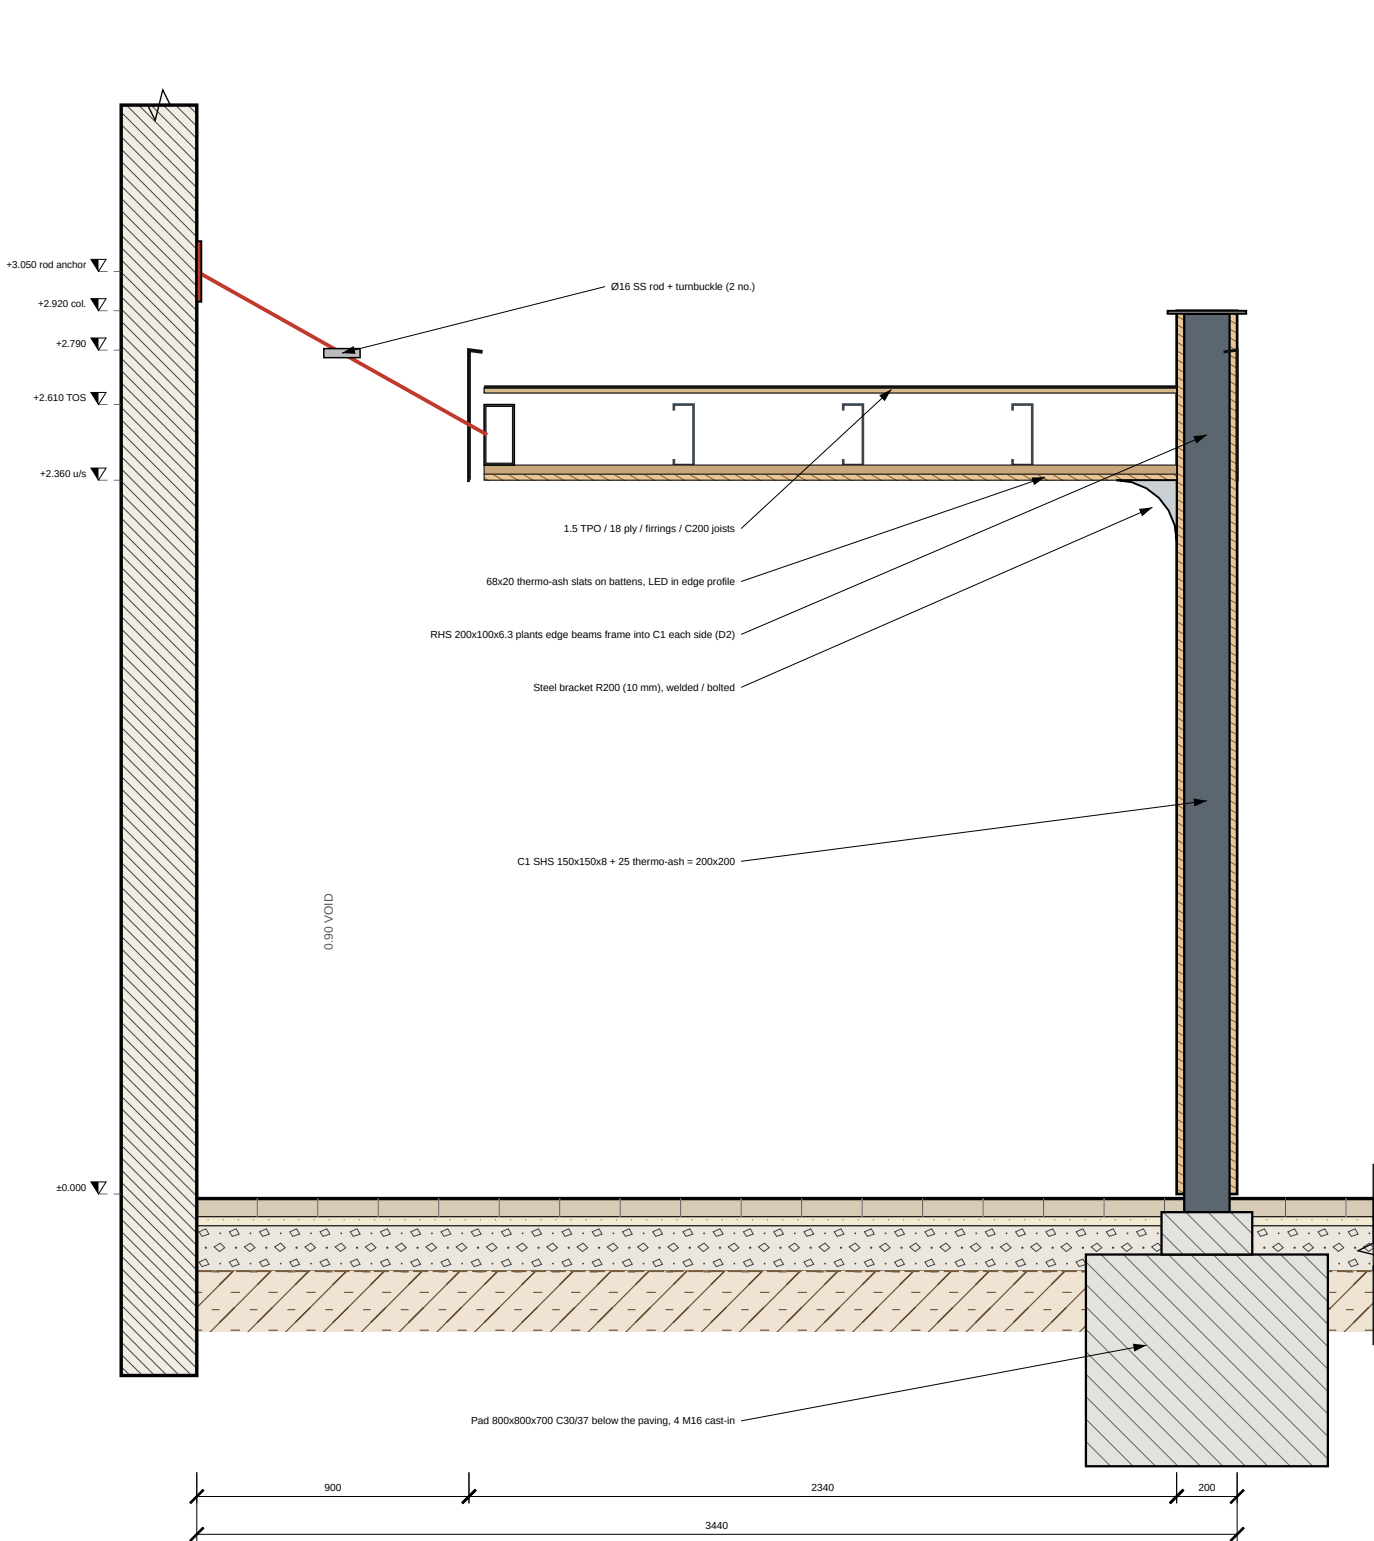


SPECIFICATION
Steel S355, hot-dip galvanised; columns & brackets powder-coated RAL 9010 or timber-clad (thermo-ash).
Roof: TPO 1.5 on 18 mm marine ply on tapered firrings (fall 1:70 to the free-edge box gutter).
Soffit: thermo-ash 68x20 slats, LED 2700 K in perimeter profile. Fascia 3 mm aluminium RAL 9010, 0.43 m.
Rods: Ø16 stainless 316, fork ends, turnbuckle, = 30° rise; engineer to confirm wall anchors.


SCALE BAR 1:25 (section 1)




D1 ROD TO WALL (client sketch B) — 1:20

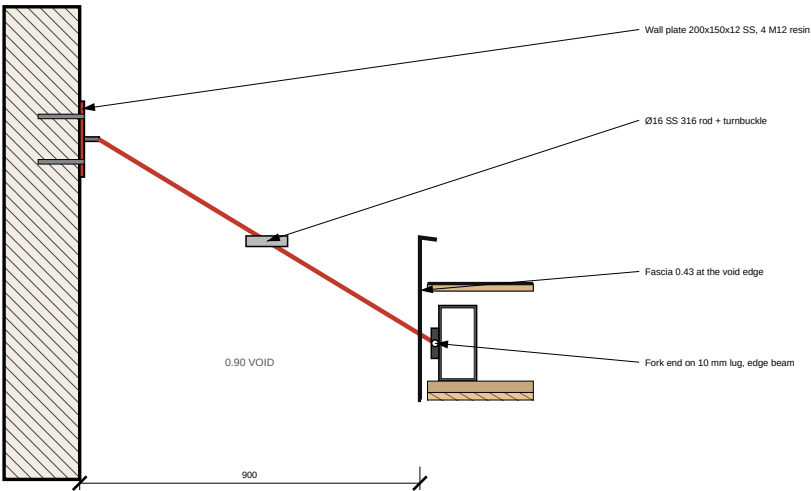

D2 COLUMN / ROOF JUNCTION (plants side) — 1:15

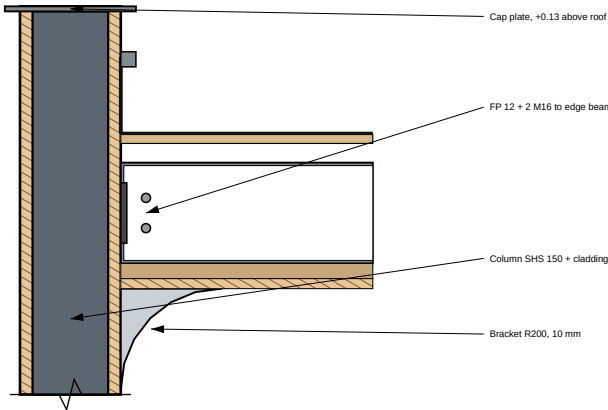

D3 TIP AT C2 (triangle) — PLAN 1:15

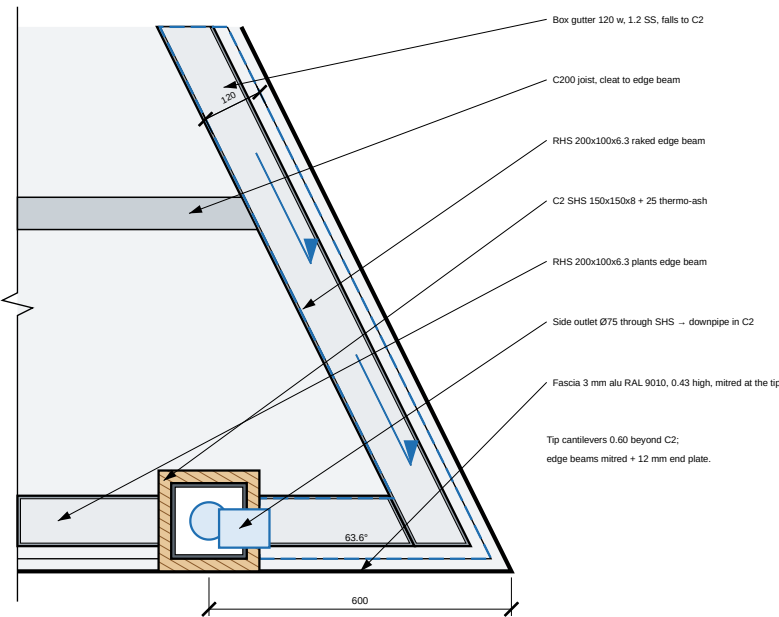

COURTYARD ROOF — V2T

VERSION 2T — TRIANGLE, 0.90 m VOID + 2 RODS: triangular roof: plants edge 3.22 + 1.26 = 4.48, void edge 3.22, raked edge 2.84; 0.90 m void open, 2 Ø16 stainless rods to the wall; 2 columns on the plants side
Client: Owner / Client
Design & drawings: Claude Code

DRAWING NOTES

- Do not scale from this drawing. Use figured dimensions only.
- All dimensions in millimetres; levels in metres relative to internal FFL ±0.000 (datum to be tied to site survey).
- Contractor to verify all dimensions, levels & existing structure on site before fabrication or ordering.
- Read with all other architectural, structural & services drawings and the specification notes (A-001).
- Structural members are preliminary: final design, connections & calculations by a licensed structural engineer to local code before construction.
- Report any discrepancy to the designer before proceeding.

REVISIONS

Rev	Date	Description
C05	07.10.2026	Garden ends at door/slider line; triangular versions V1T/V2T; 3D views
C04	07.10.2026	Two versions V1/V2 per client sections & site photo
C02	07.10.2026	Canopy to client sketch: 8.00 house, roof 3.22, u/s 2.36, fascia 0.43

PREVIEW FOR CLIENT REVIEW — per client sketch, mark-ups & site photo; not for construction

DRAWING TITLE

V2T TRIANGLE + RODS
roof section & details

SCALE @ A3

1:25 / 1:15 / 1:20

DRAWN / CHECKED

CC / —

DATE

07.10.2026

SERIES

ARCHITECTURAL

DRAWING No.

V2T-03

REV

C05