



VERSION 1 — ROOF TO THE WALL

TALL HOUSE WALL (exist., AC units)

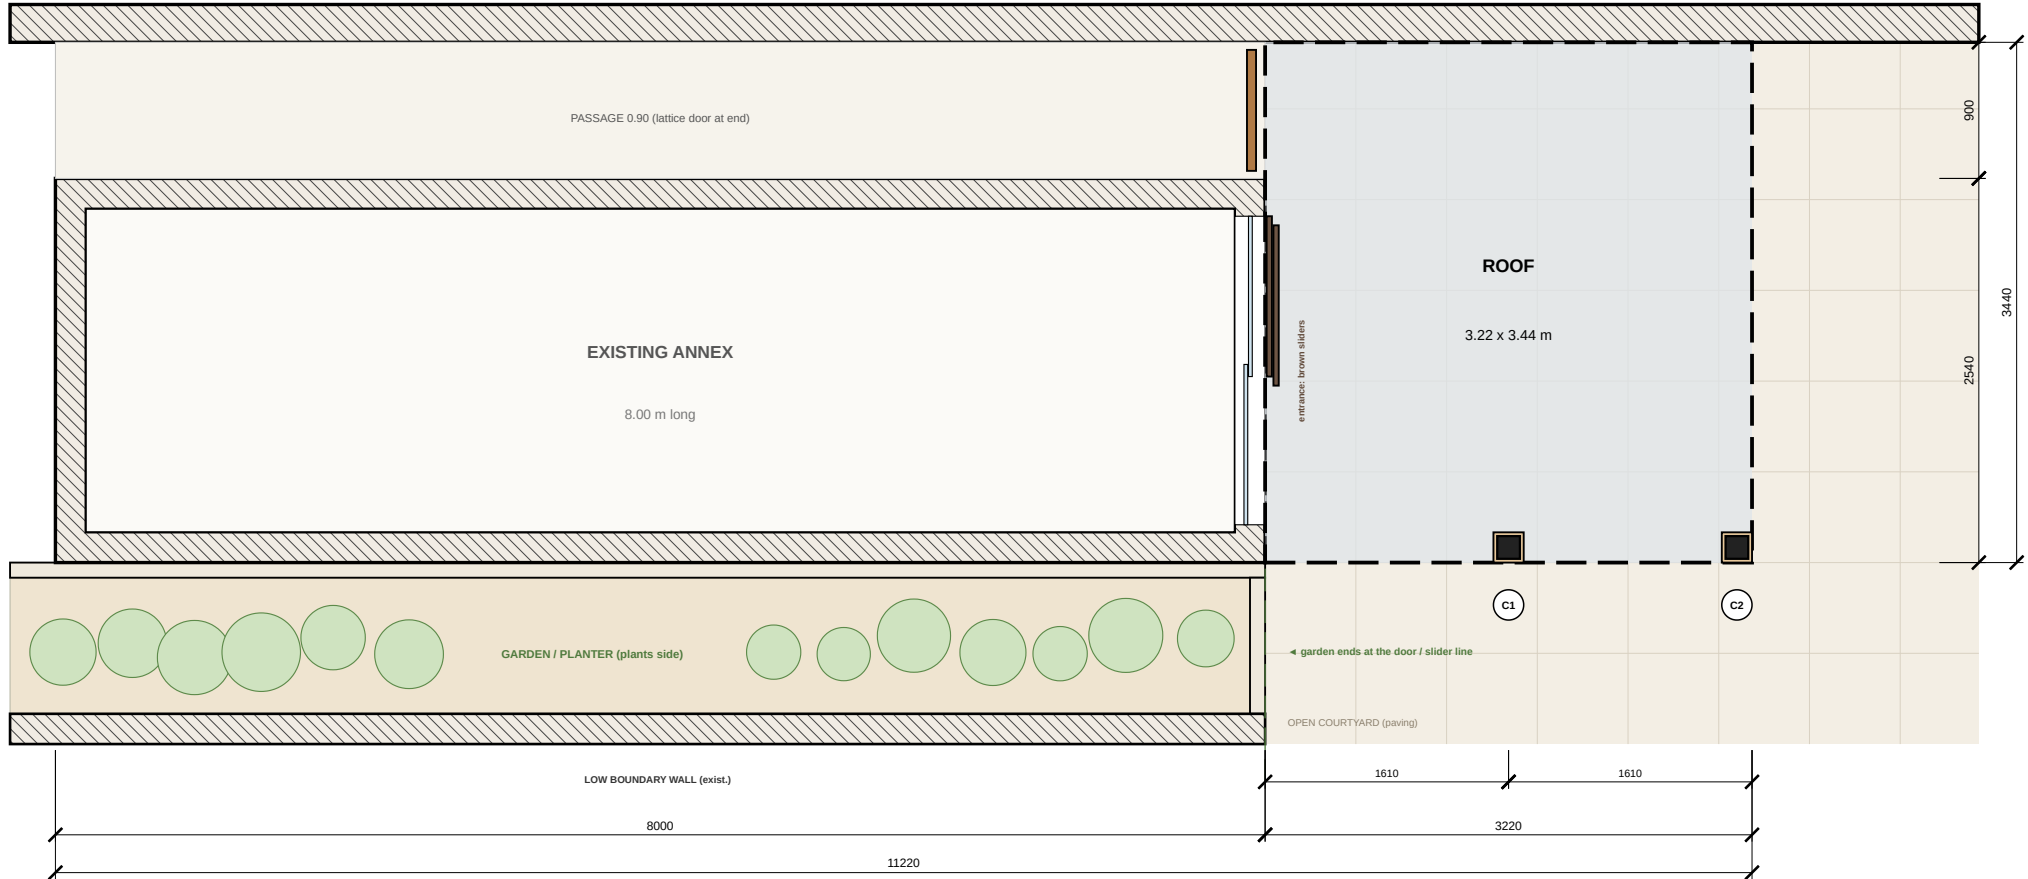

1 TOP VIEW — ANNEX, GARDEN & ROOF
V1-01 1:50 @ A3 — garden ends at the door line; trees = background

2/V1-01 ROOF FRAMING PLAN — 1:30

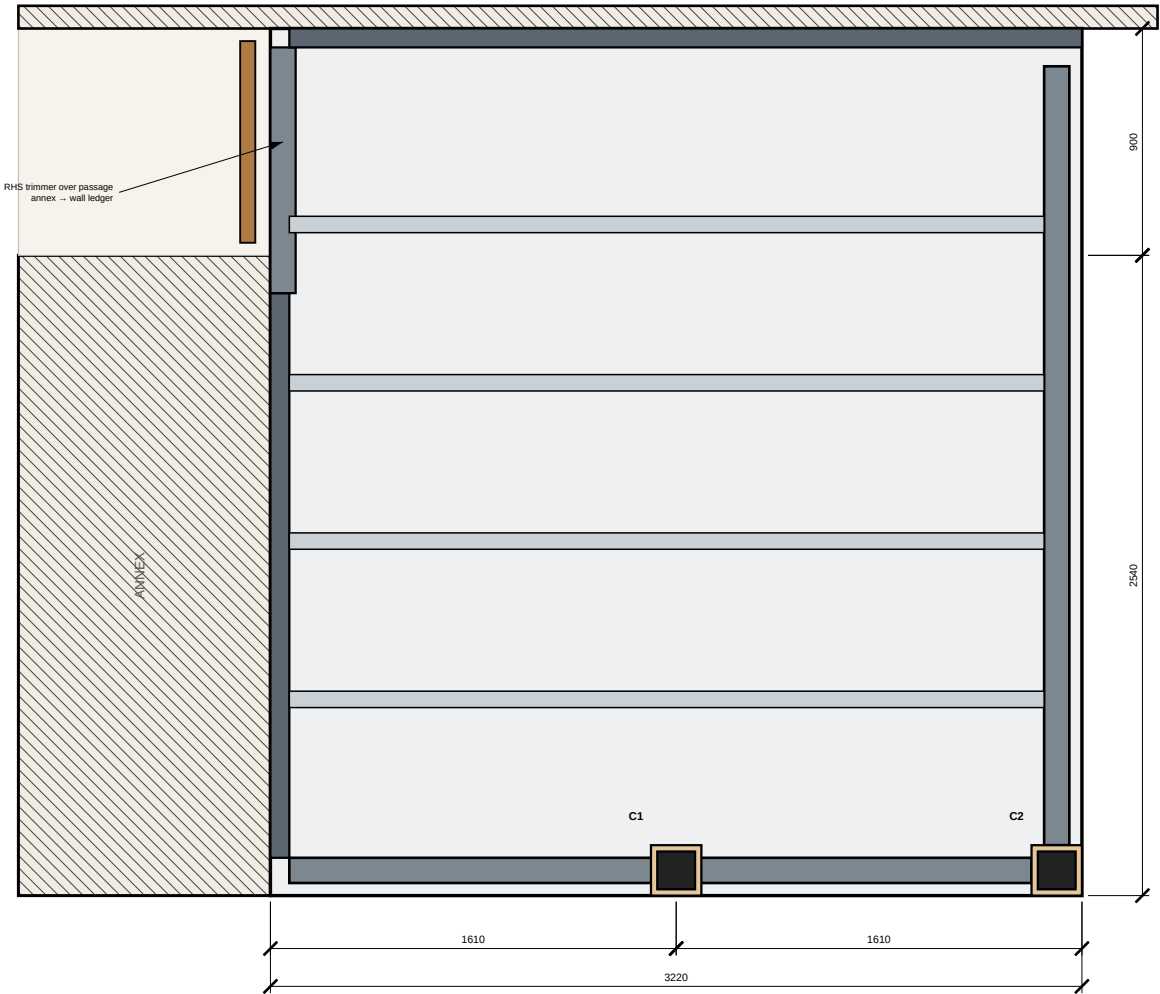

THIS VERSION
roof 3.22 x 3.44 up to the tall wall (bears on wall ledger + curved brackets); 2 columns on the plants side.
Roof fixed to the annex end façade AND to the tall house wall (steel ledgers, resin anchors); covers the passage in front of the lattice door (RHS trimmer over the passage, annex → wall ledger).
C1 in the middle of the plants edge, C2 at the corner.
COMMON
Roof 3.22 m from the annex façade along the top edge. Underside +2.36, fascia 0.43 (top +2.79); columns 200x200, 0.13 above roof, curved bracket under the junction (client section).
Garden & low wall stop at the annex end façade (door / slider line); beyond it open paving.
Falls 1:70 to the concealed gutter at the free edge; rainwater down C2.



COURTYARD ROOF — V1

VERSION 1 — ROOF TO THE WALL: roof 3.22 x 3.44 up to the tall wall (bears on wall ledger + curved brackets); 2 columns on the plants side
Client: Owner / Client
Design & drawings: Claude Code

- DRAWING NOTES**
- Do not scale from this drawing. Use figured dimensions only.
 - All dimensions in millimetres; levels in metres relative to internal FFL ±0.000 (datum to be tied to site survey).
 - Contractor to verify all dimensions, levels & existing structure on site before fabrication or ordering.
 - Read with all other architectural, structural & services drawings and the specification notes (A-001).
 - Structural members are preliminary: final design, connections & calculations by a licensed structural engineer to local code before construction.
 - Report any discrepancy to the designer before proceeding.

REVISIONS		
Rev	Date	Description
C05	07.10.2026	Garden ends at door/slider line; triangular versions V1/V2; 3D views
C04	07.10.2026	Two versions V1/V2 per client sections & site photo
C02	07.10.2026	Canopy to client sketch: 8.00 house, roof 3.22, u/s 2.36, fascia 0.43


PREVIEW FOR CLIENT REVIEW — per client sketch, mark-ups & site photo; not for construction

DRAWING TITLE	
V1 ROOF TO WALL top view & roof framing	
SCALE @ A3 1:50 / 1:30	DATE 07.10.2026
DRAWN / CHECKED CC / —	SERIES ARCHITECTURAL
DRAWING No.	REV


V1-01 C05

VERSION 1 — ROOF TO THE WALL

1/V1-02 VIEW TO ANNEX FAÇADE (as site photo) — 1:50

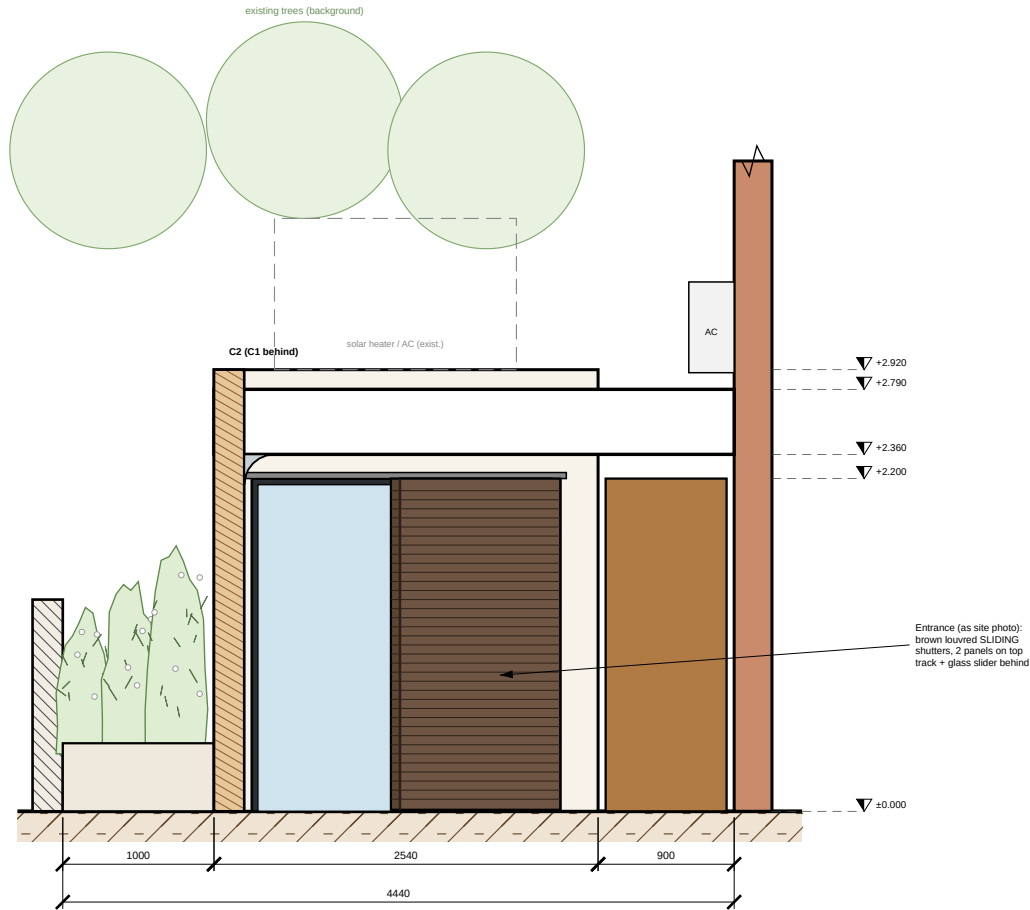


2/V1-02 PLANTS-SIDE ELEVATION — C1 + C2 — 1:50

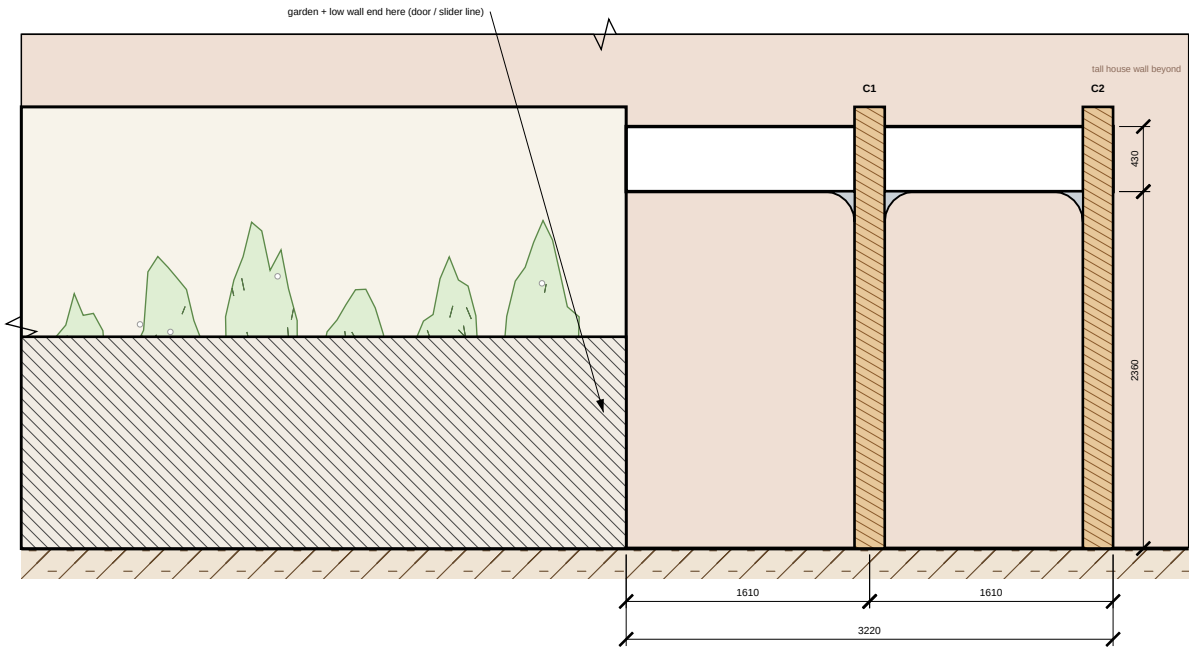


NOTES
roof 3.22 x 3.44 up to the tall wall (bears on wall ledger + curved brackets); 2 columns on the plants side.
Underside +2.36, fascia 0.43 (top +2.79); columns 0.13 above roof.
Garden + low wall end at the annex end façade (door / slider line). Trees are existing, in the background.
Refined roof section & details: sheet V1-03.

3/V1-02 SECTION ACROSS AT C1 — 1:50 (refined: V1-03)

tall wall left — plants side right

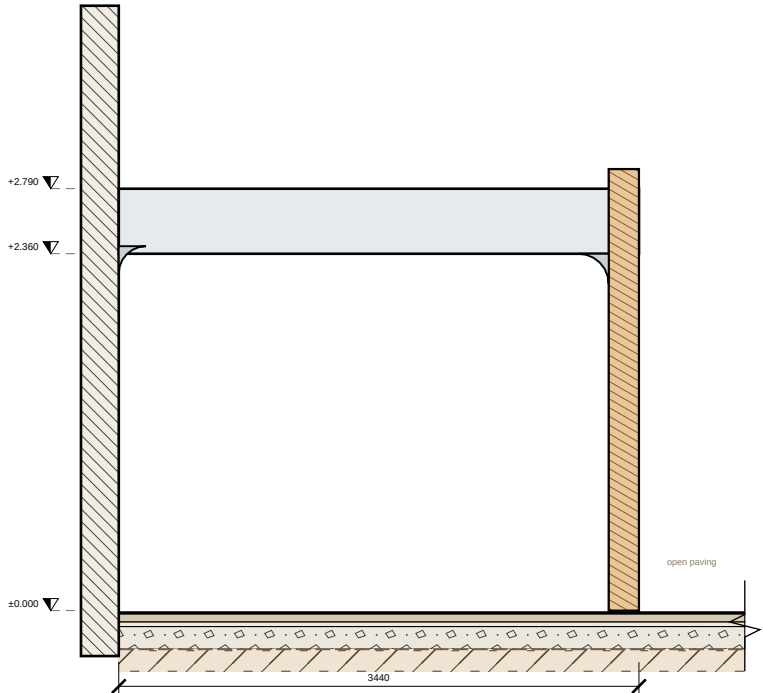

4/V1-02 3D VIEW — from the plants side (courtyard)

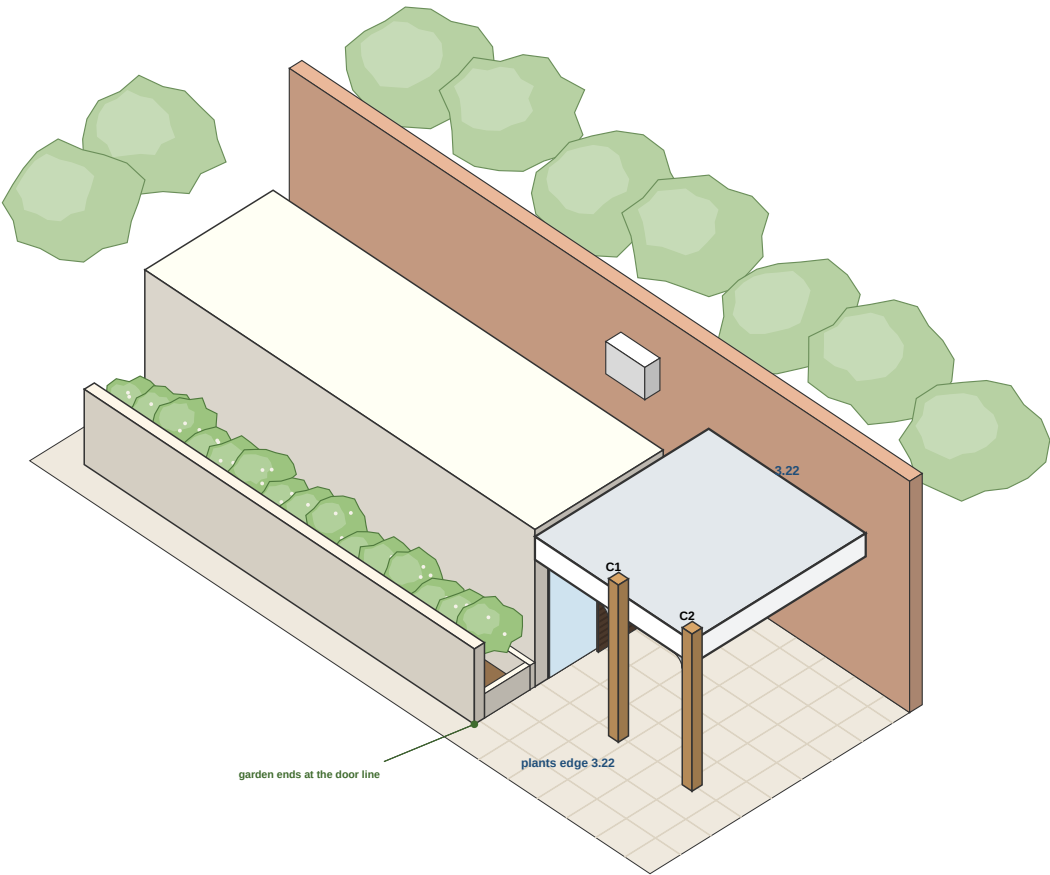

COURTYARD ROOF — V1

VERSION 1 — ROOF TO THE WALL: roof 3.22 x 3.44 up to the tall wall (bears on wall ledger + curved brackets); 2 columns on the plants side
Client: Owner / Client
Design & drawings: Claude Code

- DRAWING NOTES**
- Do not scale from this drawing. Use figured dimensions only.
 - All dimensions in millimetres; levels in metres relative to internal FFL ±0.000 (datum to be tied to site survey).
 - Contractor to verify all dimensions, levels & existing structure on site before fabrication or ordering.
 - Read with all other architectural, structural & services drawings and the specification notes (A-001).
 - Structural members are preliminary: final design, connections & calculations by a licensed structural engineer to local code before construction.
 - Report any discrepancy to the designer before proceeding.

REVISIONS		
Rev	Date	Description
C05	07.10.2026	Garden ends at door/slider line; triangular versions V1/V2; 3D views
C04	07.10.2026	Two versions V1/V2 per client sections & site photo
C02	07.10.2026	Canopy to client sketch: 8.00 house, roof 3.22, u/s 2.36, fascia 0.43

PREVIEW FOR CLIENT REVIEW — per client sketch, mark-ups & site photo; not for construction

DRAWING TITLE	
V1 ROOF TO WALL views, section & 3D view	
SCALE @ A3	DATE
1:50	07.10.2026
DRAWN / CHECKED	SERIES
CC / —	ARCHITECTURAL


DRAWING No. REV

V1-02 C05


VERSION 1 — ROOF TO THE WALL

1/V1-03 ROOF SECTION ACROSS AT C1 — 1:25


(as client sketch A: roof runs to the wall)

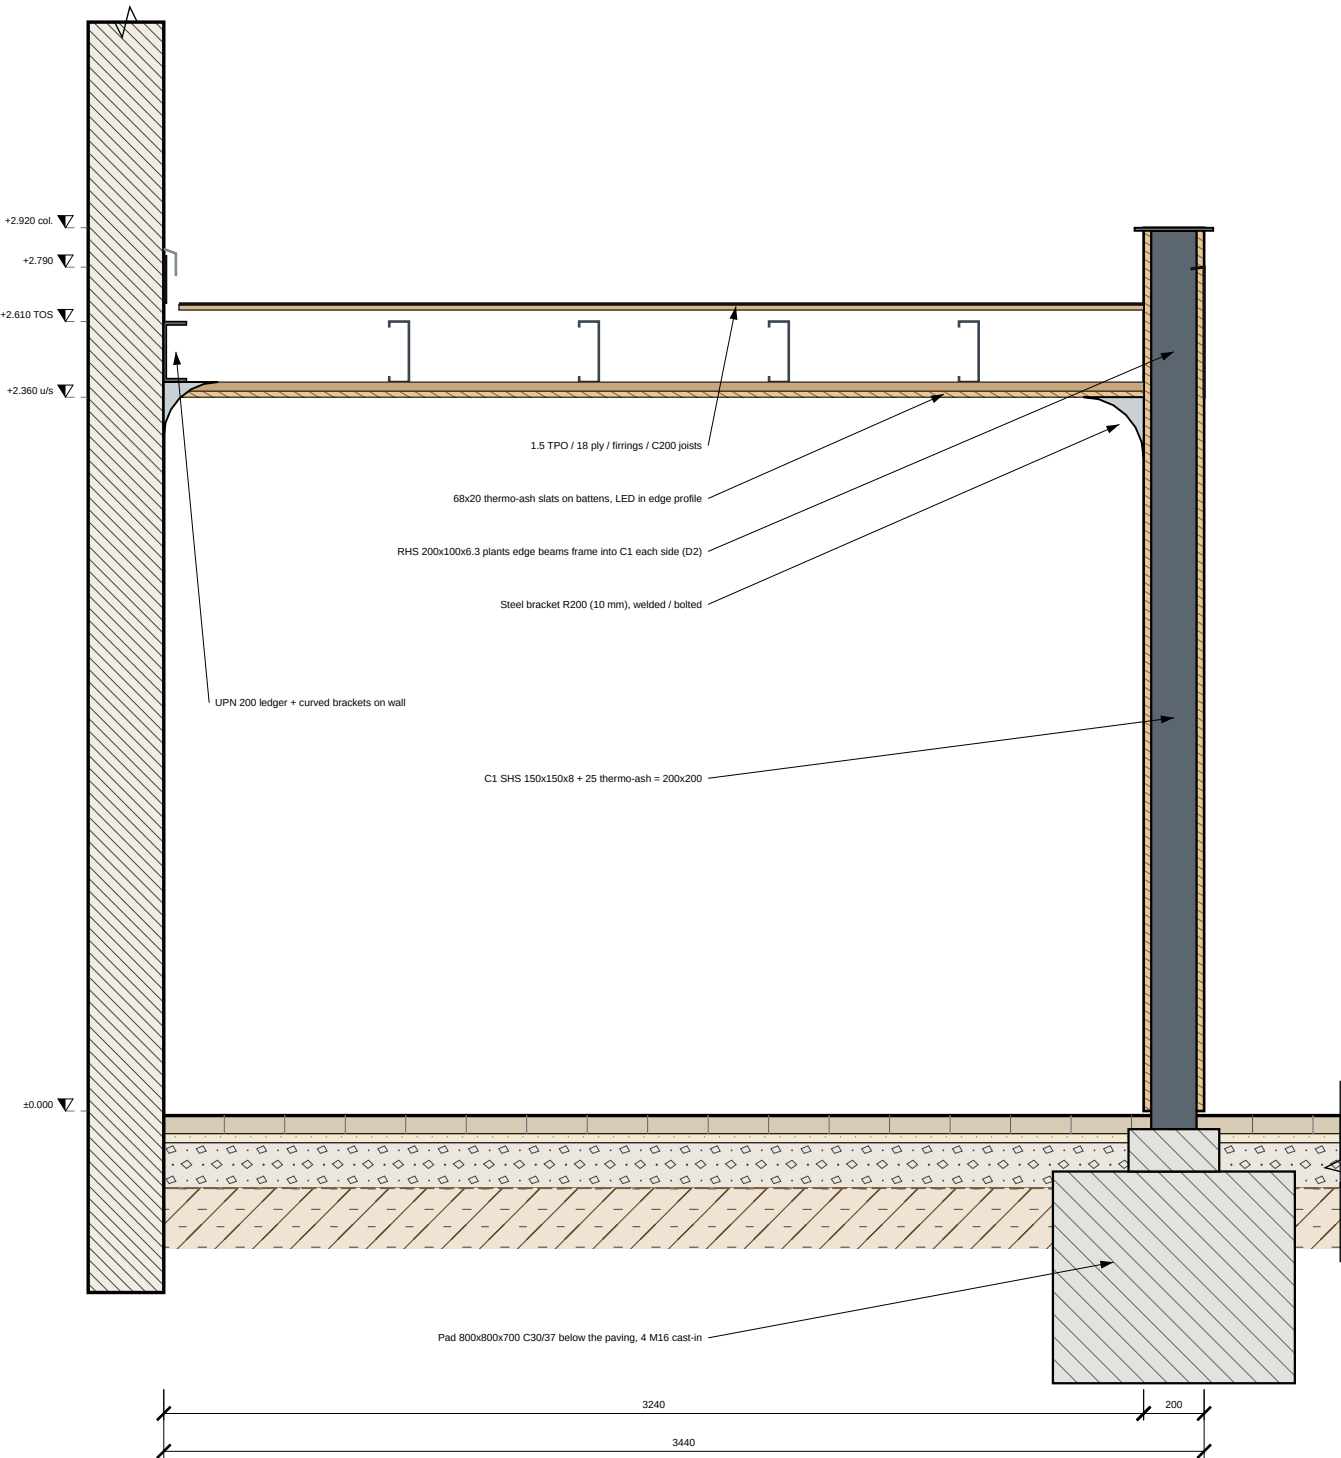


SPECIFICATION
Steel S355, hot-dip galvanised; columns & brackets powder-coated RAL 9010 or timber-clad (thermo-ash).
Roof: TPO 1.5 on 18 mm marine ply on tapered firrings (fall 1:70 to the free-edge box gutter).
Soffit: thermo-ash 68x20 slats, LED 2700 K in perimeter profile. Fascia 3 mm aluminium RAL 9010, 0.43 m.
Wall ledger & brackets into sound masonry/RC — engineer to confirm anchors.

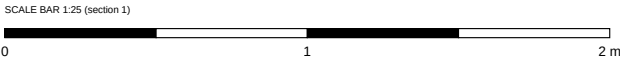


D1 ROOF TO WALL (client sketch A) — 1:15

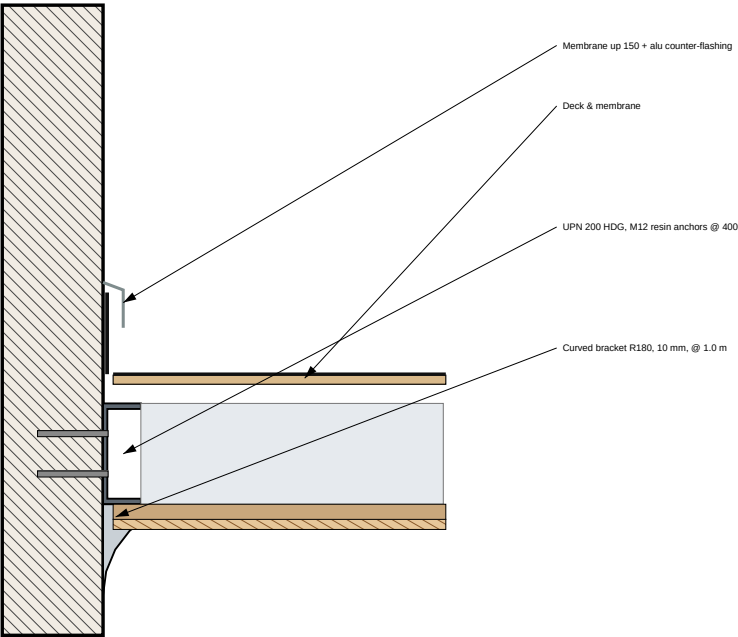

D2 COLUMN / ROOF JUNCTION (plants side) — 1:15

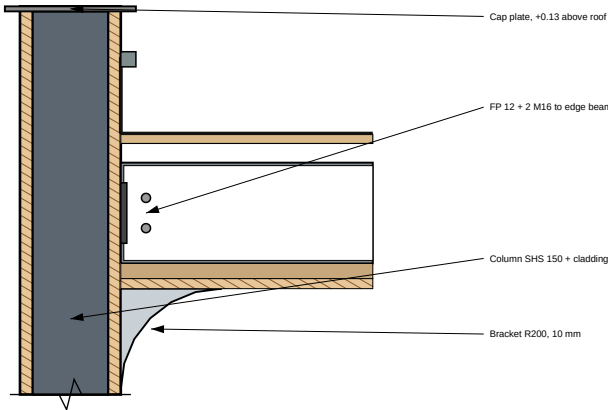

D3 CORNER AT C2 — PLAN 1:15

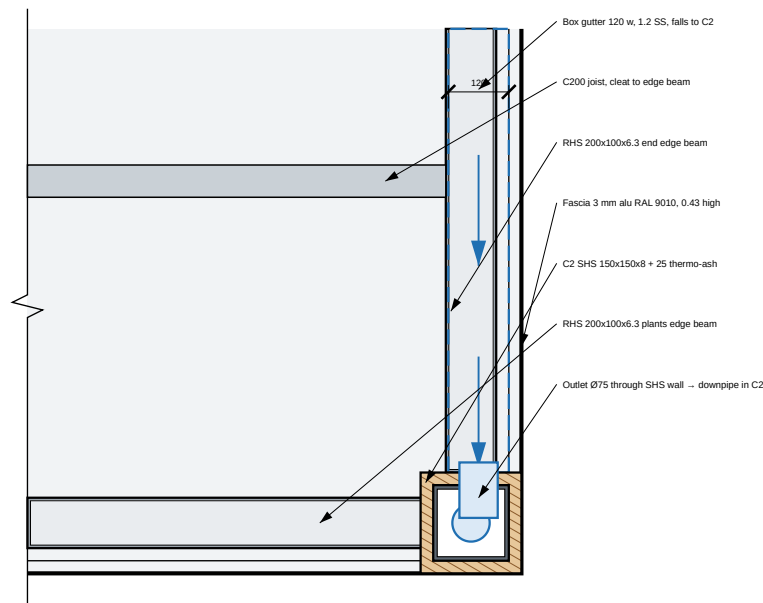

COURTYARD ROOF — V1

VERSION 1 — ROOF TO THE WALL: roof 3.22 x 3.44 up to the tall wall (bears on wall ledger + curved brackets); 2 columns on the plants side
Client: Owner / Client
Design & drawings: Claude Code

- DRAWING NOTES**
- Do not scale from this drawing. Use figured dimensions only.
 - All dimensions in millimetres; levels in metres relative to internal FFL ± 0.000 (datum to be tied to site survey).
 - Contractor to verify all dimensions, levels & existing structure on site before fabrication or ordering.
 - Read with all other architectural, structural & services drawings and the specification notes (A-001).
 - Structural members are preliminary: final design, connections & calculations by a licensed structural engineer to local code before construction.
 - Report any discrepancy to the designer before proceeding.

REVISIONS		
Rev	Date	Description
C05	07.10.2026	Garden ends at door/slider line; triangular versions V1/V2; 3D views
C04	07.10.2026	Two versions V1/V2 per client sections & site photo
C02	07.10.2026	Canopy to client sketch: 8.00 house, roof 3.22, u/s 2.36, fascia 0.43


PREVIEW FOR CLIENT REVIEW — per client sketch, mark-ups & site photo; not for construction

DRAWING TITLE	
V1 ROOF TO WALL roof section & details	
SCALE @ A3 1:25 / 1:15 / 1:20	DATE 07.10.2026
DRAWN / CHECKED CC / —	SERIES ARCHITECTURAL


DRAWING No. V1-03 REV C05

VERSION 2 — 0.90 m VOID + 2 STEEL RODS

1/V2-02 VIEW TO ANNEX FAÇADE (as site photo) — 1:50

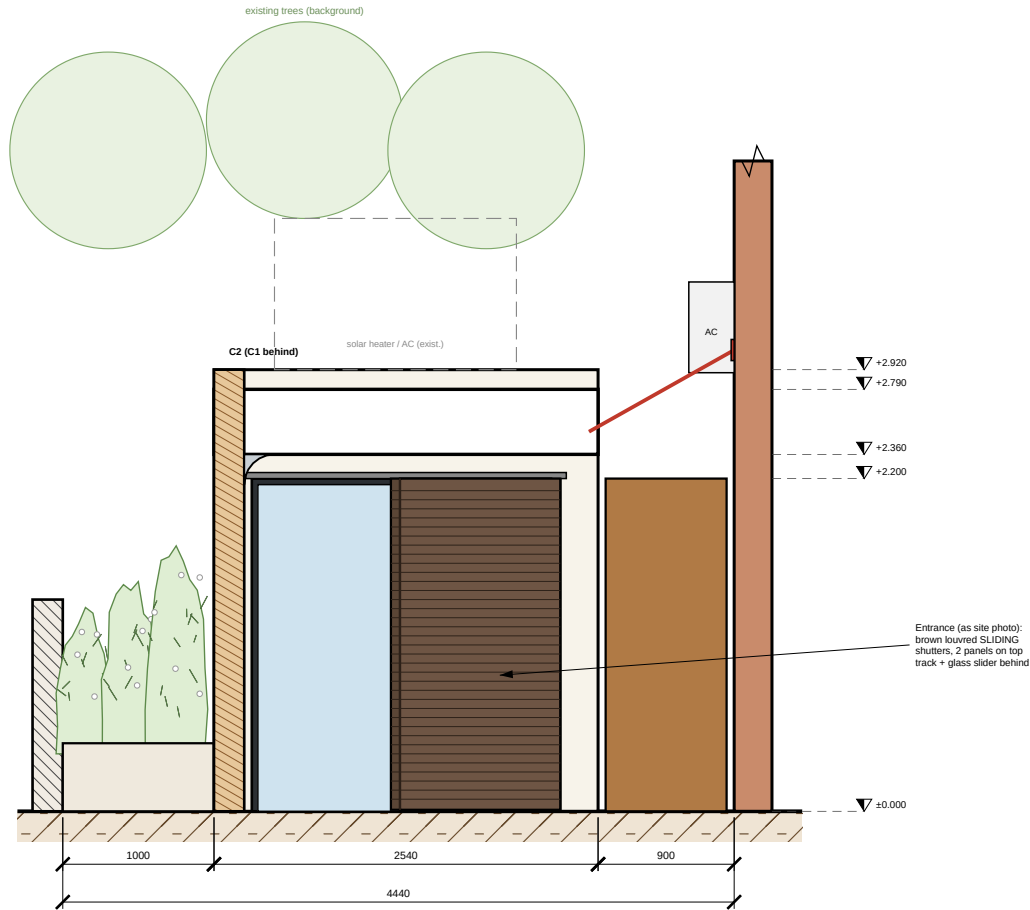


2/V2-02 PLANTS-SIDE ELEVATION — C1 + C2 — 1:50

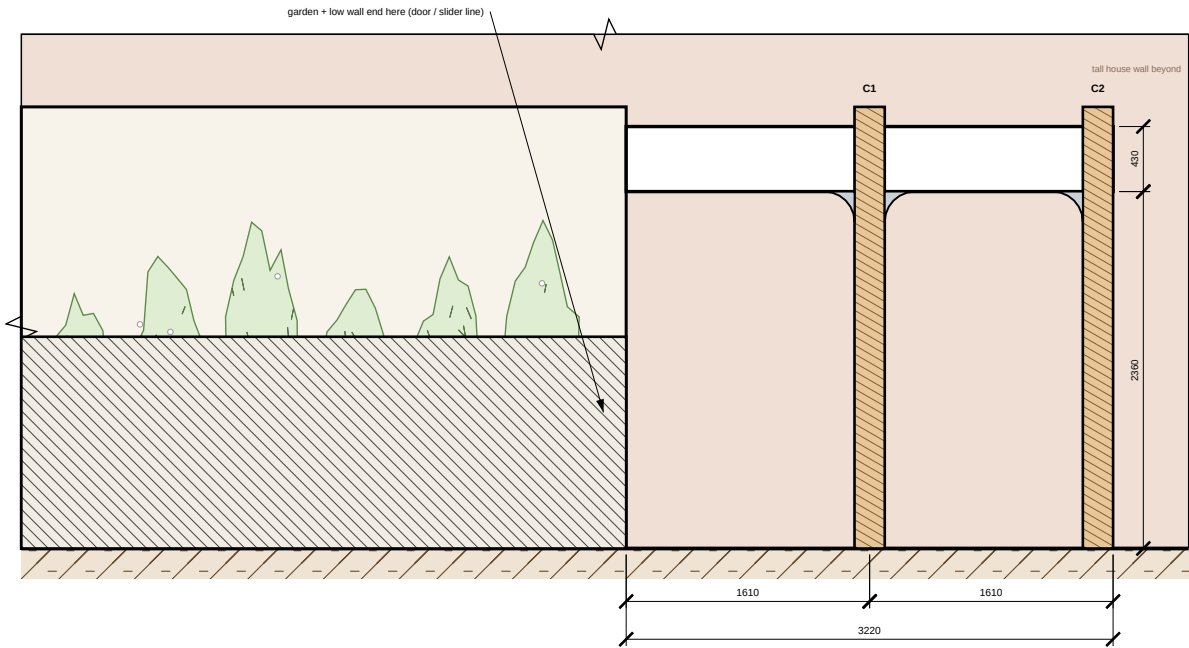


NOTES
roof 3.22 x 2.54; 0.90 m void left open; void edge tied to the tall wall with 2 slim Ø16 stainless rods (rising = 30°); 2 columns on the plants side.
Underside +2.36; fascia 0.43 (top +2.79); columns 0.13 above roof.
Garden + low wall end at the annex end façade (door / slider line). Trees are existing, in the background.
Refined roof section & details: sheet V2-03.

3/V2-02 SECTION ACROSS AT C1 — 1:50 (refined: V2-03)

tall wall left — plants side right

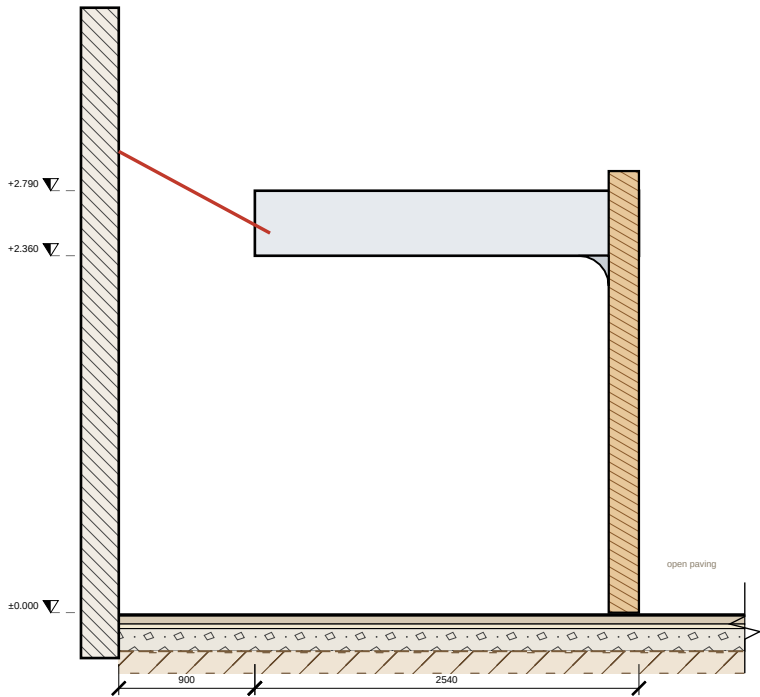

4/V2-02 3D VIEW — from the plants side (courtyard)

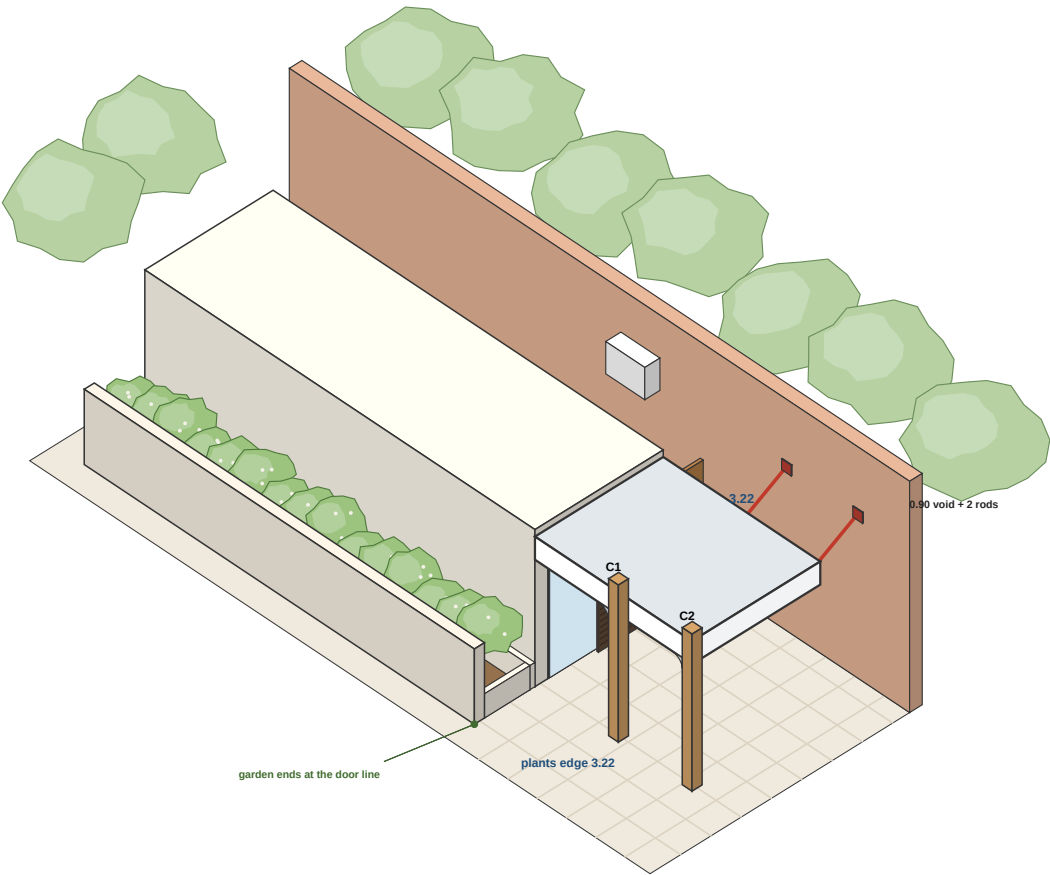

COURTYARD ROOF — V2

VERSION 2 — 0.90 m VOID + 2 STEEL RODS: roof 3.22 x 2.54; 0.90 m void left open; void edge tied to the tall wall with 2 slim Ø16 stainless rods (rising = 30°); 2 columns on the plants side
Client: Owner / Client
Design & drawings: Claude Code

DRAWING NOTES

- Do not scale from this drawing. Use figured dimensions only.
- All dimensions in millimetres; levels in metres relative to internal FFL ±0.000 (datum to be tied to site survey).
- Contractor to verify all dimensions, levels & existing structure on site before fabrication or ordering.
- Read with all other architectural, structural & services drawings and the specification notes (A-001).
- Structural members are preliminary: final design, connections & calculations by a licensed structural engineer to local code before construction.
- Report any discrepancy to the designer before proceeding.

REVISIONS

Rev	Date	Description
C05	07.10.2026	Garden ends at door/slider line; triangular versions V1/V2; 3D views
C04	07.10.2026	Two versions V1/V2 per client sections & site photo
C02	07.10.2026	Canopy to client sketch: 8.00 house, roof 3.22, u/s 2.36, fascia 0.43

PREVIEW FOR CLIENT REVIEW — per client sketch, mark-ups & site photo; not for construction

DRAWING TITLE

V2 VOID + RODS
views, section & 3D view

SCALE @ A3

1:50

DRAWN / CHECKED

CC / —

DATE

07.10.2026

SERIES

ARCHITECTURAL

DRAWING No.

REV


V2-02

C05

VERSION 2 — 0.90 m VOID + 2 STEEL RODS


1/V2-03 ROOF SECTION ACROSS AT C1 — 1:25

(as client sketch B: roof stops, rods to the wall)

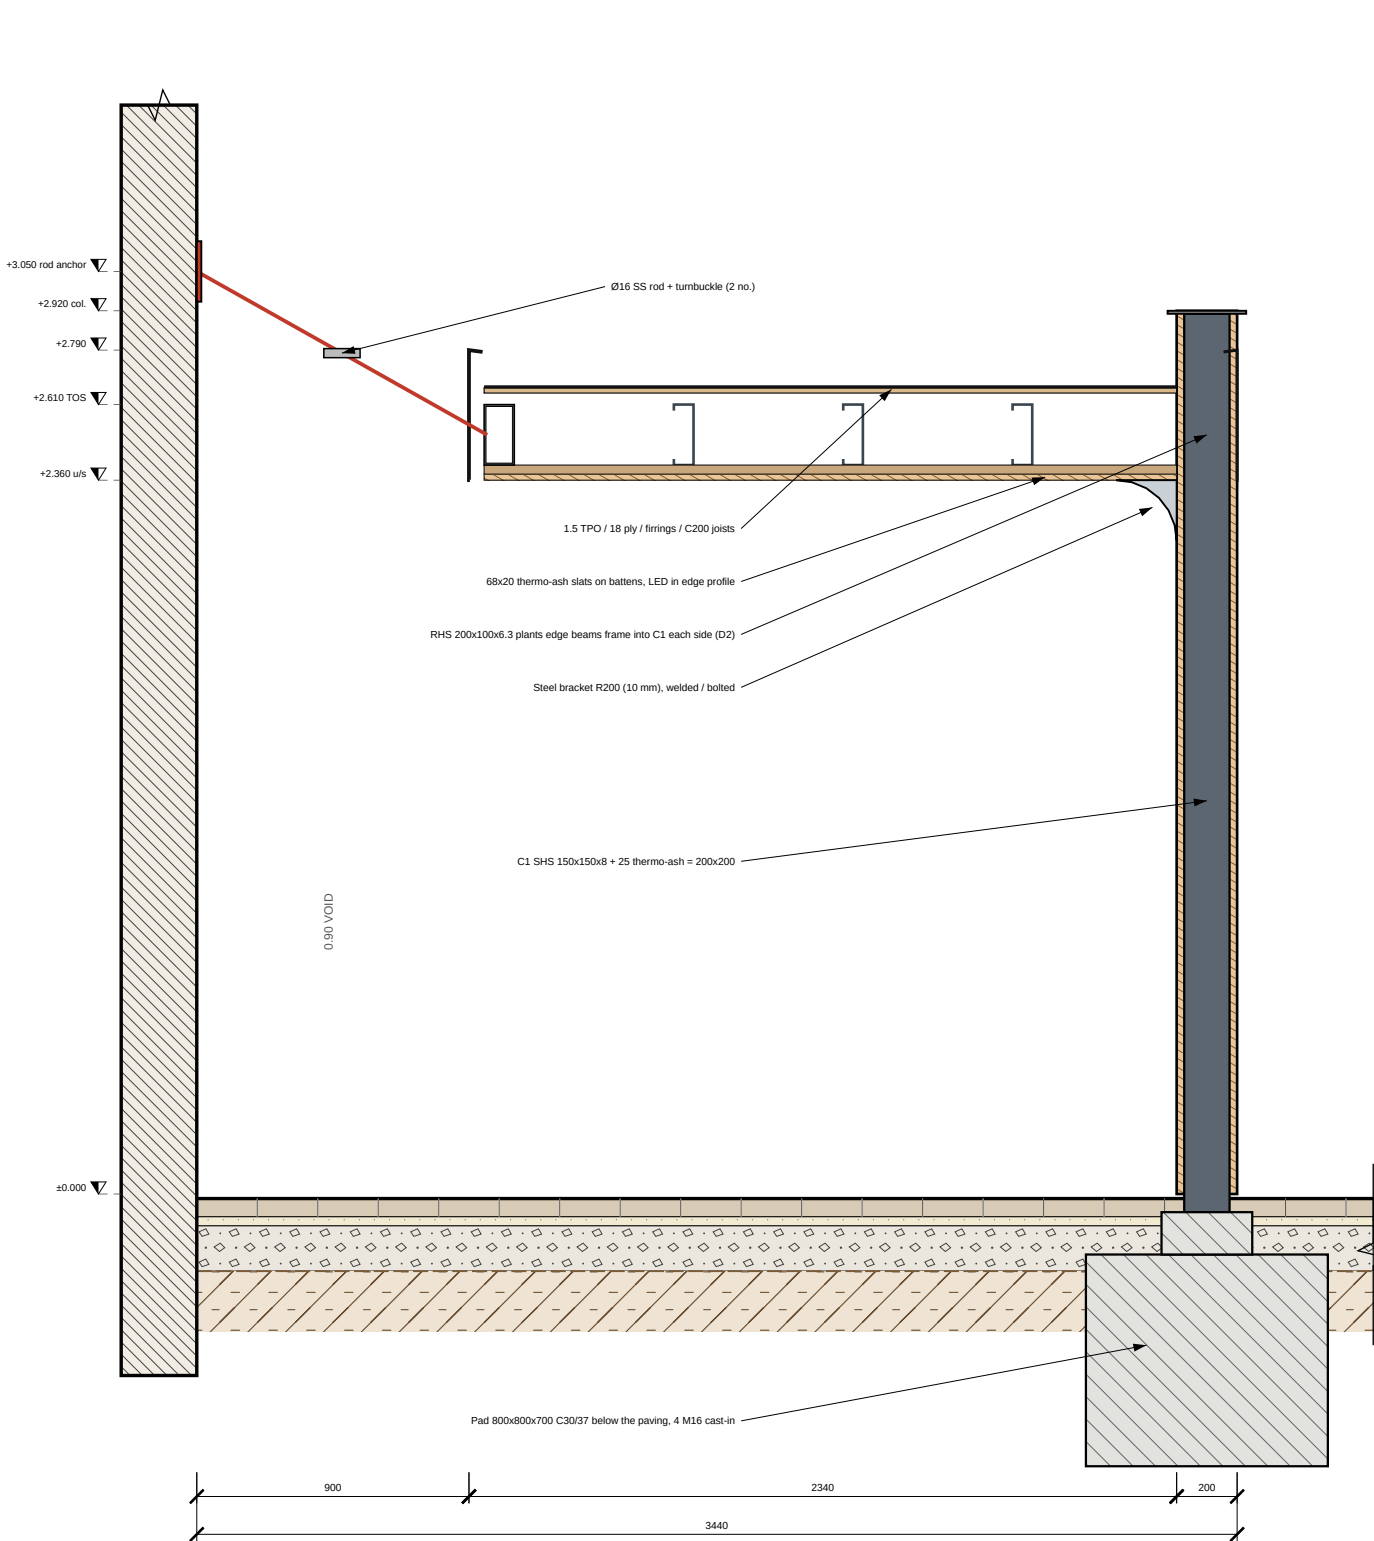


SPECIFICATION
Steel S355, hot-dip galvanised; columns & brackets powder-coated RAL 9010 or timber-clad (thermo-ash).
Roof: TPO 1.5 on 18 mm marine ply on tapered firrings (fall 1:70 to the free-edge box gutter).
Soffit: thermo-ash 68x20 slats, LED 2700 K in perimeter profile. Fascia 3 mm aluminium RAL 9010, 0.43 m.
Rods: Ø16 stainless 316, fork ends, turnbuckle, = 30° rise; engineer to confirm wall anchors.


SCALE BAR 1:25 (section 1)

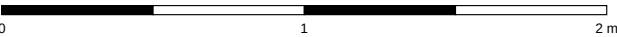


D1 ROD TO WALL (client sketch B) — 1:20

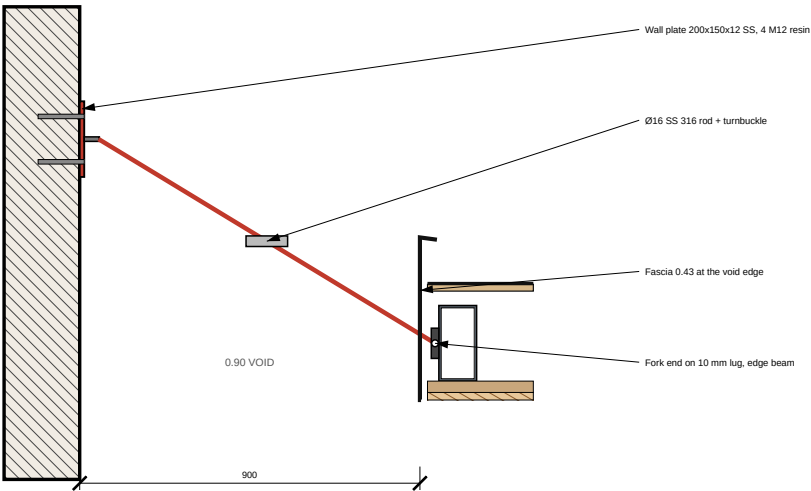

D2 COLUMN / ROOF JUNCTION (plants side) — 1:15

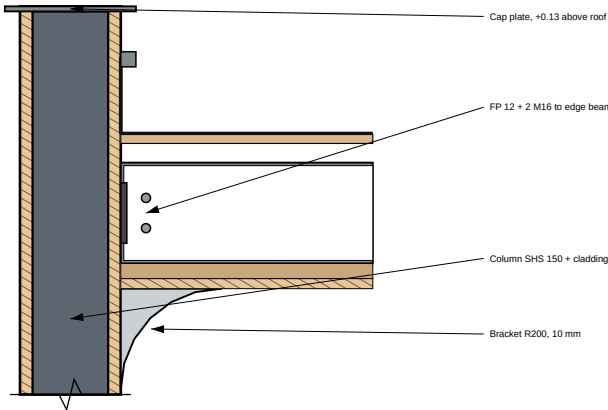

D3 CORNER AT C2 — PLAN 1:15

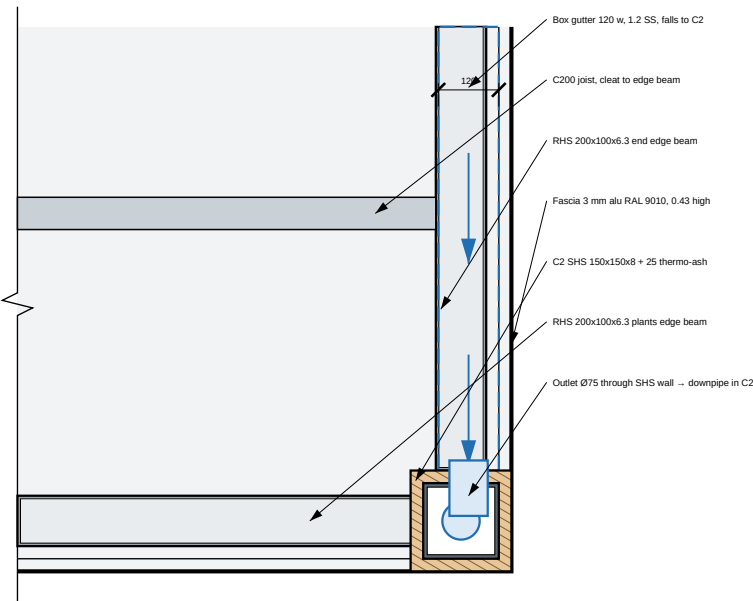

COURTYARD ROOF — V2

VERSION 2 — 0.90 m VOID + 2 STEEL RODS: roof 3.22 x 2.54; 0.90 m void left open; void edge tied to the tall wall with 2 slim Ø16 stainless rods (rising ≈ 30°); 2 columns on the plants side
Client: Owner / Client
Design & drawings: Claude Code

DRAWING NOTES

- Do not scale from this drawing. Use figured dimensions only.
- All dimensions in millimetres; levels in metres relative to internal FFL ±0.000 (datum to be tied to site survey).
- Contractor to verify all dimensions, levels & existing structure on site before fabrication or ordering.
- Read with all other architectural, structural & services drawings and the specification notes (A-001).
- Structural members are preliminary: final design, connections & calculations by a licensed structural engineer to local code before construction.
- Report any discrepancy to the designer before proceeding.

REVISIONS

Rev	Date	Description
C05	07.10.2026	Garden ends at door/slider line; triangular versions V1/V2; 3D views
C04	07.10.2026	Two versions V1/V2 per client sections & site photo
C02	07.10.2026	Canopy to client sketch: 8.00 house, roof 3.22, u/s 2.36, fascia 0.43

PREVIEW FOR CLIENT REVIEW — per client sketch, mark-ups & site photo; not for construction

DRAWING TITLE

V2 VOID + RODS
roof section & details

SCALE @ A3

1:25 / 1:15 / 1:20

DRAWN / CHECKED

CC / —

DATE

07.10.2026

SERIES

ARCHITECTURAL

DRAWING No.

V2-03

REV

C05